


DESCRIÇÃO DO PROJETO




A reforma da cozinha foi projetada para criar um ambiente moderno, funcional e acolhedor, priorizando a otimização do espaço e a circulação fluida. O projeto inclui uma bancada em formato "L" e uma torre quente para acomodar fornos e micro-ondas de forma ergonômica. Materiais como mármore preto para as bancadas, armários em MDF cinza-sagrado com detalhes em madeira e porcelanato de grande formato foram usados para um visual contemporâneo. A iluminação foi aprimorada com LED embutidos. A cozinha agora é equipada com eletrodomésticos embutidos de última geração e possui uma coifa silenciosa, garantindo um ambiente bem ventilado e iluminado. O resultado é uma cozinha que alia estética e a prática






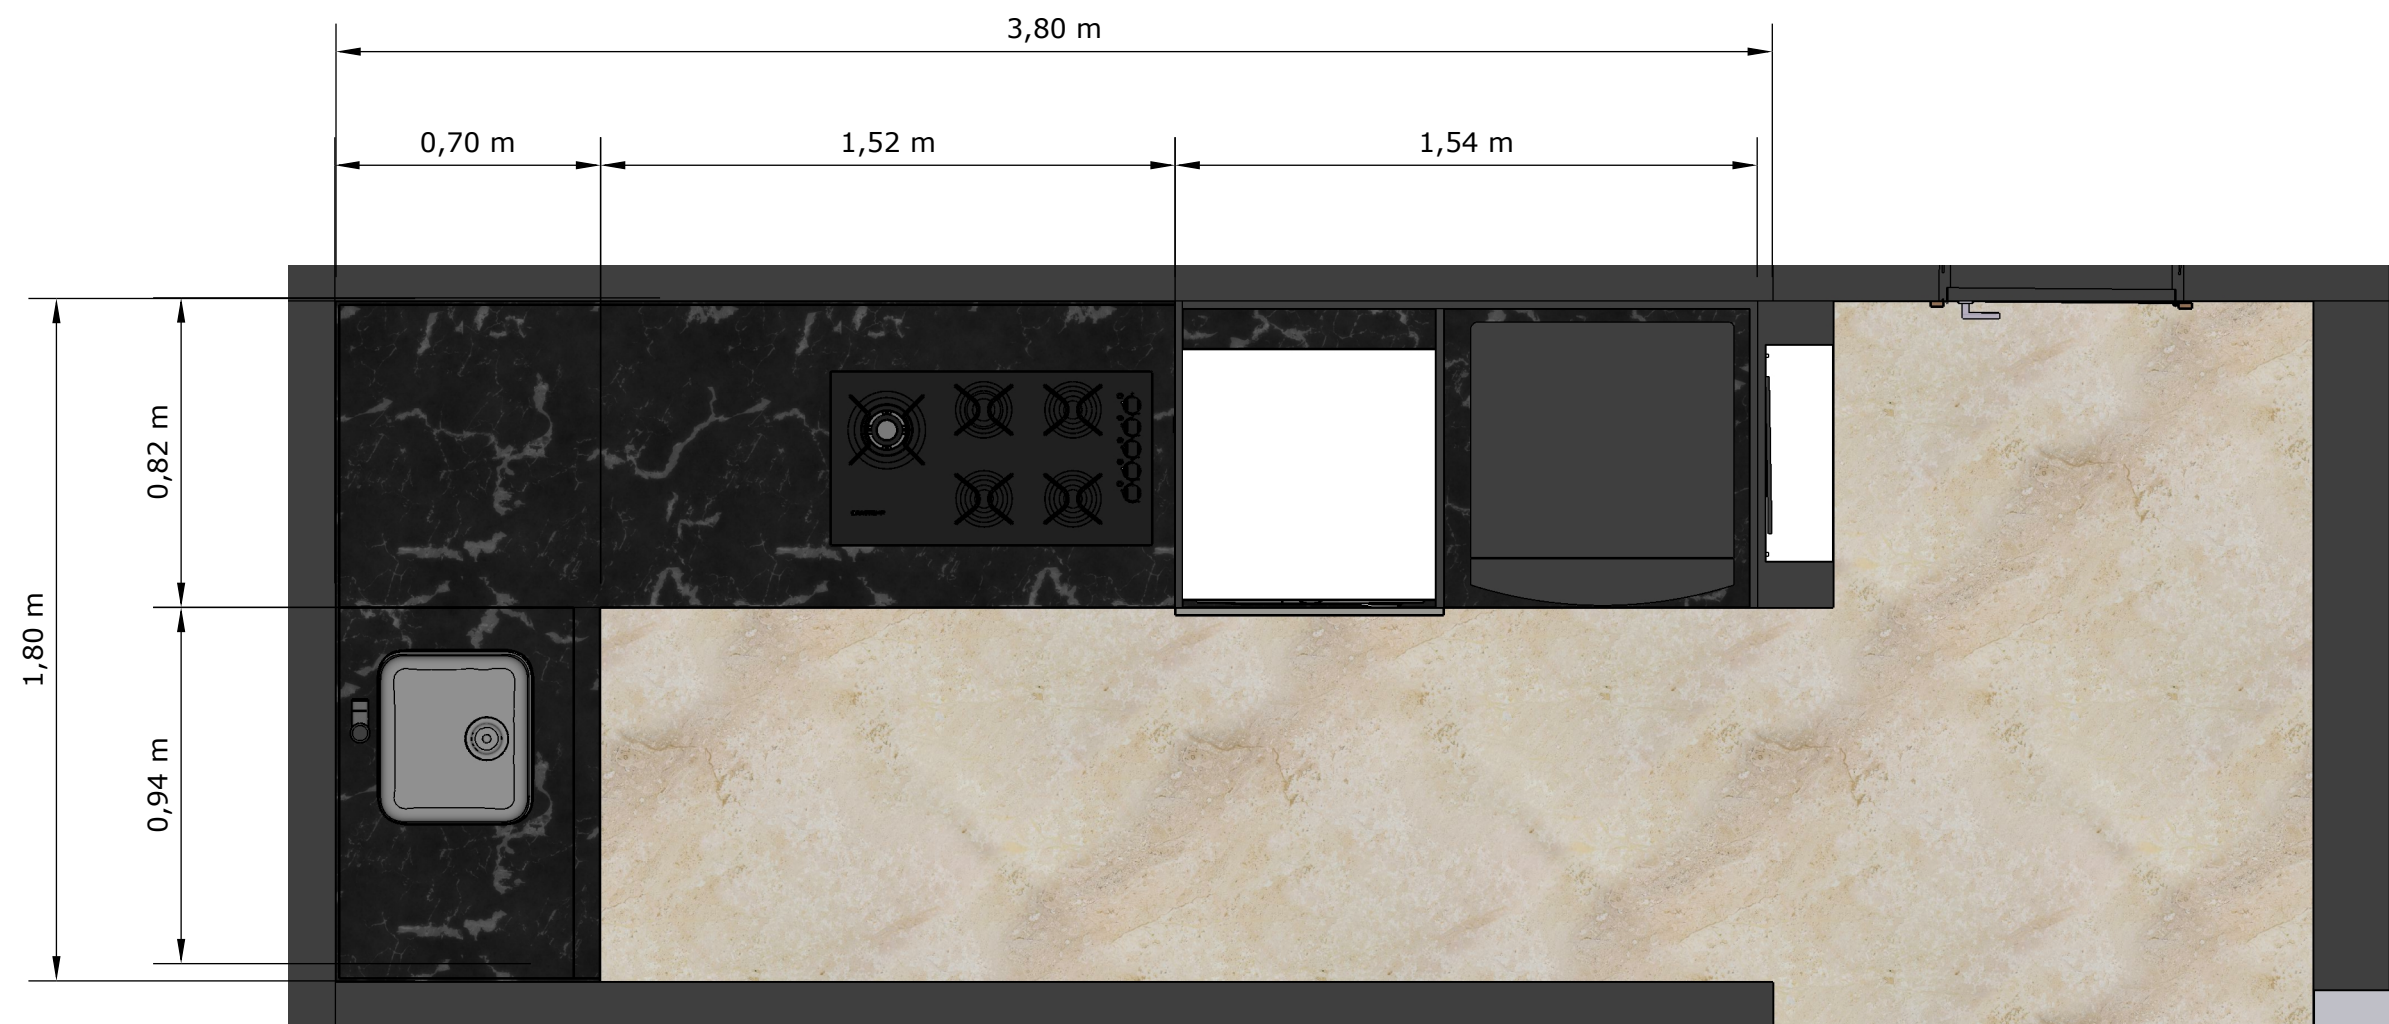


1 PLANTA
1:20

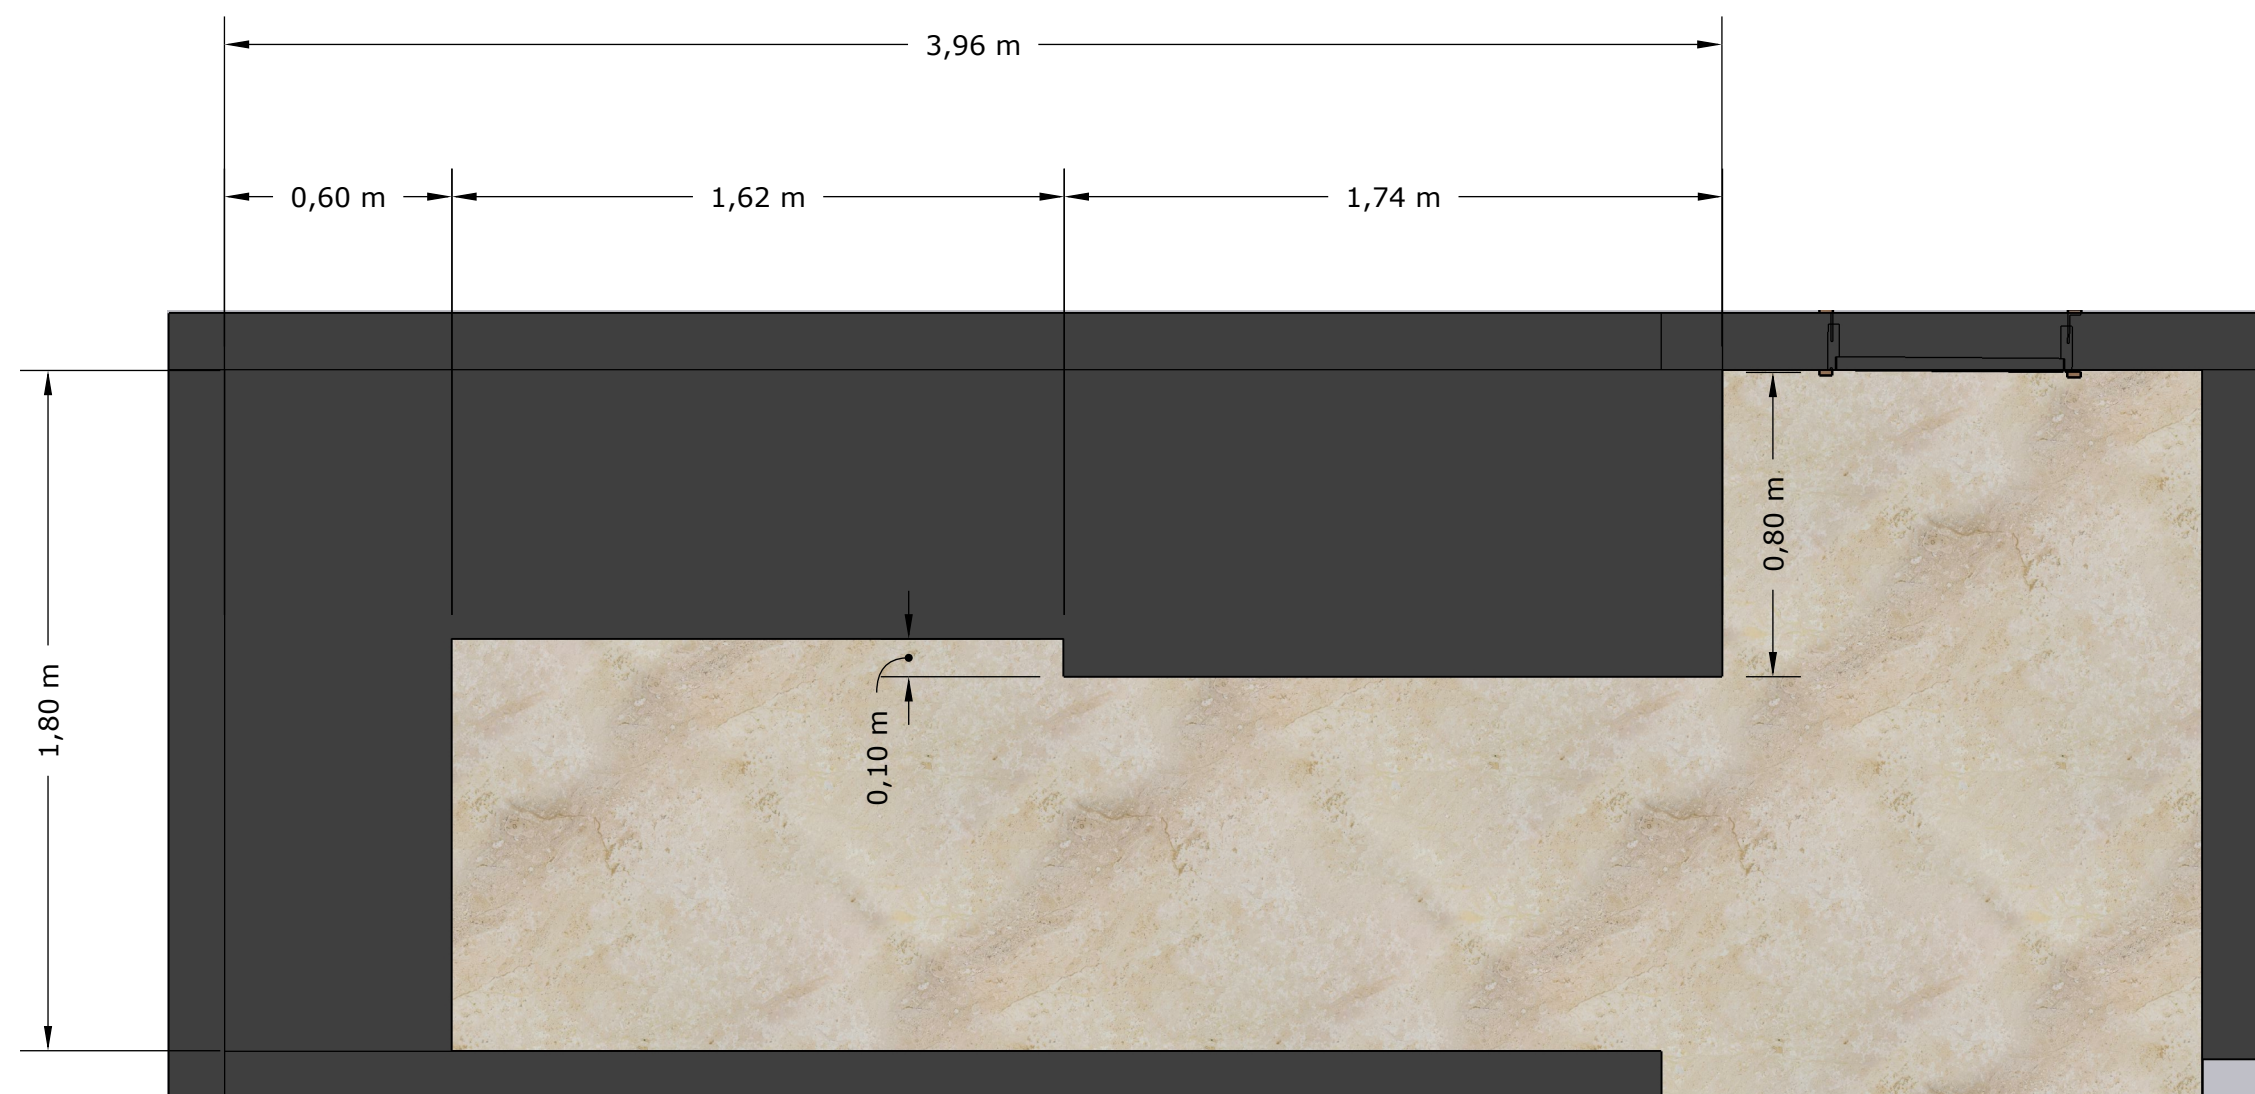


1 PLANTA - RODA BASE
1:20

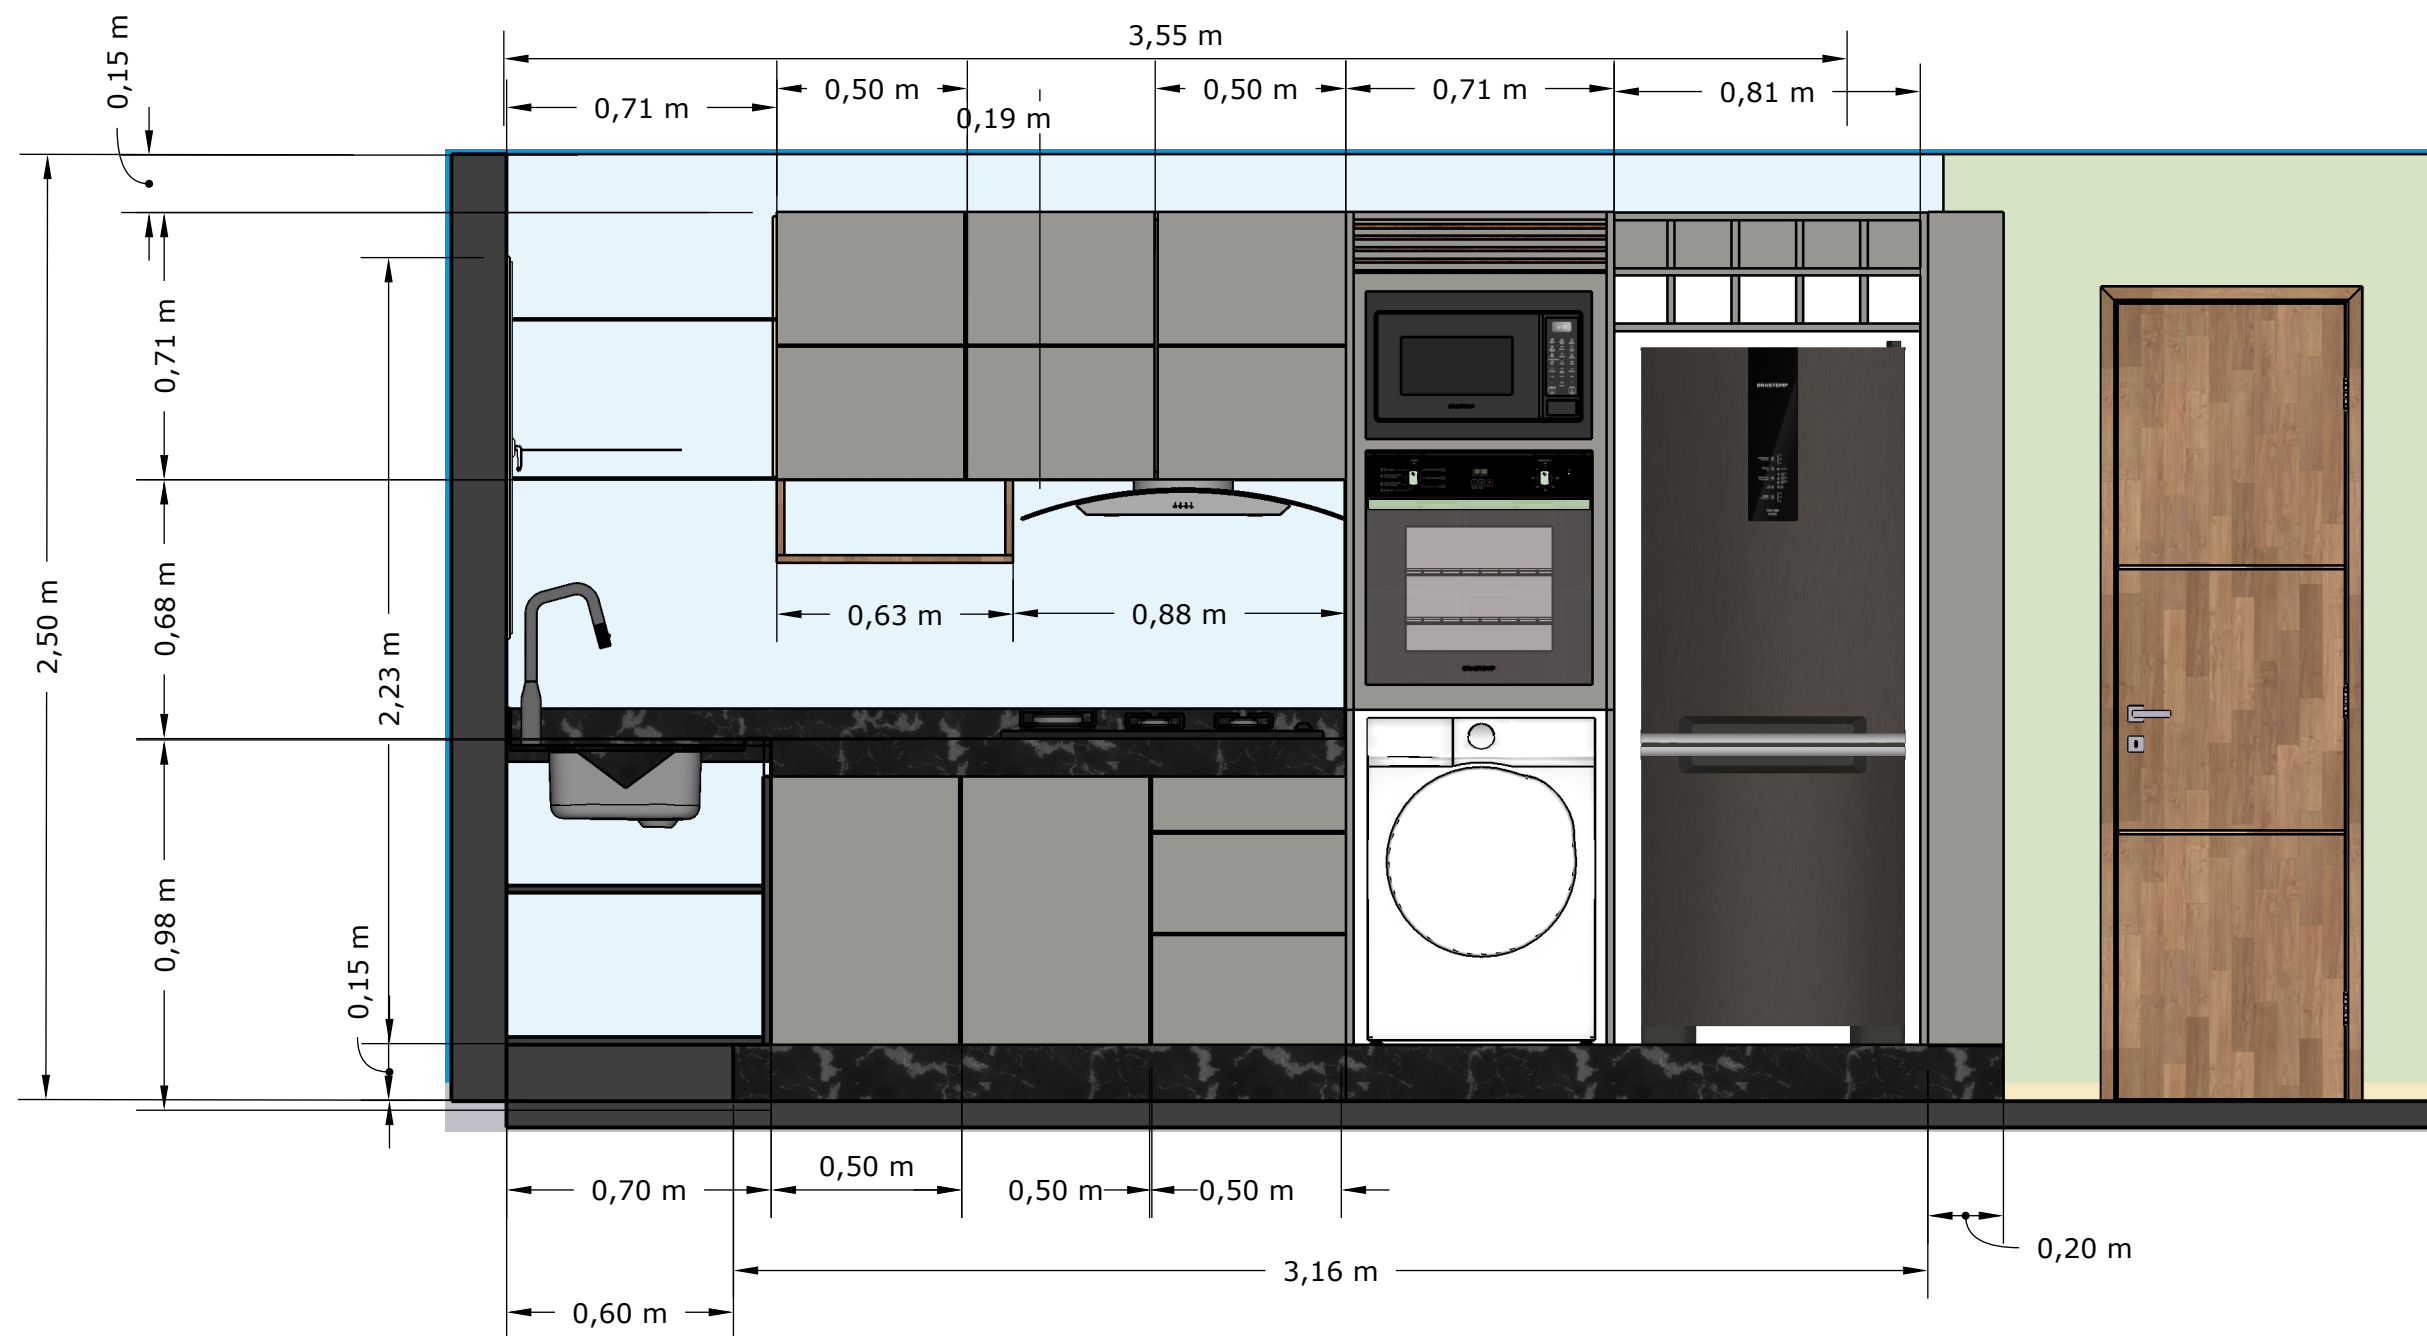


1 VISTA
1:20

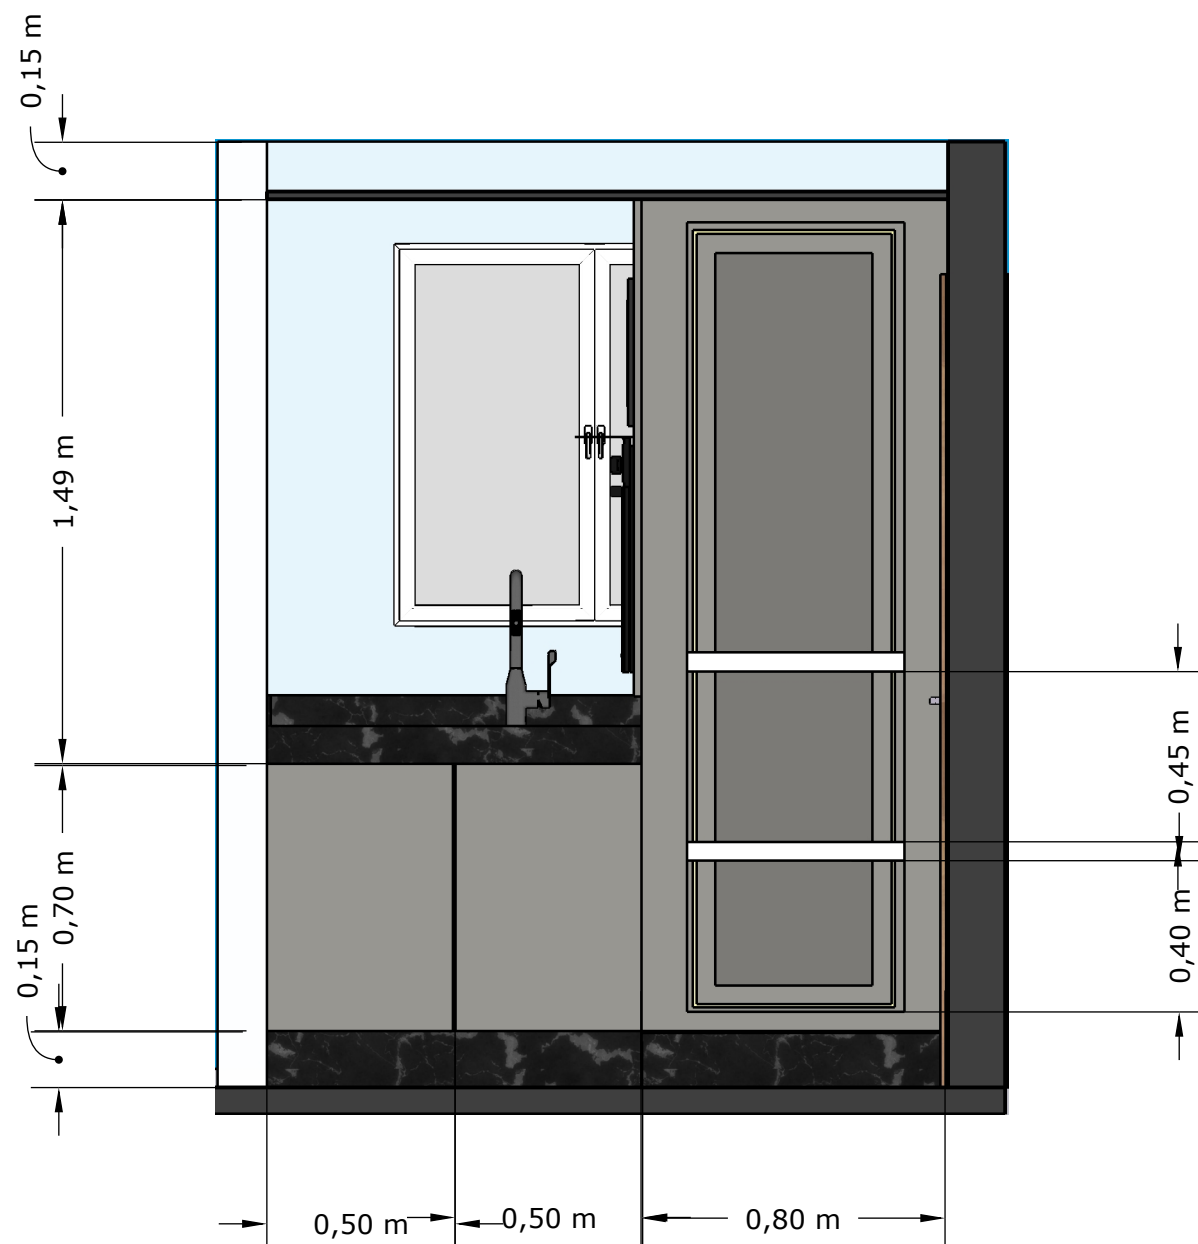


1 VISTA 2
1:20

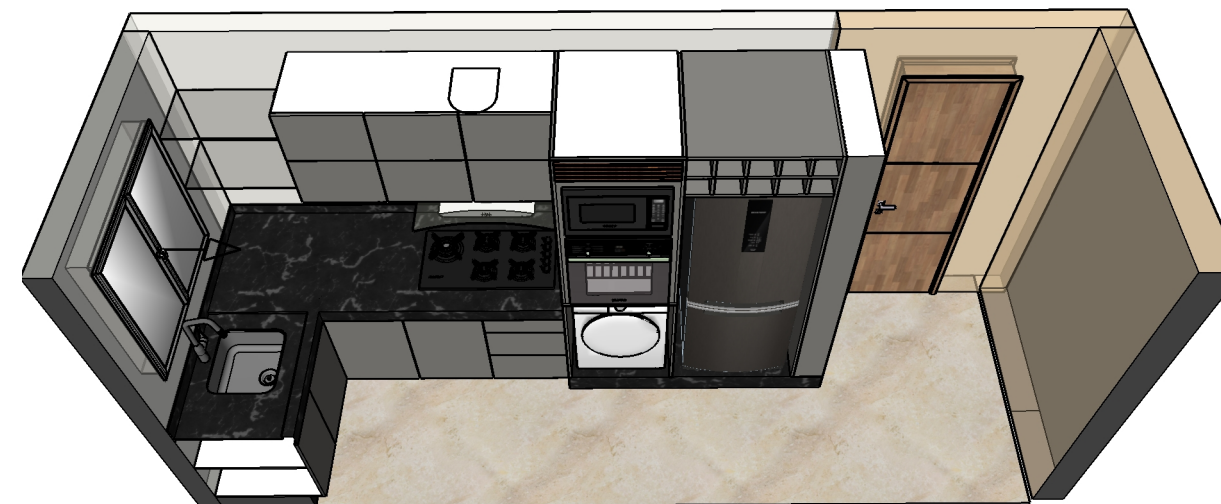



2 PESPECTIVA
SEM ESCALA

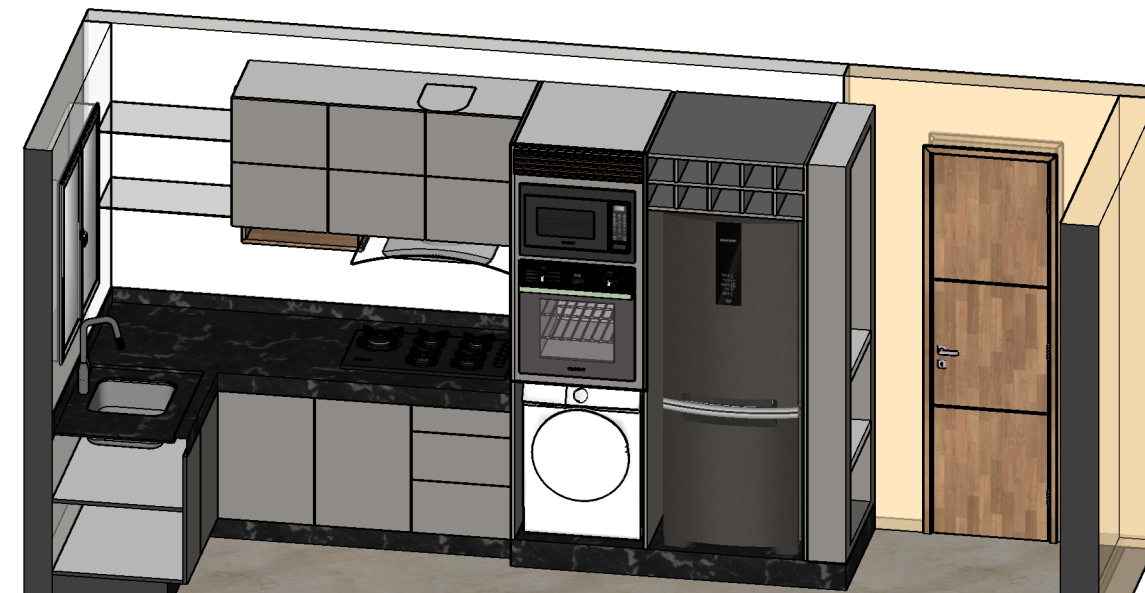


3 PESPECTIVA
SEM ESCALA

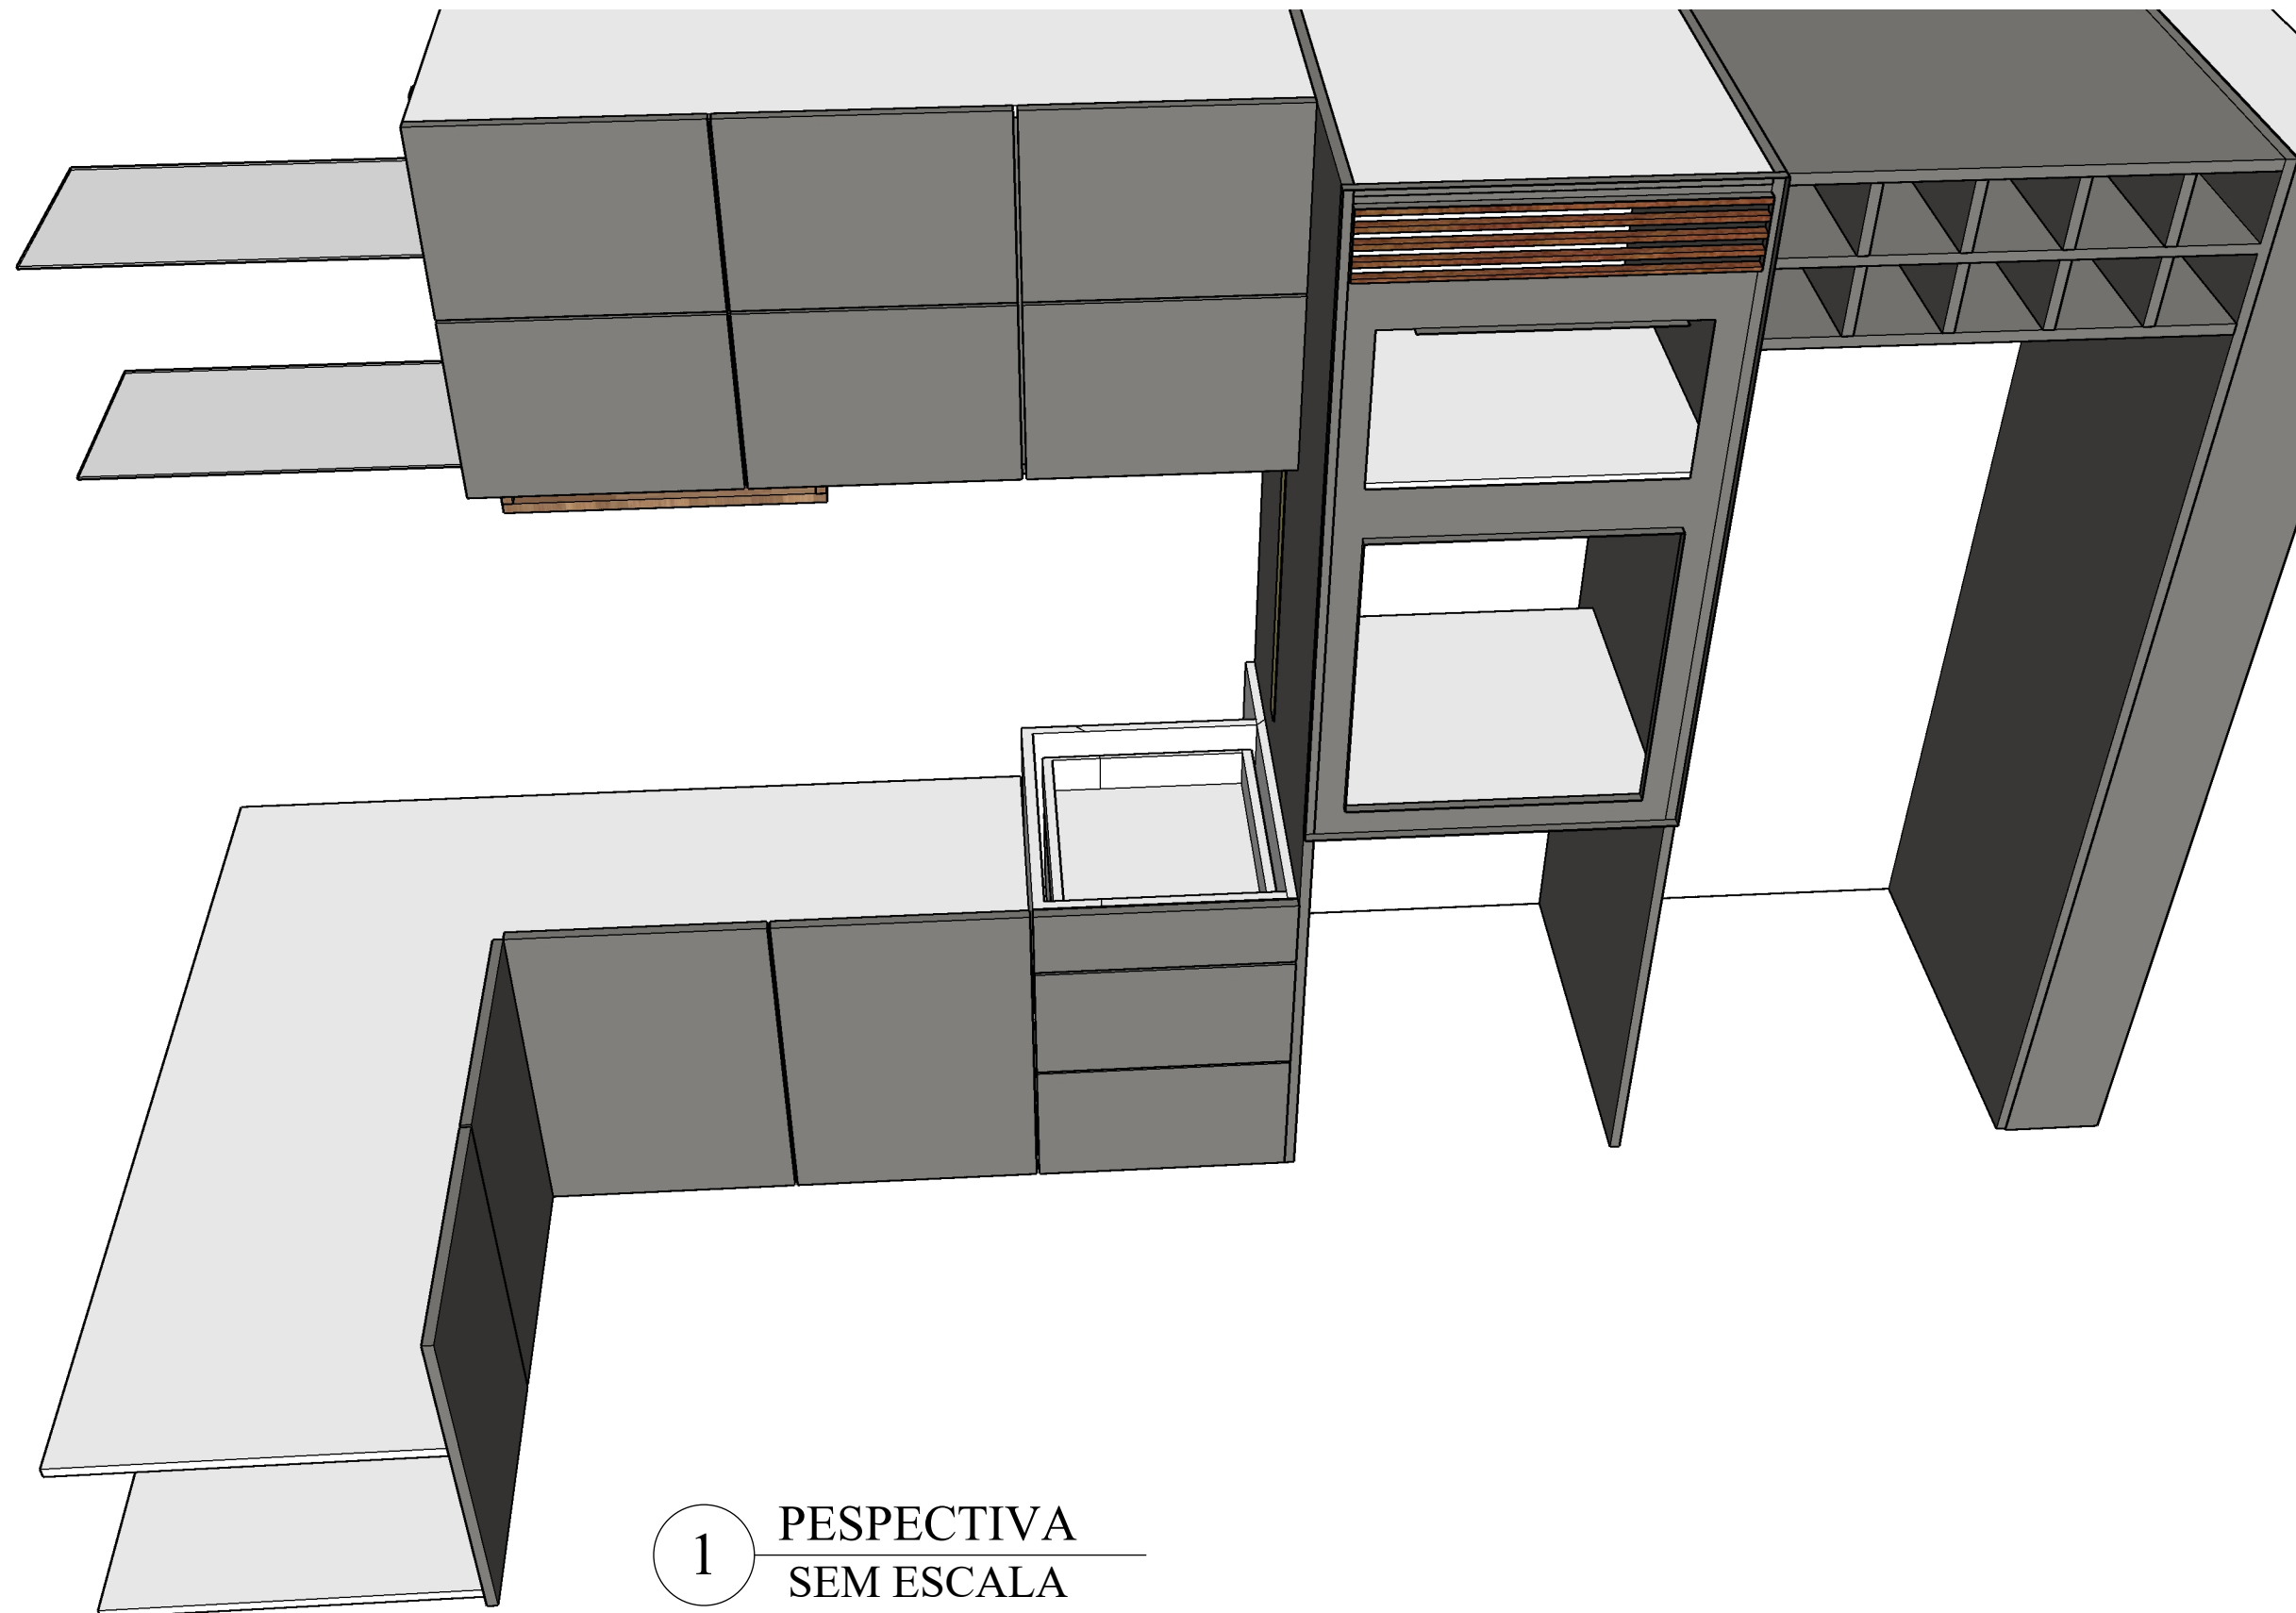

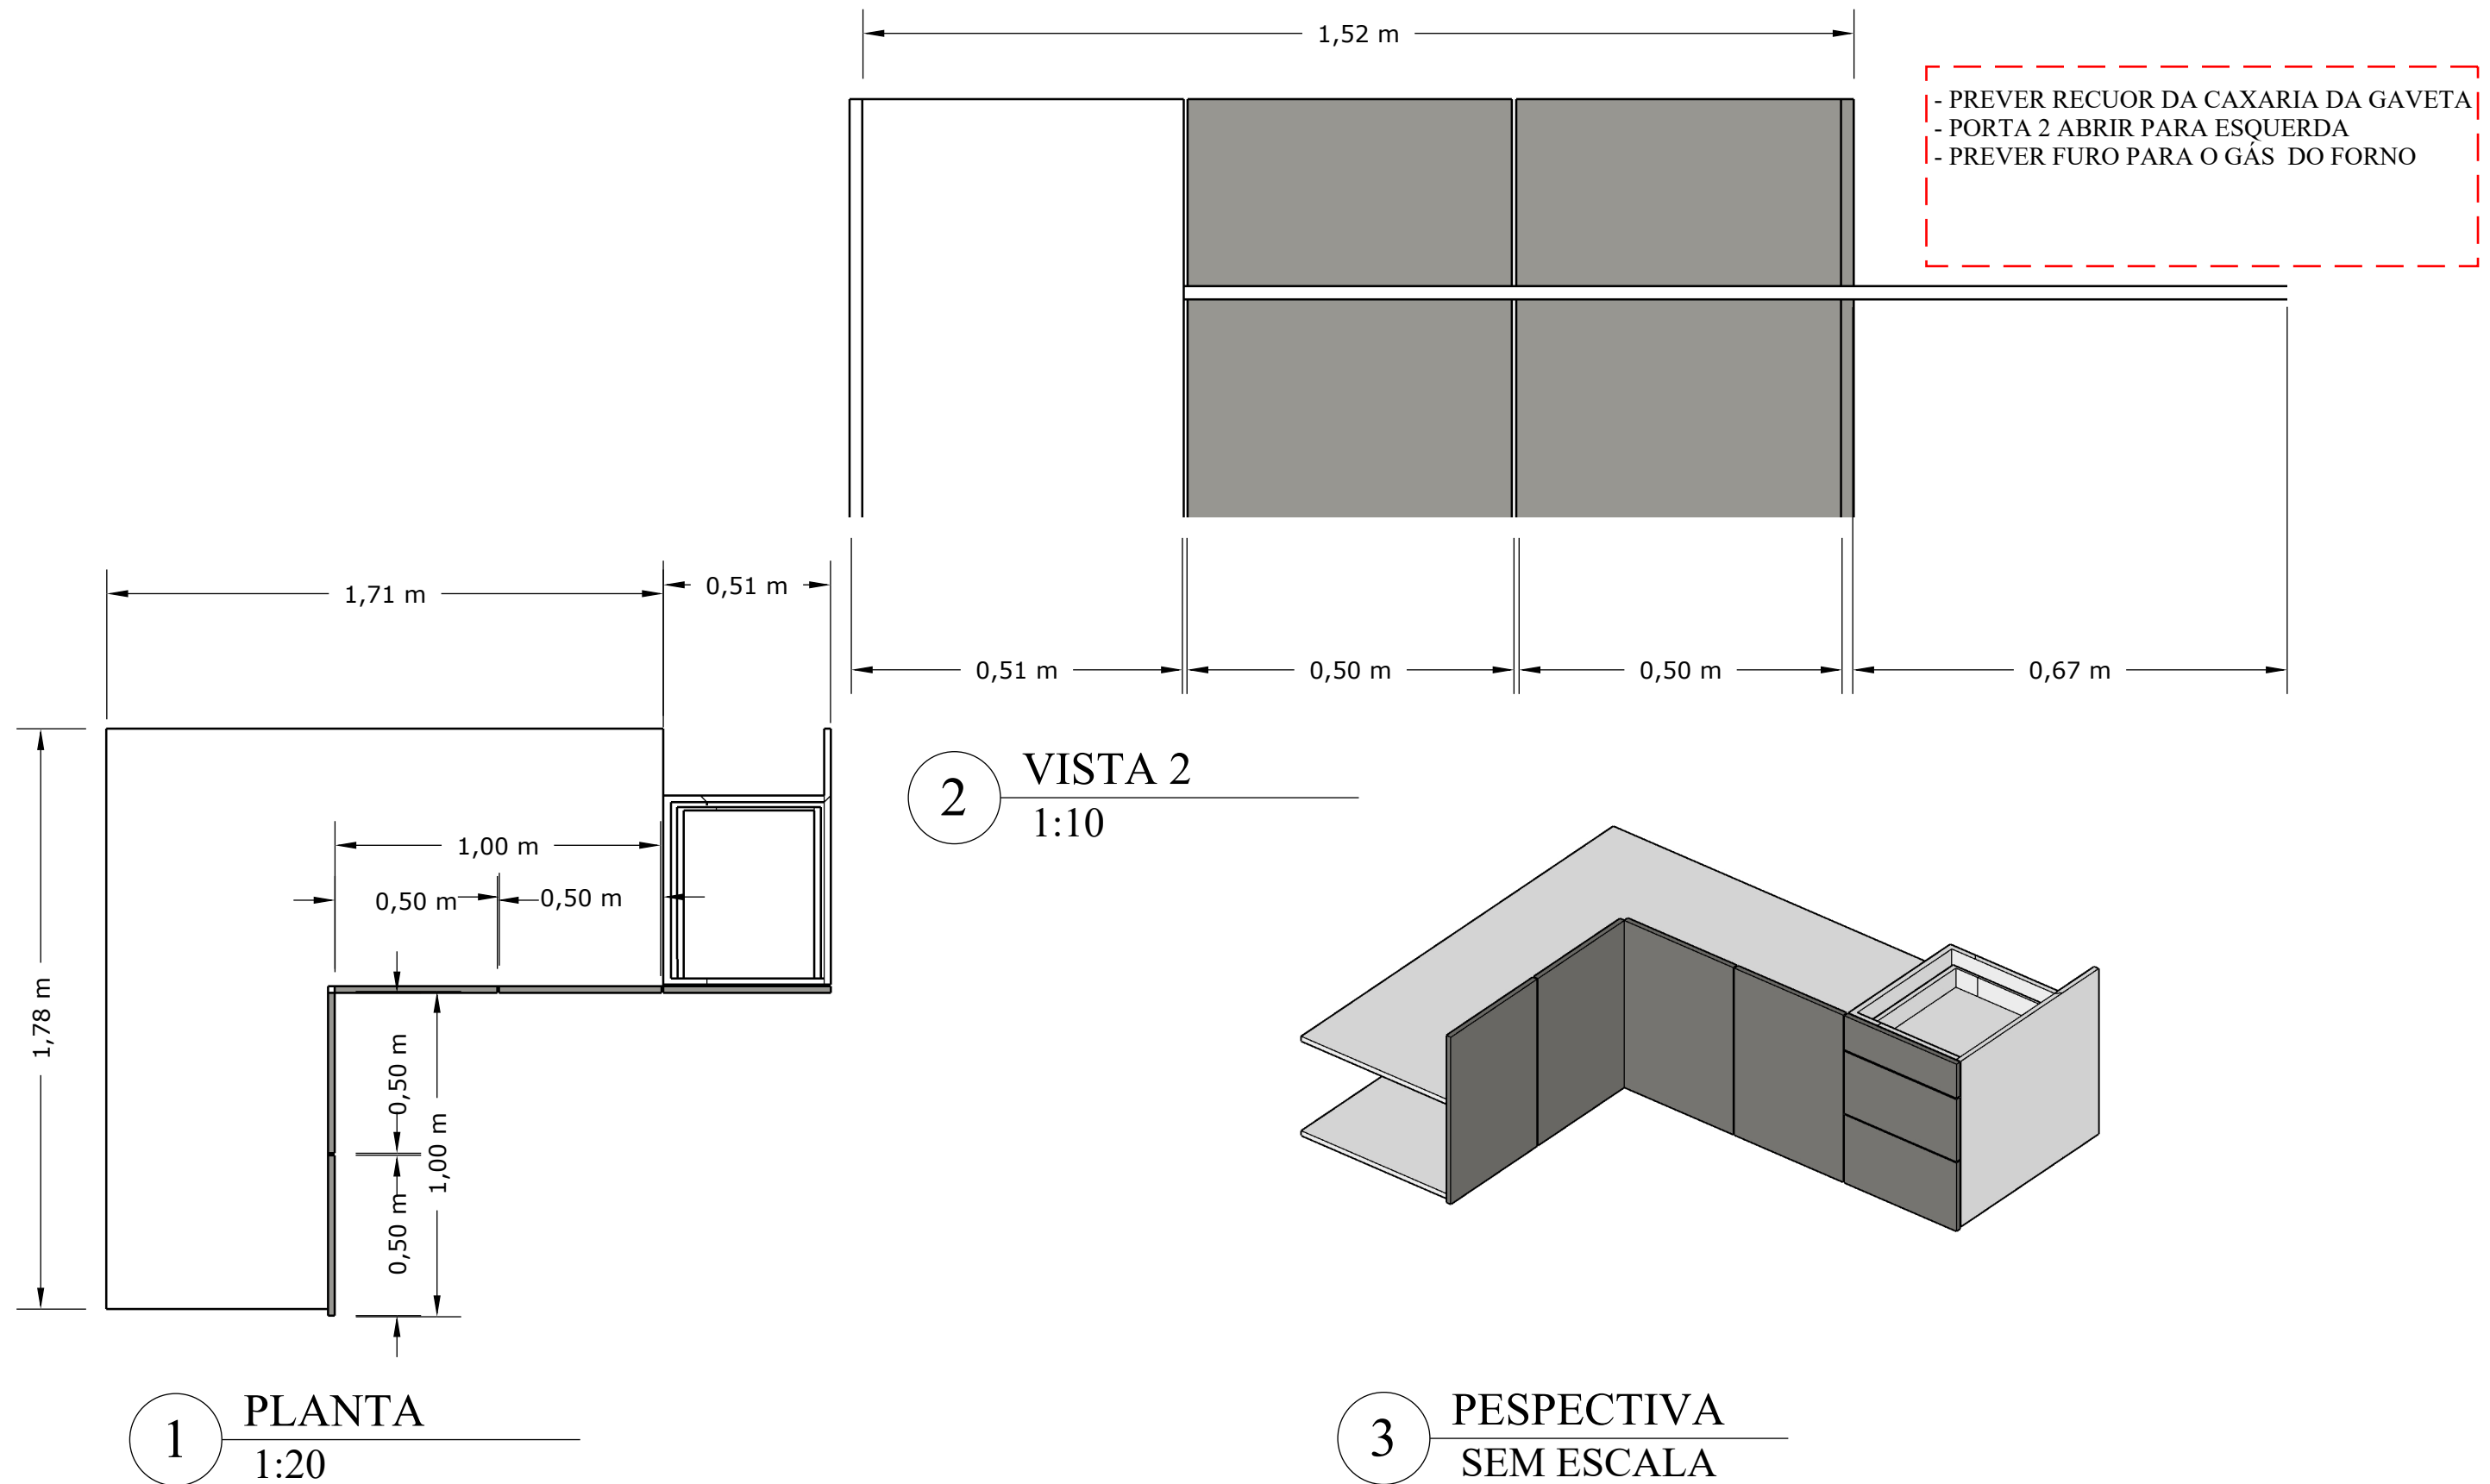

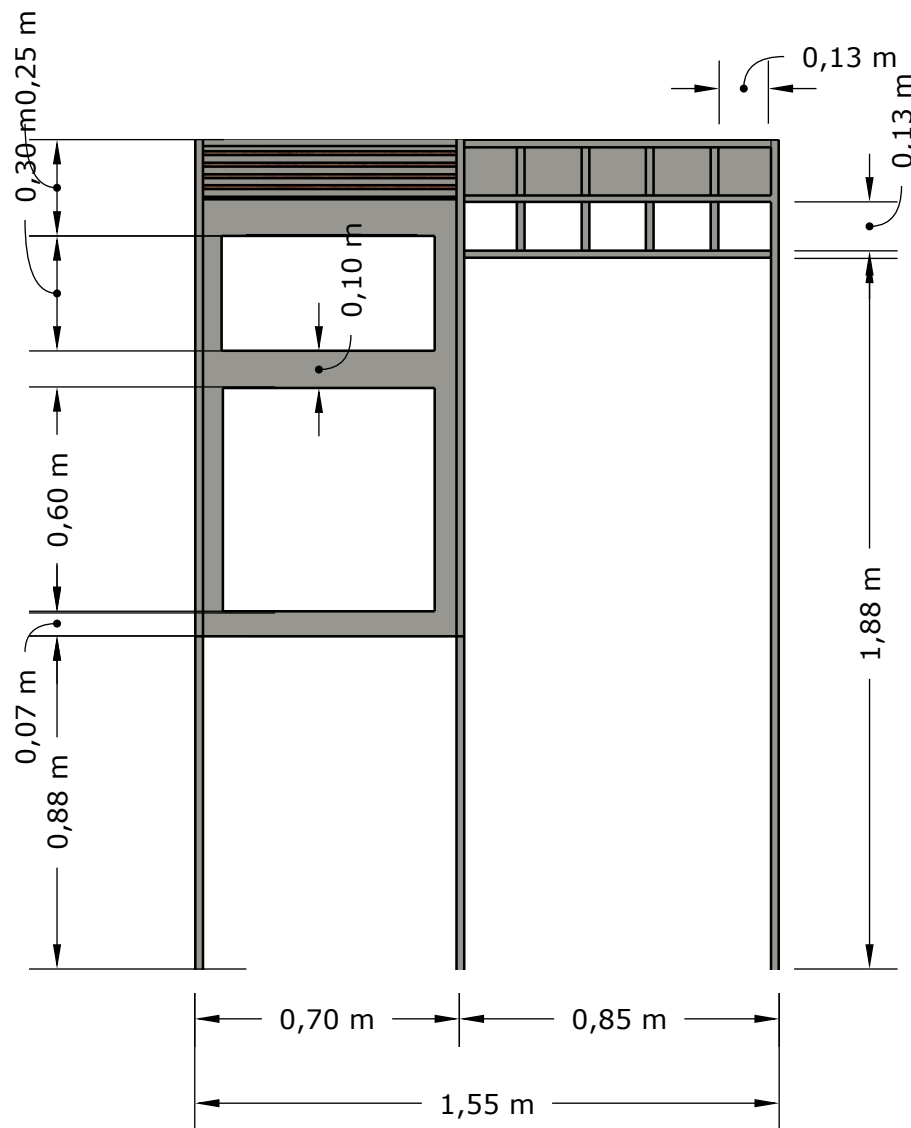

1 VISTA 2
1:20

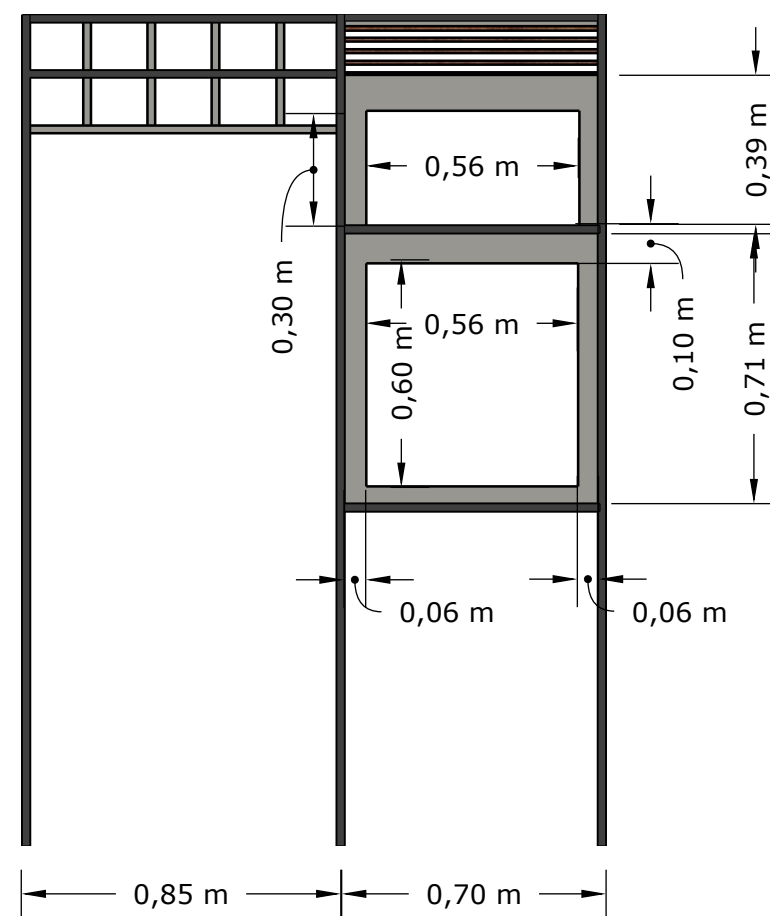


2 VISTA 2
1:20




3 PESPECTIVA
SEM ESCALA

- CONFERIR AS MEDIDAS DO FORNO ANTES DO CORTE
- CONSULTAR AS MEDIDAS DA MICRO-ONDAS ANTES DO CORTE
- PREVER FORNTE DE ENERGIA PARA TODOS OS ELETROS

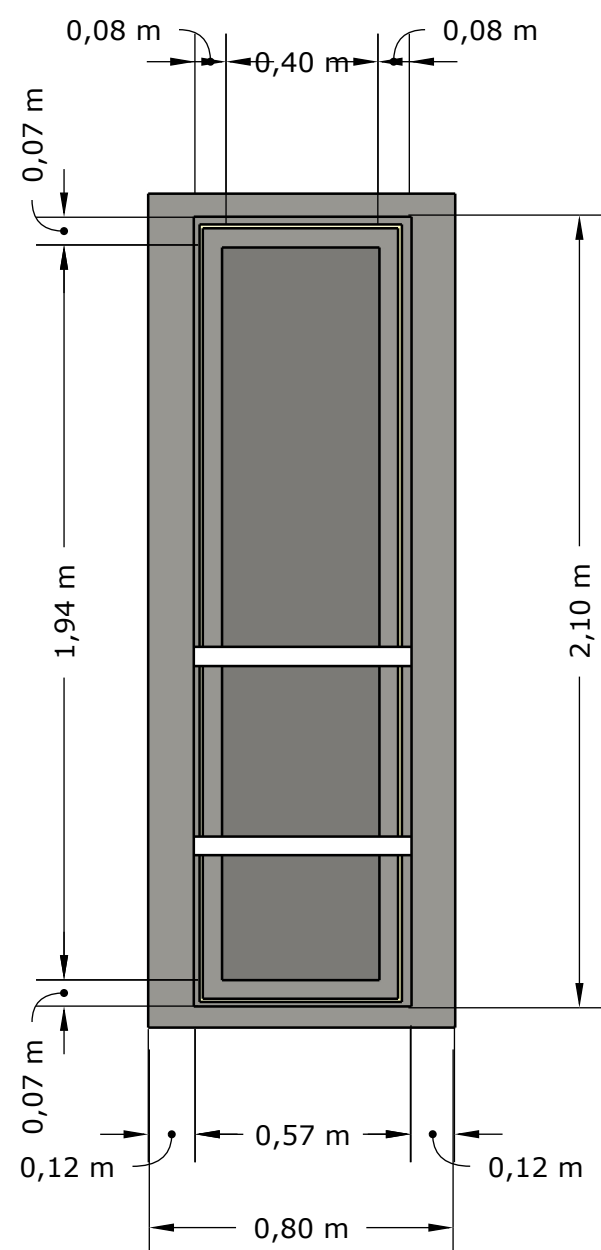


1 VISTA 1
1:20

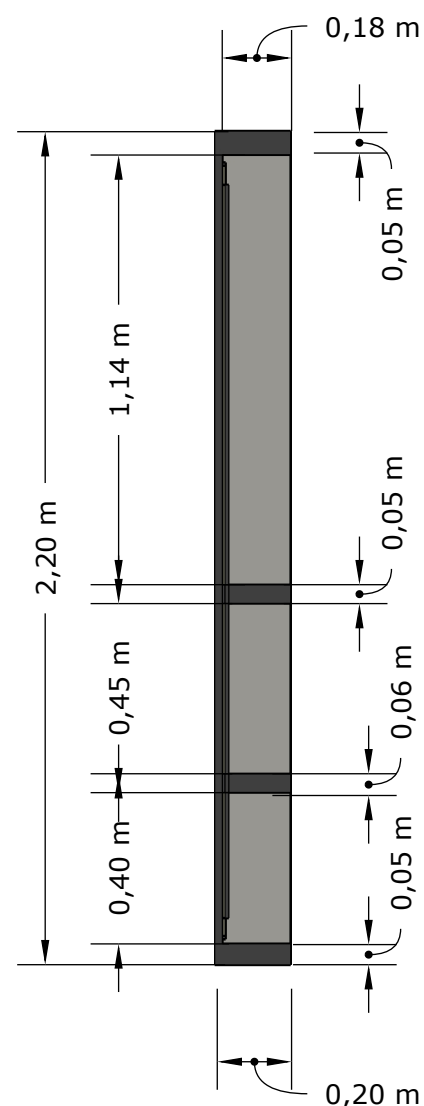


2 CORTE
1:20

- PREVER PONTO DE ENERGIA PARA O LED
- PREVE INTERRUPTOR PARA O LED
- LED 2500 W

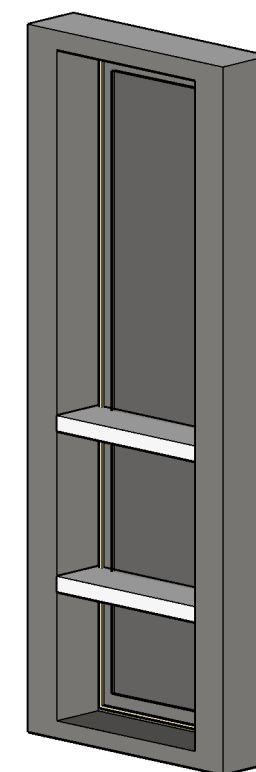


3 PESPECTIVA
SEM ESCALA

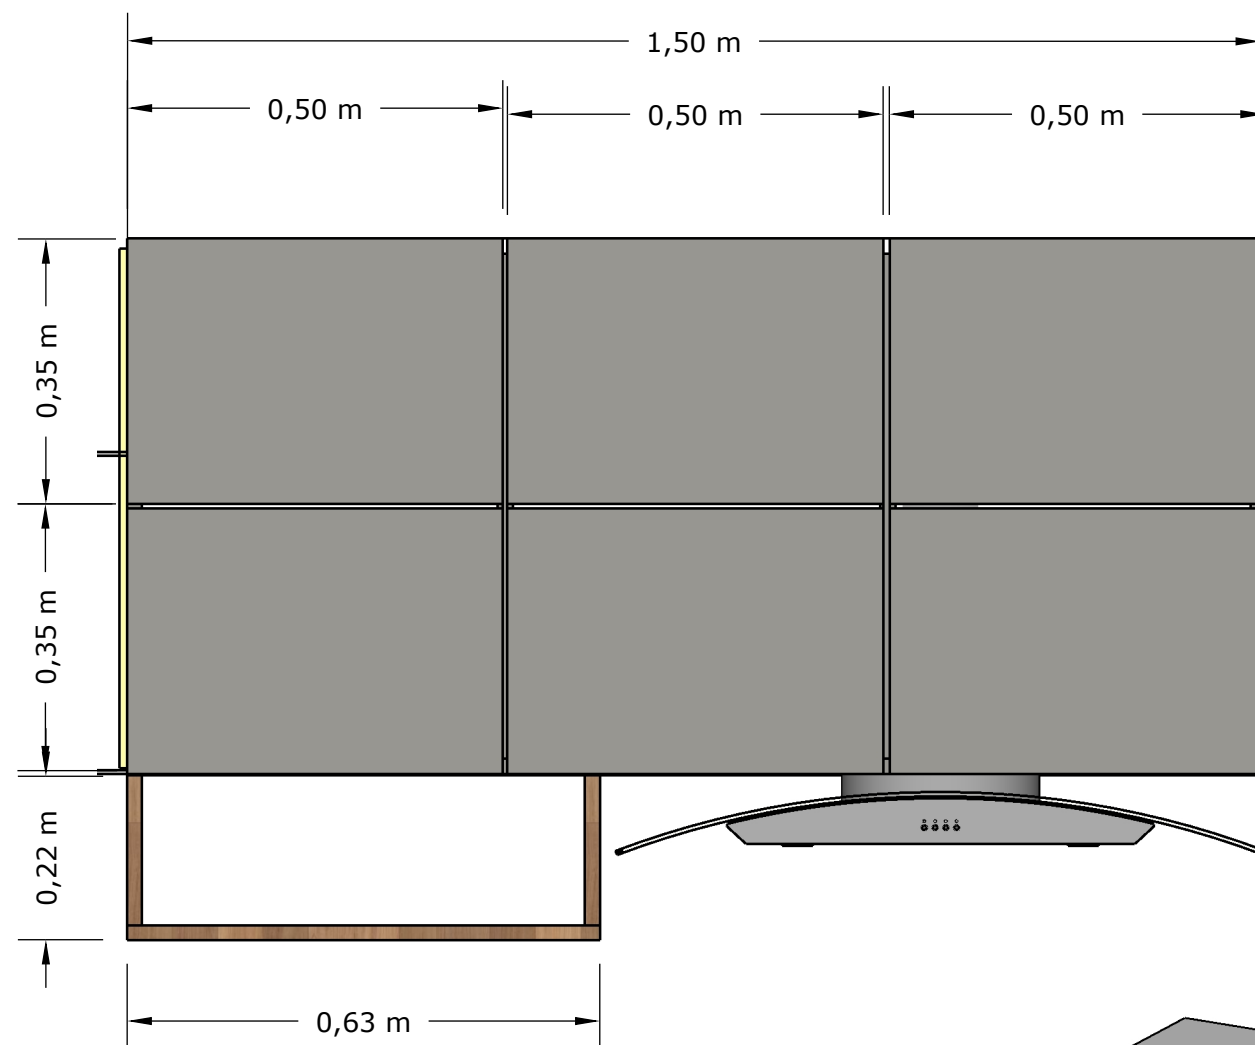


1 VISTA 2
1:10


3 PESPECTIVA
SEM ESCALA

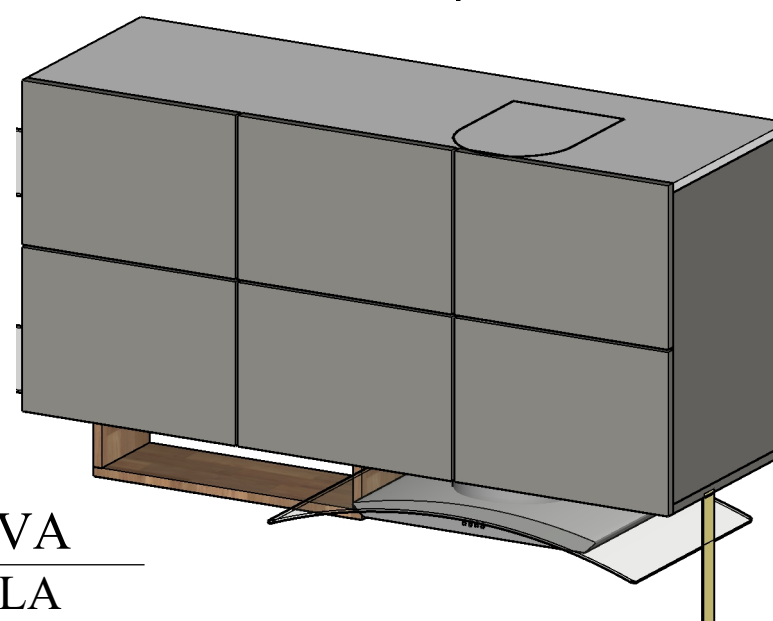

- DEFINIR AO DEPURADOR
- PREVER PONTO PARA LED
- PREVER FORNTE DE ENERGIA PARA DEPURADOR

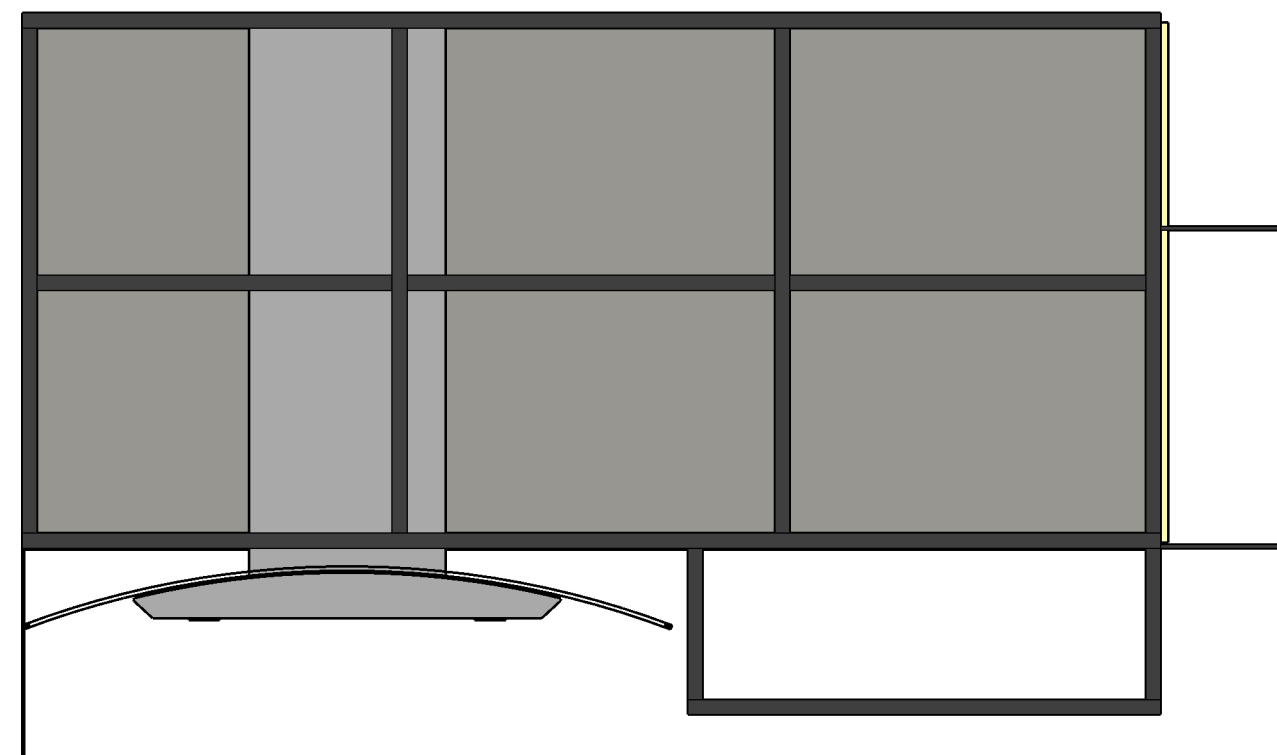

2 VISTA 2
1:10

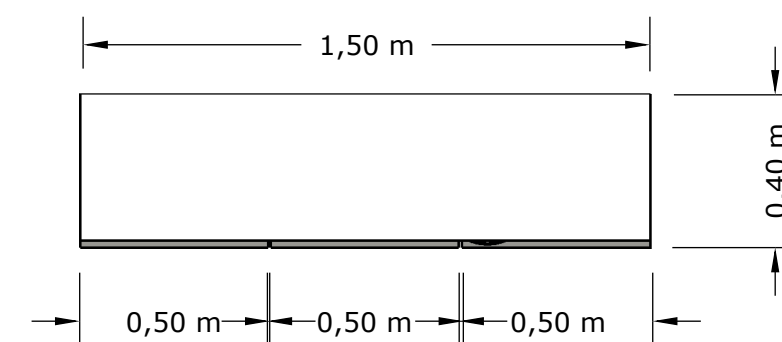

4 VISTA 2
1:20

MATERIAL	ESPESSURA	COMPRIMENTO	LARGURA	M²
MDF CINZA SAGRADO	0.15	0.81	2.20	1.78
MDF CINZA SAGRADO	0.15	0.79	2.2	1.74
MDF CINZA SAGRADO	0.15	0.79	2.2	1.74
MDF CINZA SAGRADO	0.15	0.8	0.13	0.10
MDF CINZA SAGRADO	0.15	0.8	0.13	0.10
MDF CINZA SAGRADO	0.15	0.16	2.09	0.33
MDF CINZA SAGRADO	0.15	0.8	0.13	0.10
MDF CINZA SAGRADO	0.15	0.5	0.71	0.36
MDF CINZA SAGRADO	0.15	0.5	0.71	0.36
MDF CINZA SAGRADO	0.15	0.47	0.67	0.31
MDF CINZA SAGRADO	0.15	1.51	0.48	0.72
MDF CINZA SAGRADO	0.15	0.5	0.71	0.36
MDF CINZA SAGRADO	0.15	0.5	0.71	0.36
MDF CINZA SAGRADO	0.15	0.67	0.47	0.31
MDF CINZA SAGRADO	0.15	0.5	0.71	0.36
MDF CINZA SAGRADO	0.15	0.5	0.71	0.36
MDF CINZA SAGRADO	0.15	0.81	0.79	0.64
MDF CINZA SAGRADO	0.15	0.51	0.29	0.15
MDF CINZA SAGRADO	0.15	0.51	0.29	0.15
MDF CINZA SAGRADO	0.15	0.55	0.18	0.10
MDF CINZA SAGRADO	0.15	0.2	2.2	0.44
MDF CINZA SAGRADO	0.15	0.79	0.81	0.64
MDF CINZA SAGRADO	0.15	0.81	0.79	0.64
MDF CINZA SAGRADO	0.15	0.8	0.13	0.10
MDF CINZA SAGRADO	0.15	0.55	0.19	0.10
MDF CINZA SAGRADO	0.15	0.55	0.19	0.10
MDF CINZA SAGRADO	0.15	0.5	0.71	0.36
MDF CINZA SAGRADO	0.15	0.81	2.2	1.78
MDF CINZA SAGRADO	0.15	0.5	0.71	0.36
MDF CINZA SAGRADO	0.15	0.55	0.04	0.02
MDF CINZA SAGRADO	0.15	0.69	1.31	0.90
MDF CINZA SAGRADO	0.15	0.2	2.2	0.44
MDF CINZA SAGRADO	0.15	0.12	2.2	0.26
MDF CINZA SAGRADO	0.15	0.51	0.26	0.13
MDF CINZA SAGRADO	0.15	0.51	0.26	0.13
MDF CINZA SAGRADO	0.15	0.51	0.14	0.07
MDF CINZA SAGRADO	0.15	0.51	0.14	0.07
MDF CINZA SAGRADO	0.15	0.8	0.13	0.10
MDF CINZA SAGRADO	0.15	0.8	0.13	0.10
MDF CINZA SAGRADO	0.15	0.8	0.13	0.10
MDF CINZA SAGRADO	0.15	0.8	0.13	0.10
MDF CINZA SAGRADO	0.15	0.16	2.09	0.33
MDF CINZA SAGRADO	0.15	0.12	2.2	0.26
TOTAL				18.00

1 TABELA SEM ESCALA

MATERIAL	ESPESSURA	COMPRIMENTO	LARGURA	M²
MDF BRANCO	1 m	0.66	0.67	0.44
MDF BRANCO	1 m	0.79	0.7	0.55
MDF BRANCO	1 m	0.49	0.47	0.23
MDF BRANCO	1 m	0.47	0.47	0.22
MDF BRANCO	1 m	0.47	0.47	0.22
MDF BRANCO	1 m	0.47	0.05	0.02
MDF BRANCO	1 m	0.79	2.2	1.74
MDF BRANCO	1 m	0.55	0.09	0.05
MDF BRANCO	1 m	1.71	1.78	3.04
MDF BRANCO	1 m	1.71	1.78	3.04
MDF BRANCO	1 m	0.47	0.67	0.31
MDF BRANCO	1 m	0.55	0.19	0.10
MDF BRANCO	1 m	0.55	0.19	0.10
MDF BRANCO	1 m	0.18	0.57	0.10
MDF BRANCO	1 m	0.18	0.57	0.10
MDF BRANCO	1 m	0.77	0.67	0.52

2 TABELA SEM ESCALA

CINZA SAGRADO				
MDF²	M²	QUANTIDADE	VALOR UNI	TOTAL
5.0875	20.35	4	R\$ 604.02	R\$ 2,416.08
	20.35			
NECESSARIO:		18.00		

MDF BRANCO FUNDO				
MDF²	M²	QUANTIDADE	VALOR UNI	TOTAL
5.0875	10.175	2	R\$ 272.00	R\$ 544.00
	10.175			
NECESSARIO:		13.14		


MDF BRANCO FUNDO				
MDF²	M²	QUANTIDADE	VALOR UNI	TOTAL
5.0875	10.175	2	R\$ 272.00	R\$ 544.00
	10.175			
NECESSARIO:		5.32		

4 PRECIFICAÇÃO SEM ESCALA


- PRECIFICAÇÃO FEITO NA LEO MADEIRA
- QUANTITIVO FEITO NO SKETCHUP,
PREVER AJUSTE NA QUANTIDADE.

MATERIAL	ESPESSURA	COMPRIMENTO	LARGURA	M²
MDF BRANCO	0.01	0.55	0.2	0.11
MDF BRANCO	0.01	1.51	0.67	1.01
MDF BRANCO	1 m	0.81	2.2	1.78
MDF BRANCO	0.01	0.4	0.18	0.07
MDF BRANCO	1 m	0.47	0.7	0.33


3 TABELA SEM ESCALA

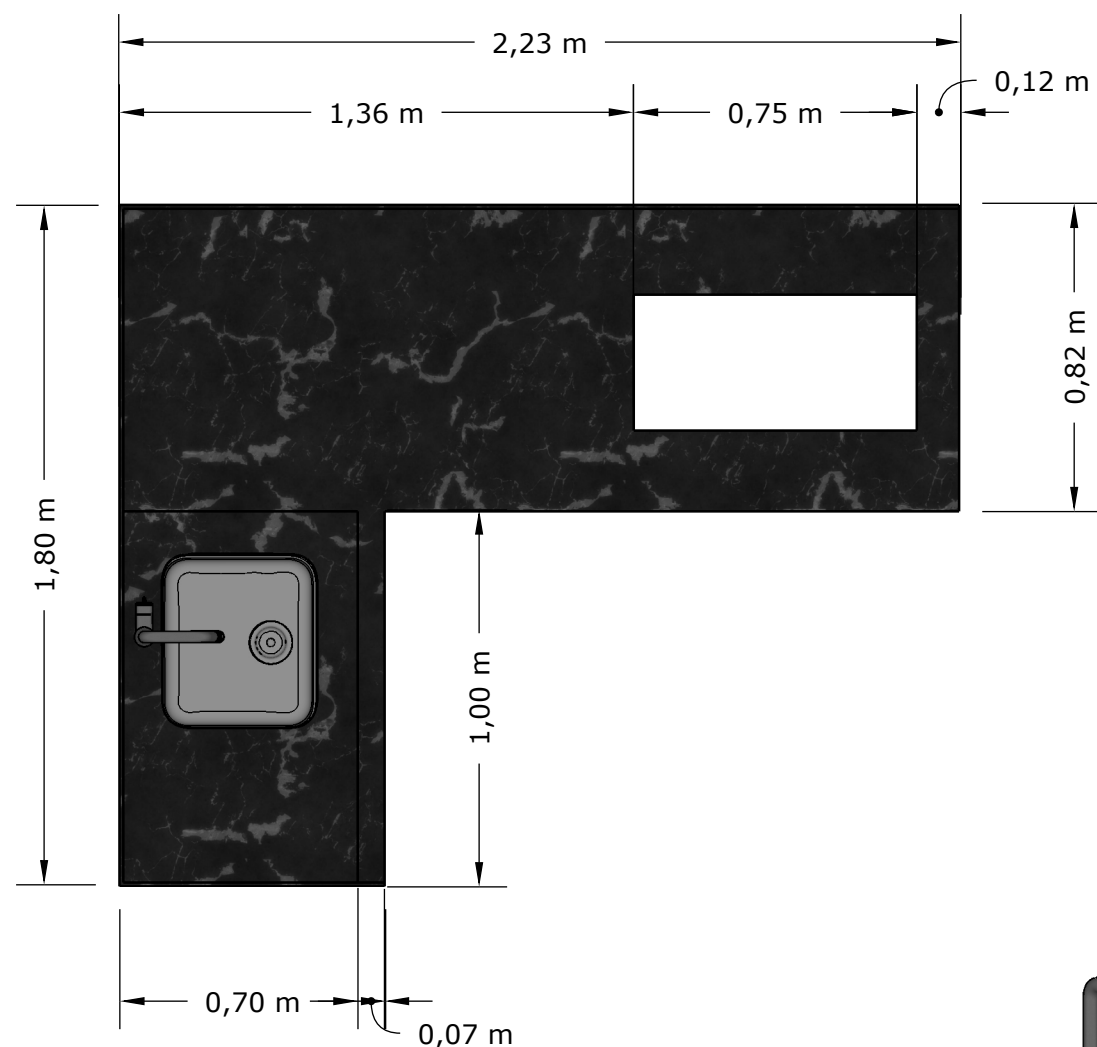

1 PLANTA
1:20

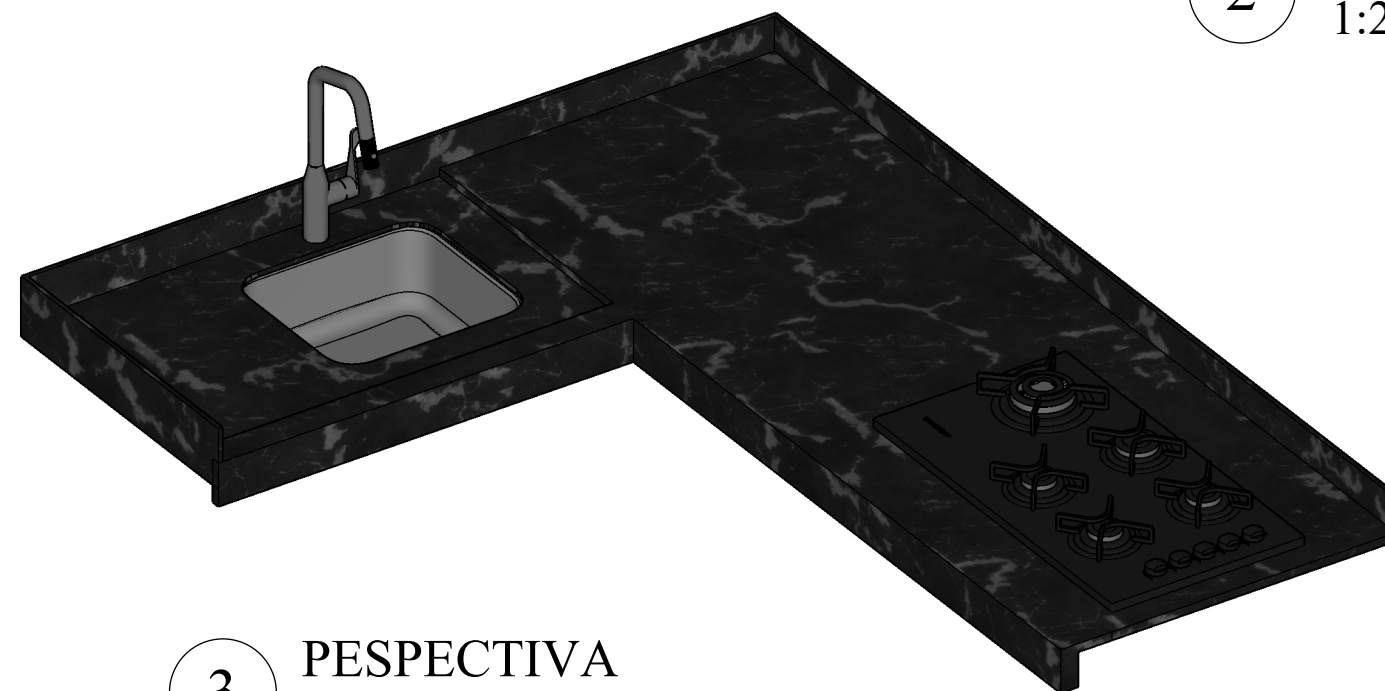

3 PESPECTIVA
SEM ESCALA

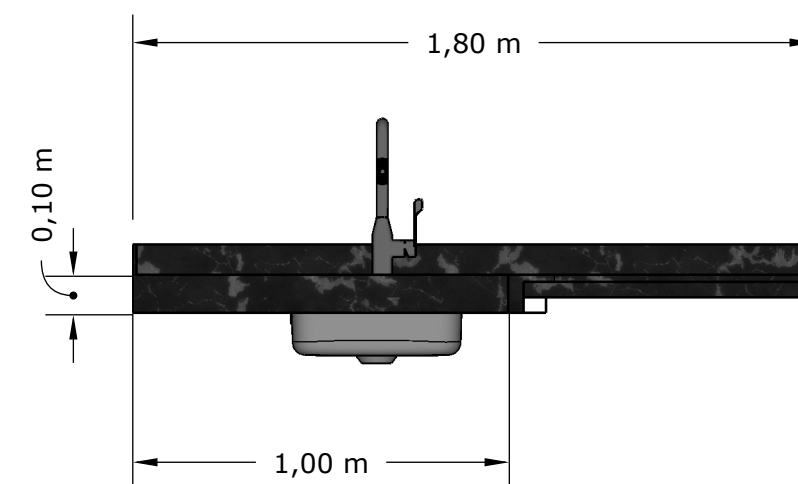

2 VISTA 2
1:20

- CONFERIR AS MEDIDAS DO COOKTOP ANTES DO CORTE
- CONSULTAR AS MEDIDAS DA CUBAS ANTES DO CORTE
- PREVER ALINHAMENTO COM A MACENARIA