
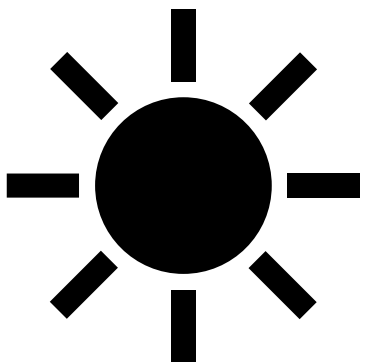


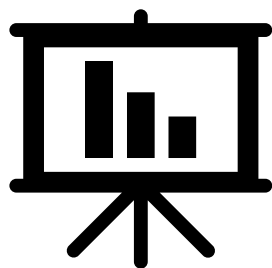


Fundamentos dos quais usamos para desenvolver o projeto


- Legislação municipal, Código de obras.
- Pedidos e ideias das clientes
- Programa de Necessidades
- Orientação Solar

Estudo Volumétrico

- PAV. SUPERIOR

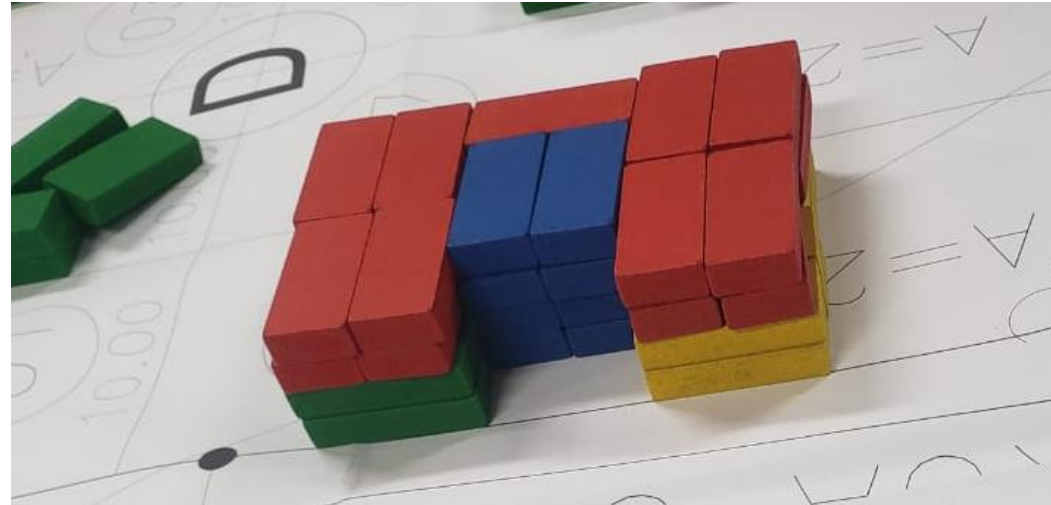

- PAV. INFERIOR

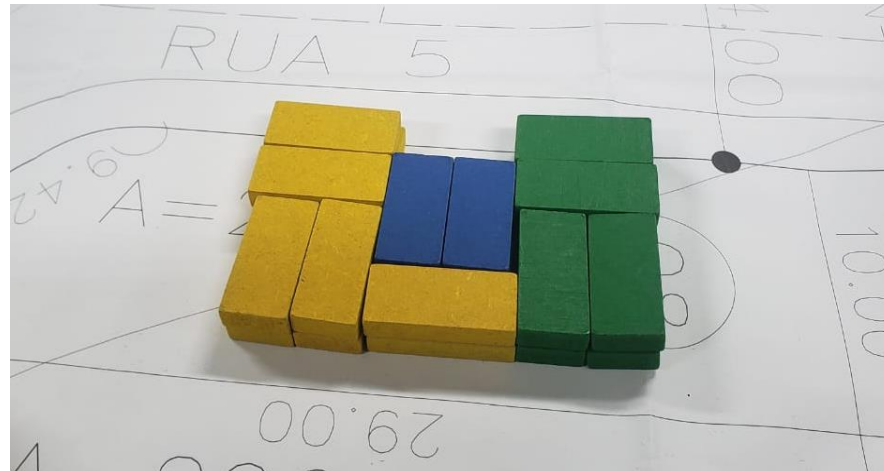

Fichas técnicas


FICHA TÉCNICA

LOCAÇÃO	RUA 5	
ÁREA DO LOTE	290,00 M²	
RECUOS	FROTAL MIN.: 2M	LATERAL MIN.: 1.5
GABARITO	7 M	
	LEGISLAÇÃO	PROJETADO
C.A	299.00 M²	188.90 / 63%
T.O	80%	94.5 M²/ 32%
T.P	20%	59.8 M² / 21%


PROGRAMAS DE NECESSIDADES


COMPATIMENTOS	ÁREA
ÁREA SOCIAL	
SALA	29.50 M²
ESCRITORIO	76.56 M²
LAVABO	3.43 M²
ÁREA DE SERVIÇOS	
COZINHA	25.80 M²
B.W.C SERVIÇOS	3.43 M²
ÁREA DE SERVIÇOS	7.52 M²
ÁREA ÍNTIMA	
DORM. 1	14.70 M²
DORM. 2	12.57 M²
B.W.C SUPERIOR	3.43 M²
B.W.C SUÍTE	3.43 M²
CLOSED	17,79 M²
SUÍTE	17,79 M²
VARANDA	4.61 M²
TERRAÇO	7.15 M²
ÁREA DE CIRCULAÇÃO	
ESCADA	6.00 M²
CIRCULAÇÃO	6.88 M²

PAVIMENTO
SUPERIOR
ESCALA 1:50

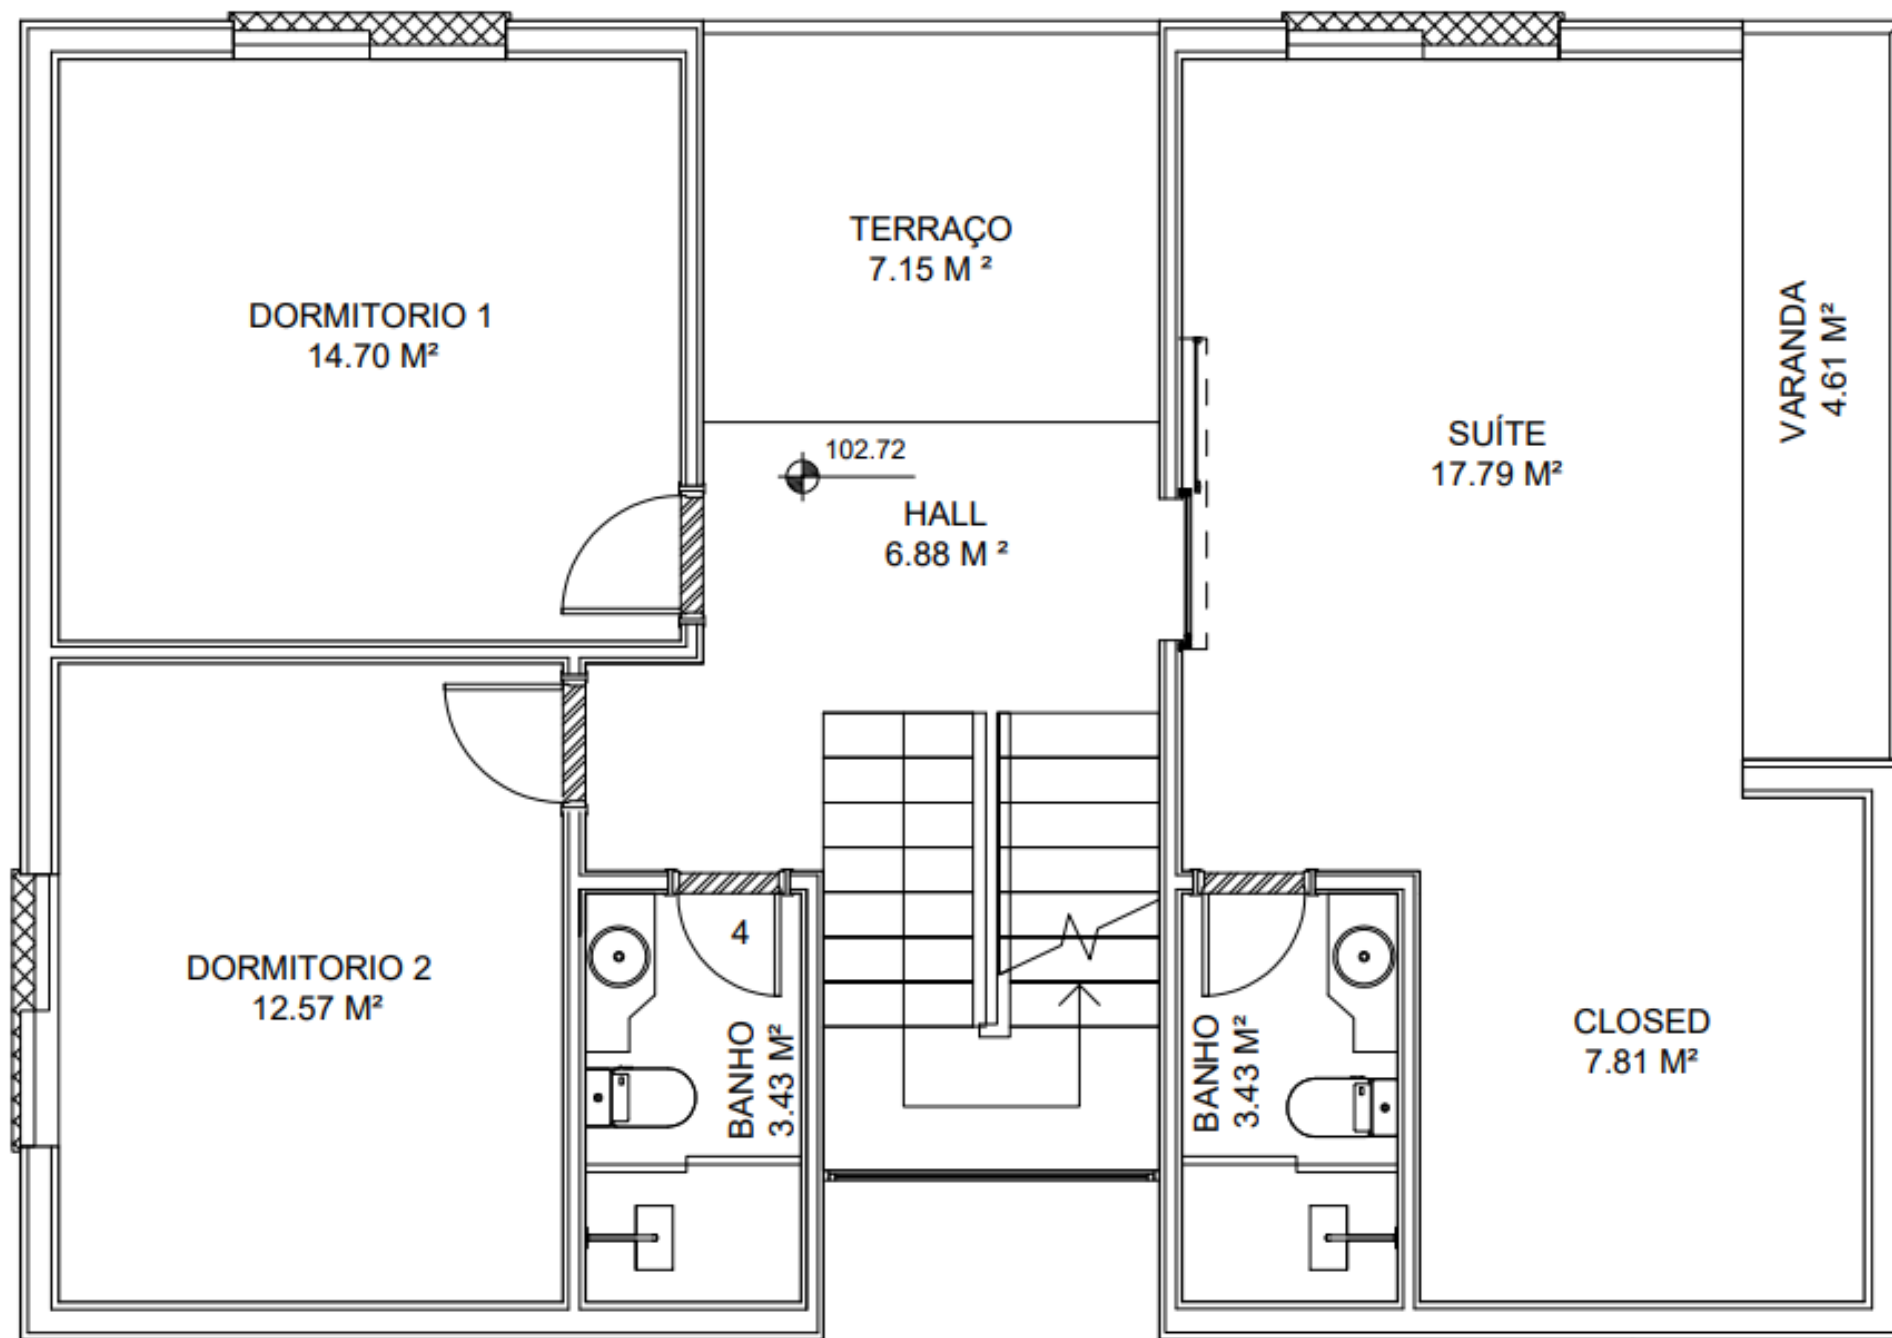


PAVIMENTO
INFERIOR
ESCALA 1:50

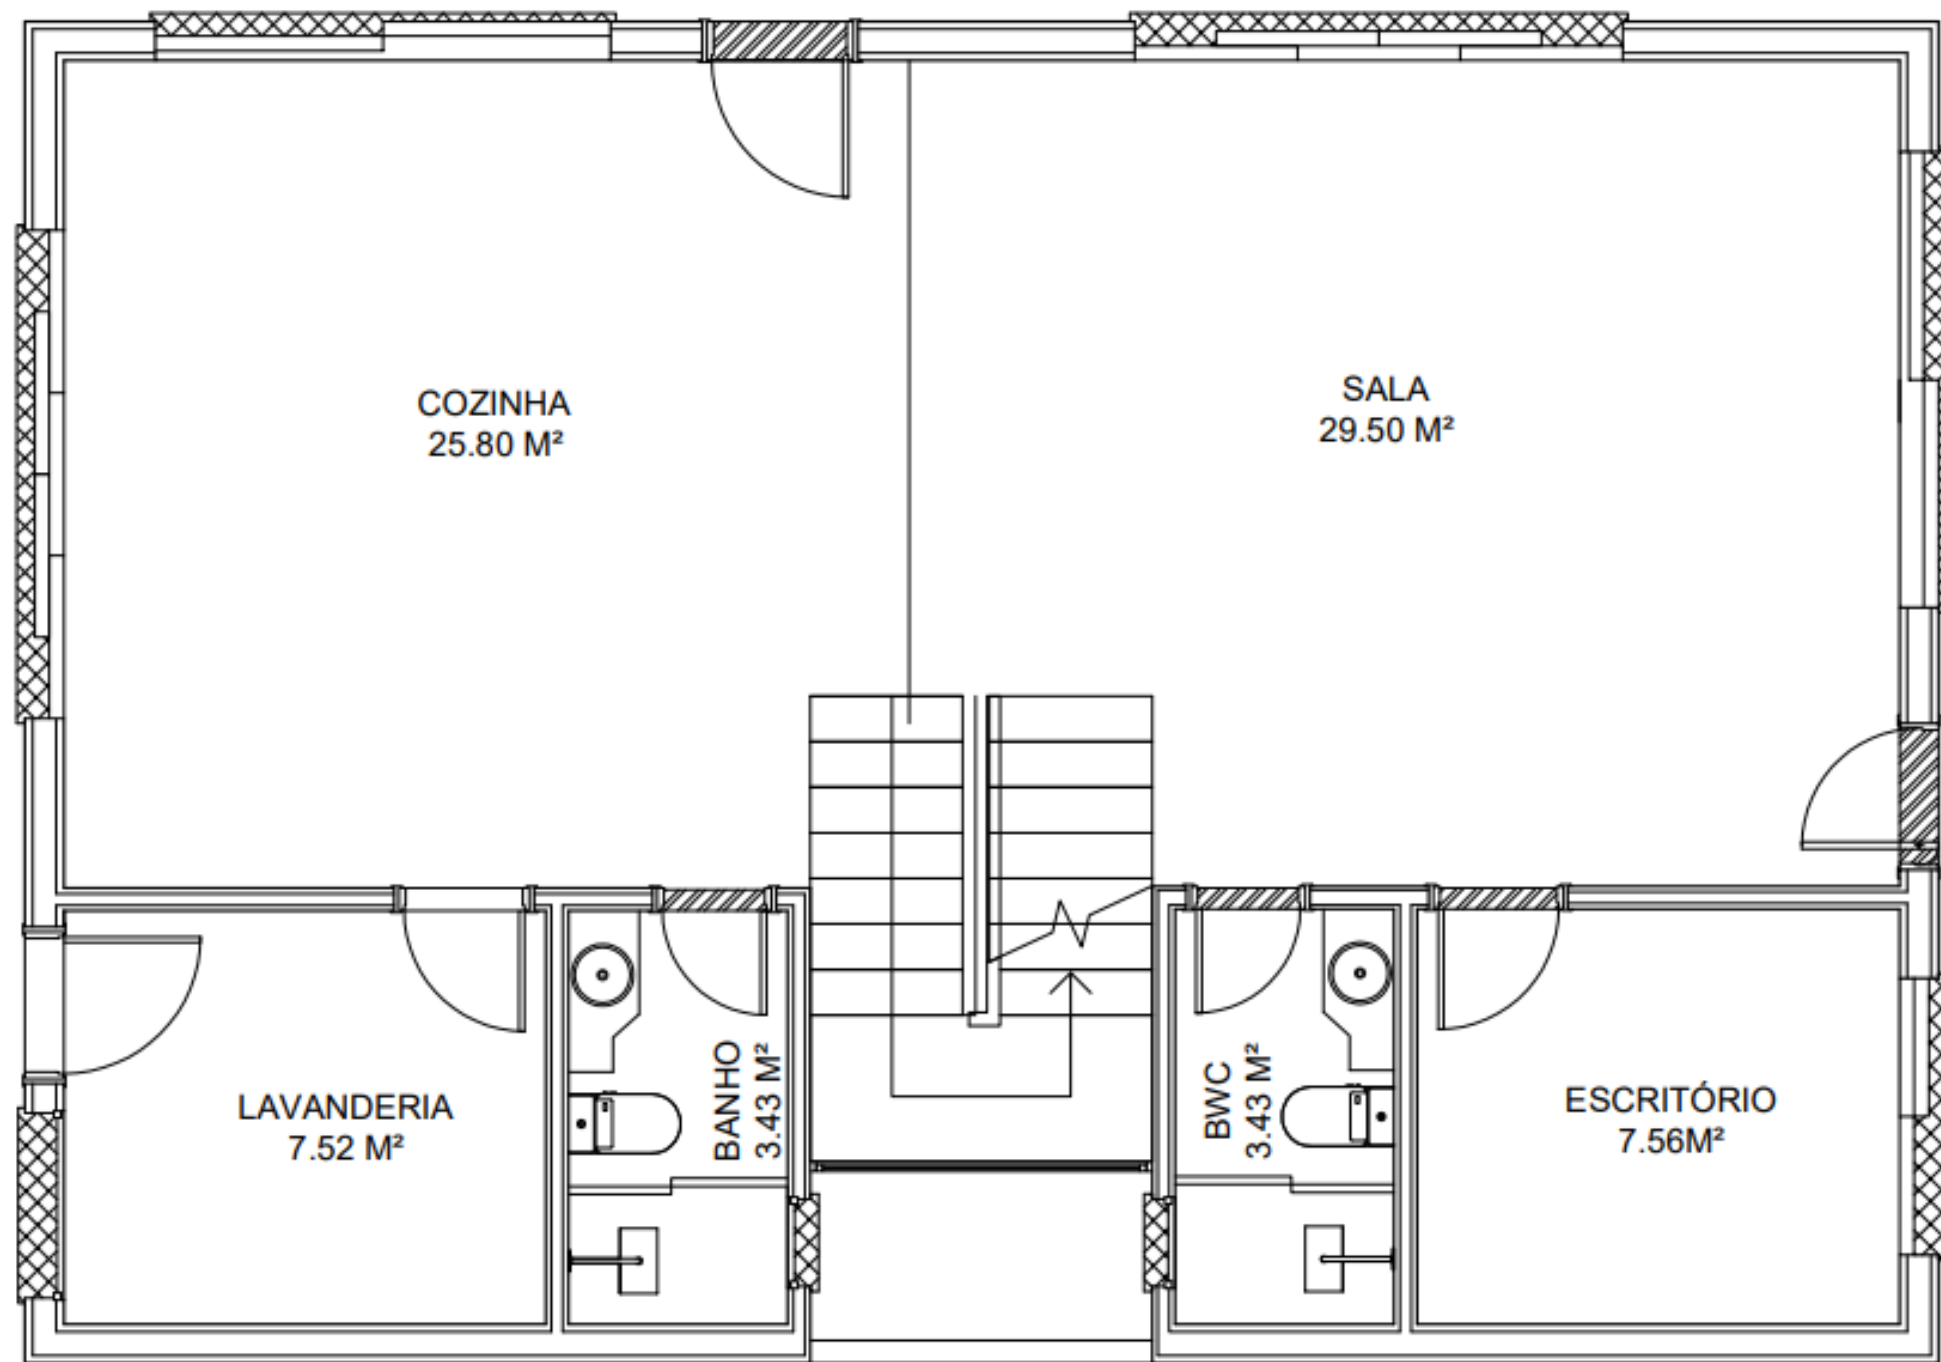


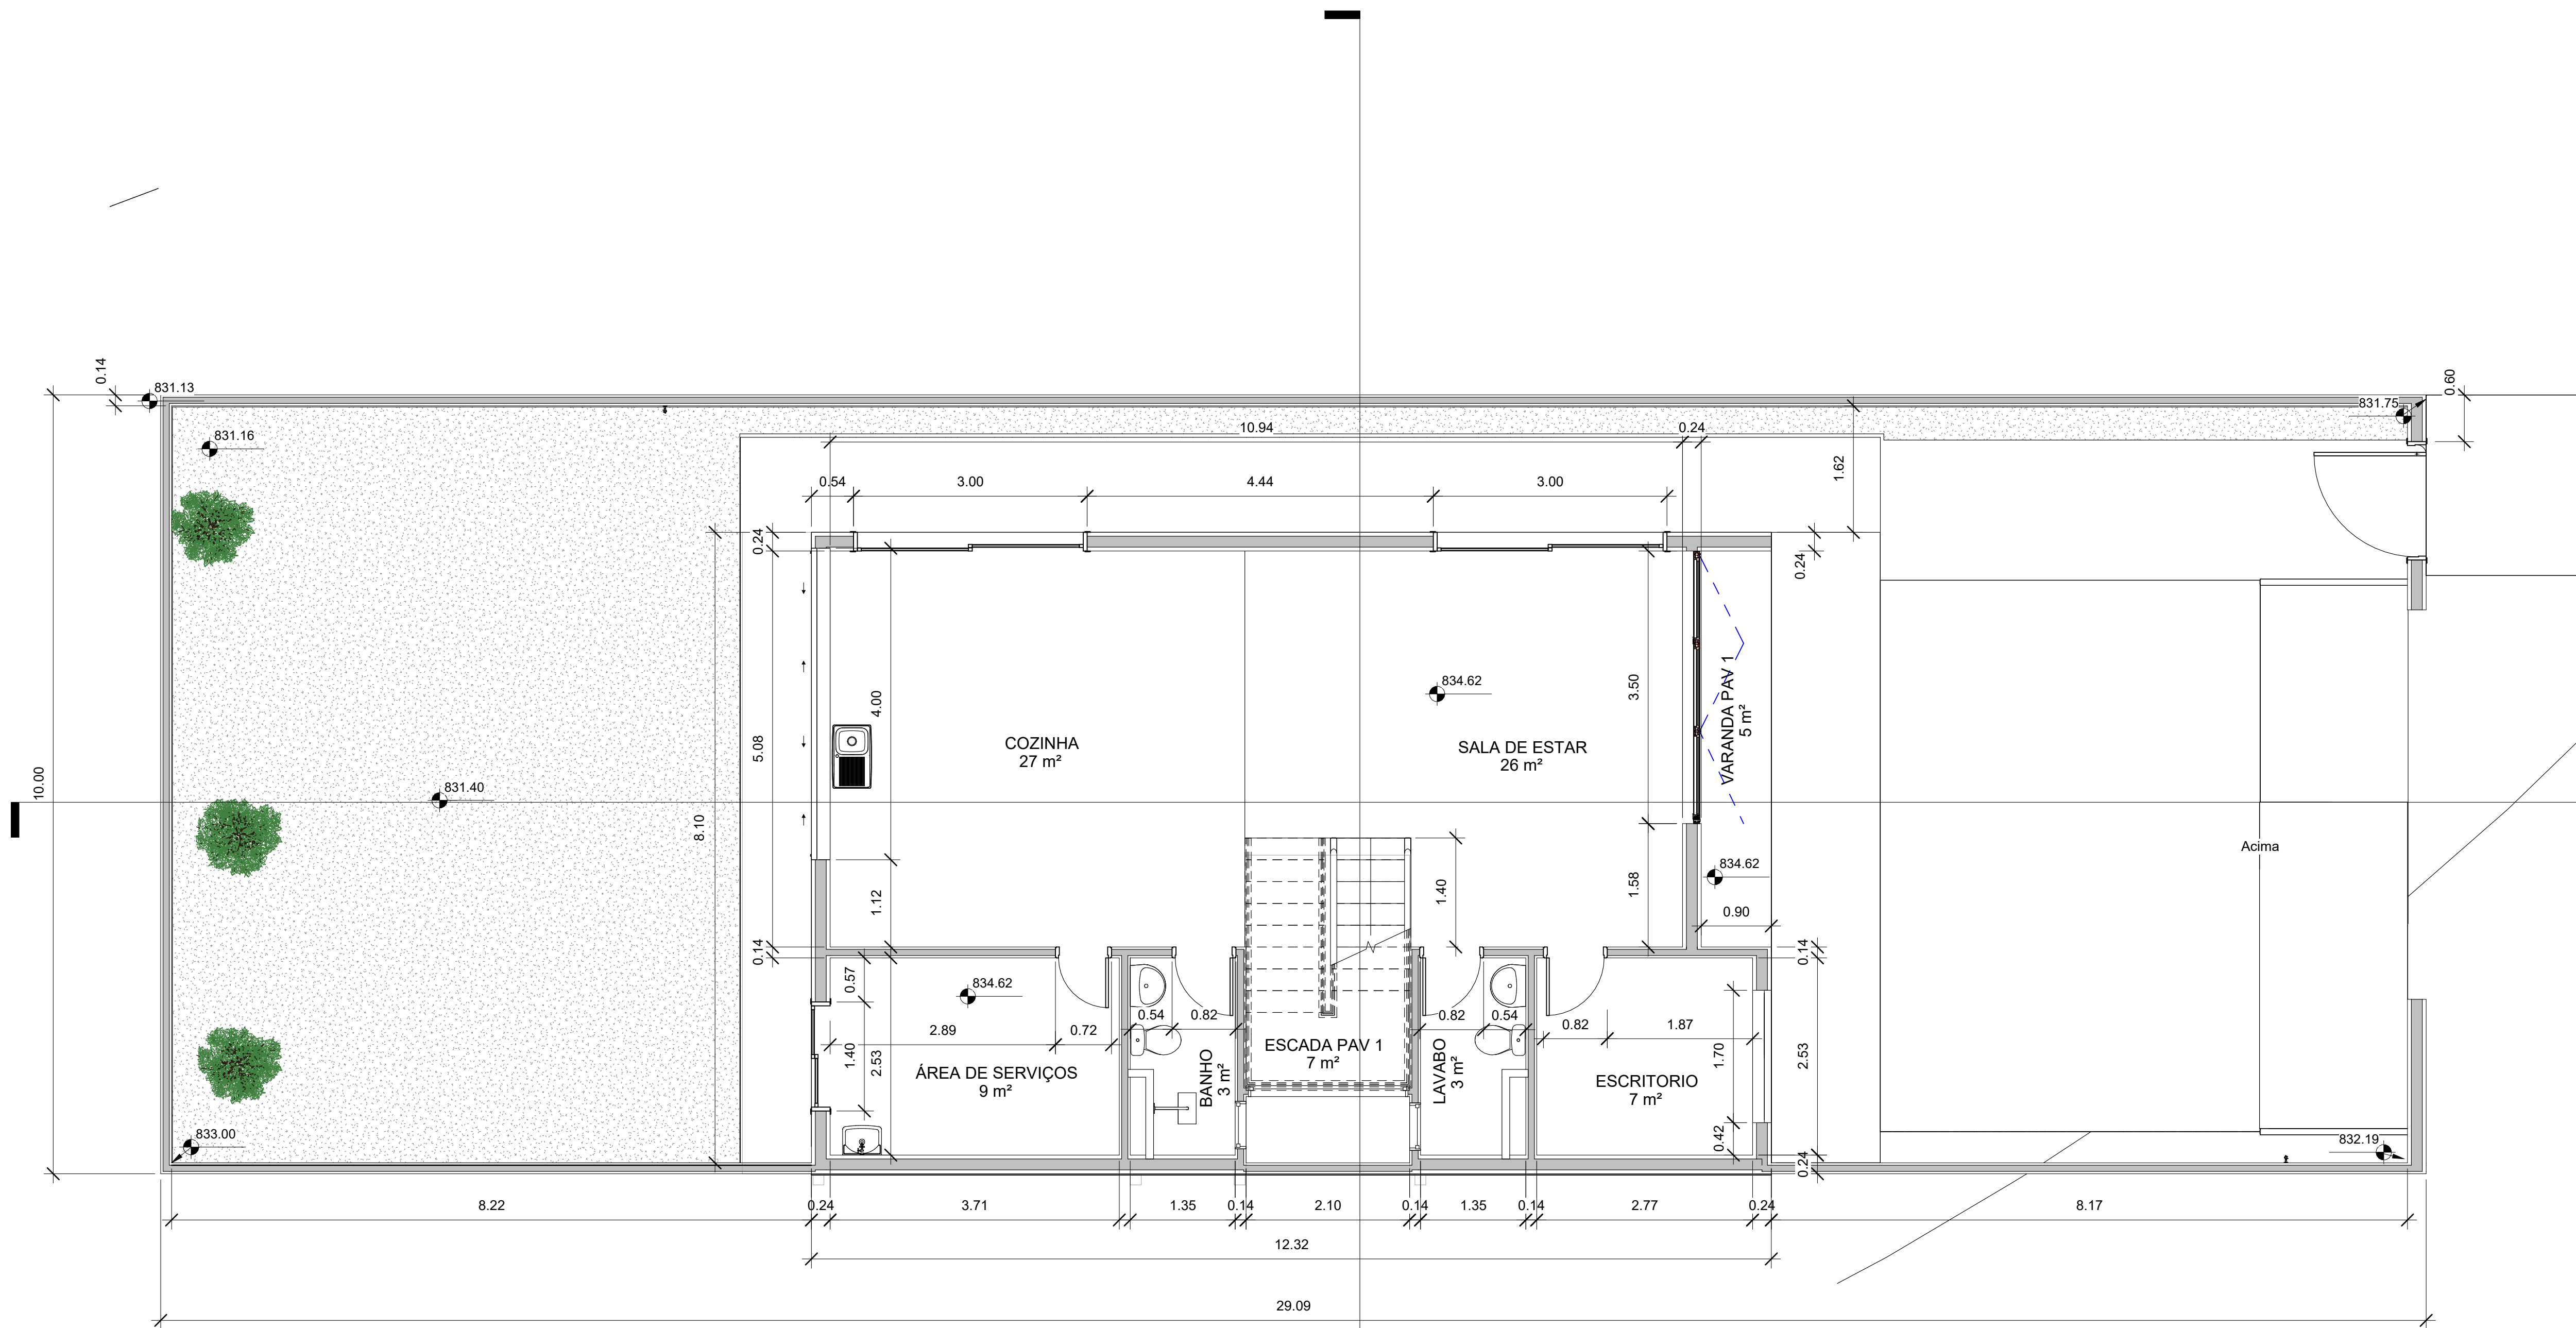


1 PAV 1
1 : 50

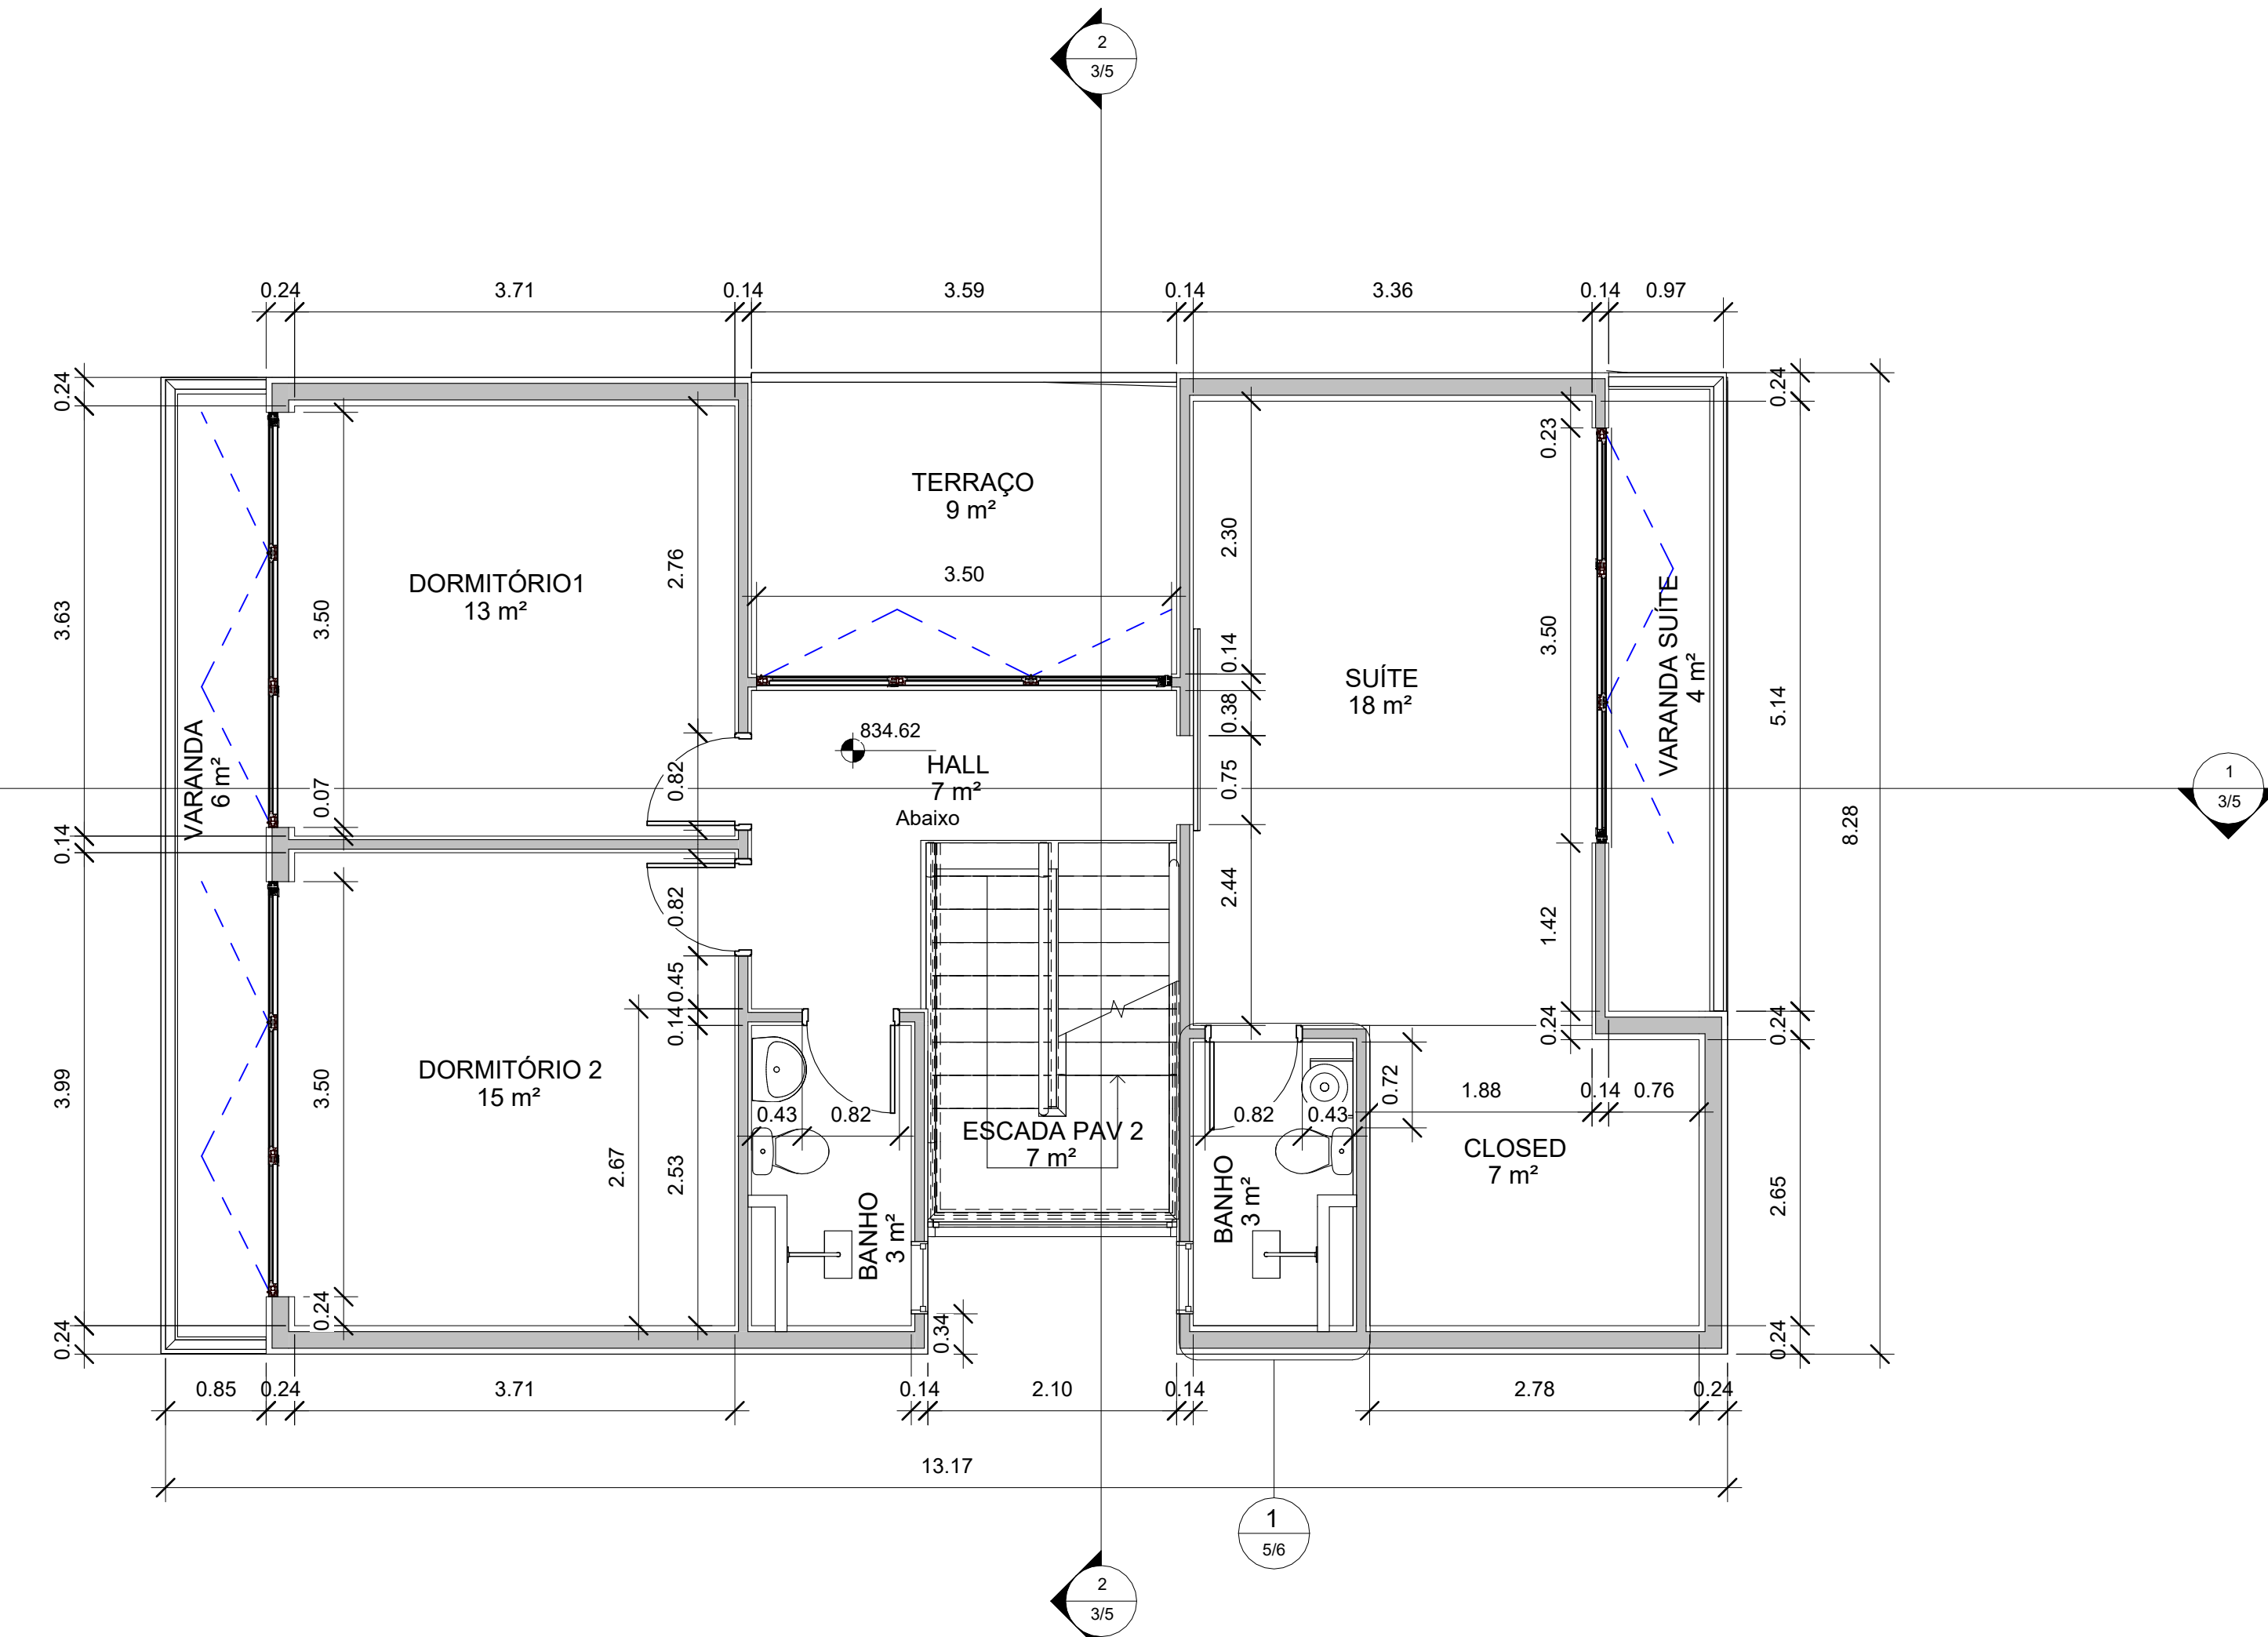


2 PAV 2
1 : 50

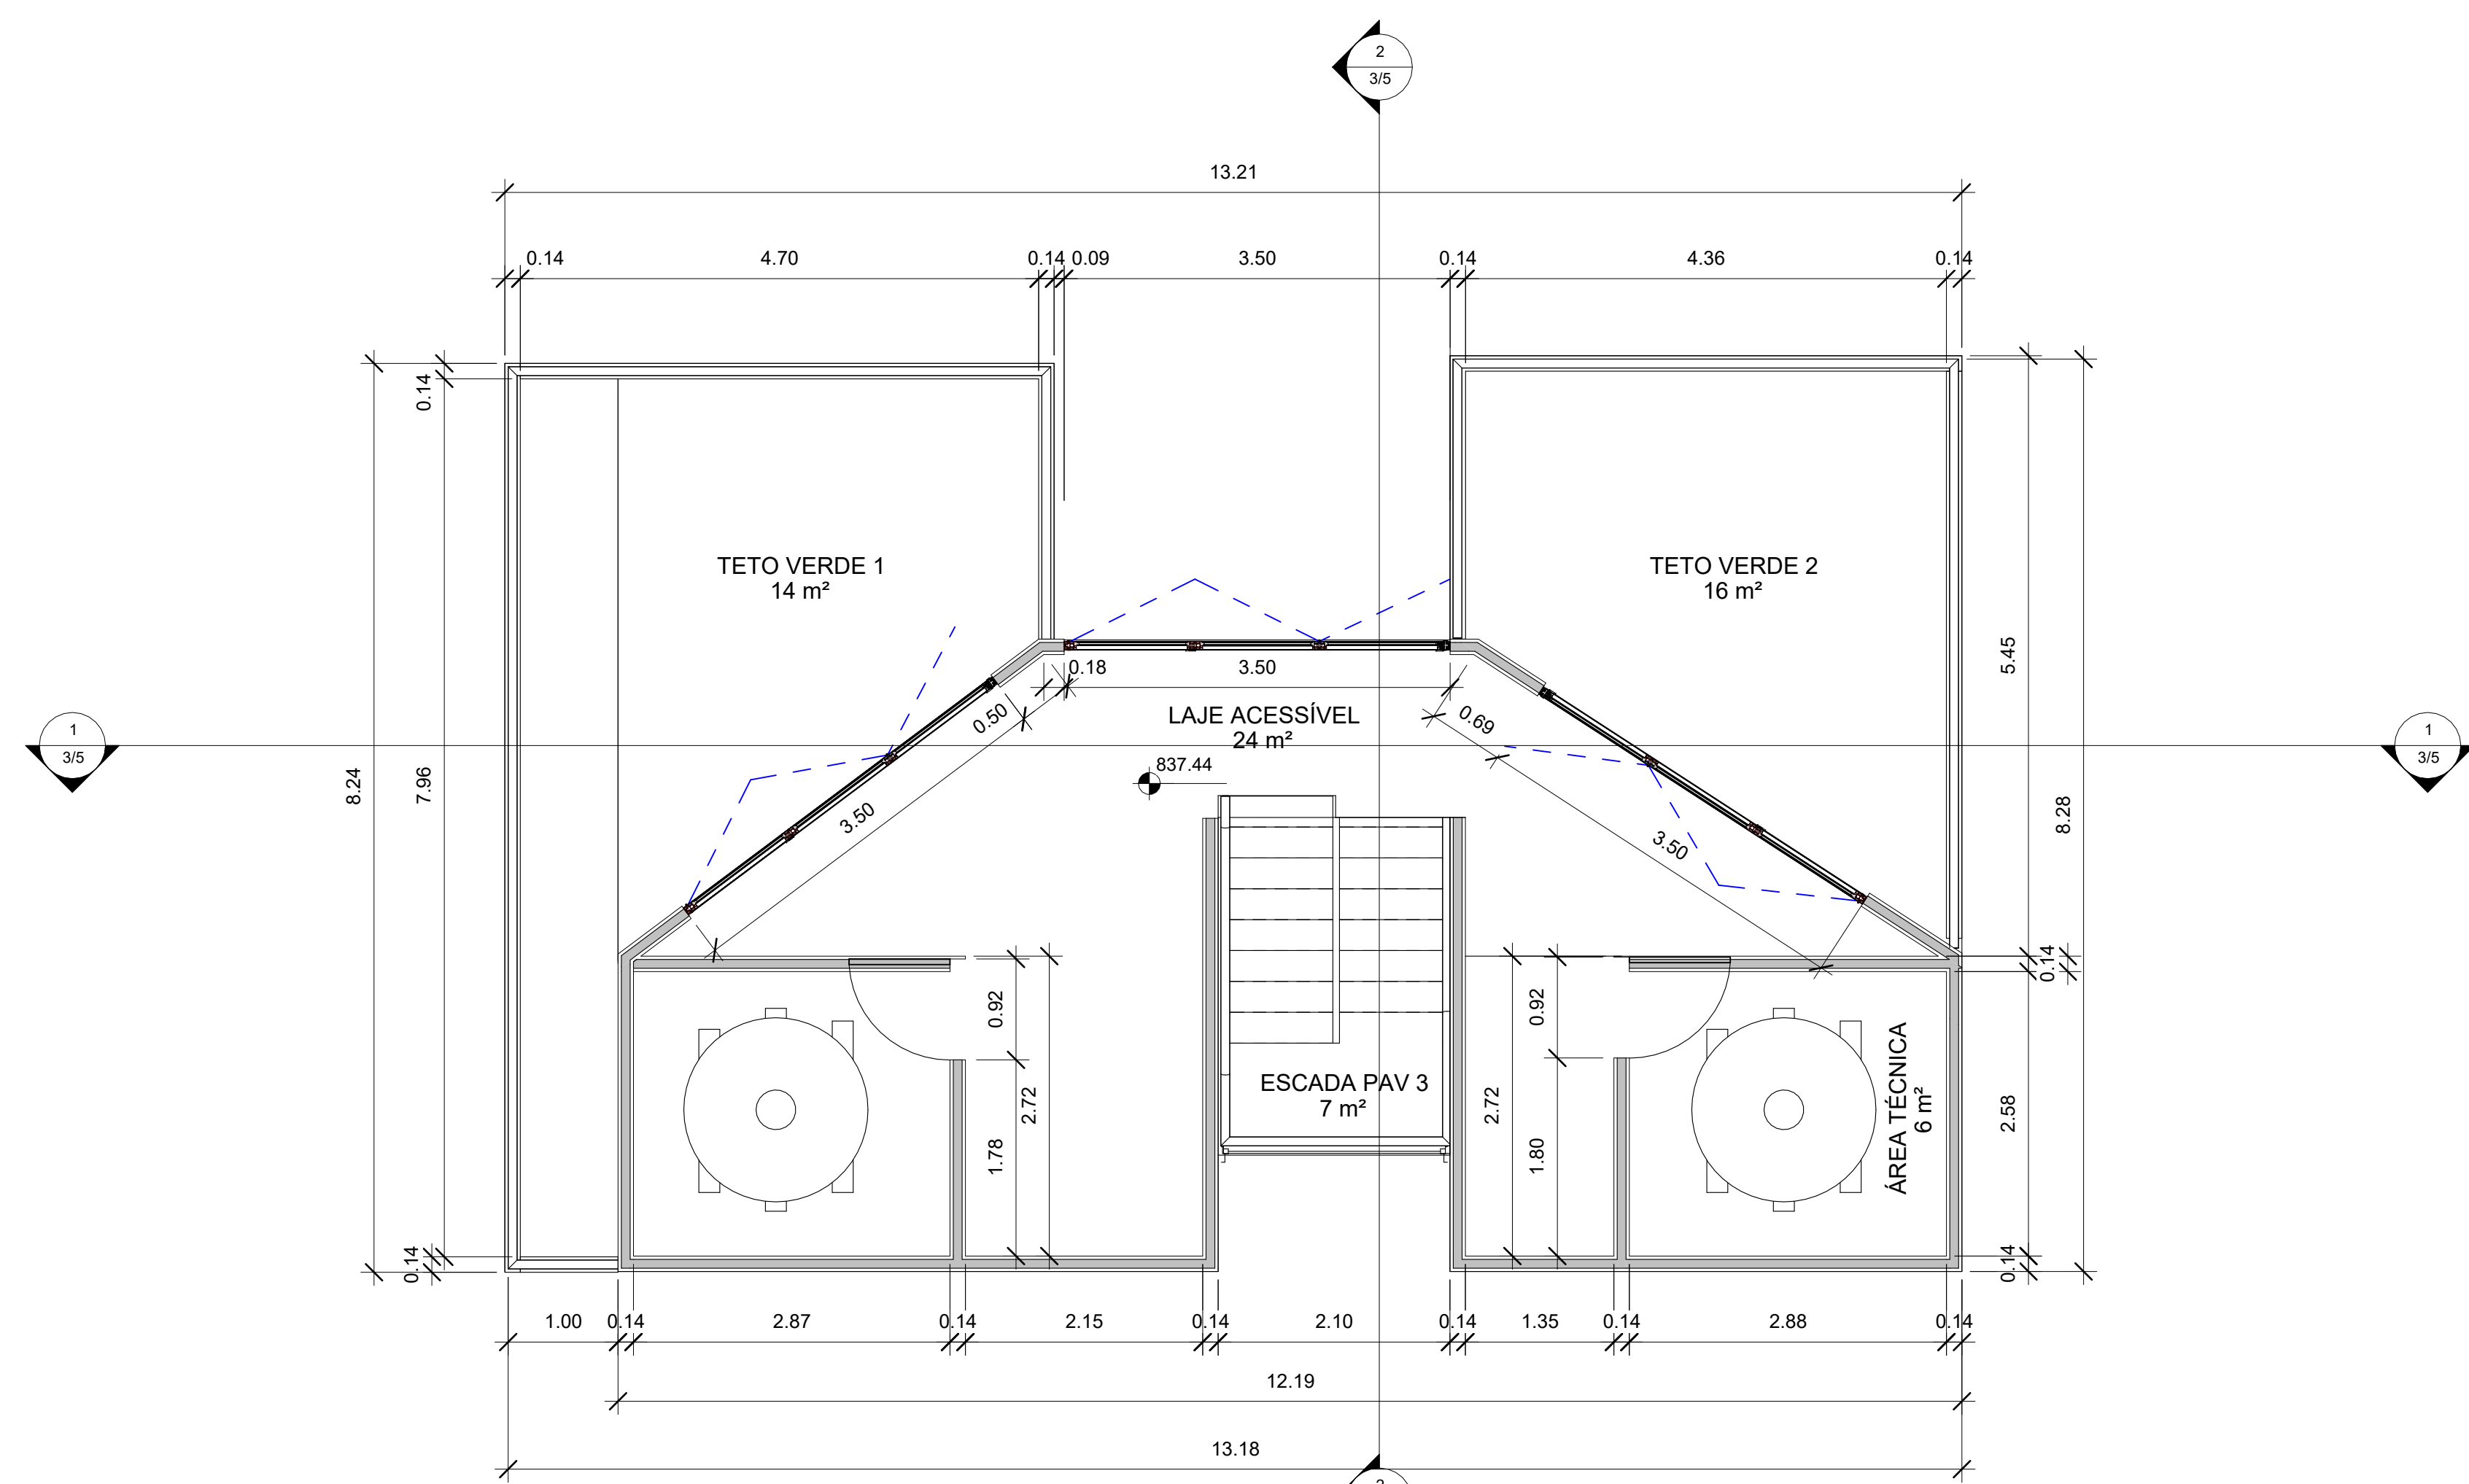


3 PAV 3
1 : 50

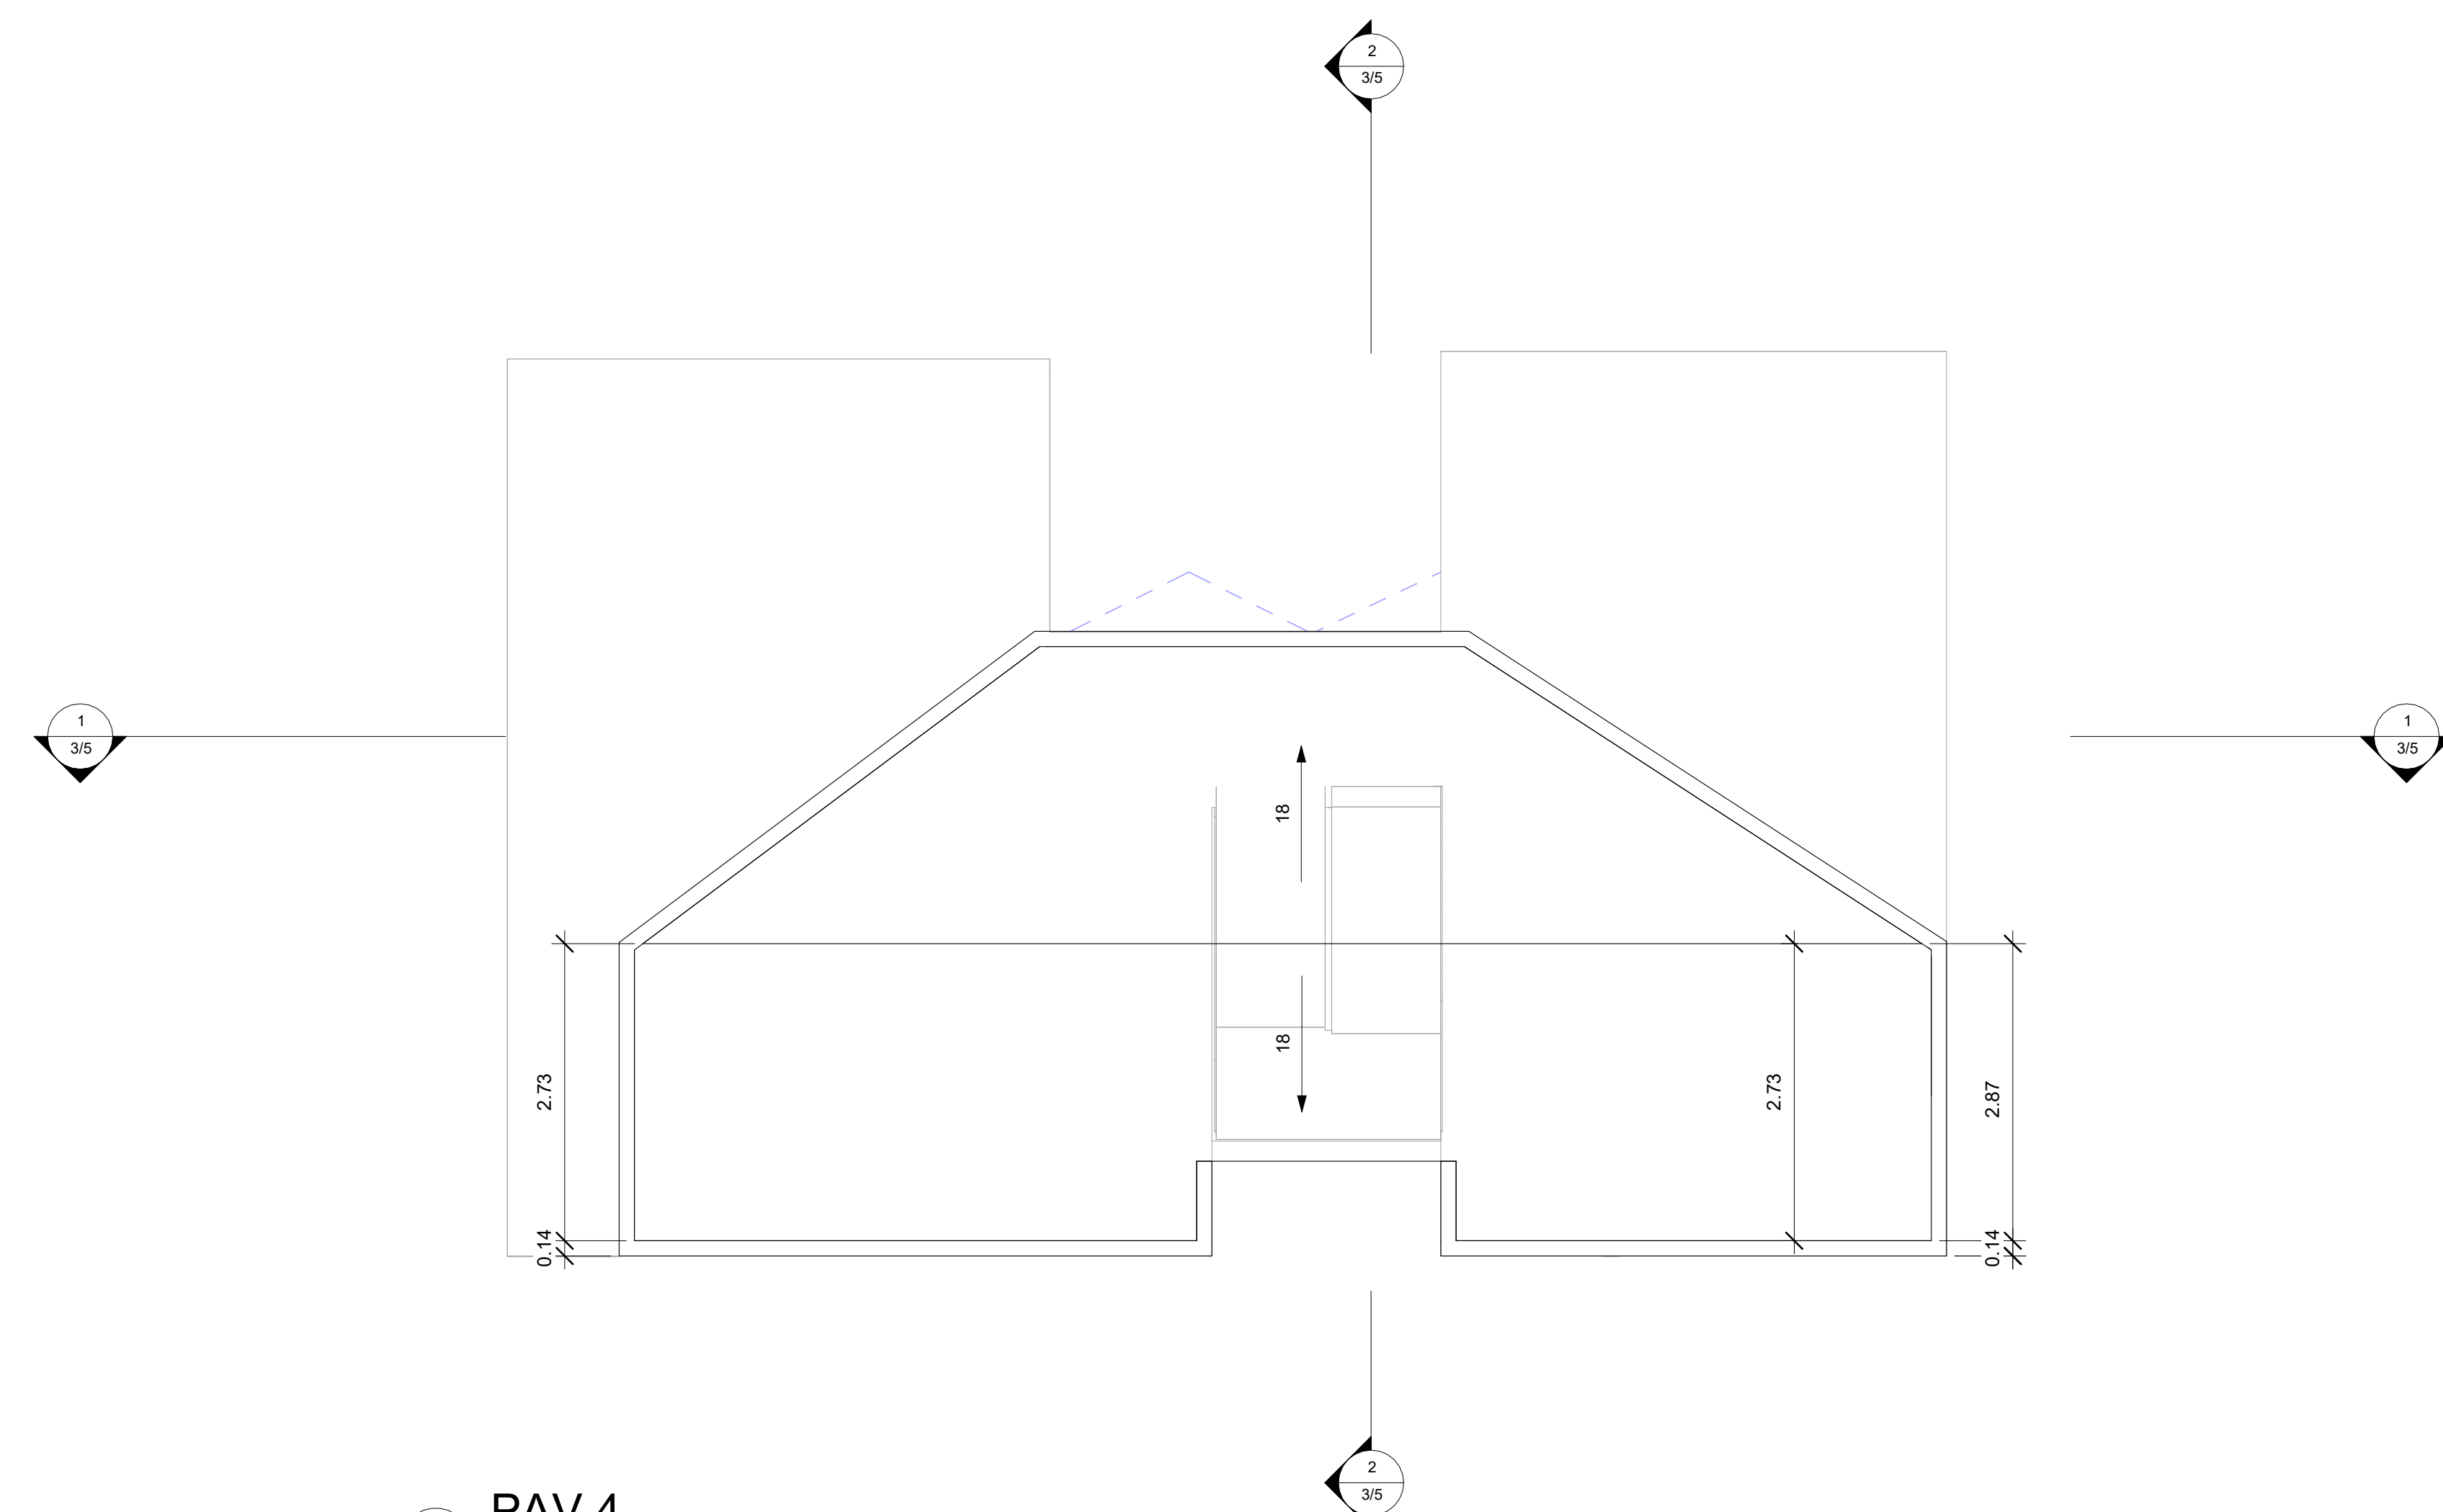


4 PAV 4
1 : 50

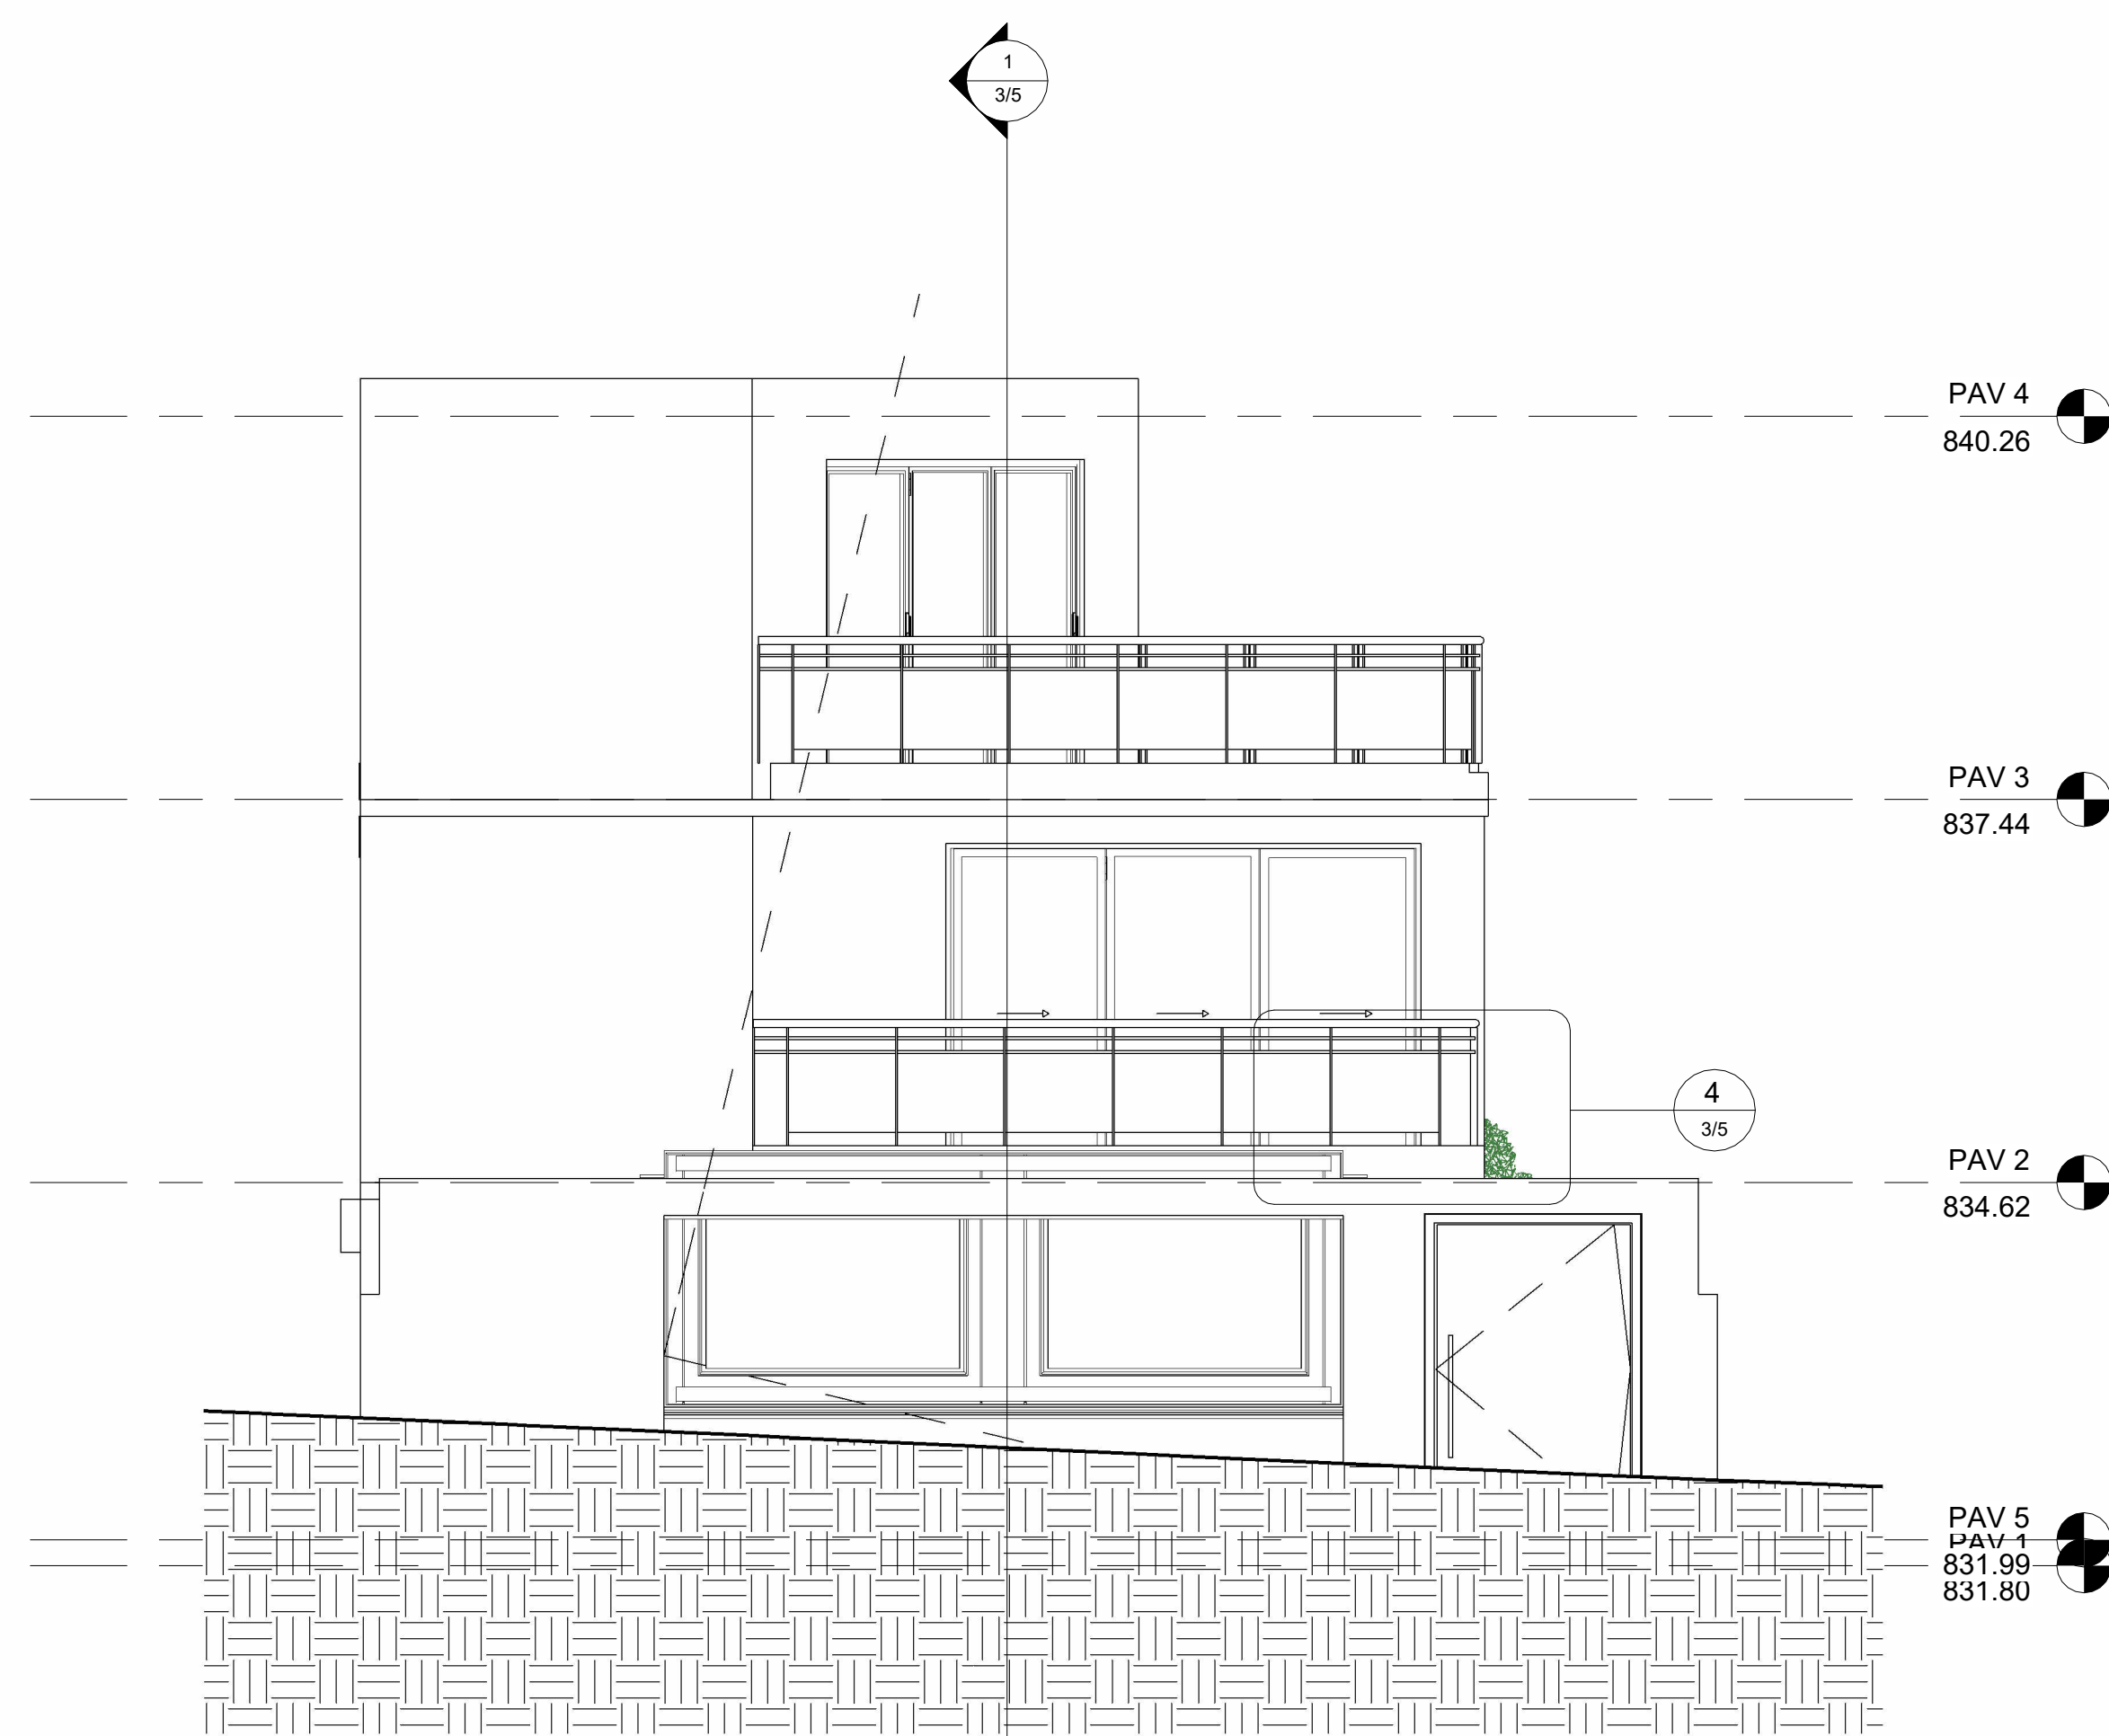


1 Leste
1 : 50

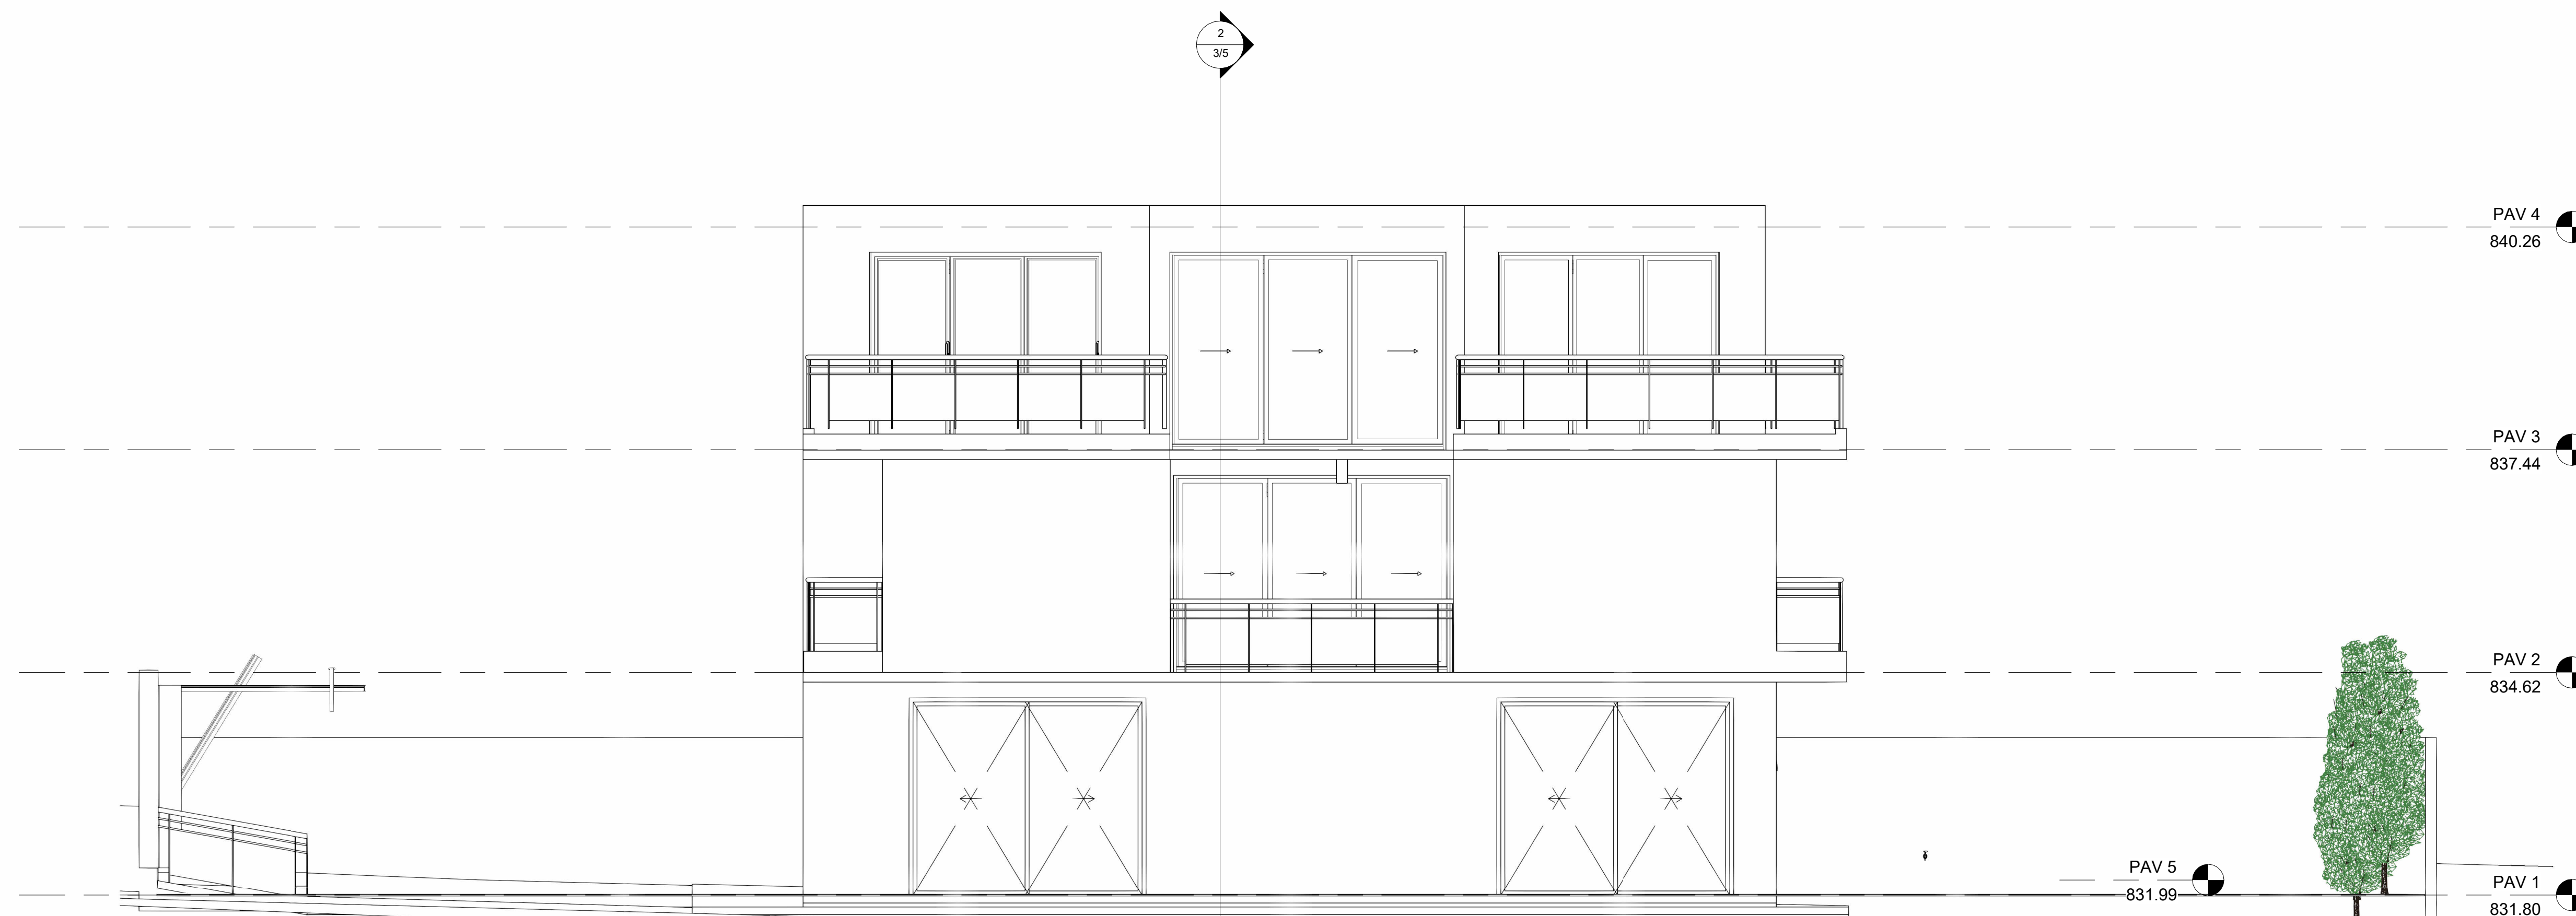


2 Norte
1 : 50

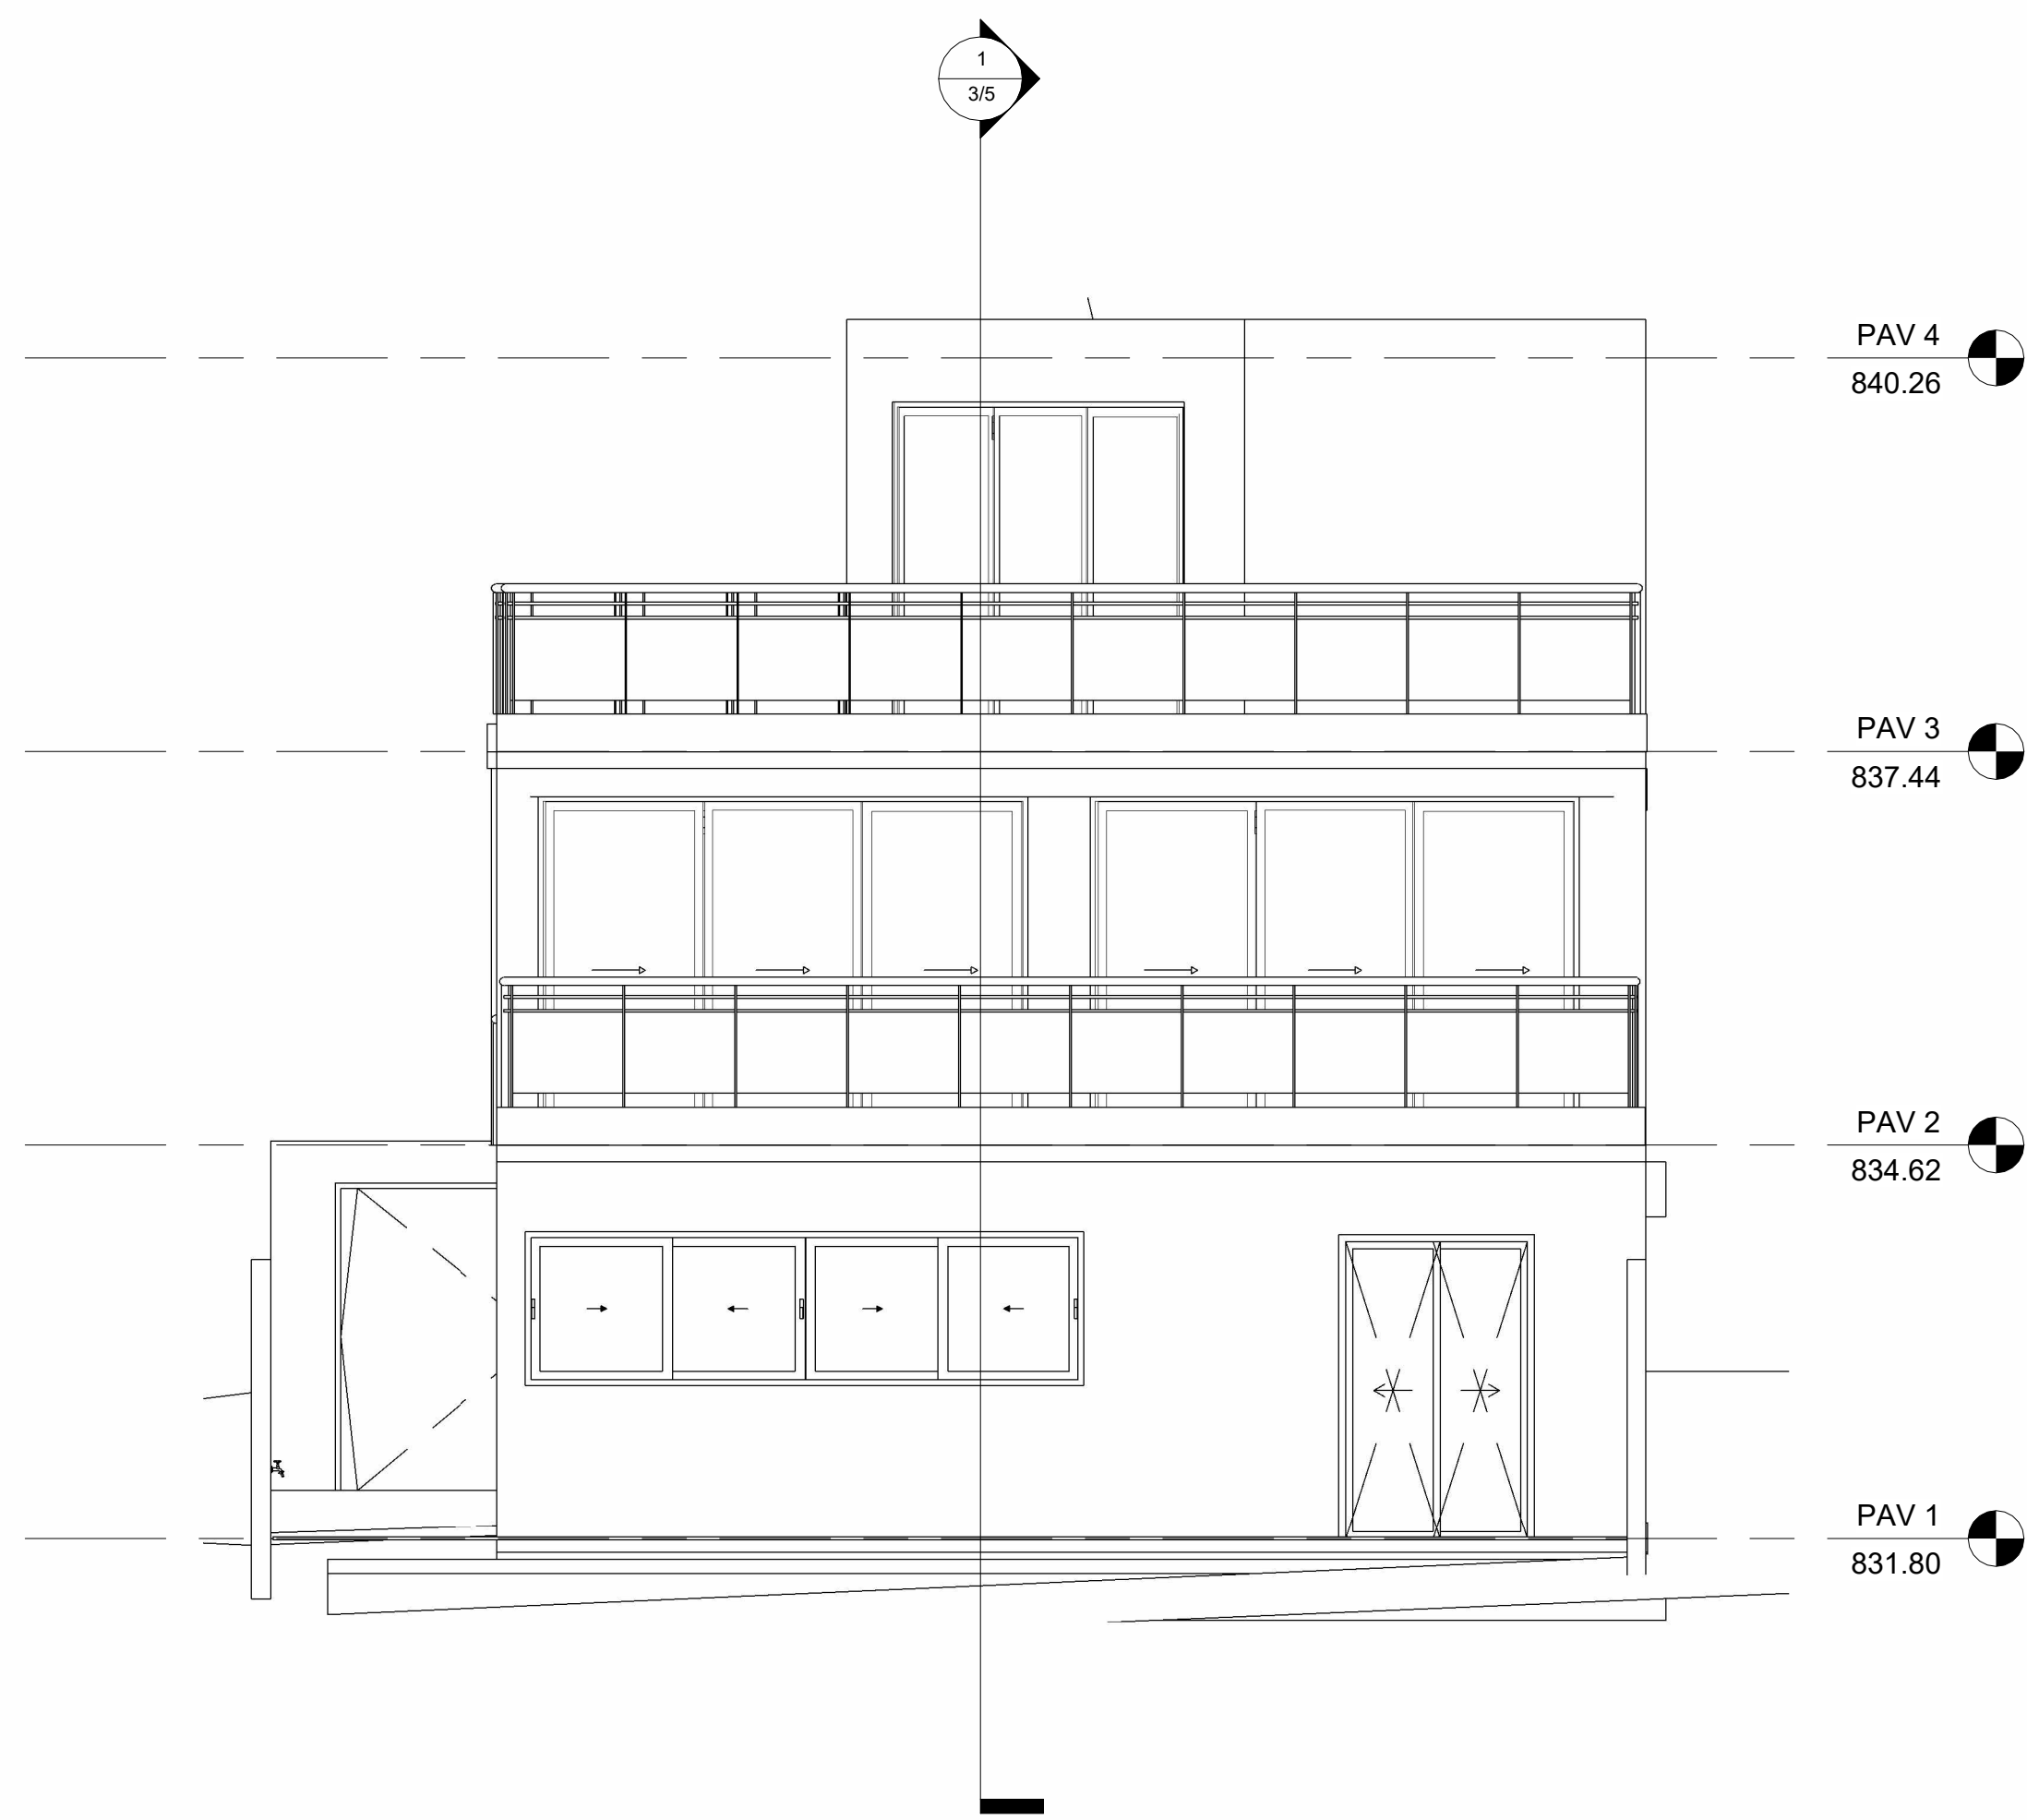


3 Oeste
1 : 50

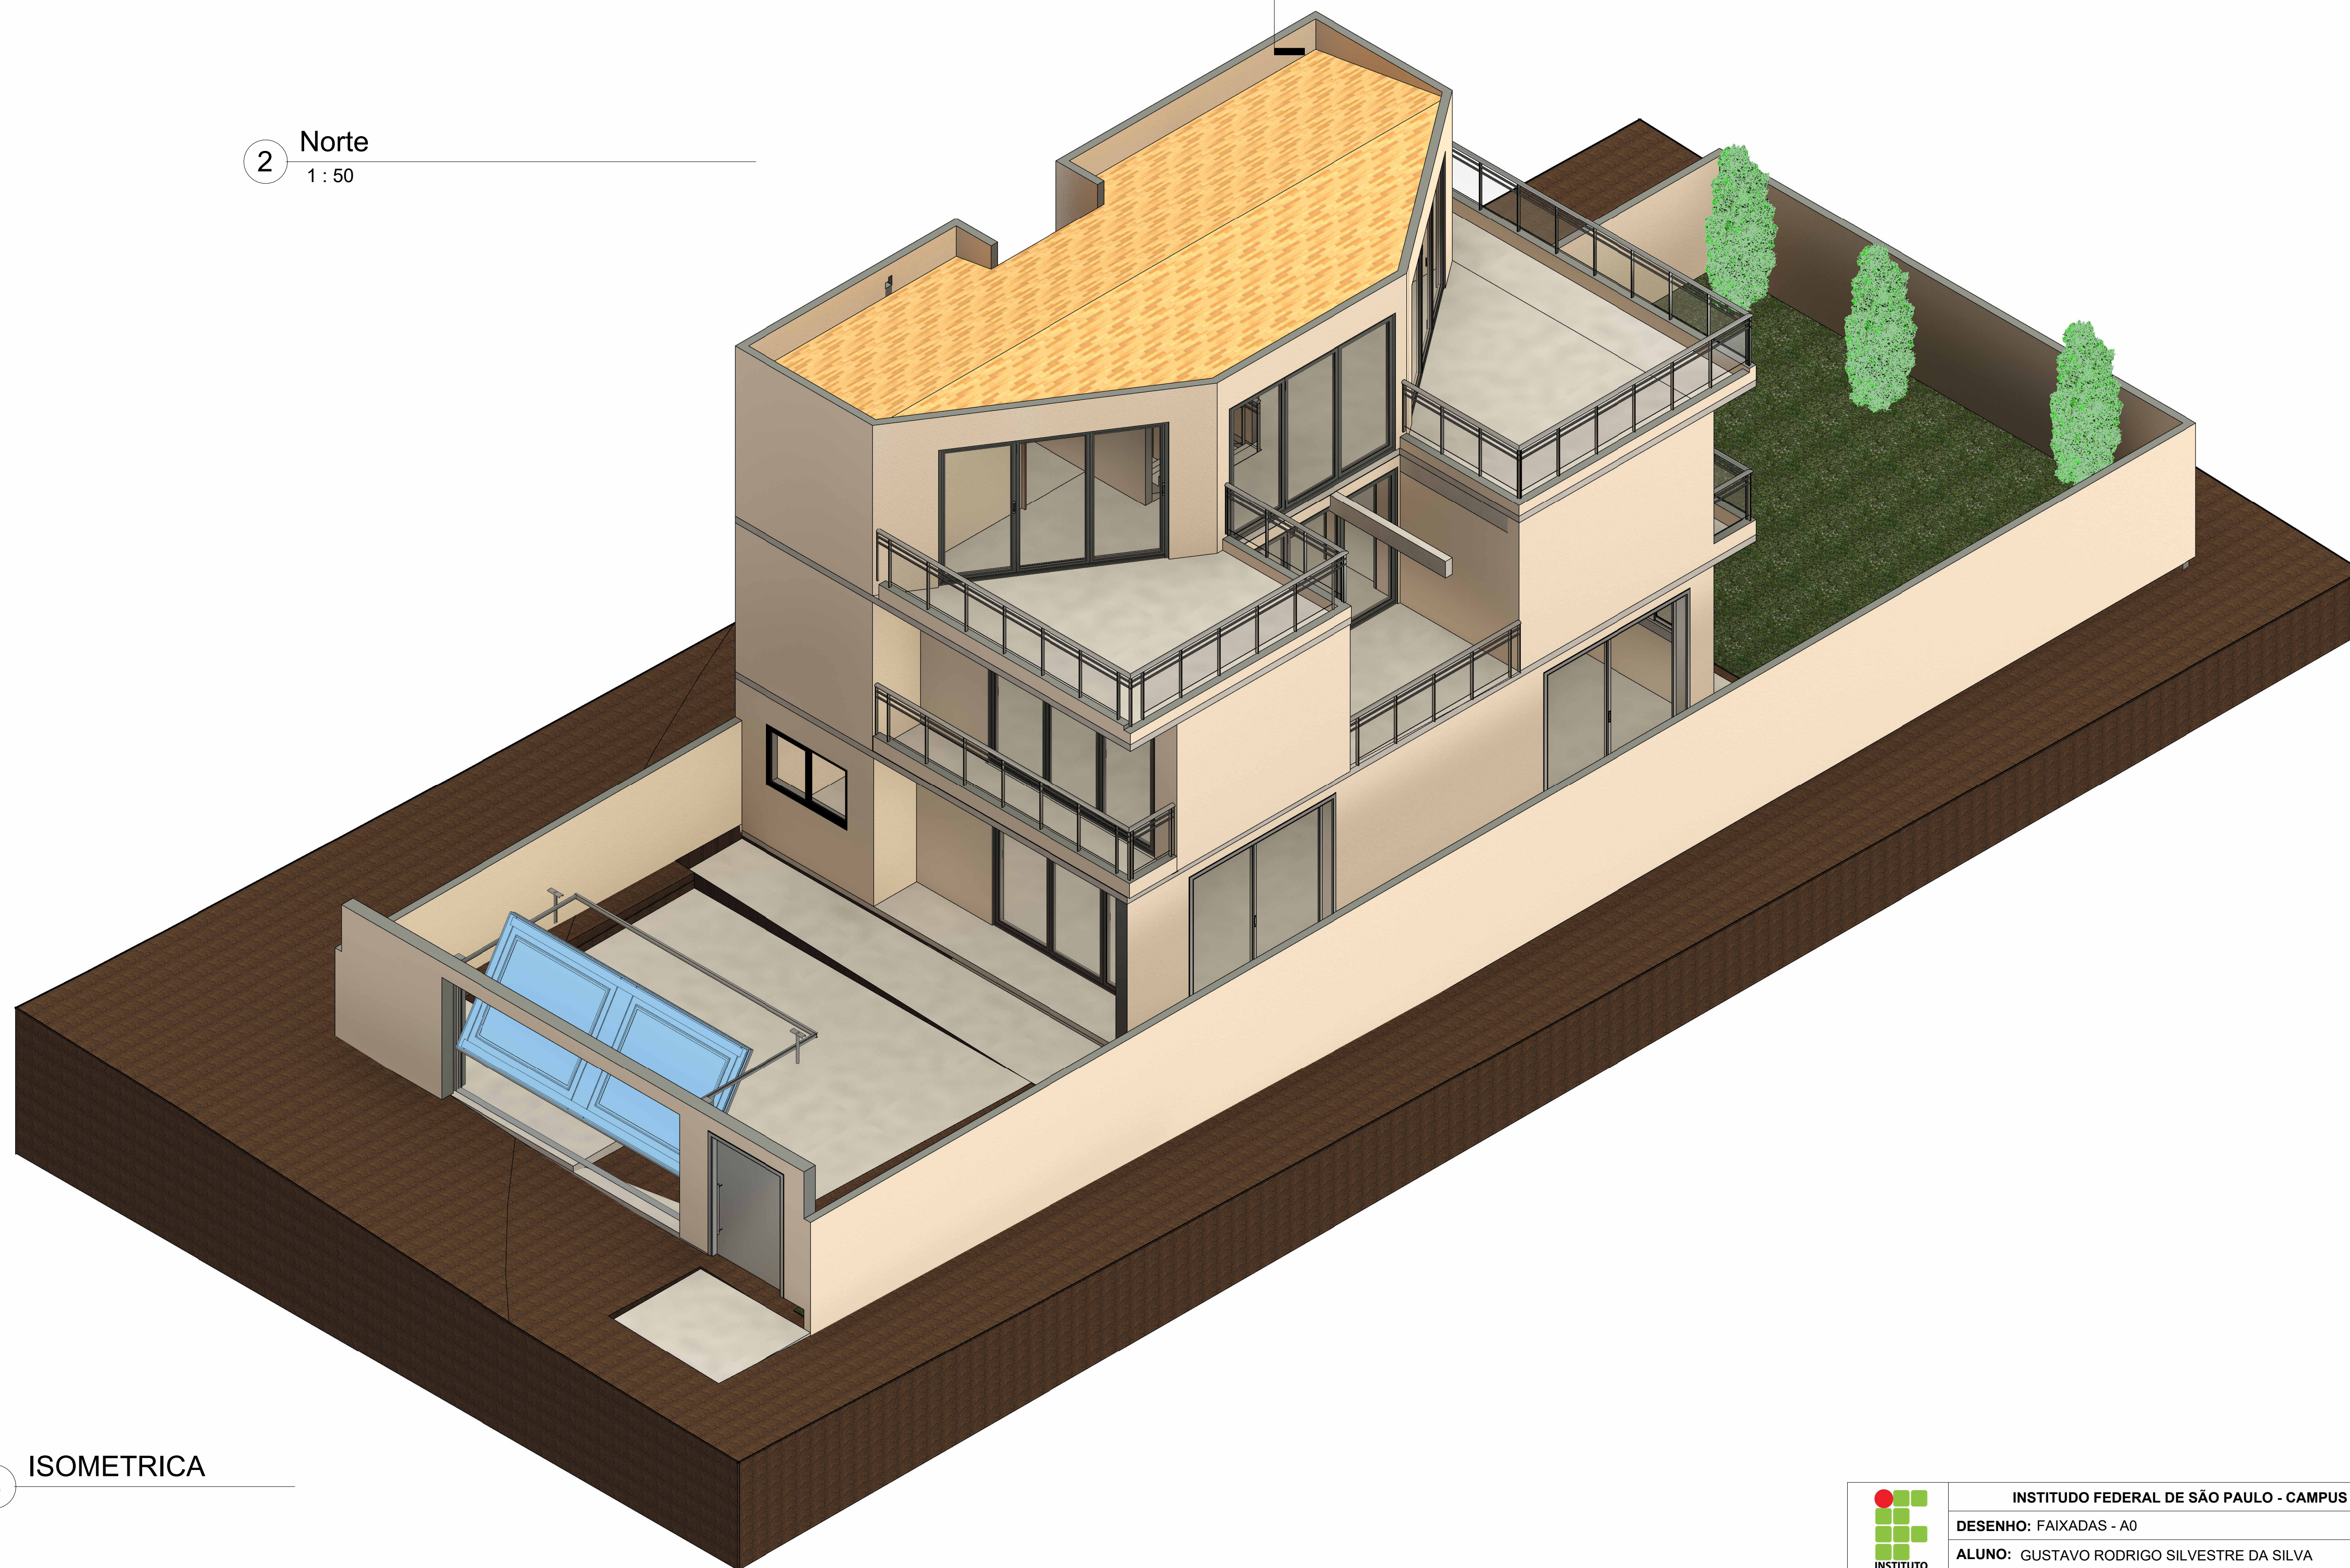


4 ISOMETRICA

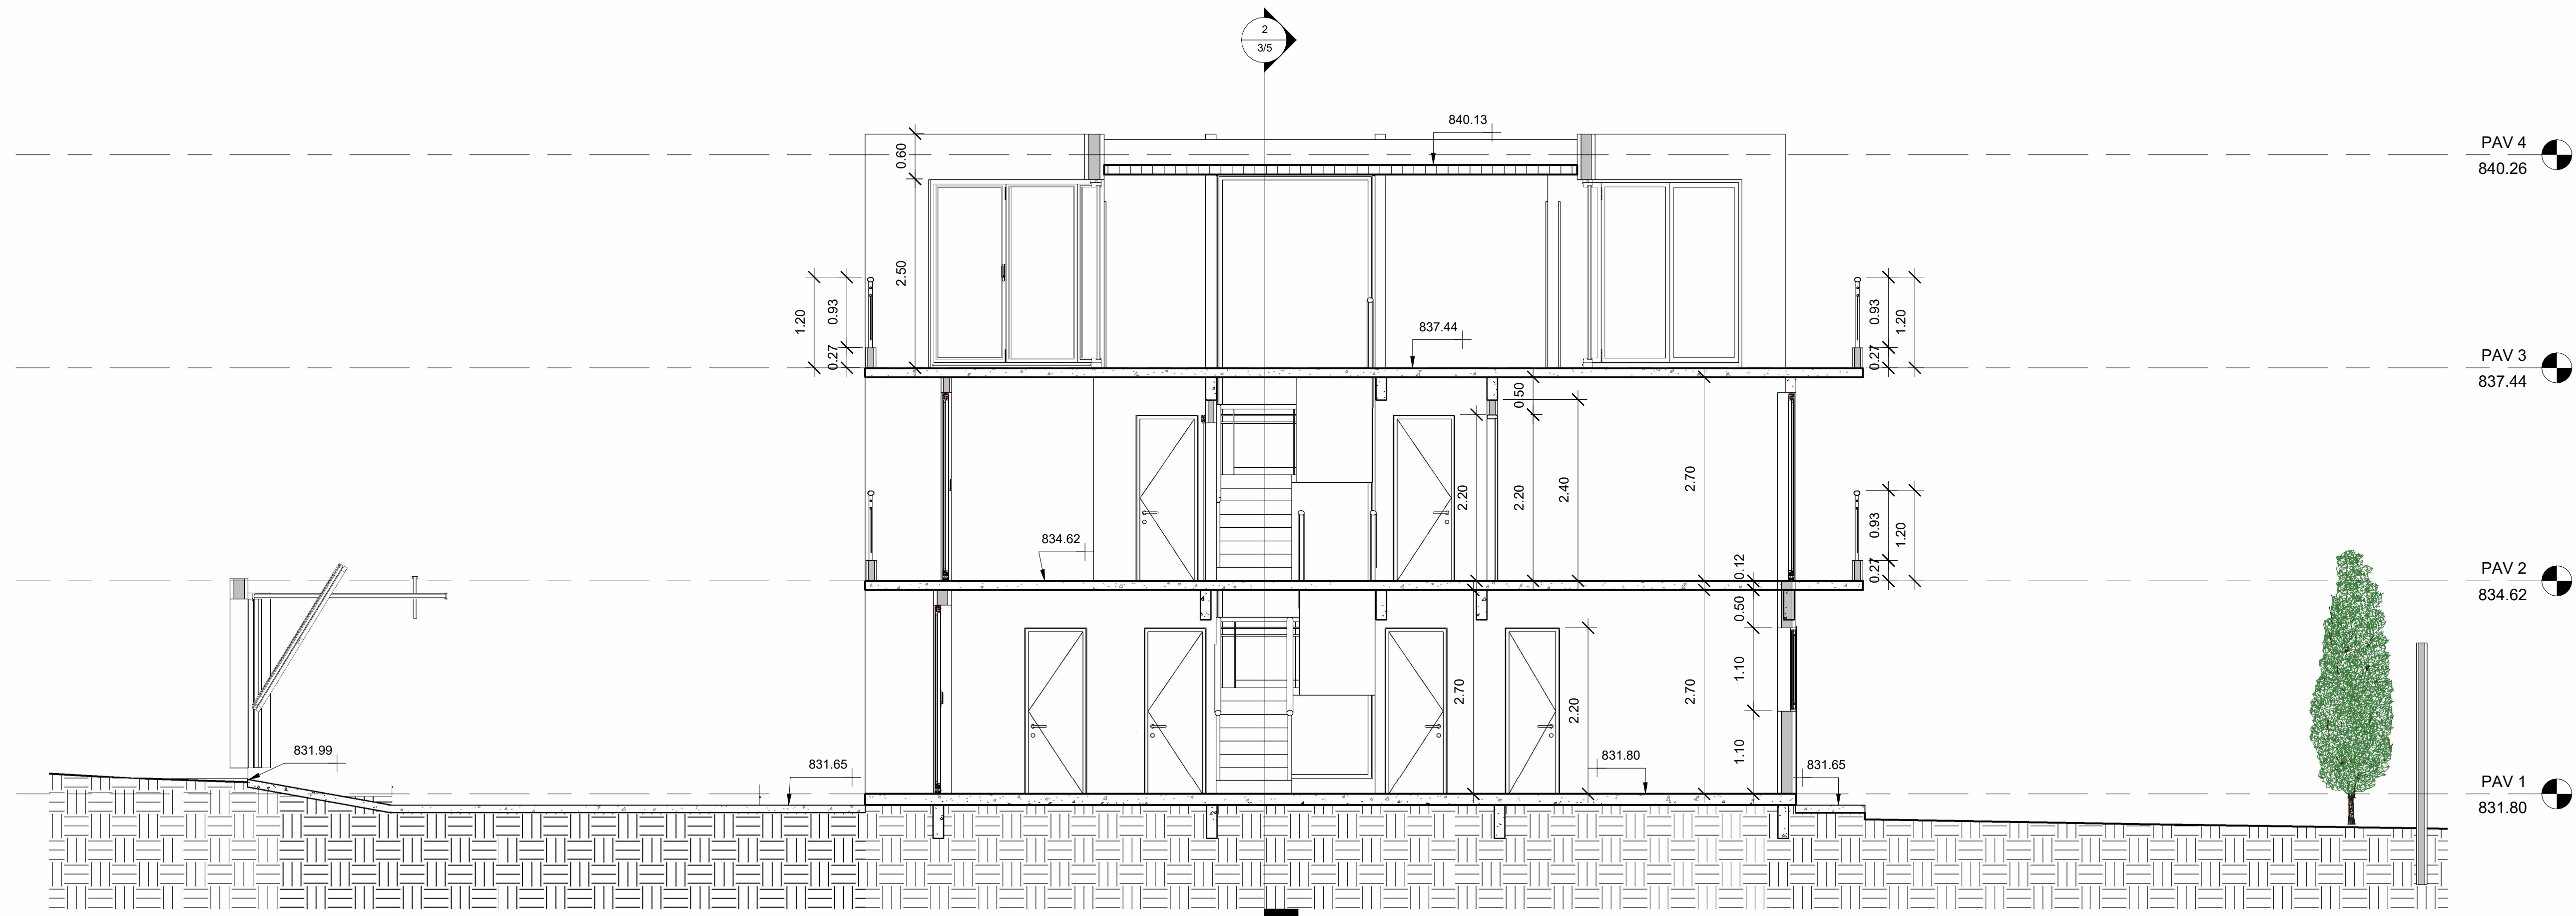


1 CORTE LONGITUDINAL
1 : 50

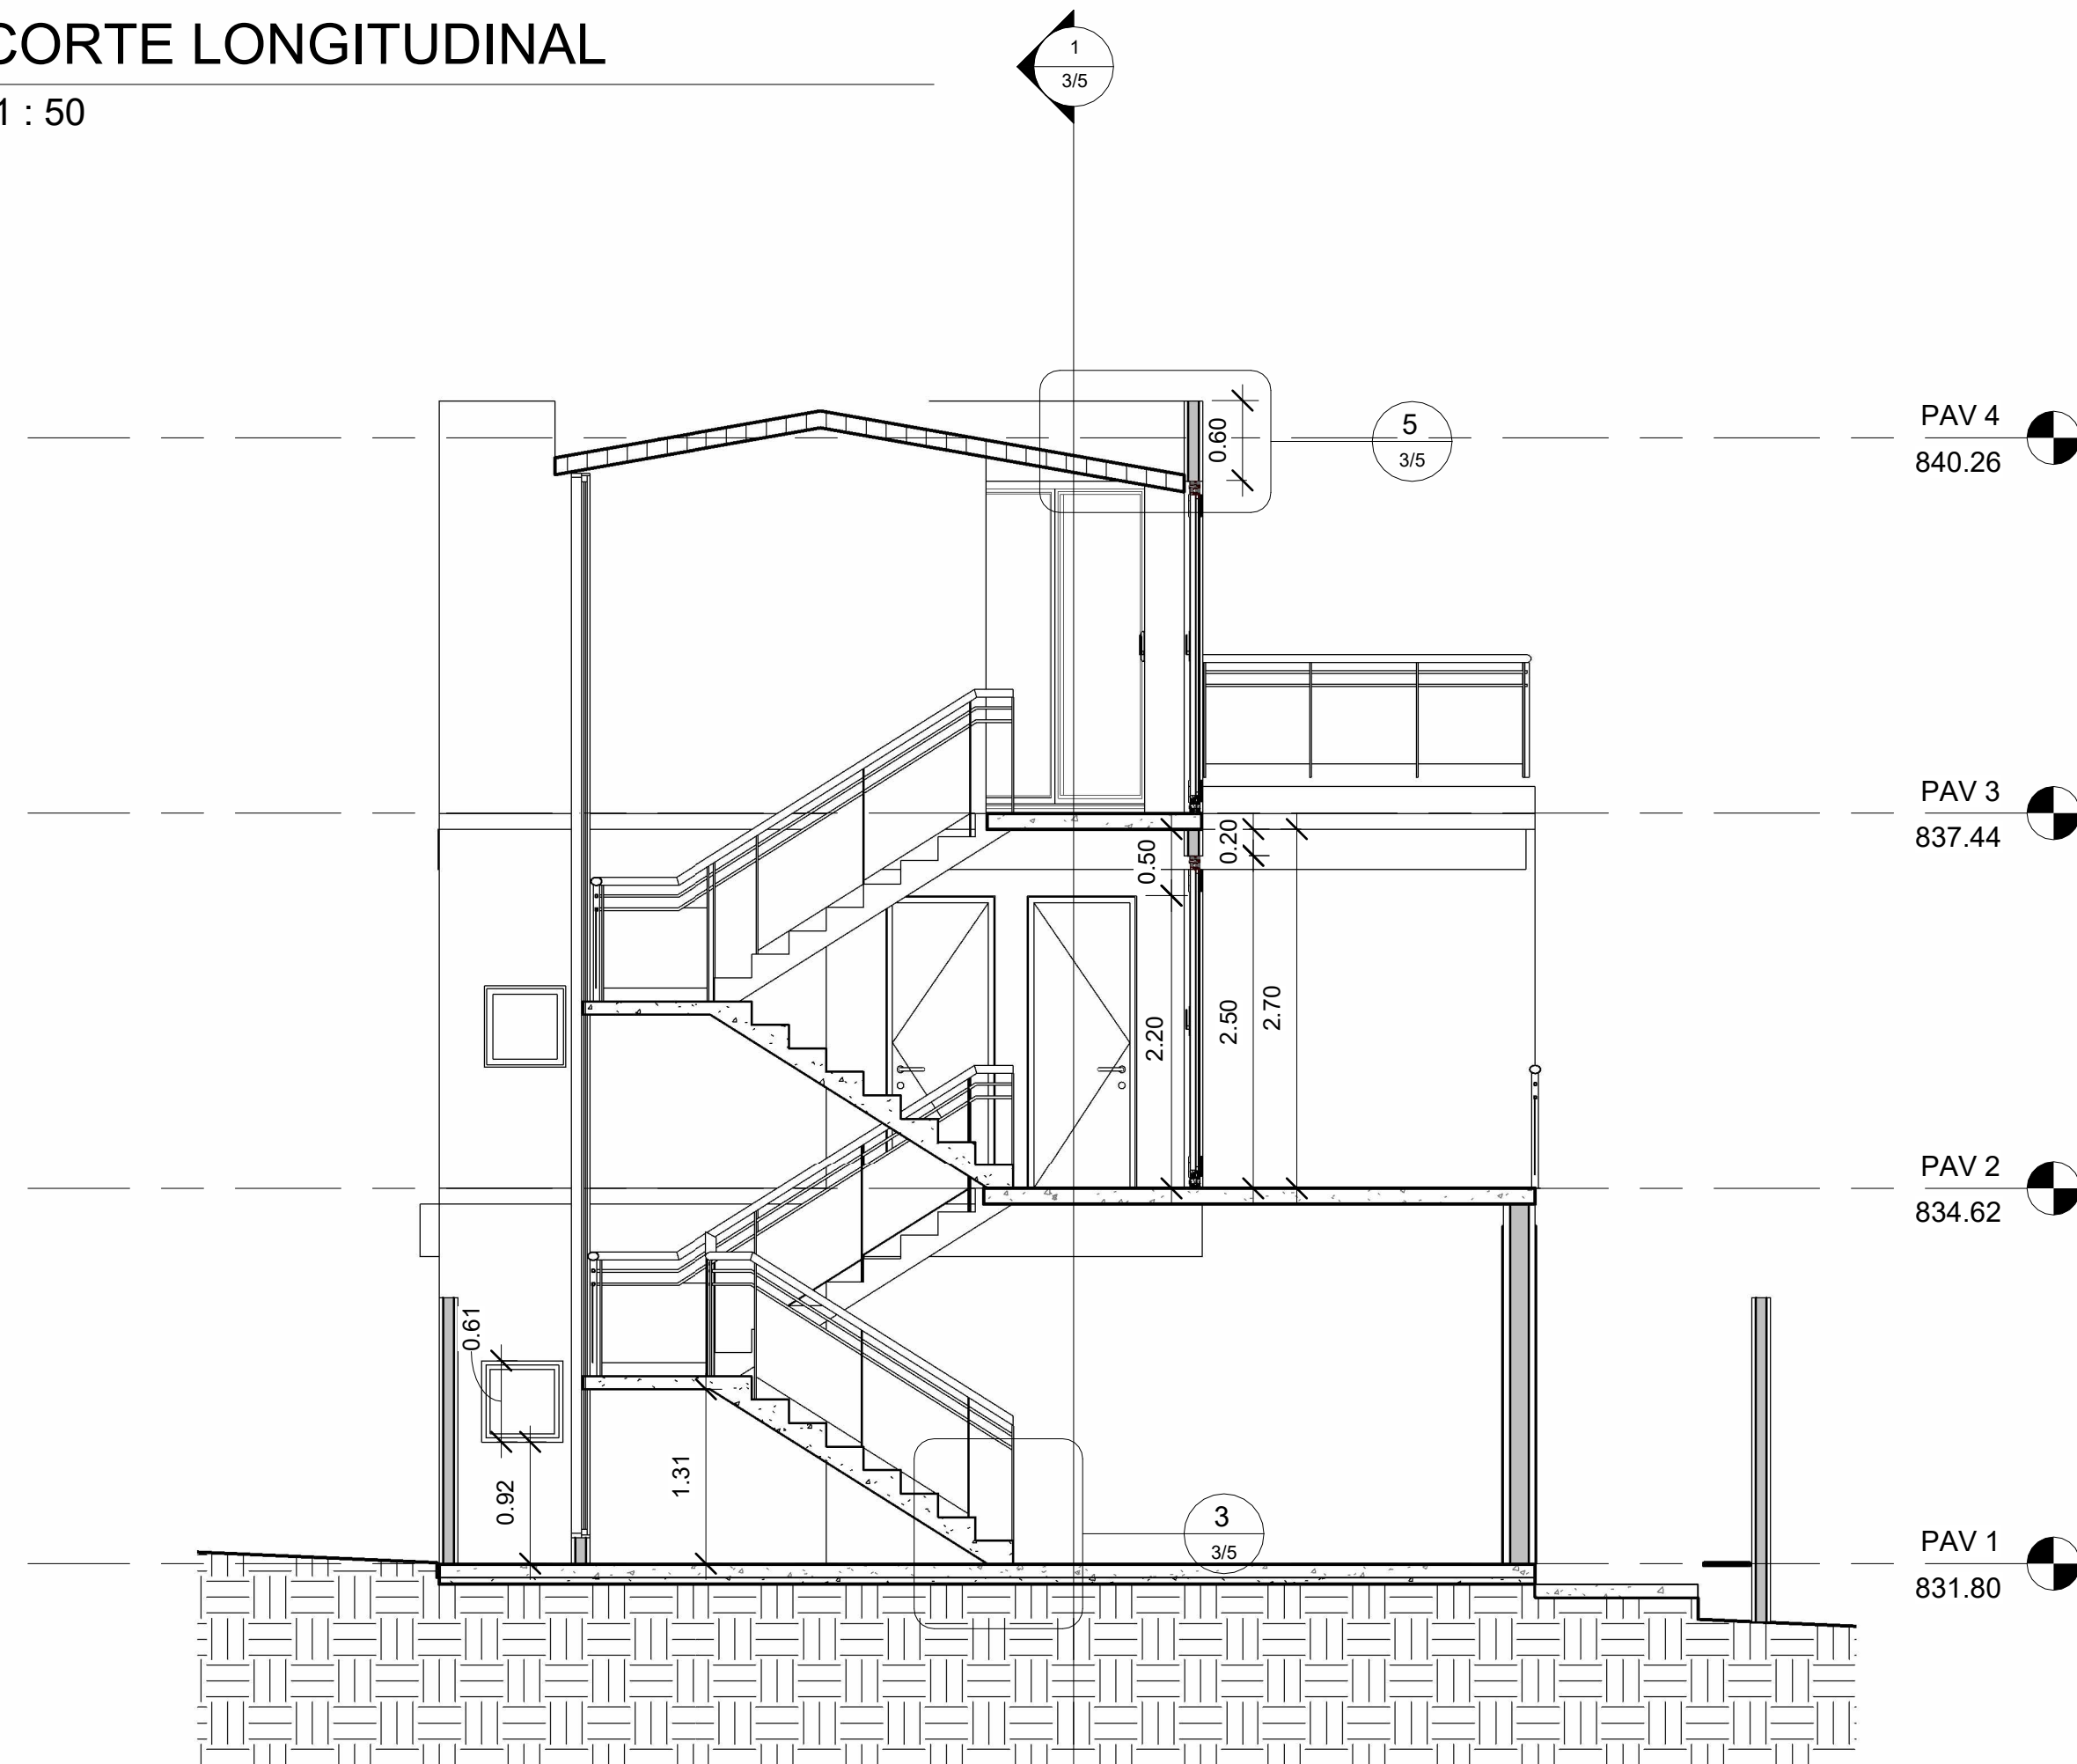


2 CORTE TRANSVERSAL
1 : 50

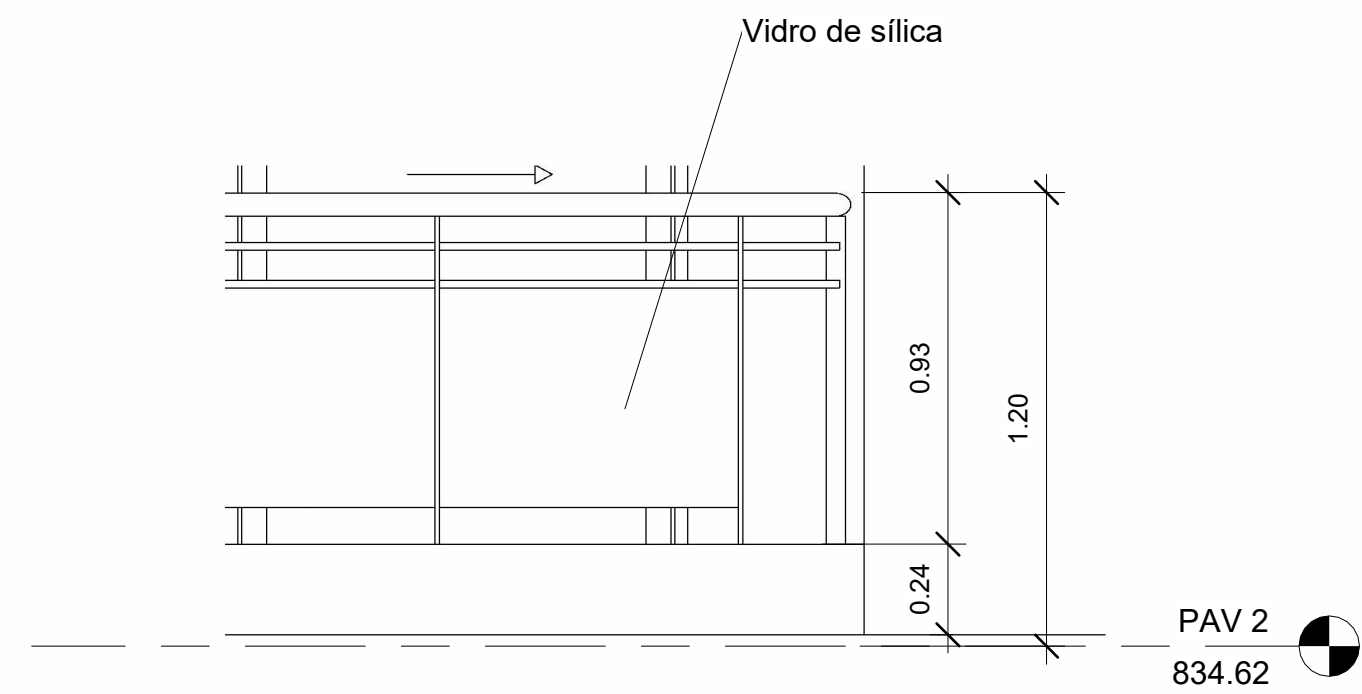


4 DETALHE - GUARDA
CORPO
1 : 20

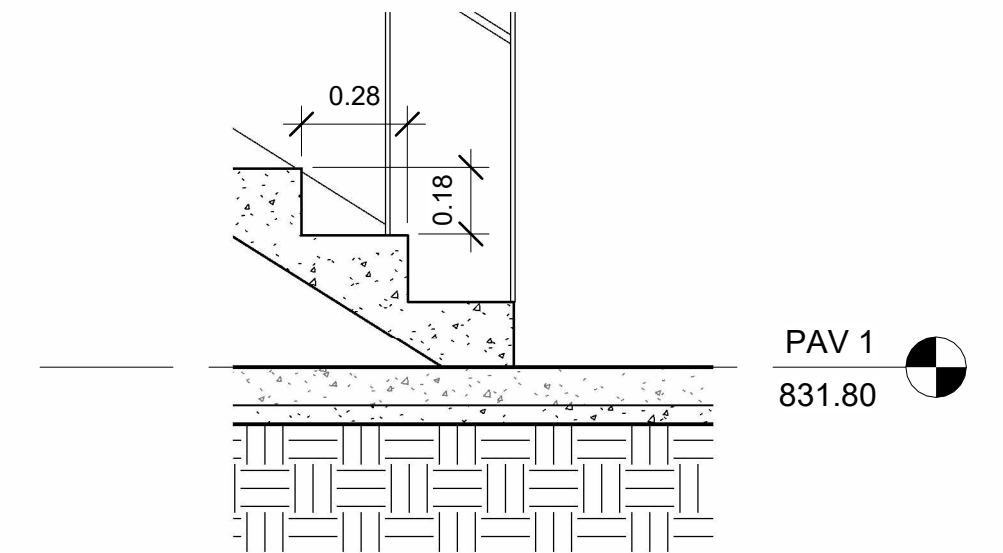


3 DETALHE - ESCADA
1 : 20

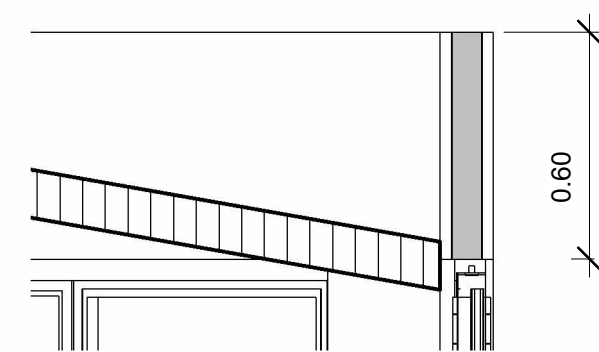


5 DETALHE - COBERTURA
1 : 20

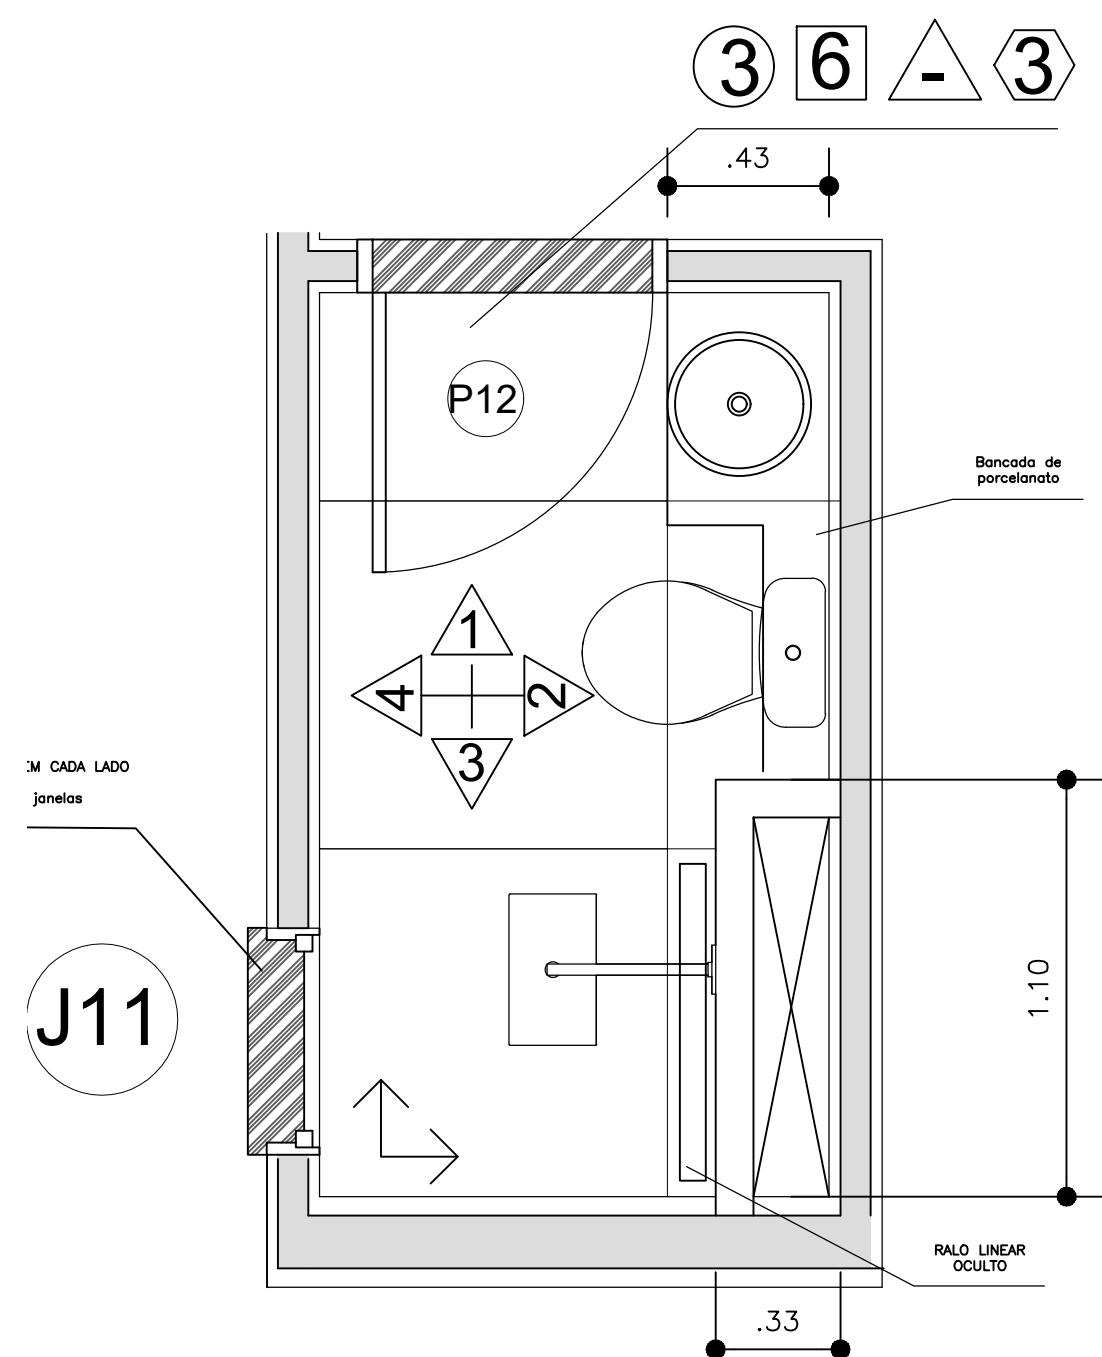


1 BANHEIRO DA SUÍTE
ESCALA: 1:20

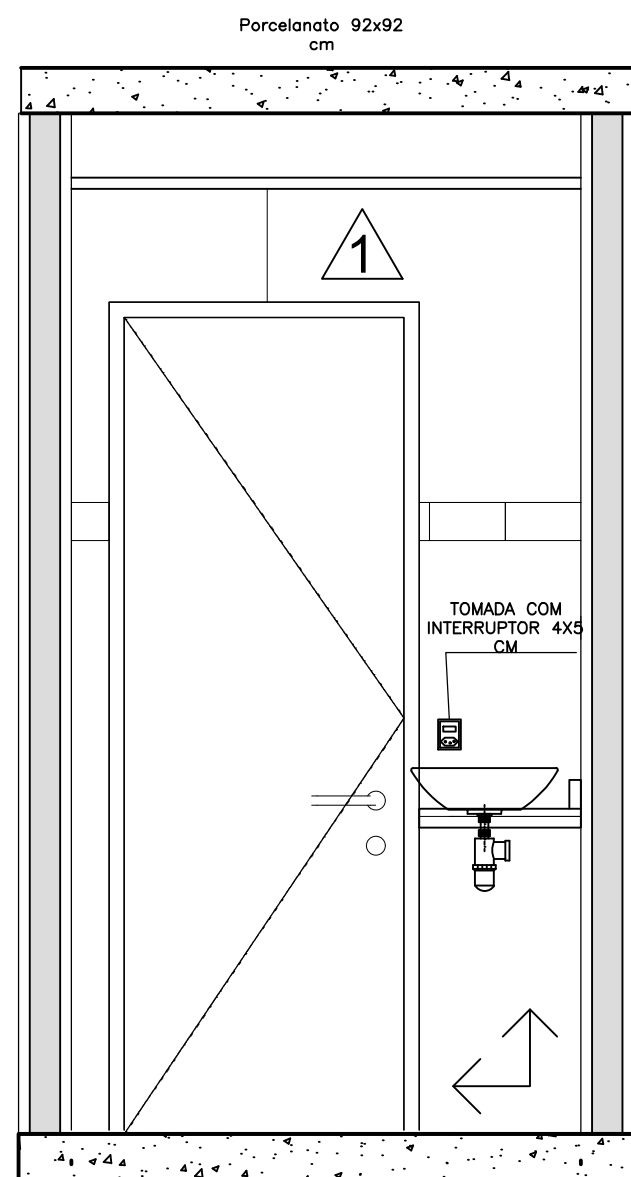


2 ELEVACÃO 1
ESCALA: 1:20

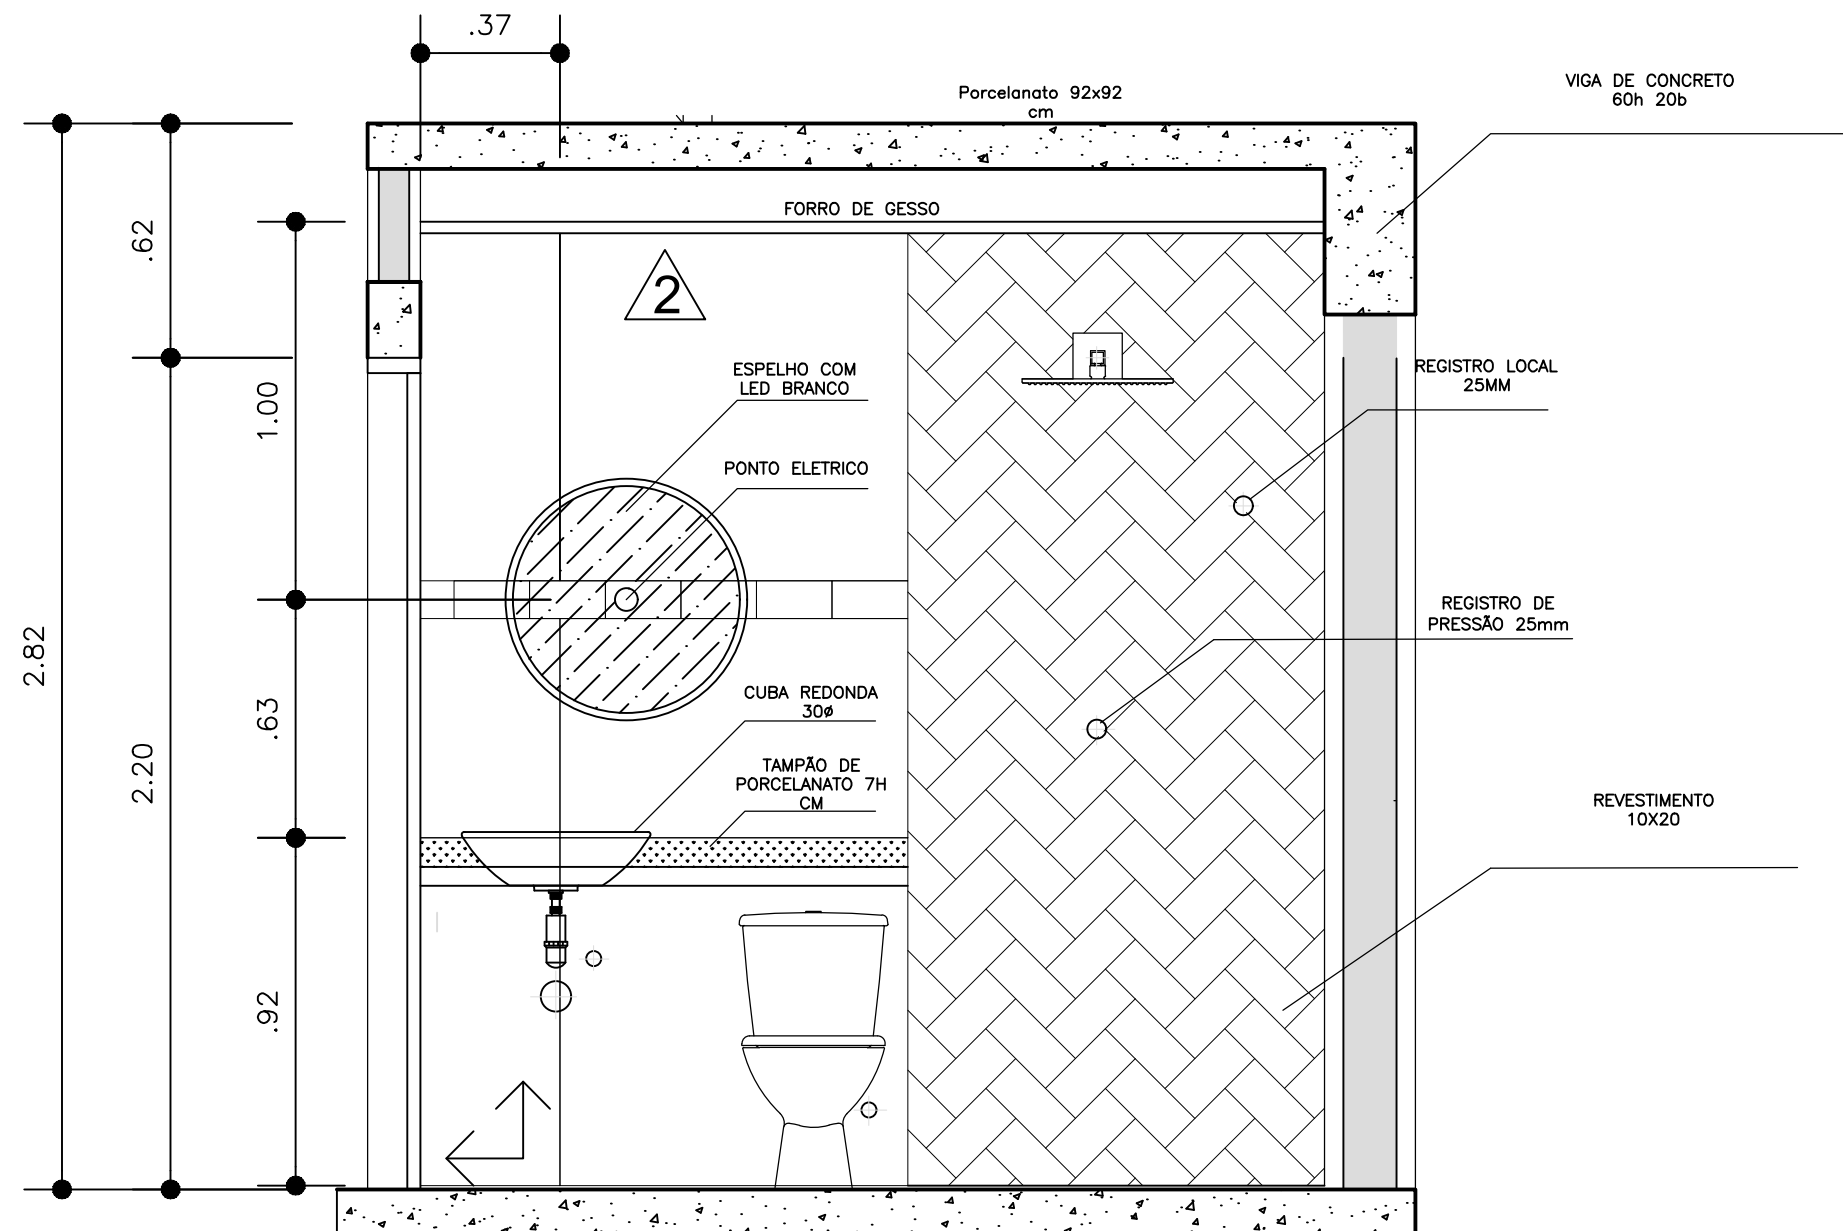


3 ELEVACÃO 2
ESCALA: 1:20

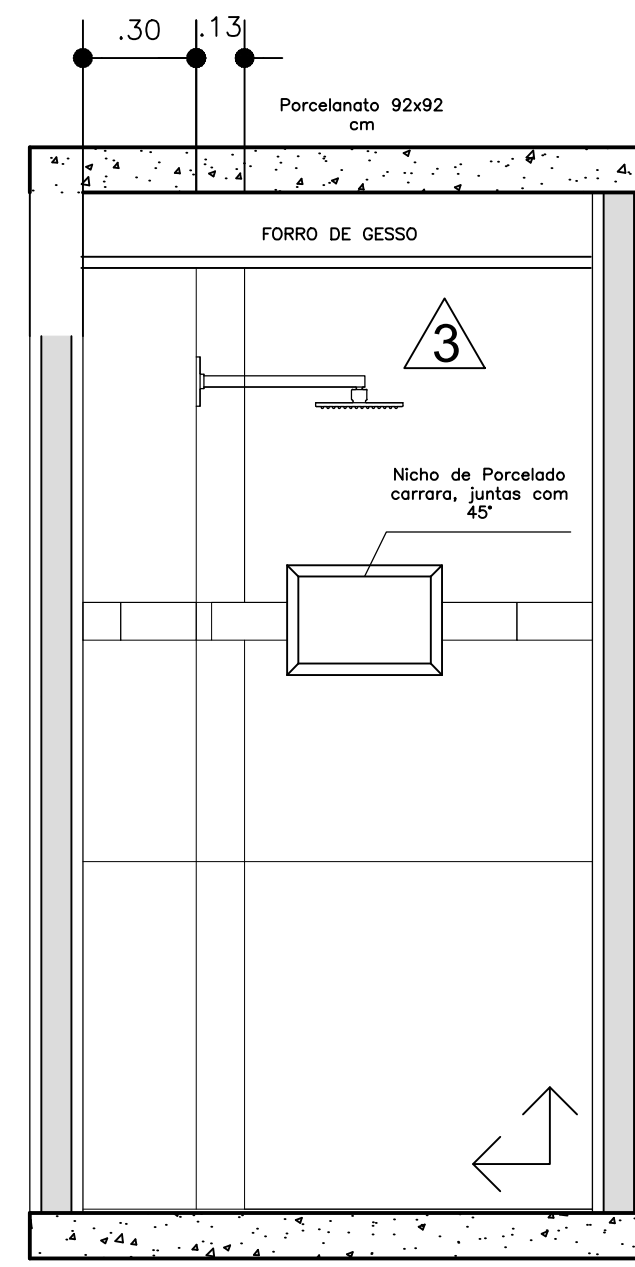


4 ELEVACÃO 3
ESCALA: 1:20

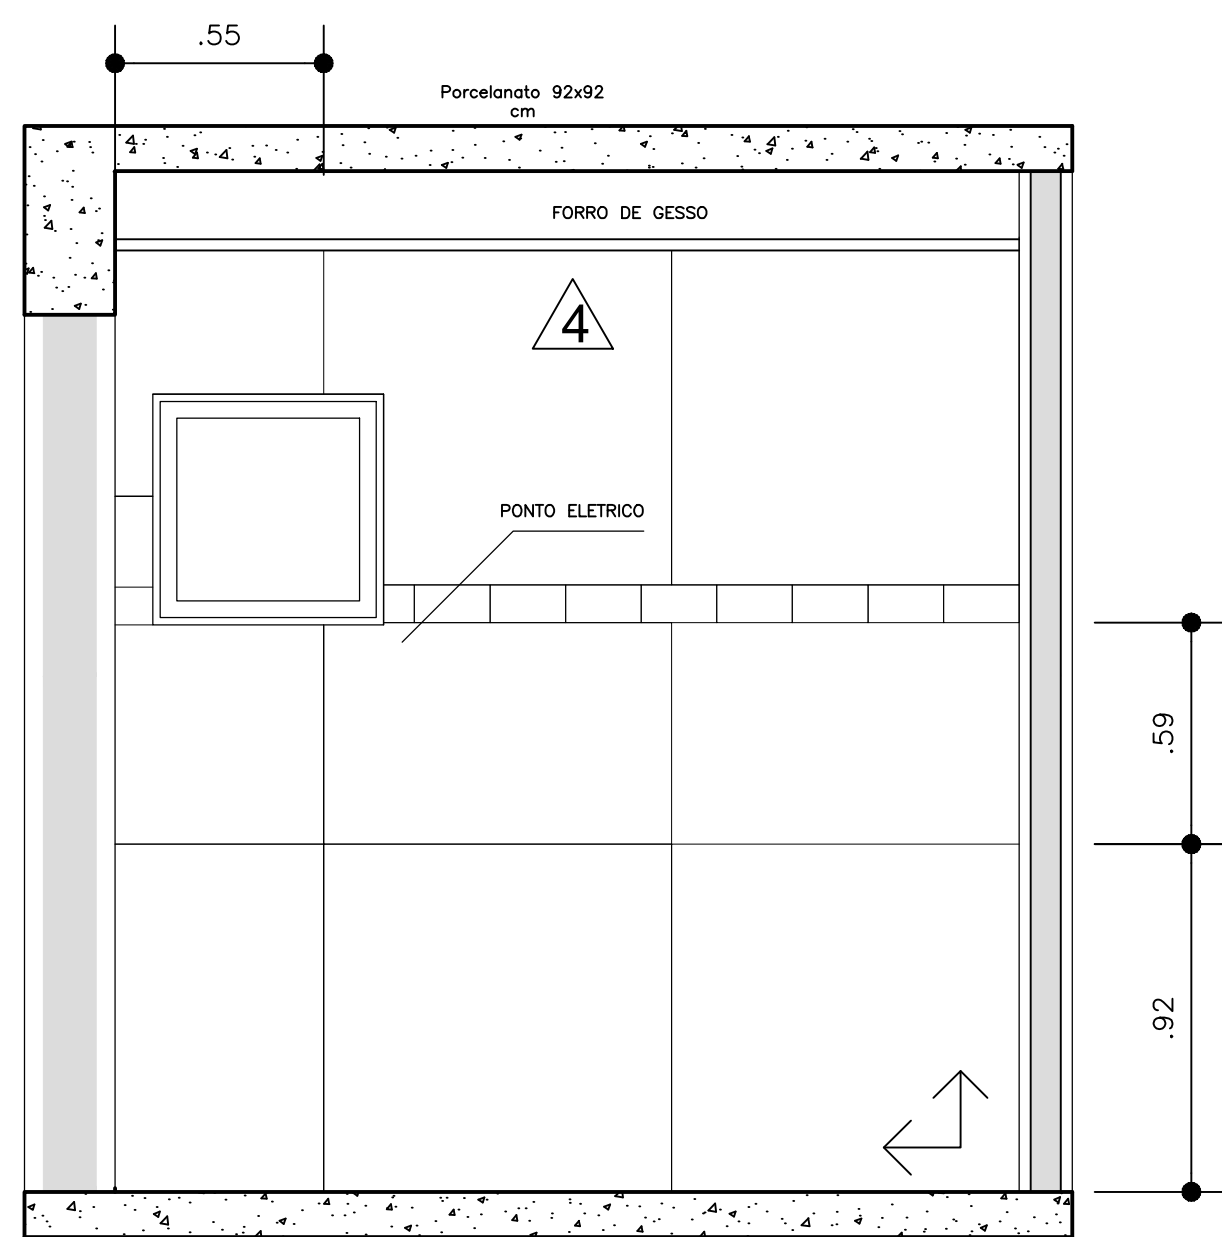

1 ELEVACÃO 4
ESCALA: 1:50

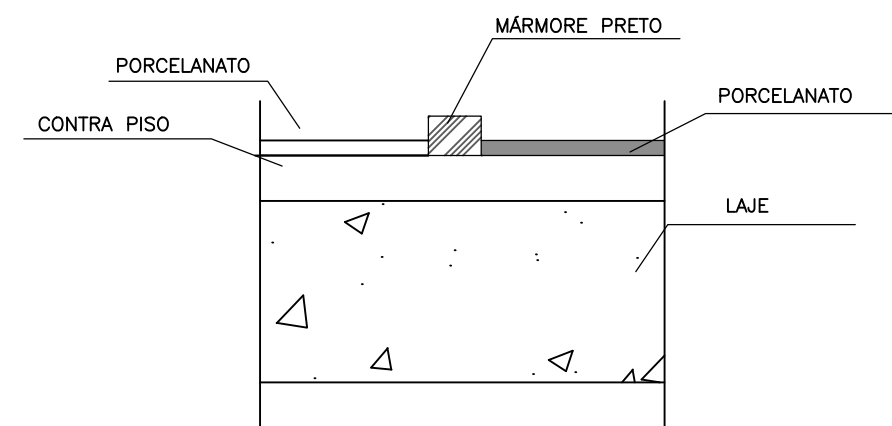

2 ELEVACÃO 1
ESCALA: 1:20

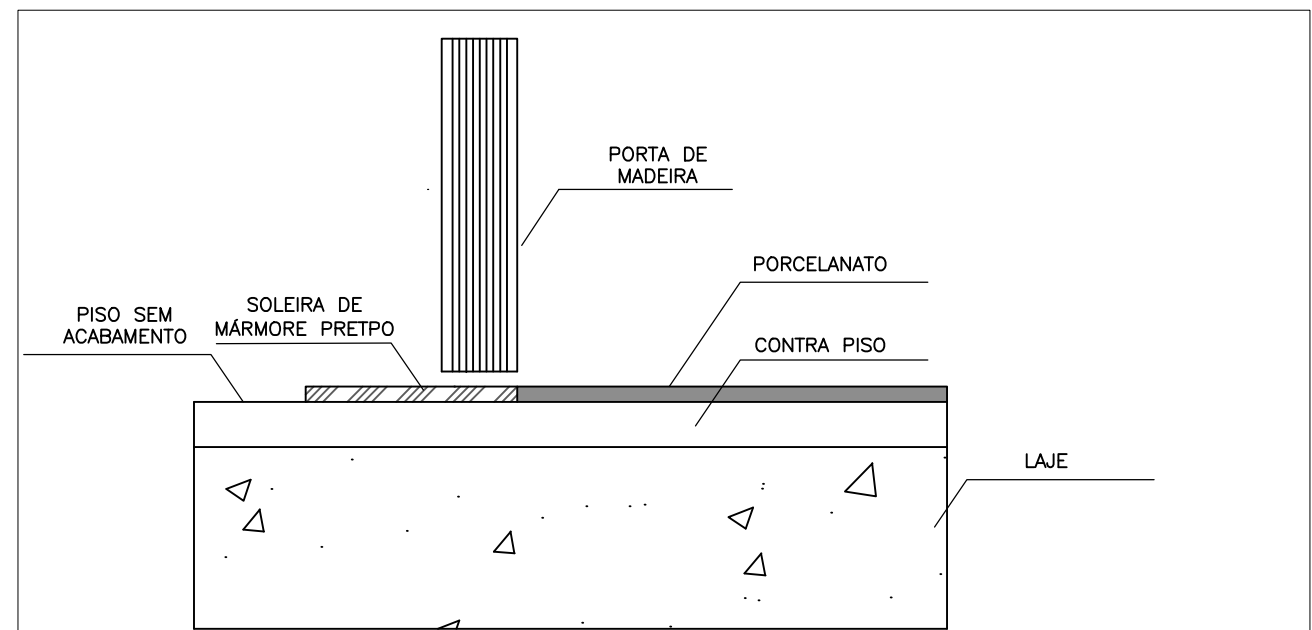

2 ELEVACÃO 1
ESCALA: 1:20

Tabelas de Metais e louças

Tipo	Marca	Material	Largura bruta	Altura bruta	Quantidade
Culpa	Deca	vidro	0.3	0.30	1
Torneira	Torneira	Aço	0,25	0.20	1
Ralo	Pingo Casa	Inox	0,10	1	1
Registro de Pressao	Registro de Pressao	Aço	0,025Ø	0	1
Registro de Gaveta	Registro de Gaveta	Aço	0.025Ø	0	1
Bacia Sanitaria	Deca	Axis	0.68	0.78	1


Tabelas de Esquadrias - Portas

Marca de tipo	Material	Largura bruta	Altura bruta	Quantidade
P03	Madeira	0.72	2.2	4

Tabela de janela



Comentário s de tipos	Marca de tipo	Largura bruta	Altura bruta	Altura do peitoril	Material	Vidro	Modelo
Banh. Superior	J11	0.80	0.60	1.50	Alumínio	Vidro, fosco	MAXIM-AR



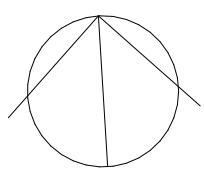


RUA
01

RUA
01

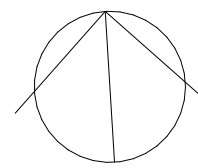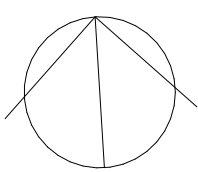


RUA
01

RUA
01

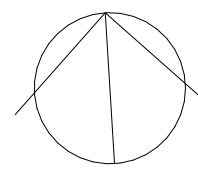

RUA
03

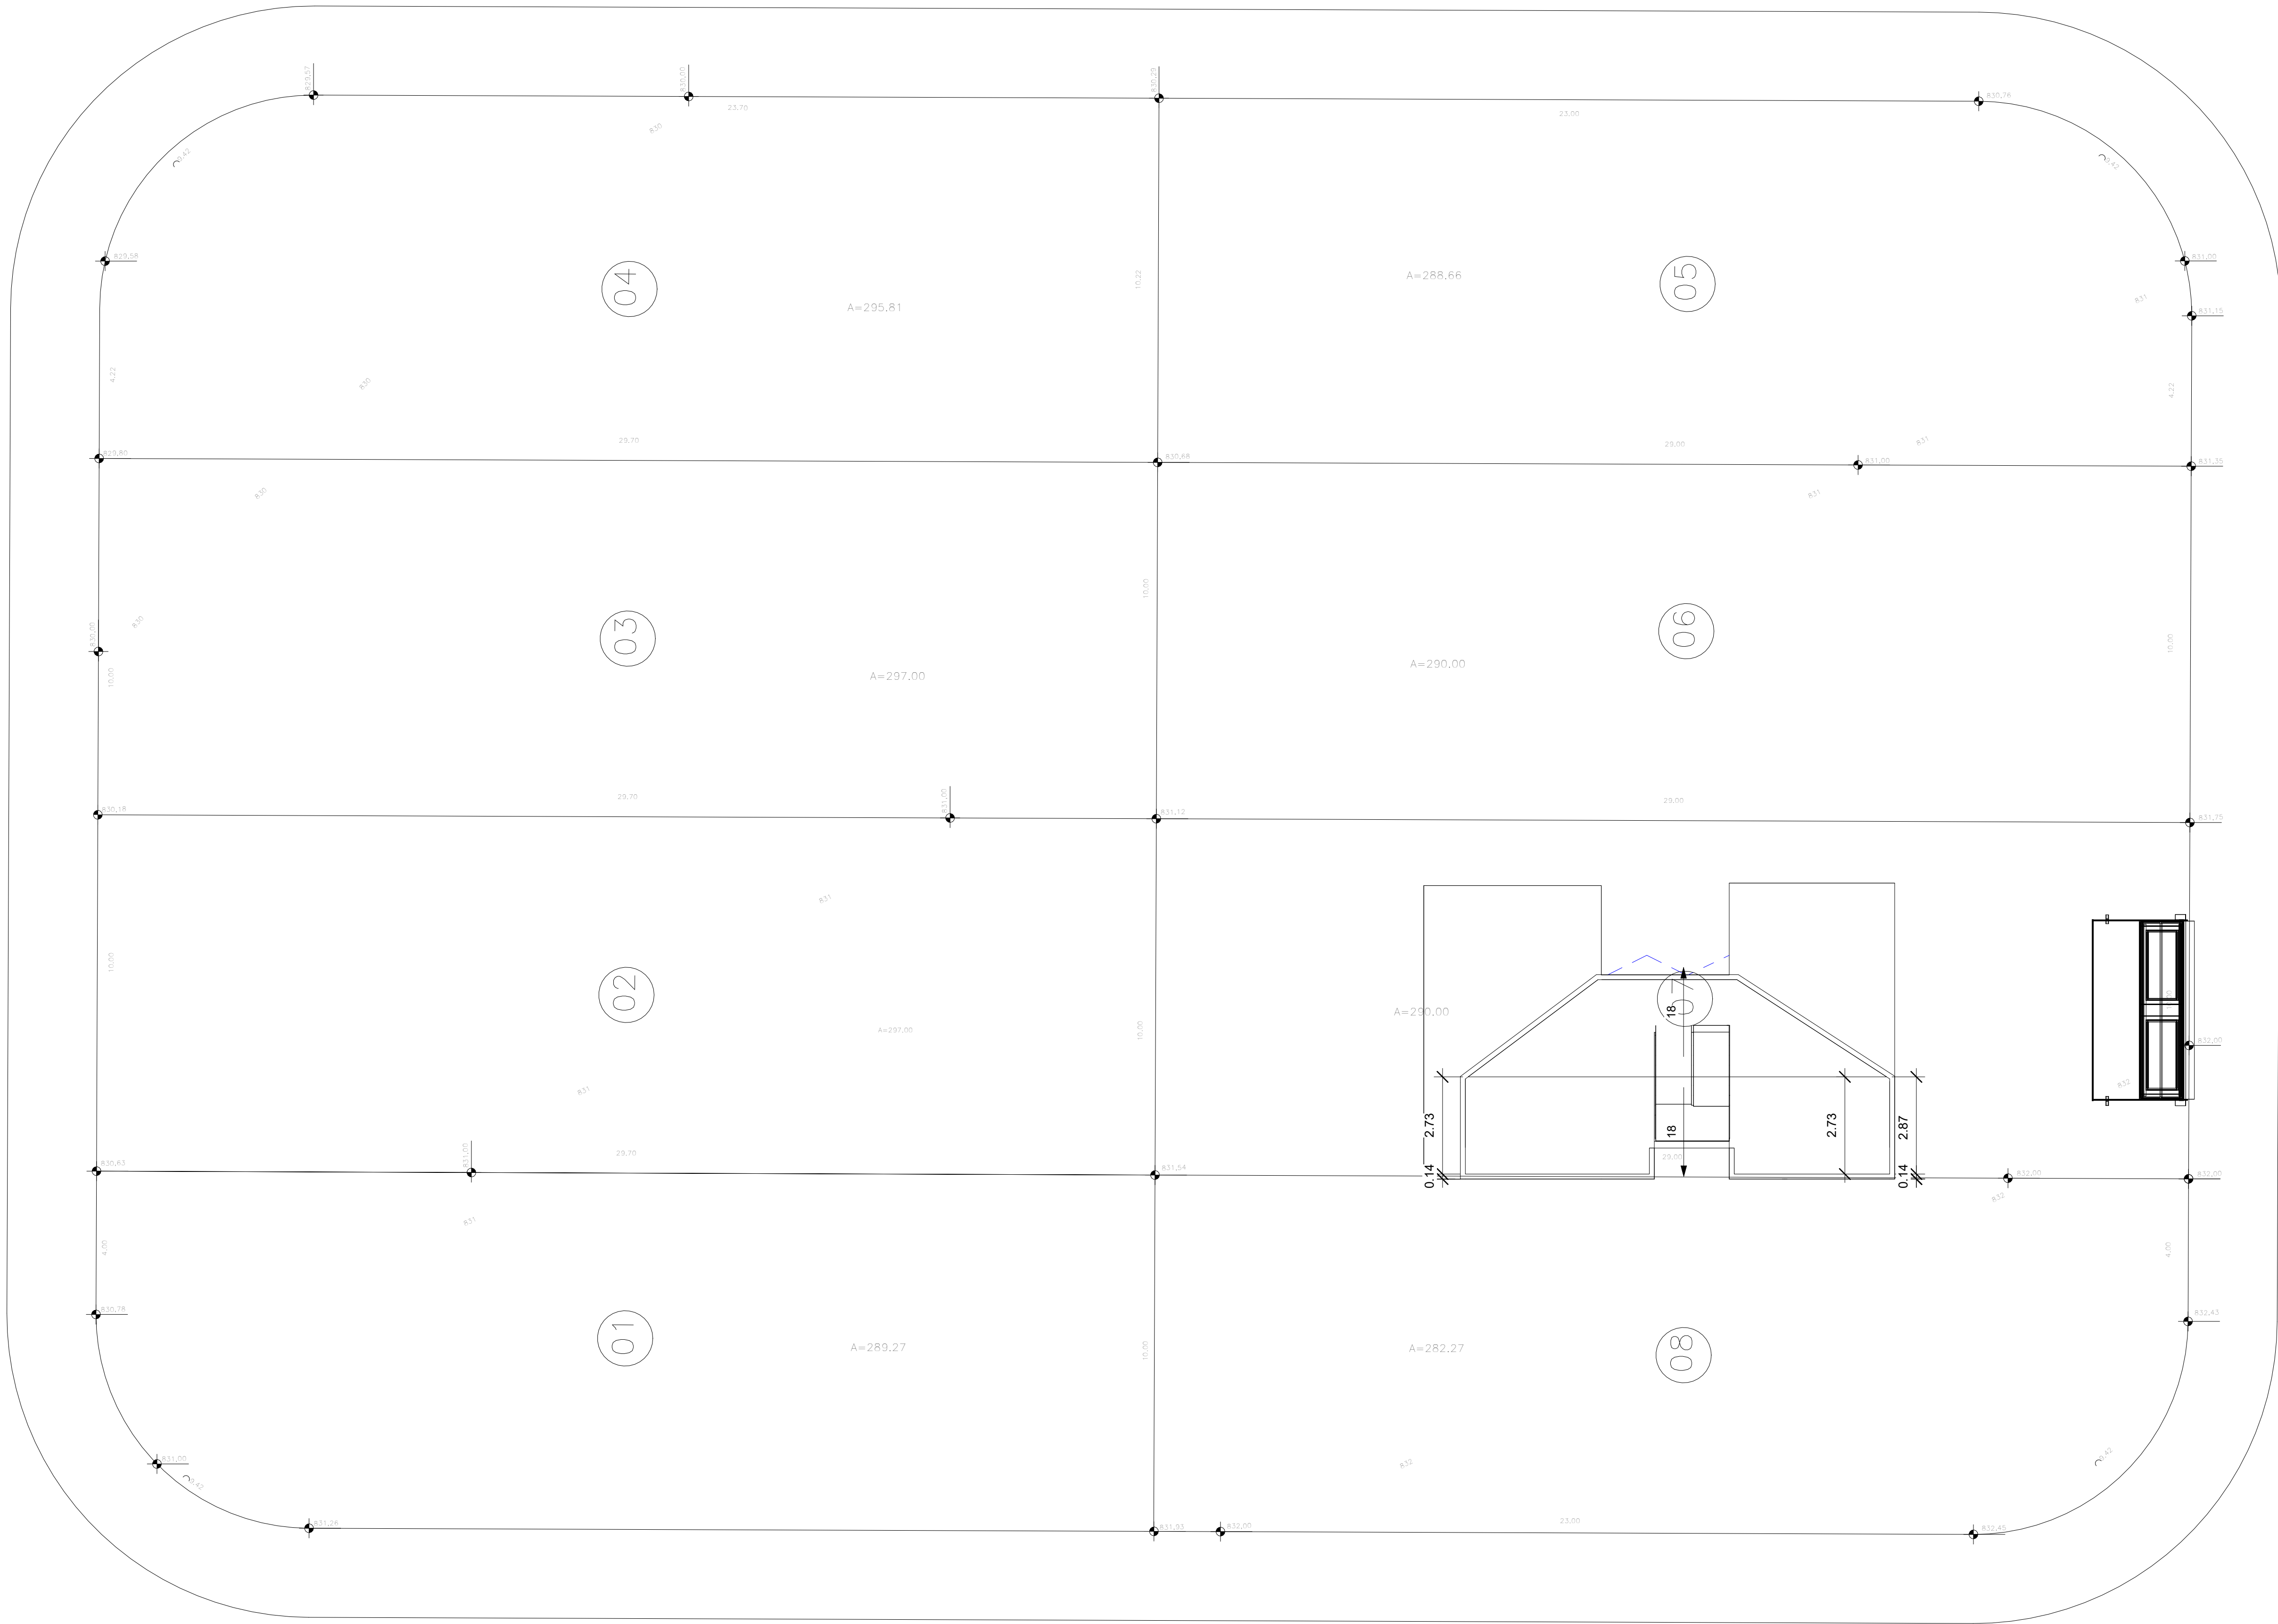

1






PAV 4 Copiar 1
1 : 100

RUA
5

RUA
5



INSTITUTO FEDERAL DE SÃO PAULO - CAMPUS SP		
DESENHO: IMPLANTAÇÃO - QUADRA		
ALUONO: GUSTAVO RODRIGO SILVESTRE DA SILVA	PRANCHA 5/7	
DOCENTE: LÉTICIA - ELIANE	DISCIPLINA: PJIU4	

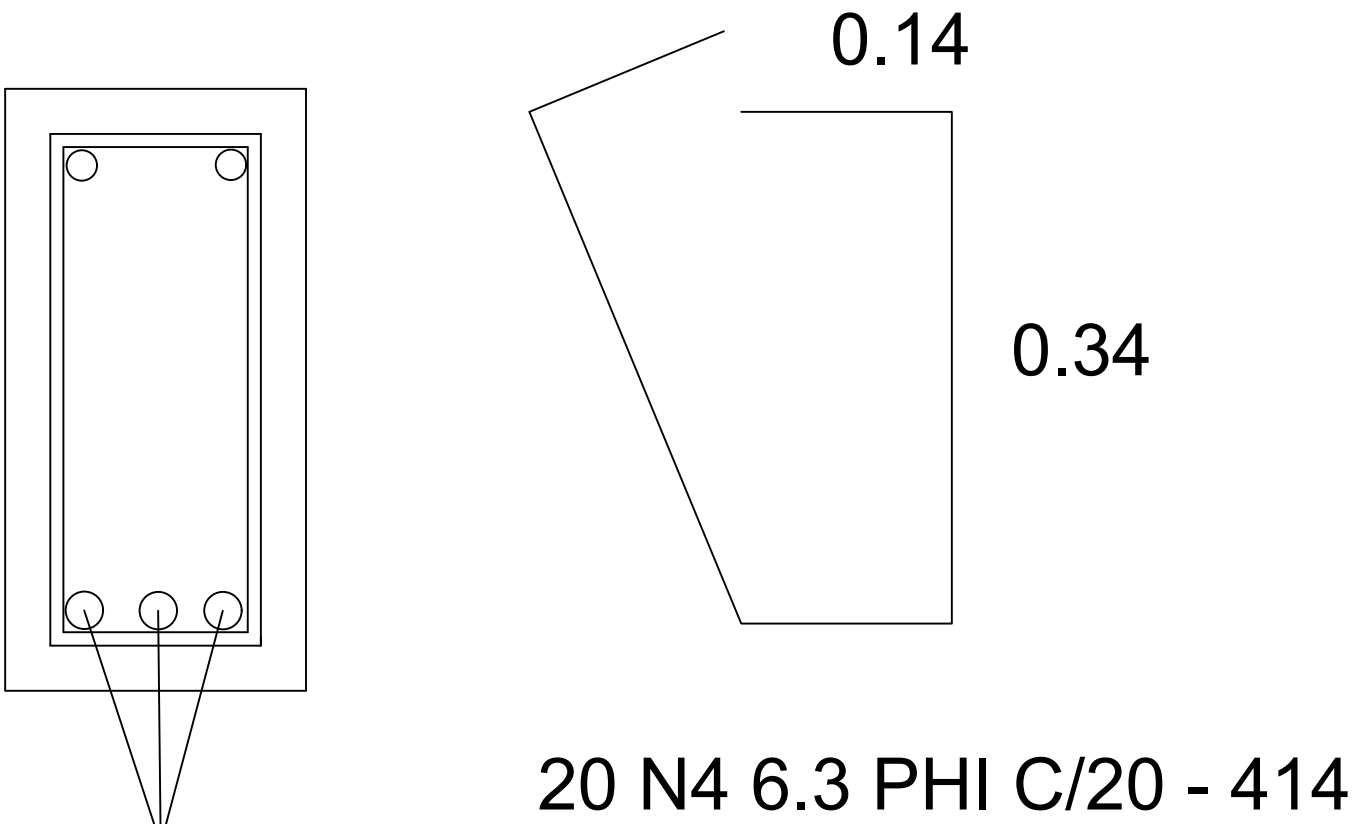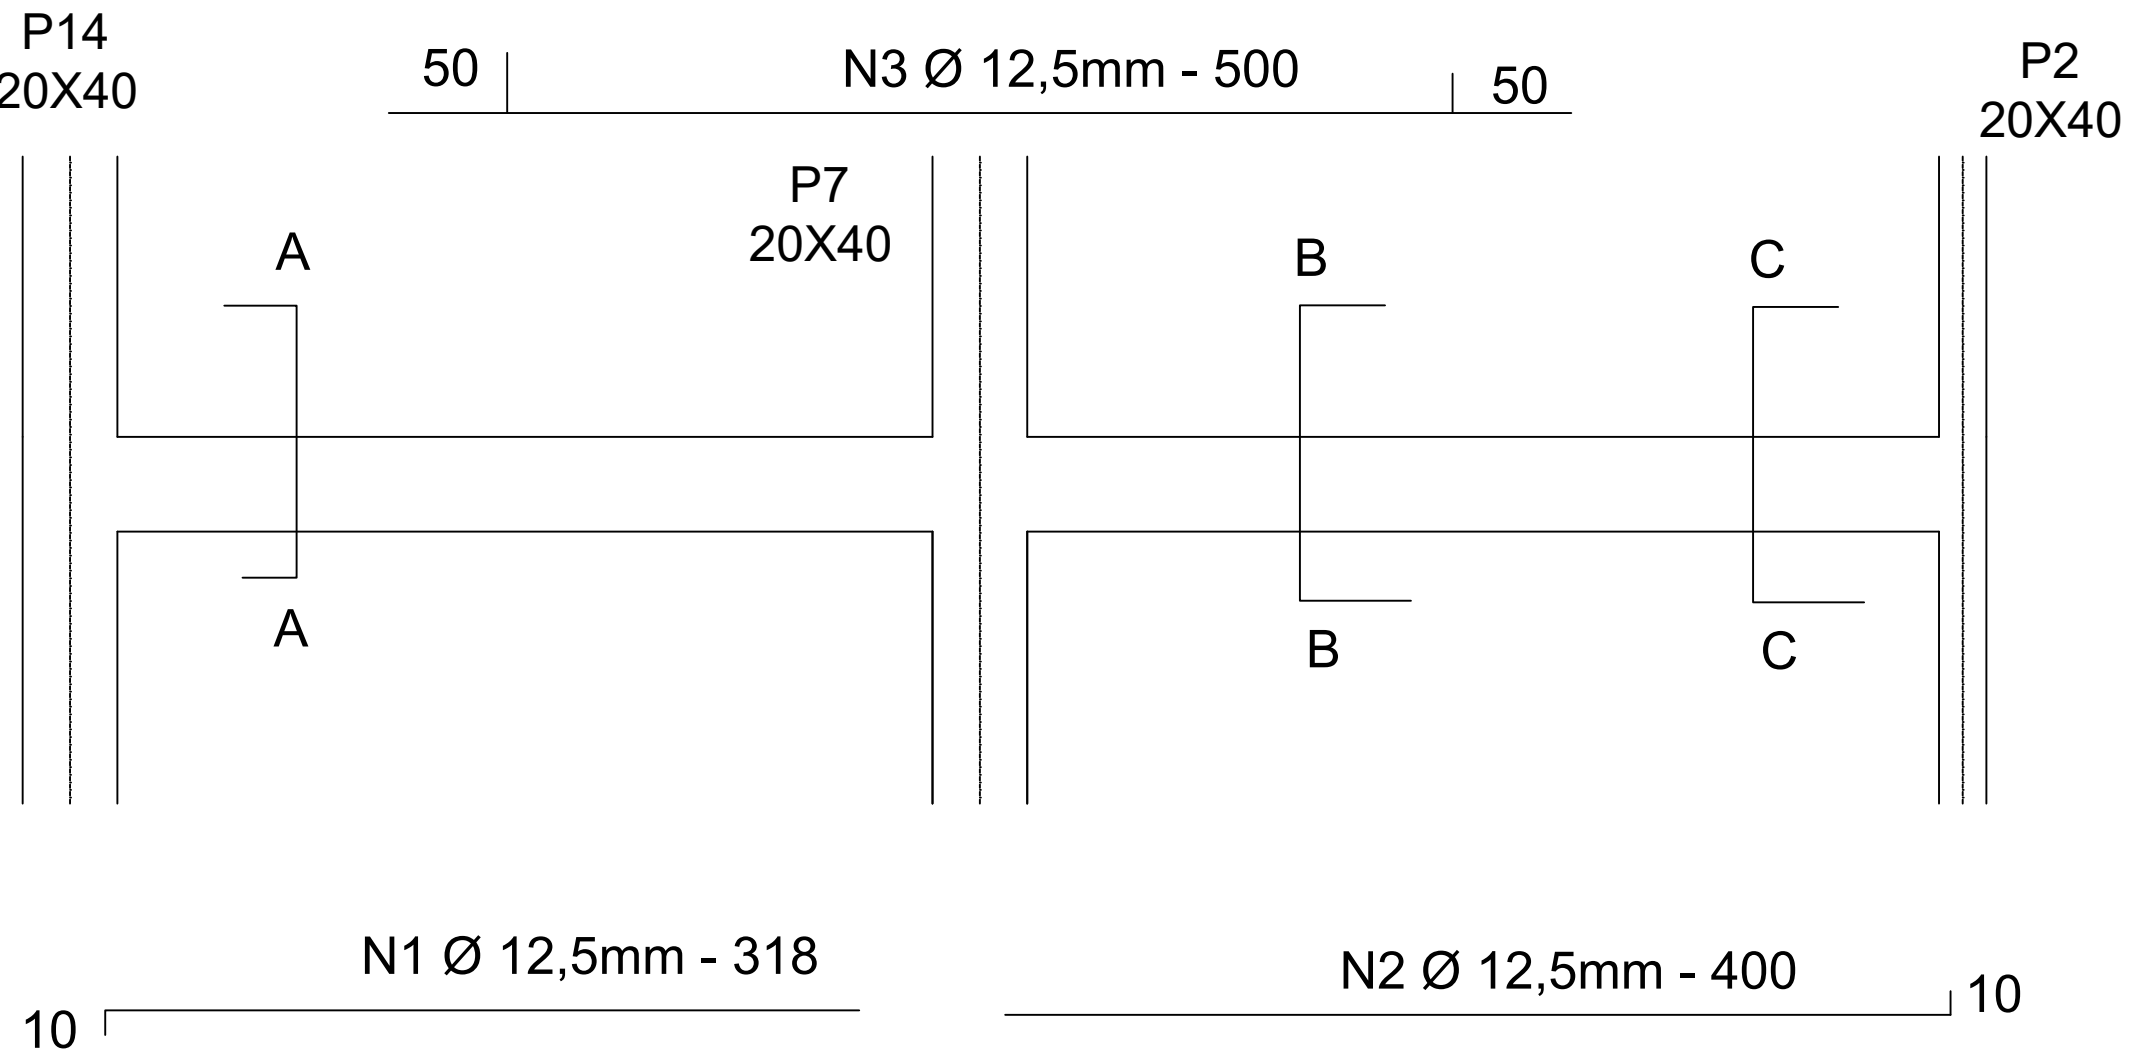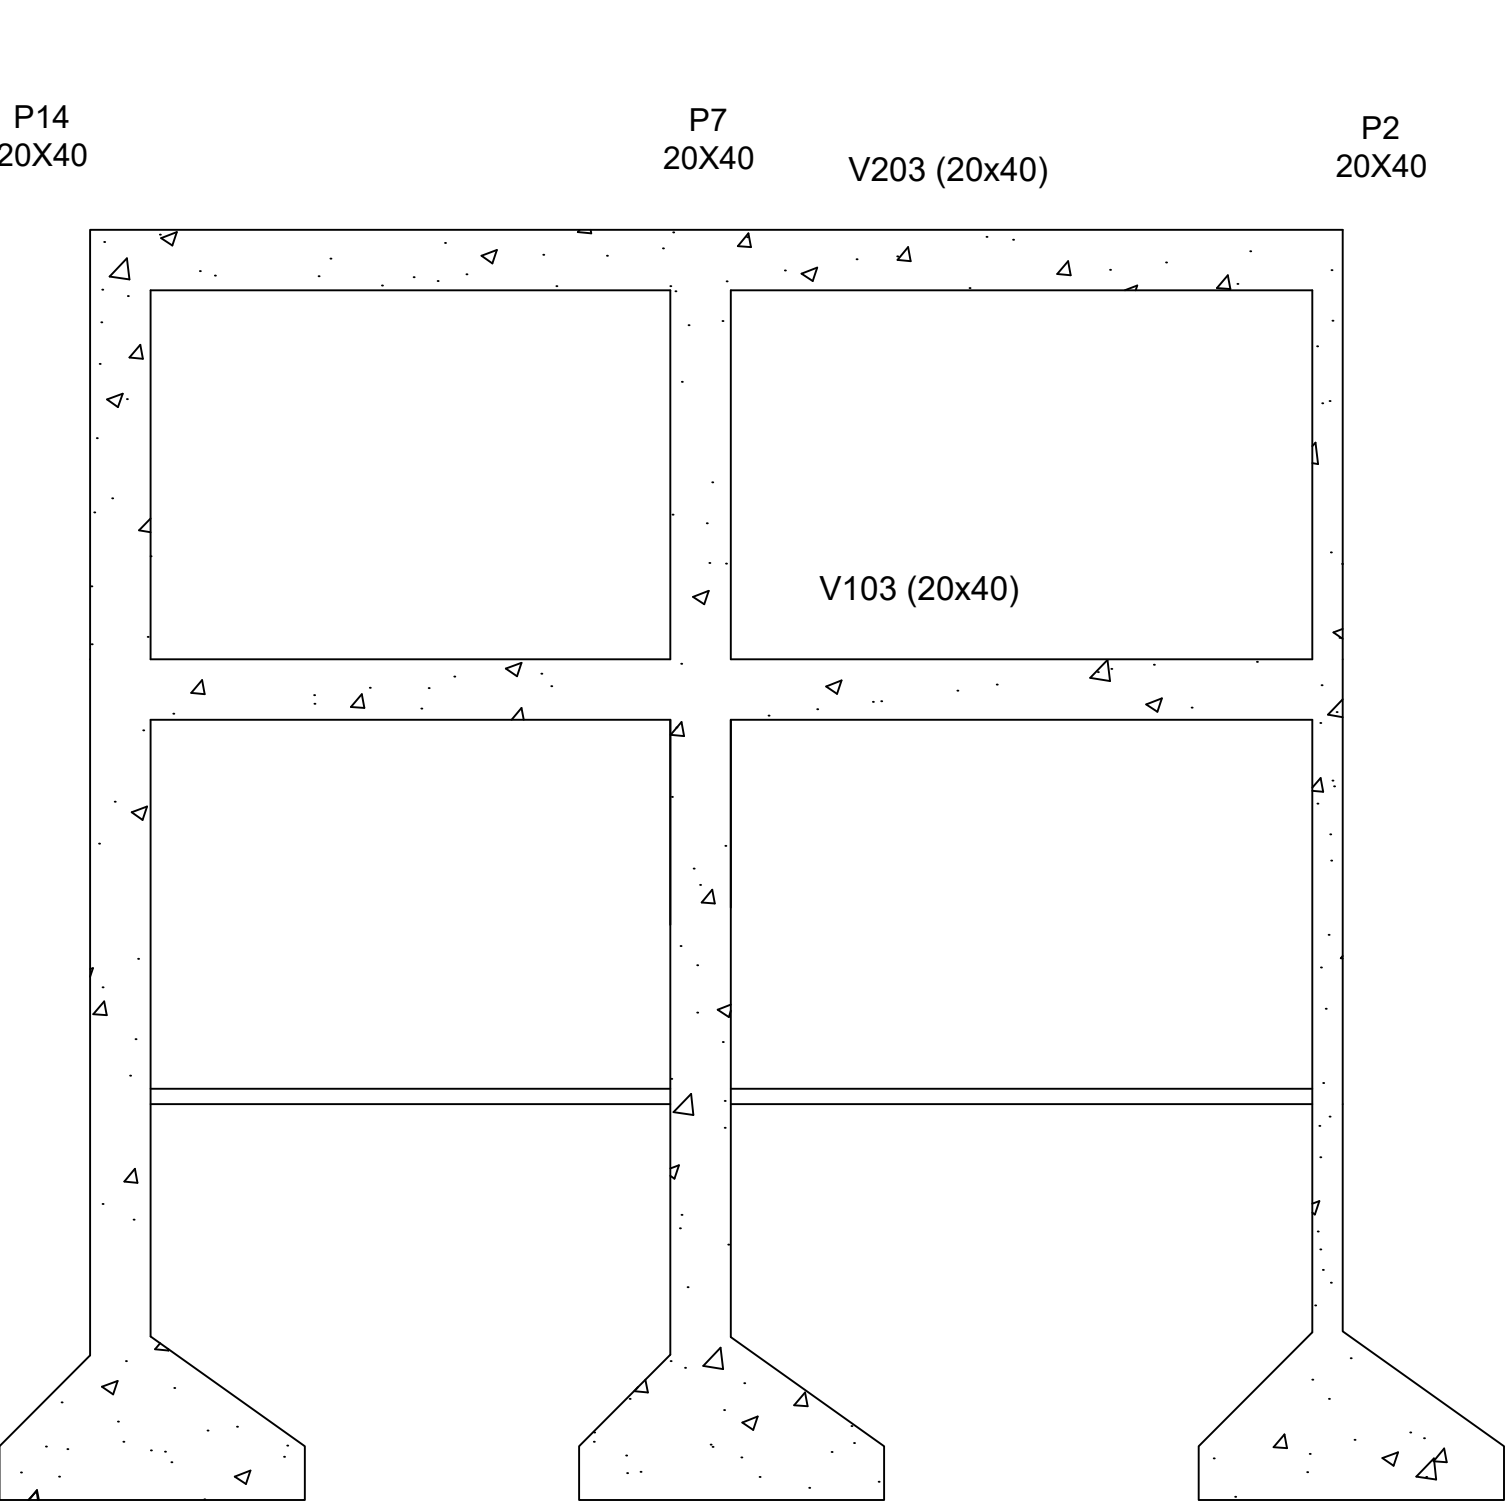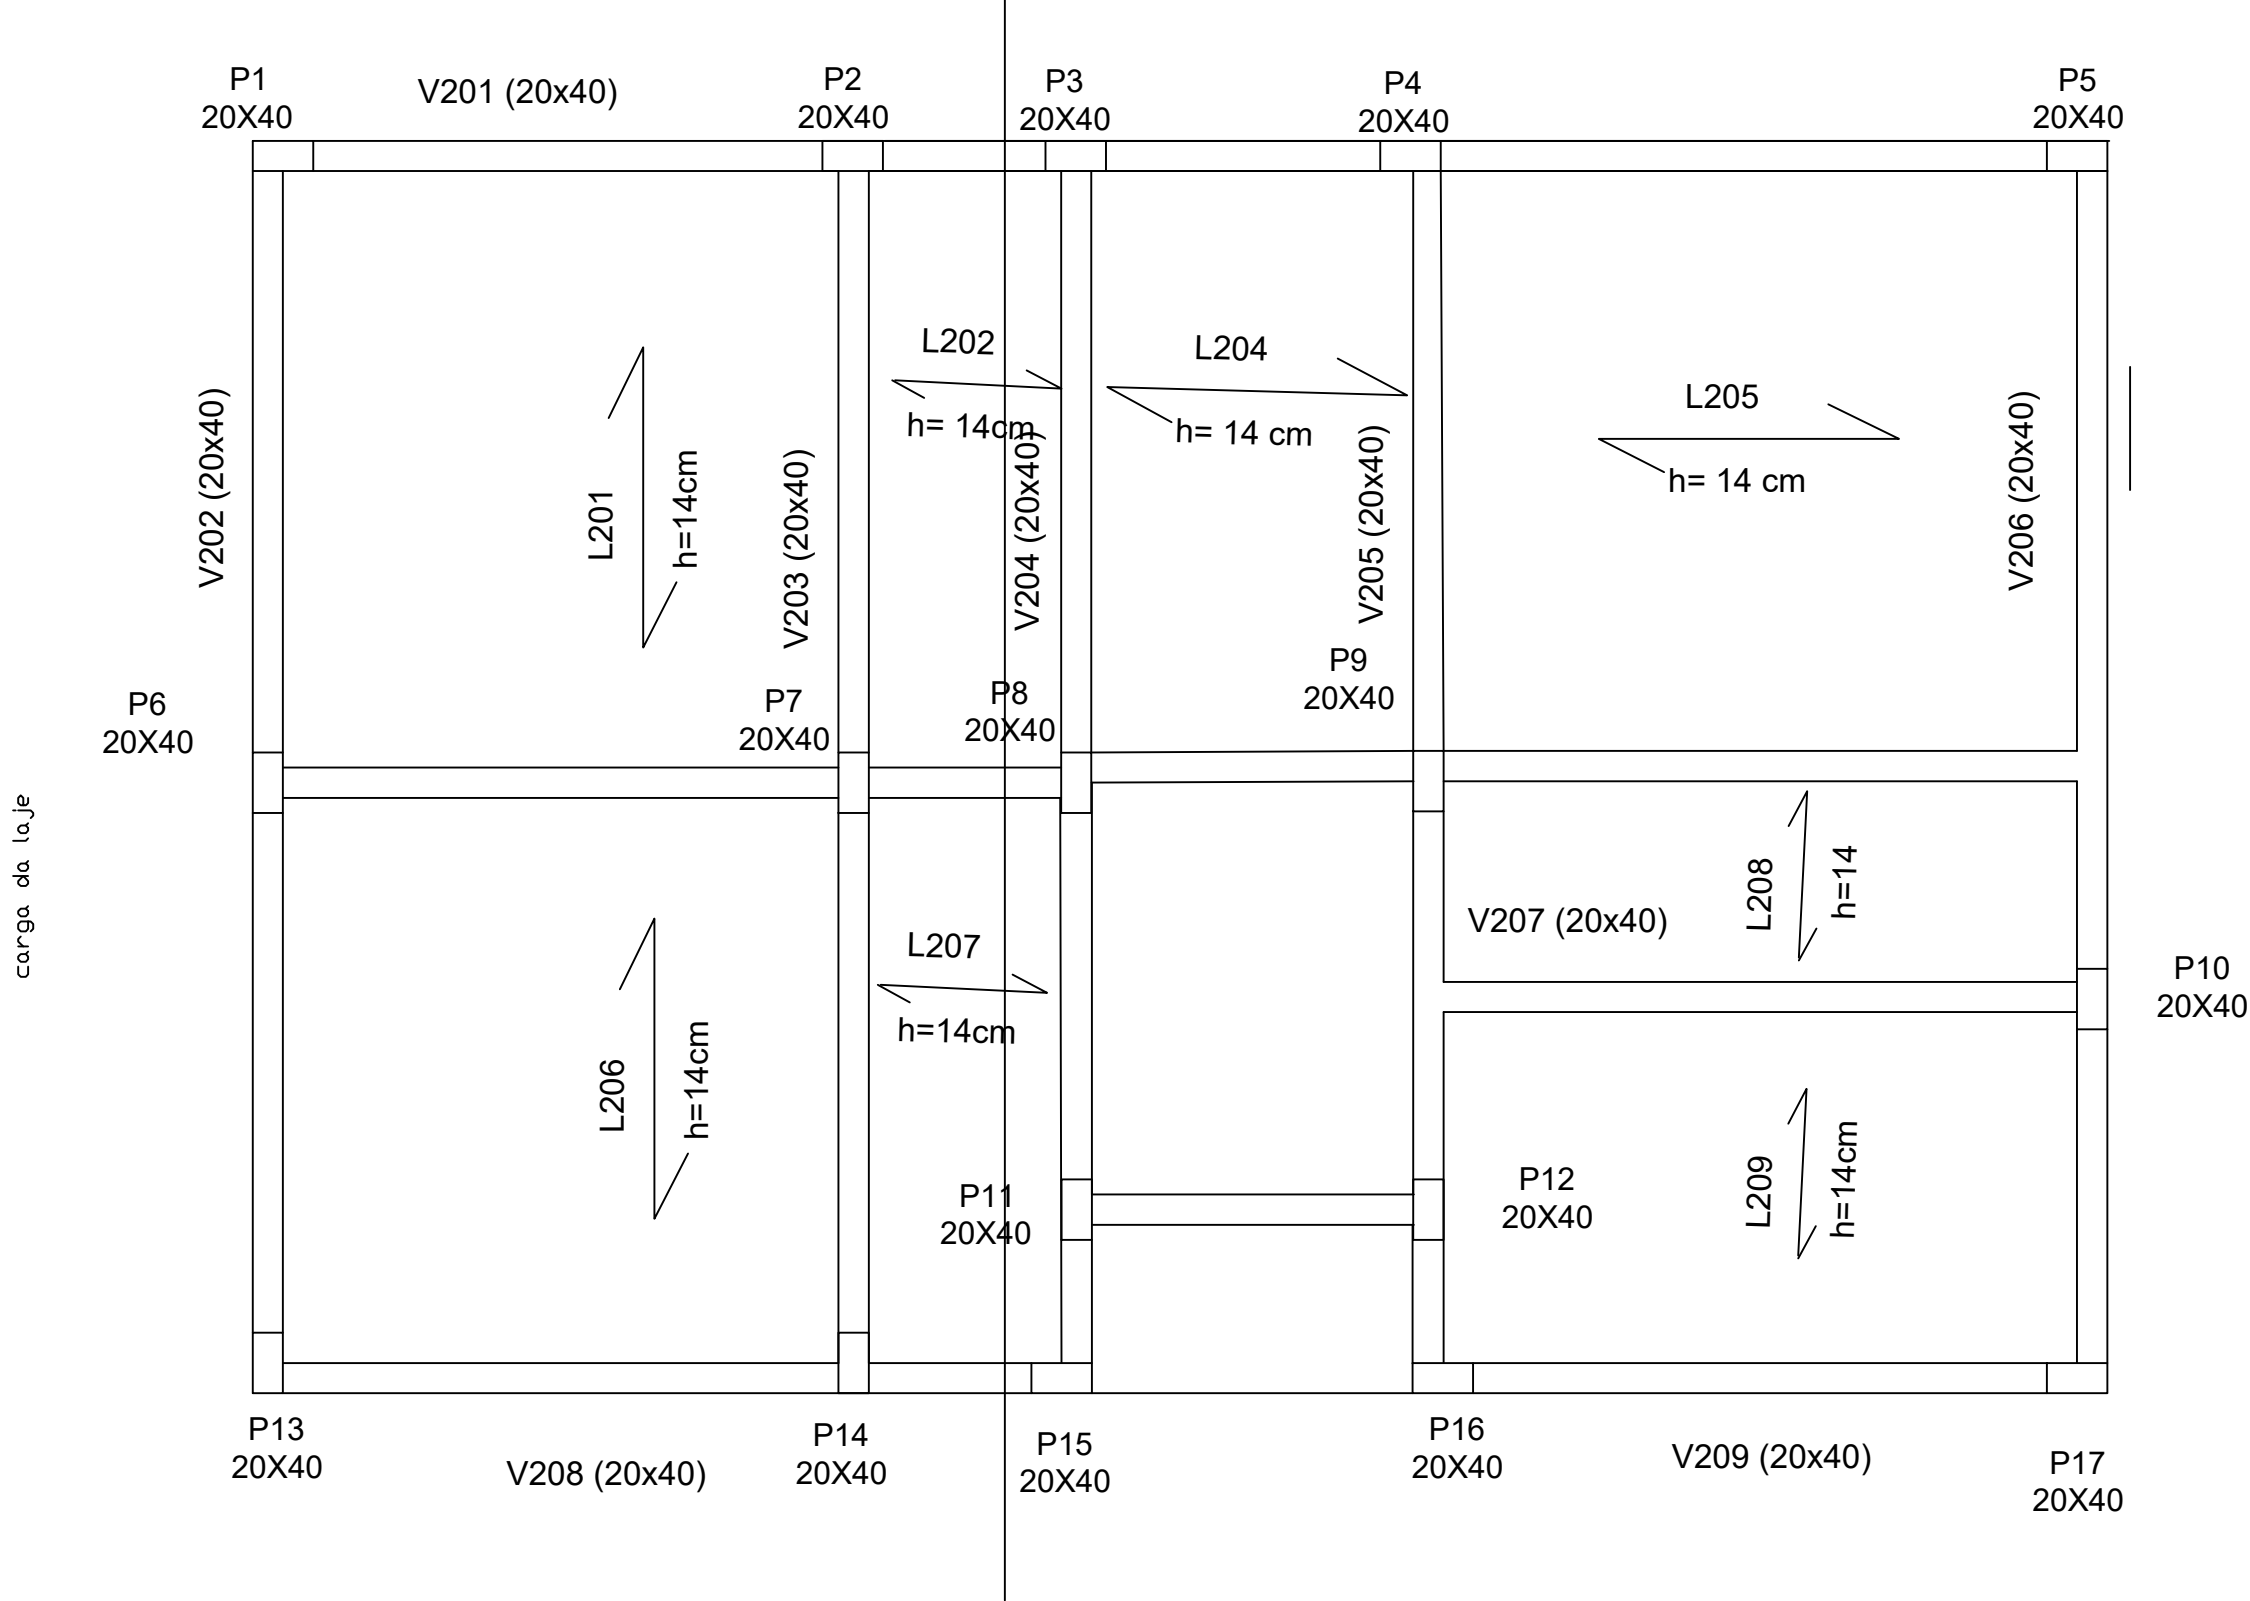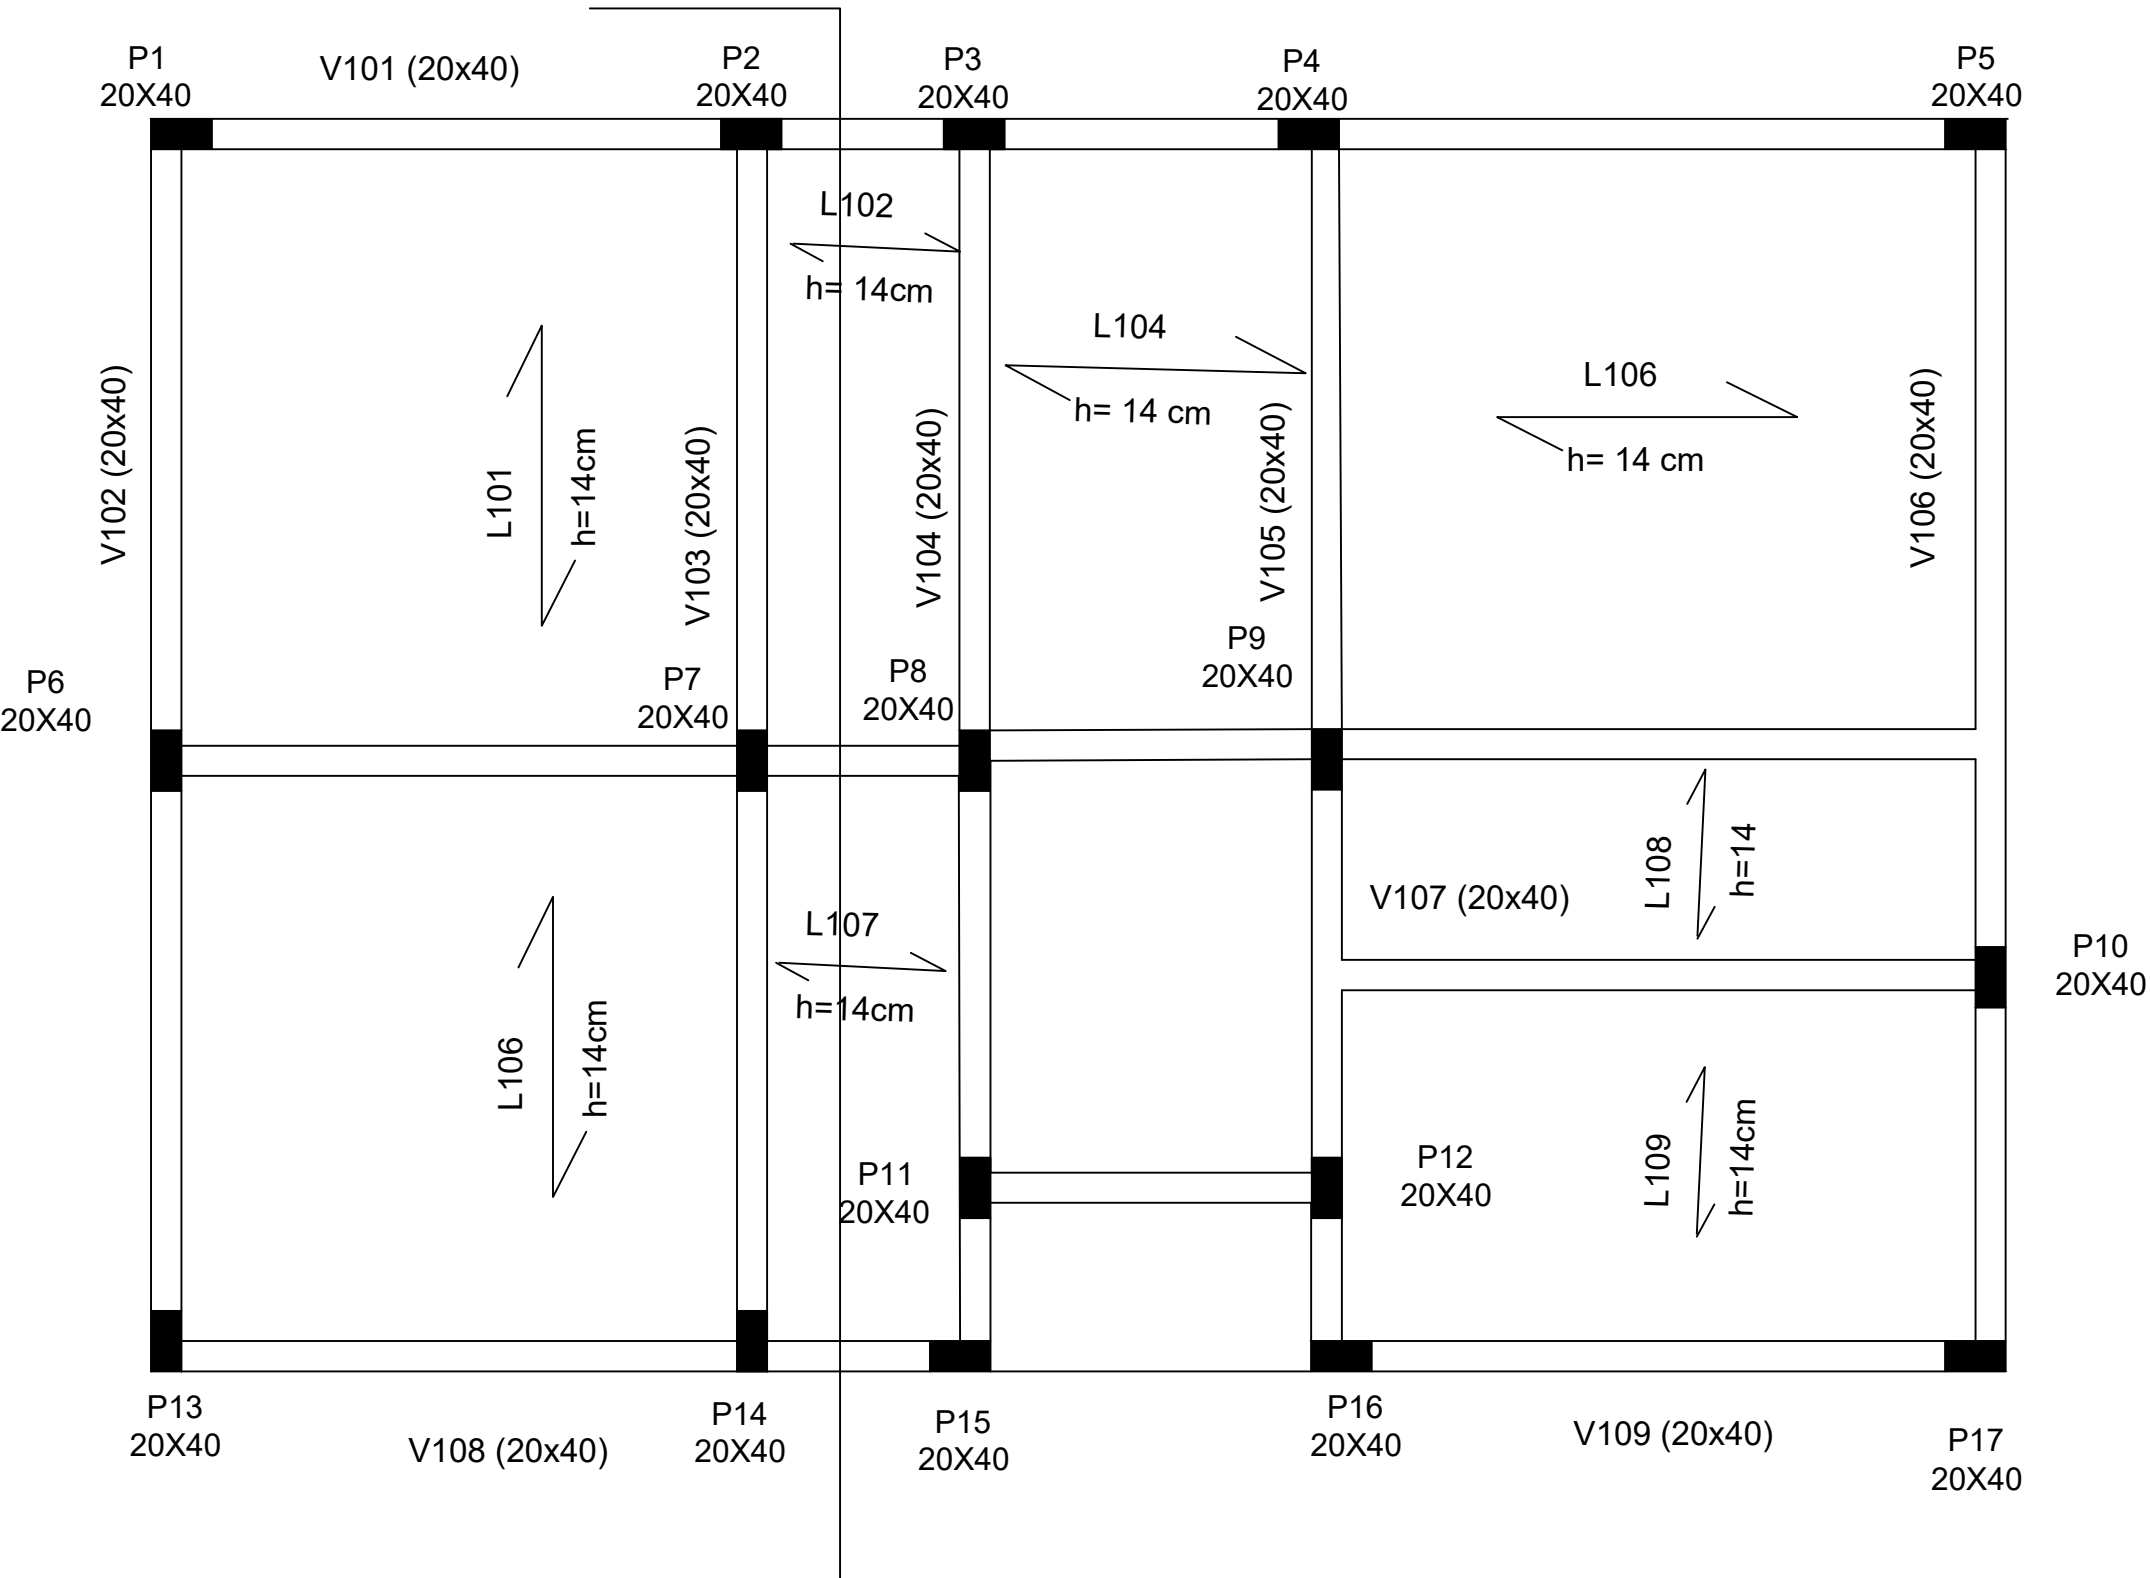


N1
CORTE - AA


Carregamento	Esp (m)	Gaamma (kN/m²)	Total (kN/m²)
Contra piso	0,04	21	0,84
Impermeabilizante	0,05	0,11	0,0055
Revestimento Gesso	0,02	15	0,3
Porcelanato	0,01	21	0,21
Sobrecarga		1,5	1,5
Total 1 (kN/m²)			2,8555

Paredes Sobre Laje		
Lx	Ly	Alaje (M²)
3,97	4,34	17,2298


Paredes					
MATERIAL	Esp (m)	Largura (m)	Pé direito (m)	Gaamma (kN/m³)	Carga (Kn)
Tijolo Furado	0,14	3,8	2,7	14	20,1096
Repoco	0,06	3,8	2,7	21	12,9276
impermeabiliz	0,04	3,8	2,7	0,11	0,045144
				Total 2 (kN/m²)	33,08234
Cpar (kN/m²)	1,92007				
Total 2 (Kn/m²)	4,77557				
hest (cm)	Peso próp. (kN/m²)		1,36		
hlaje (cm)					
Carga total (kN/m²)	6,13557	Especificações			
Capa (cm)	4	total (cm)	14		
Enchimento	40	Vigota	433 arranjo 1		
Inter eixo (cm)	50				

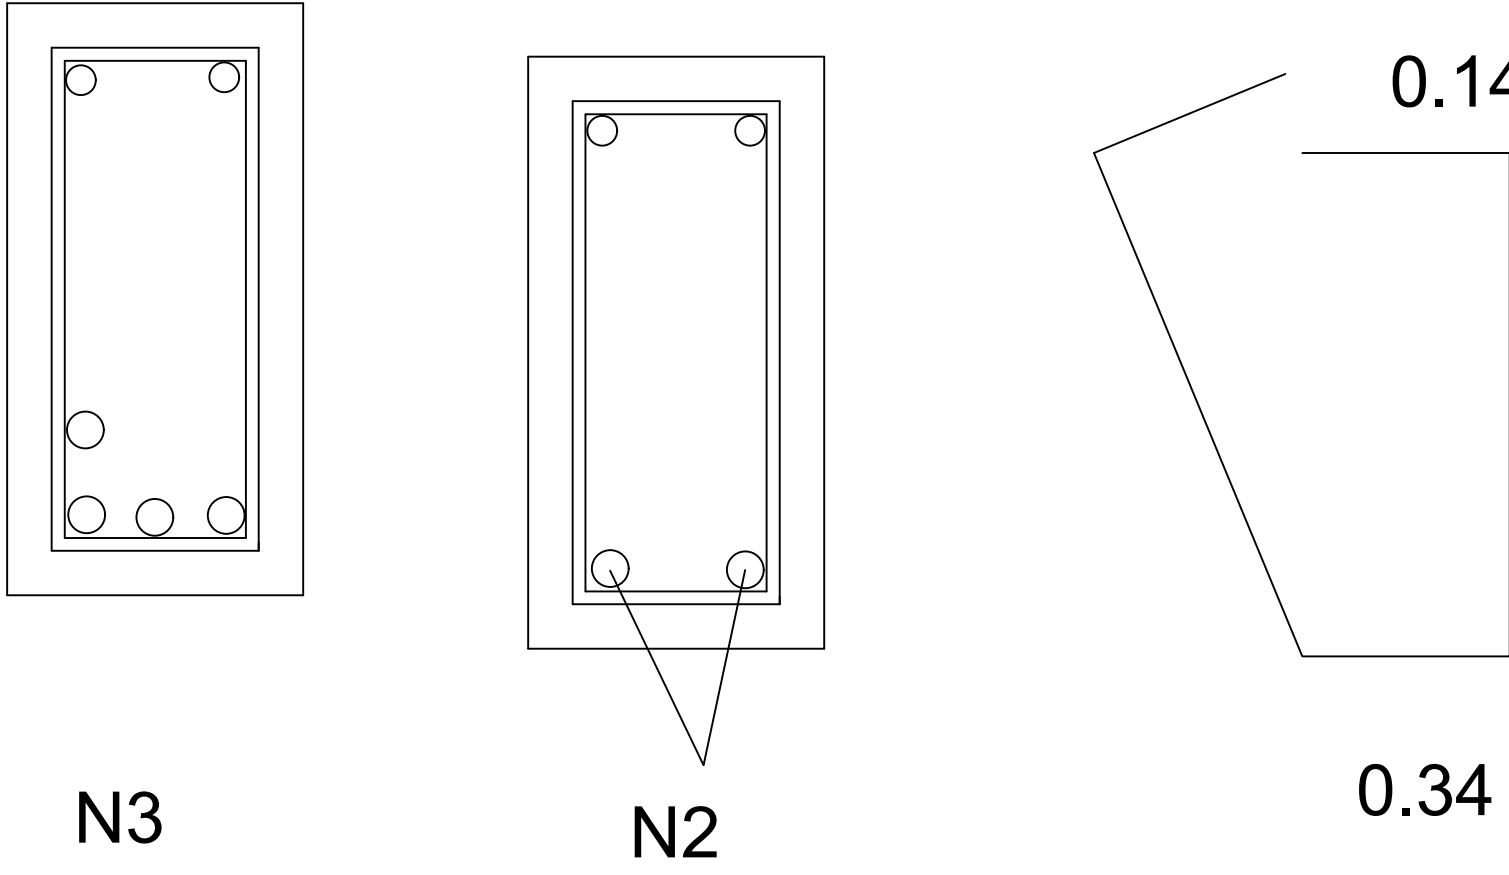



N3
CORTE - BB

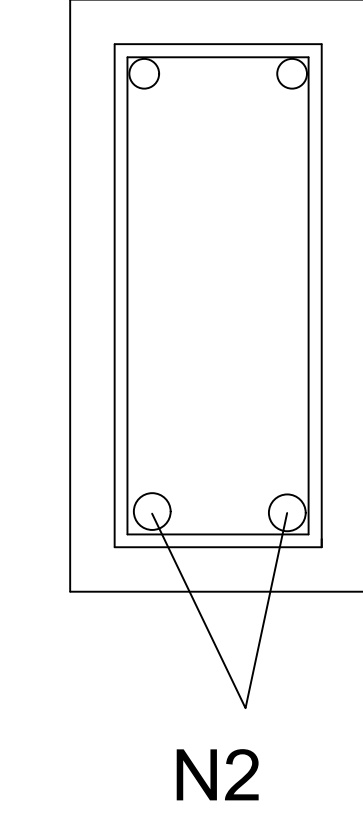


N2
CORTE - CC




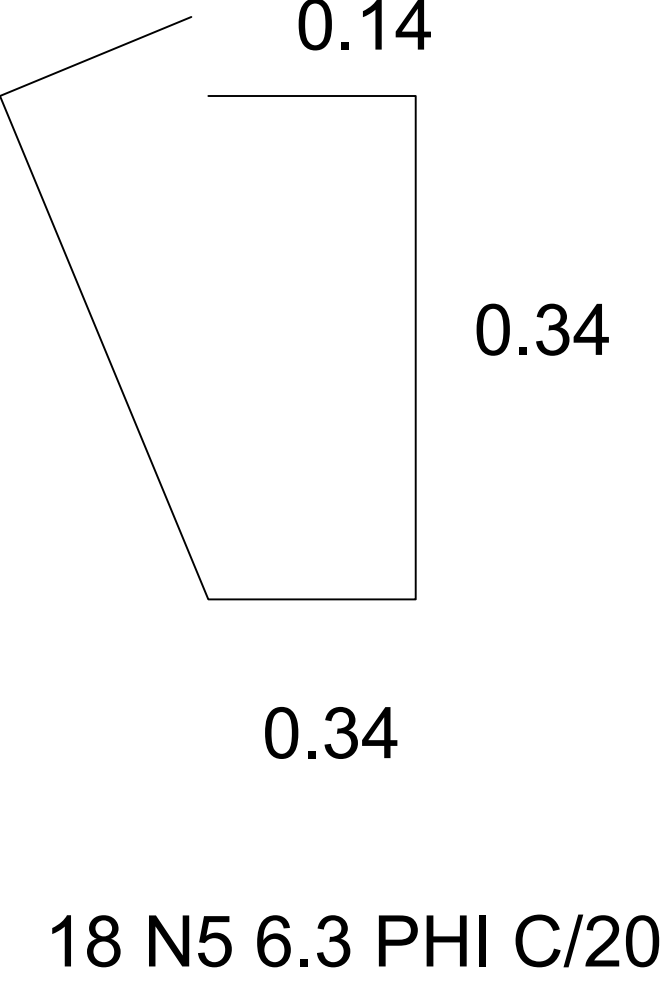


18 N5 6.3 PHI C/20 -

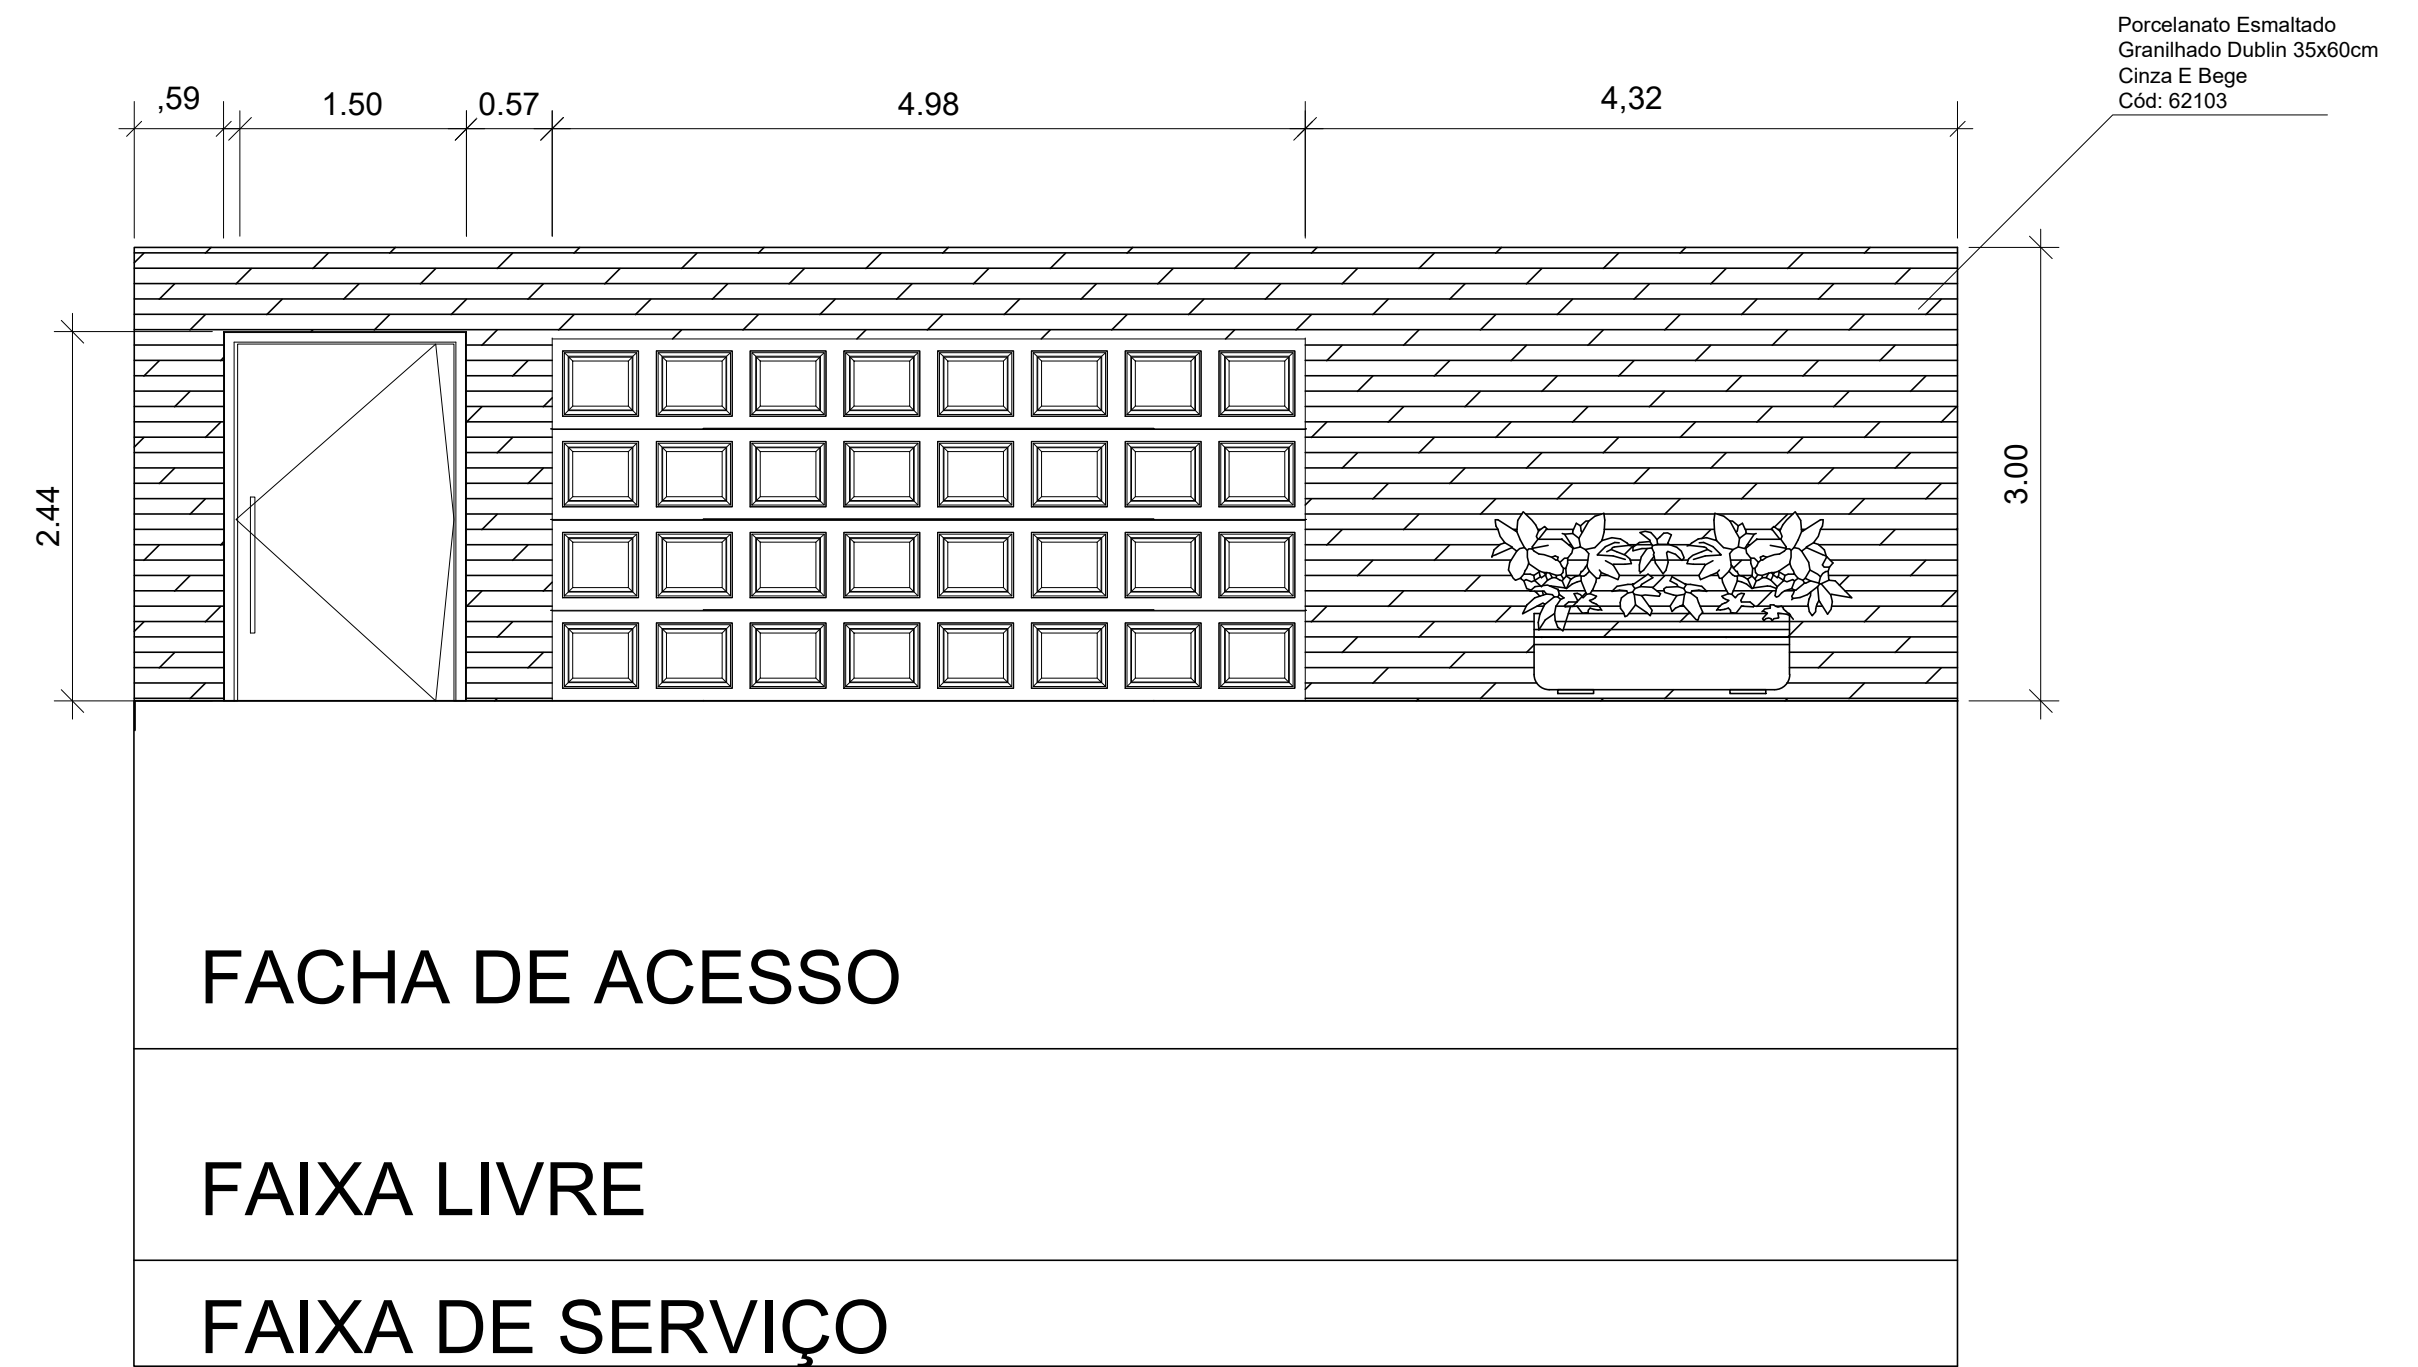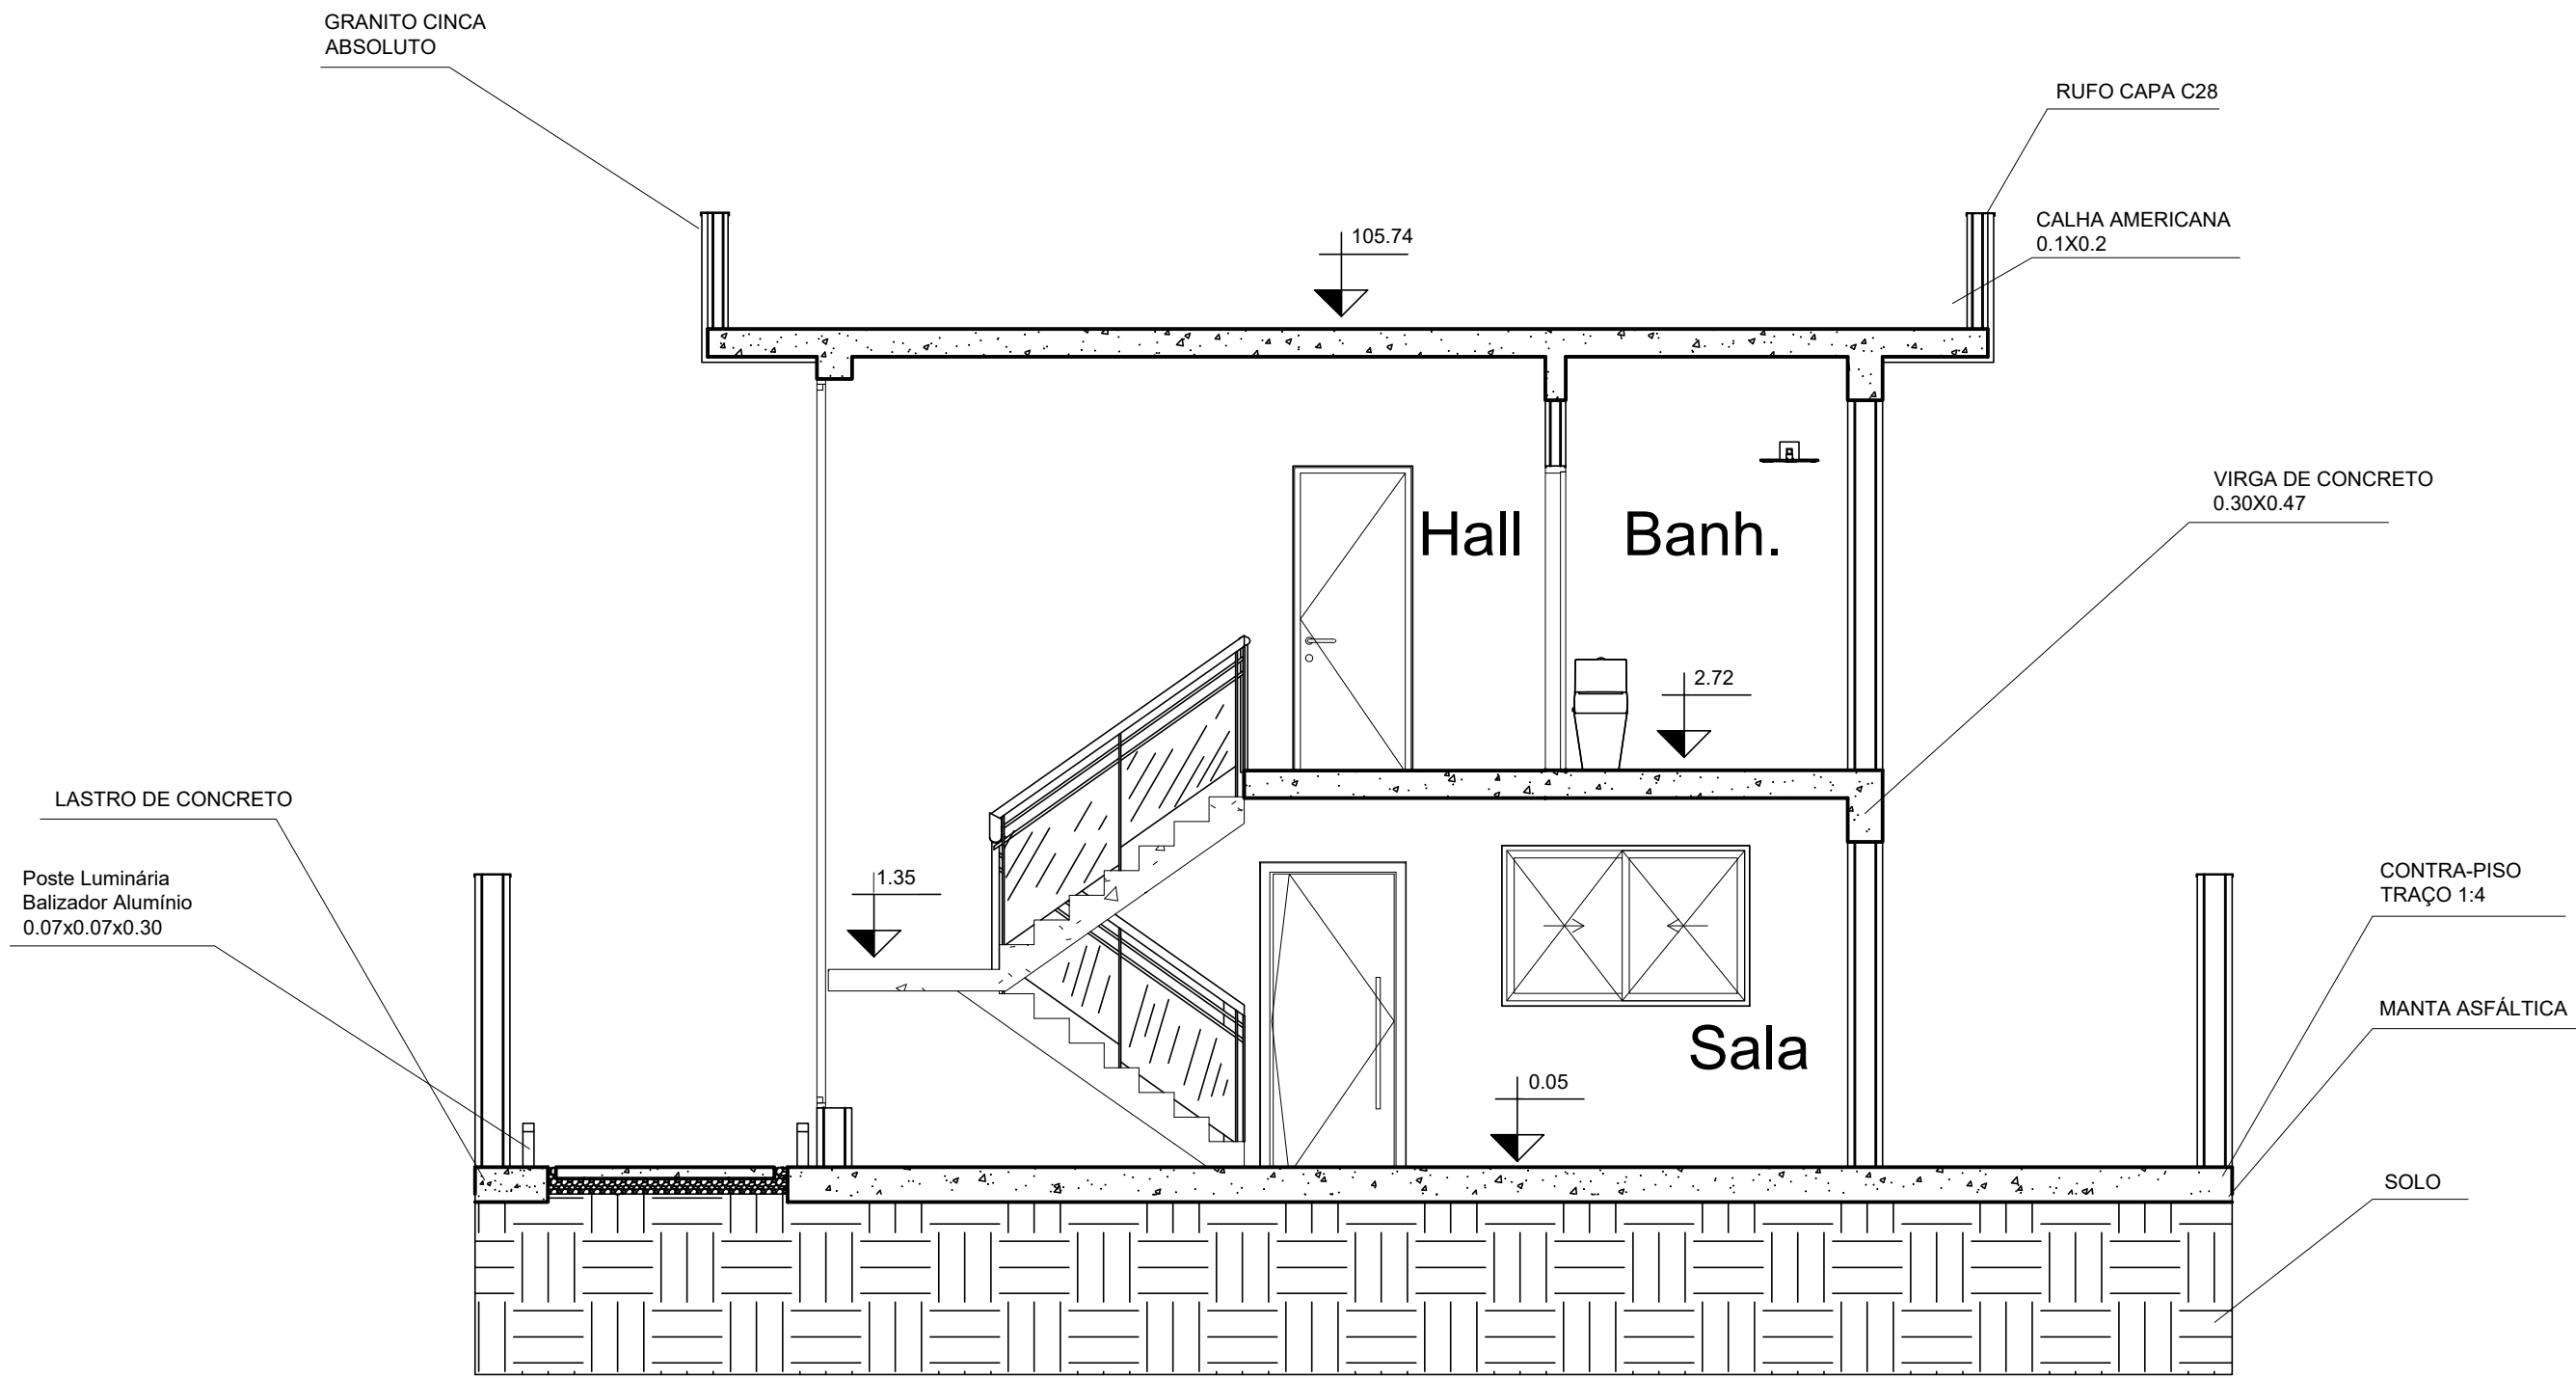


i 1%

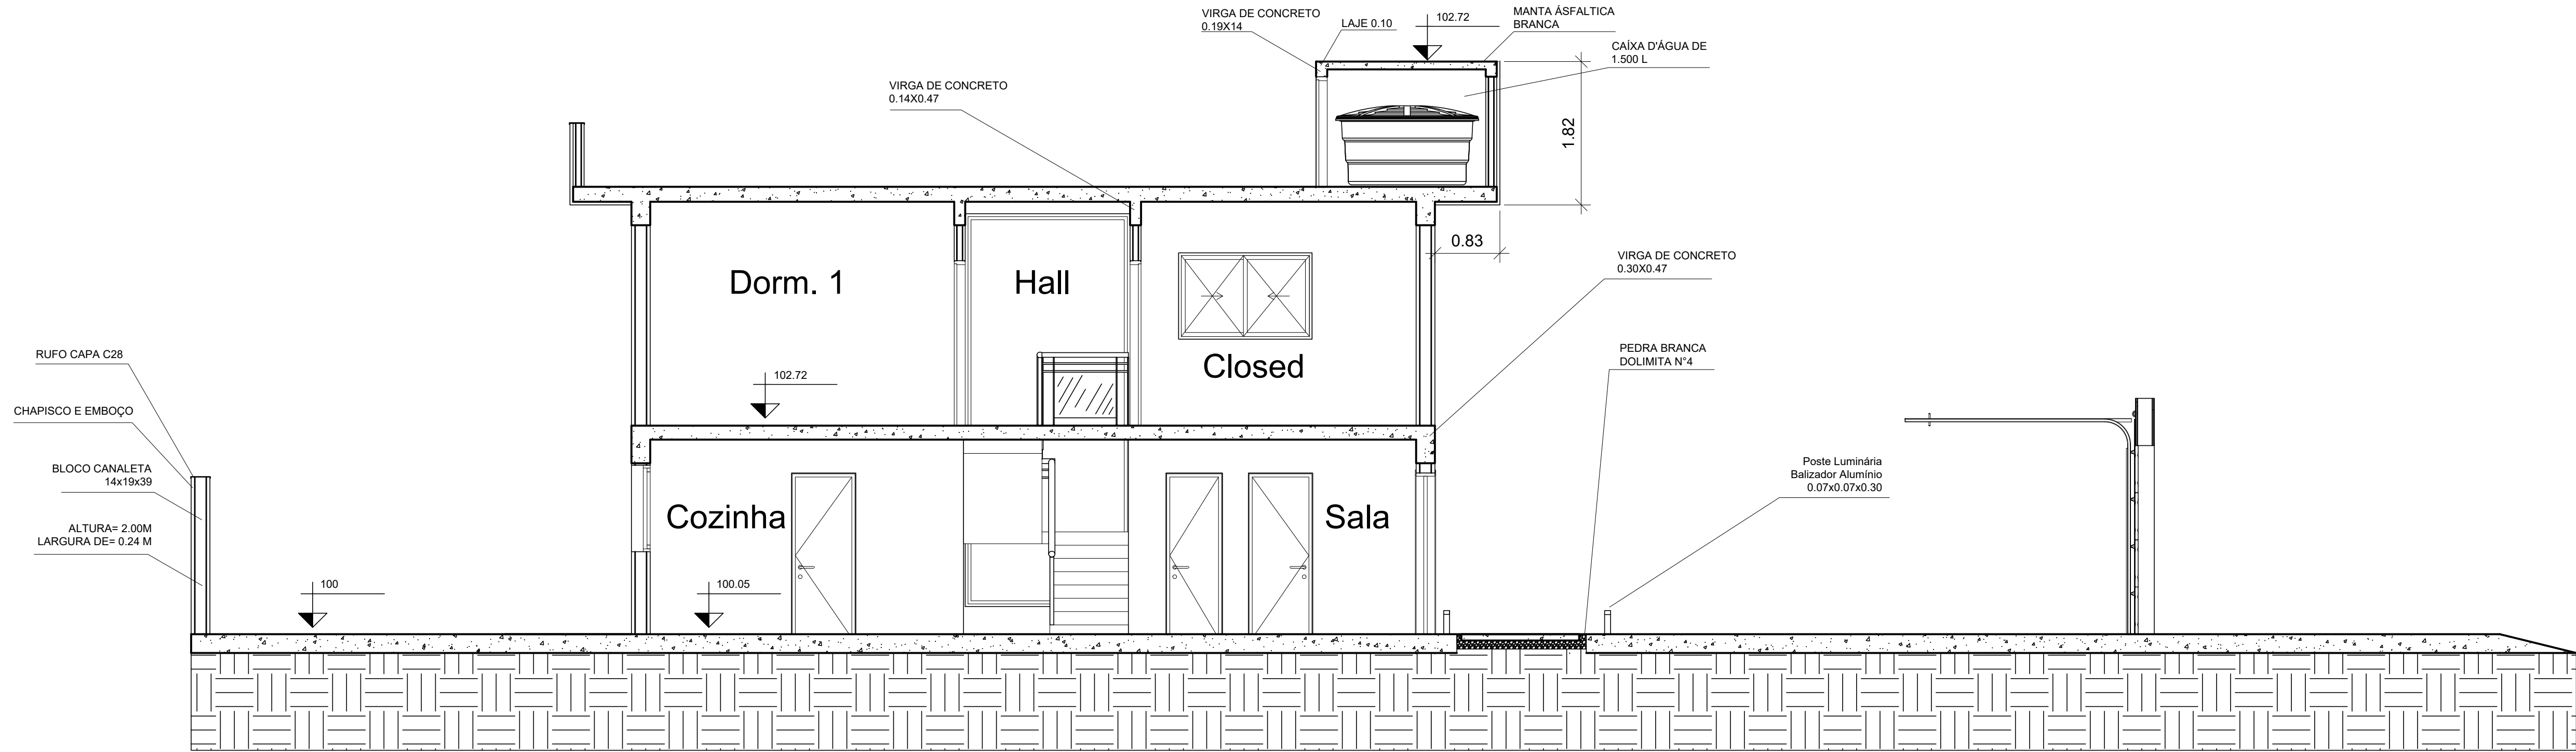

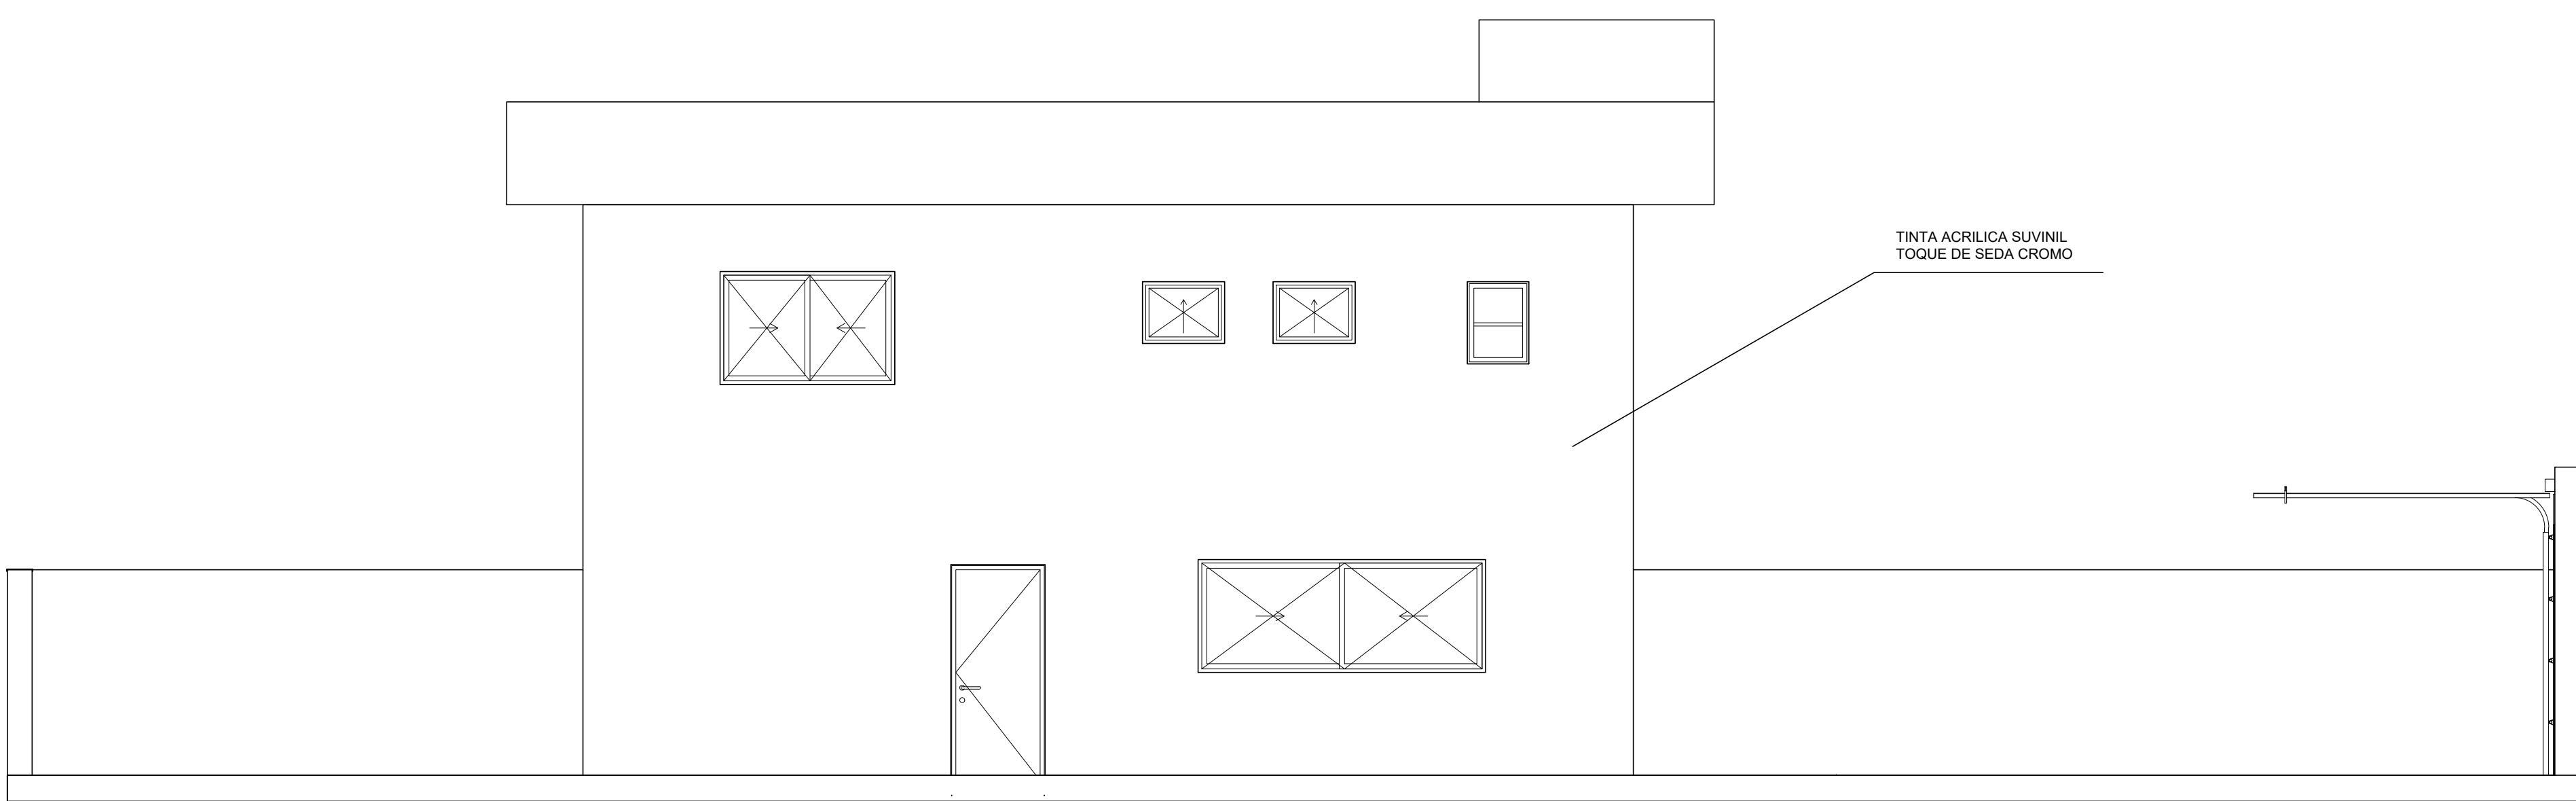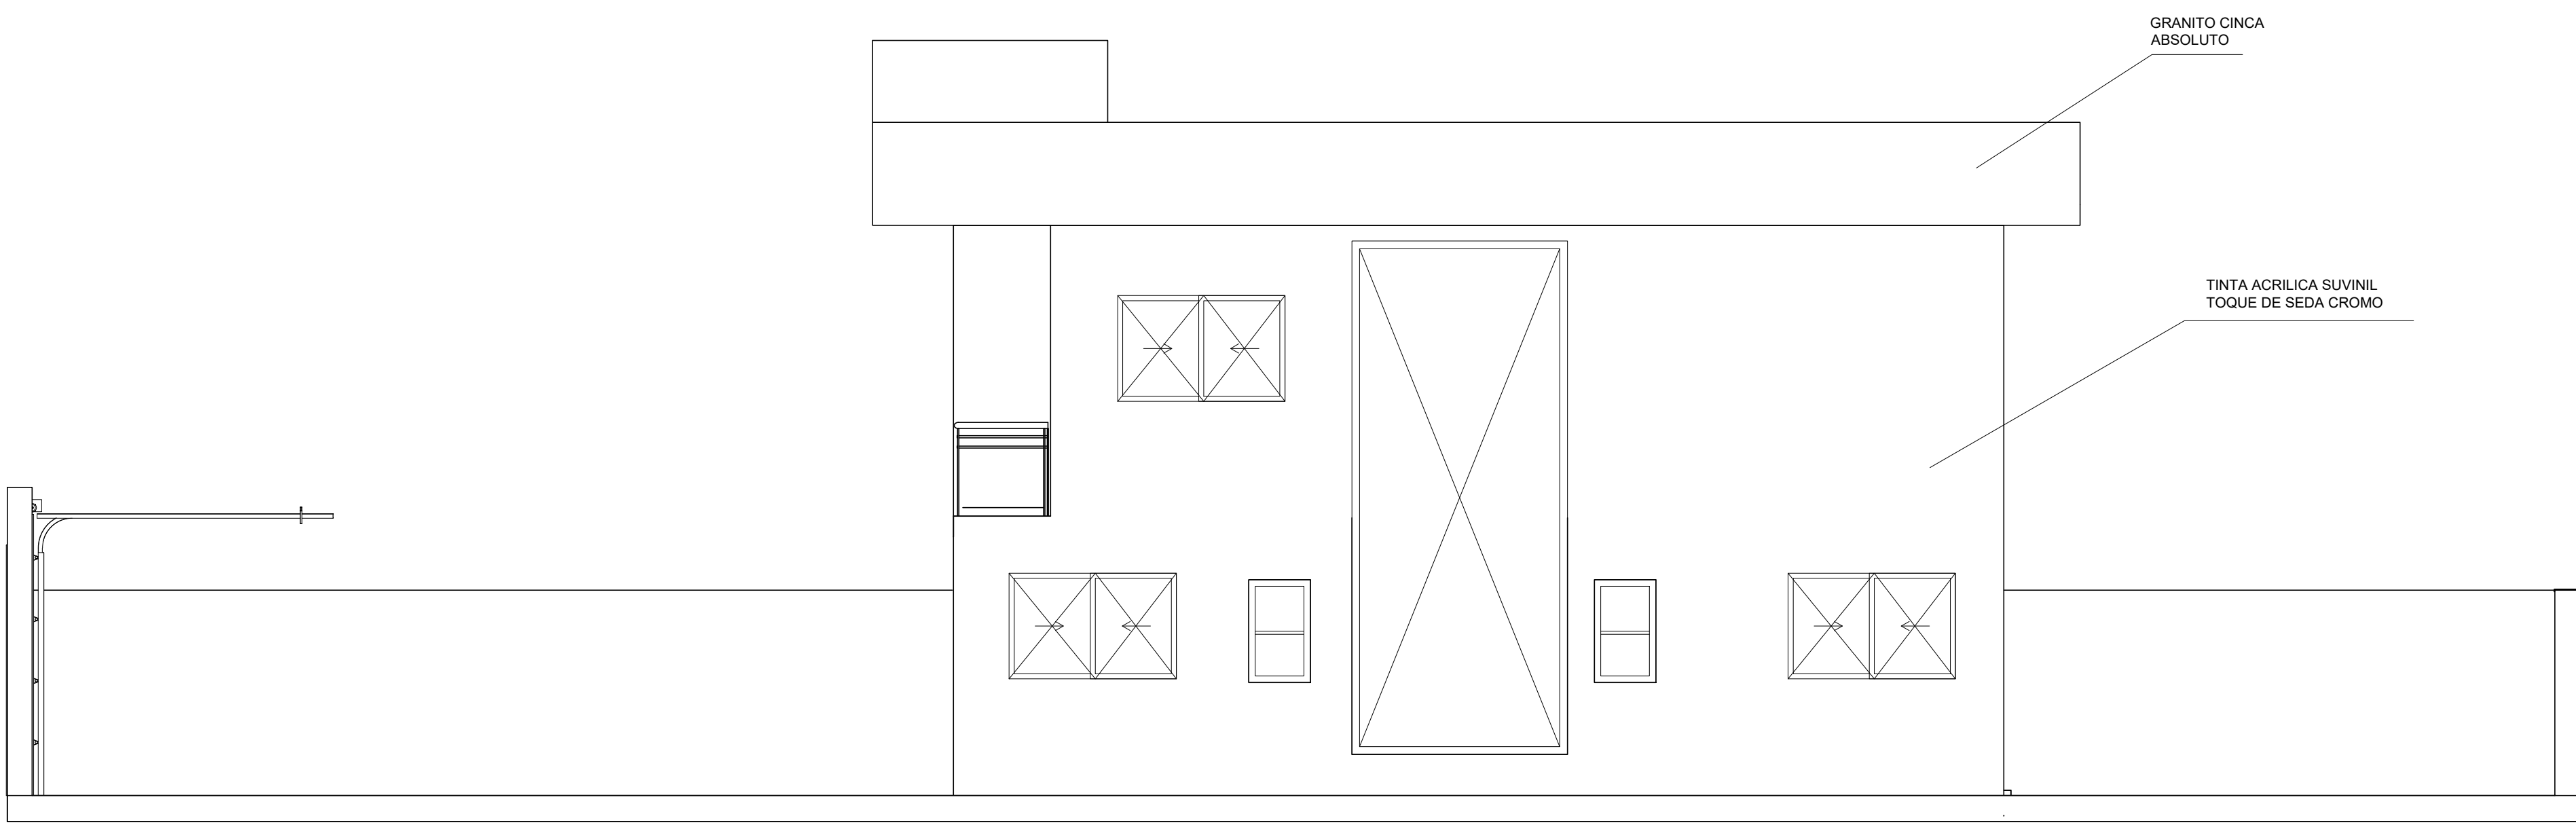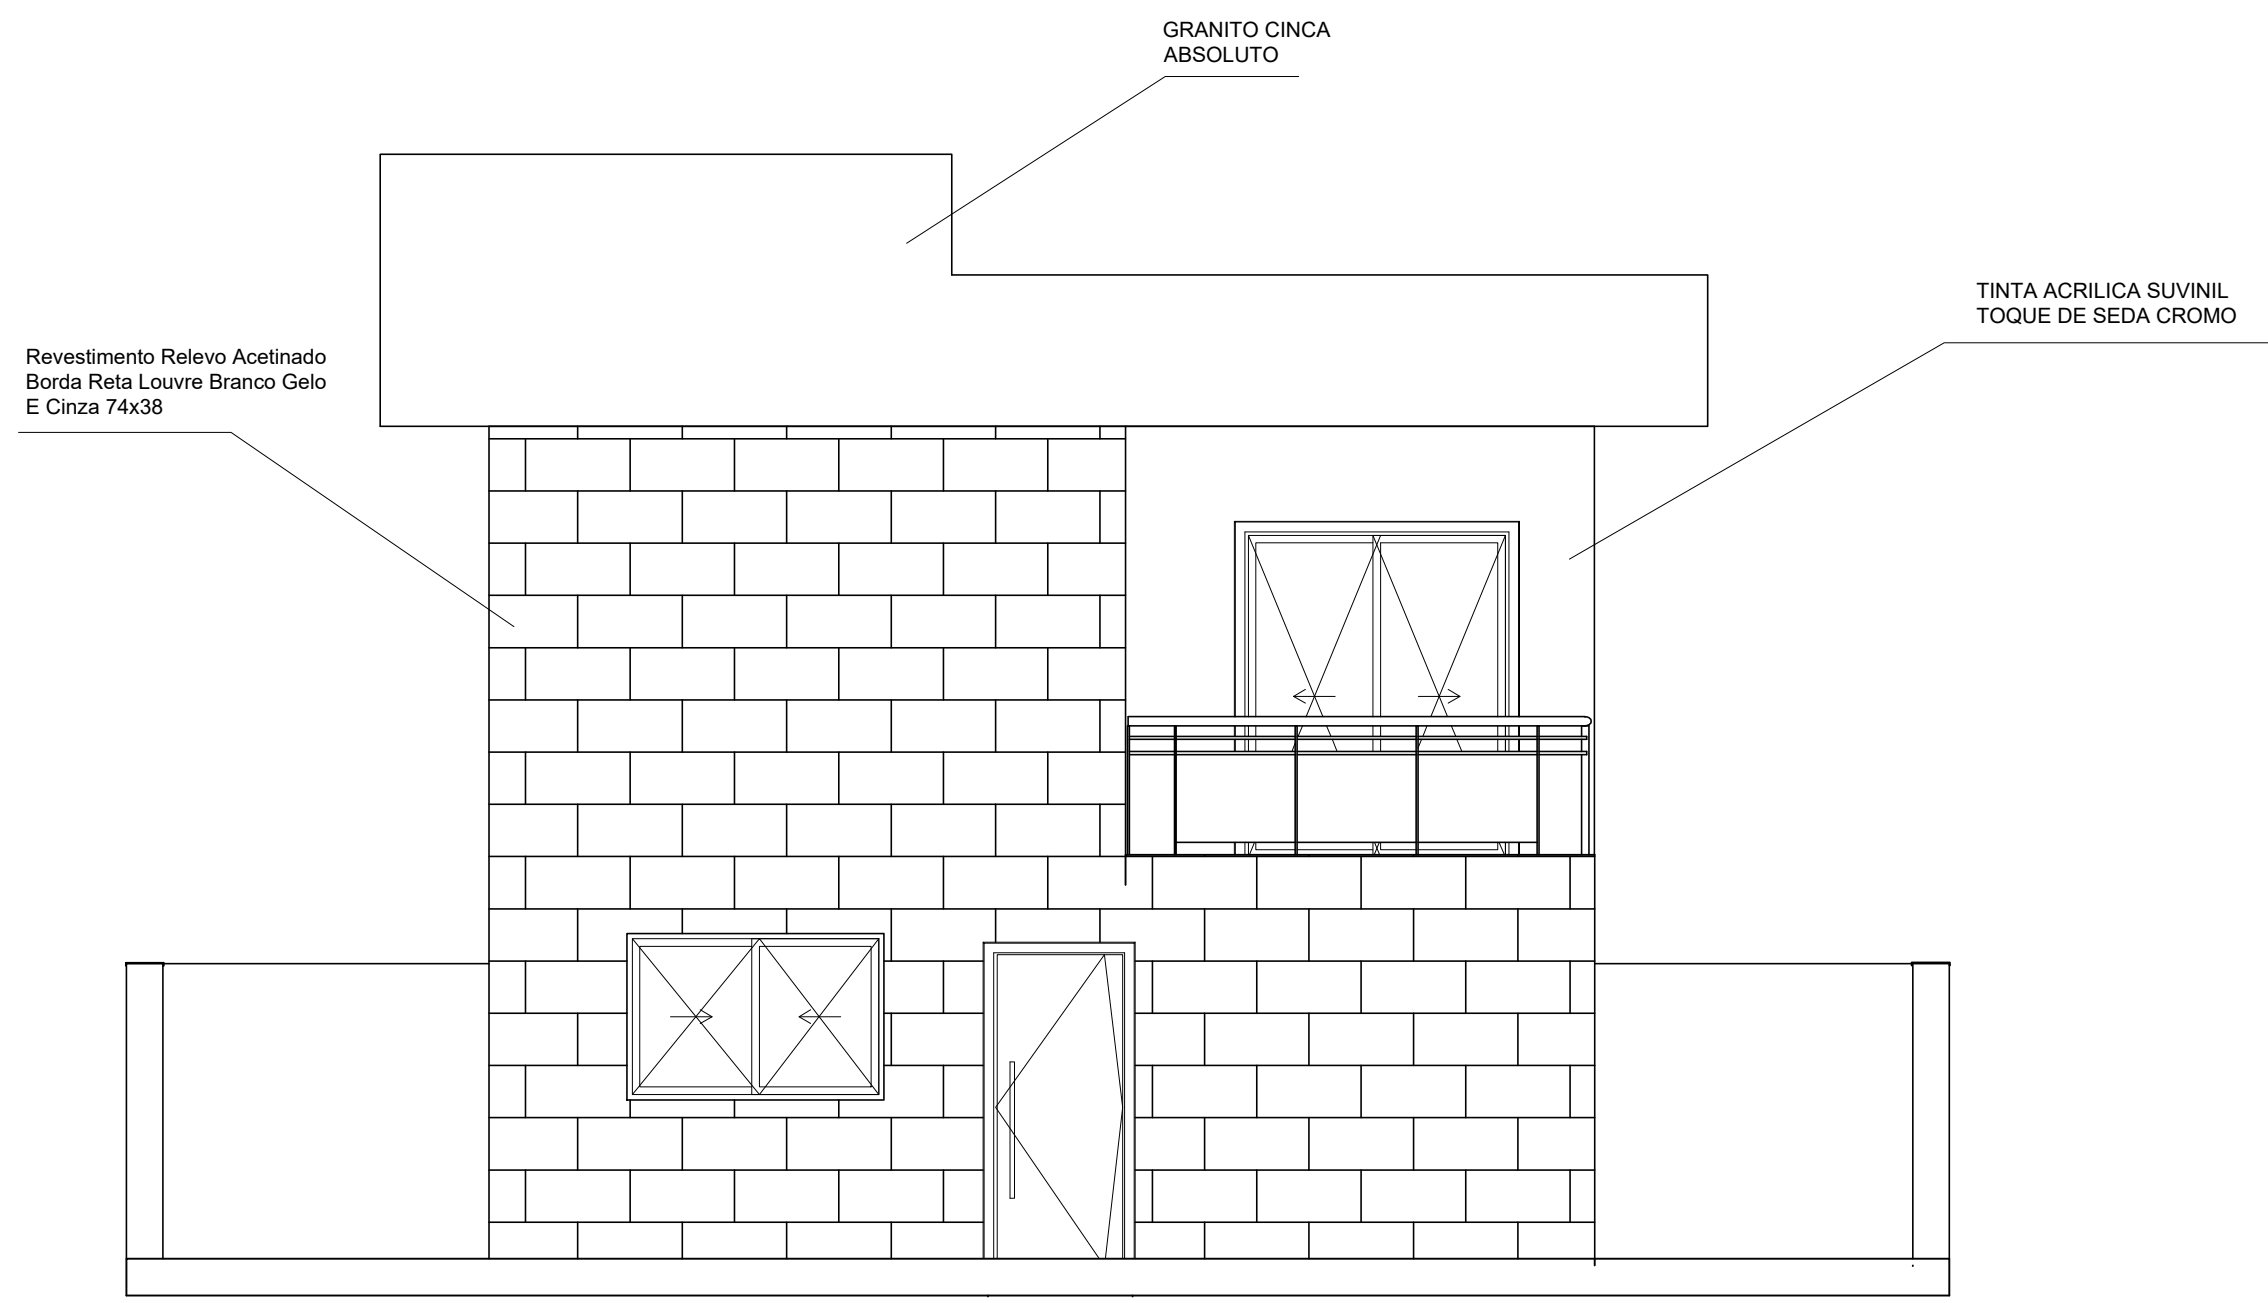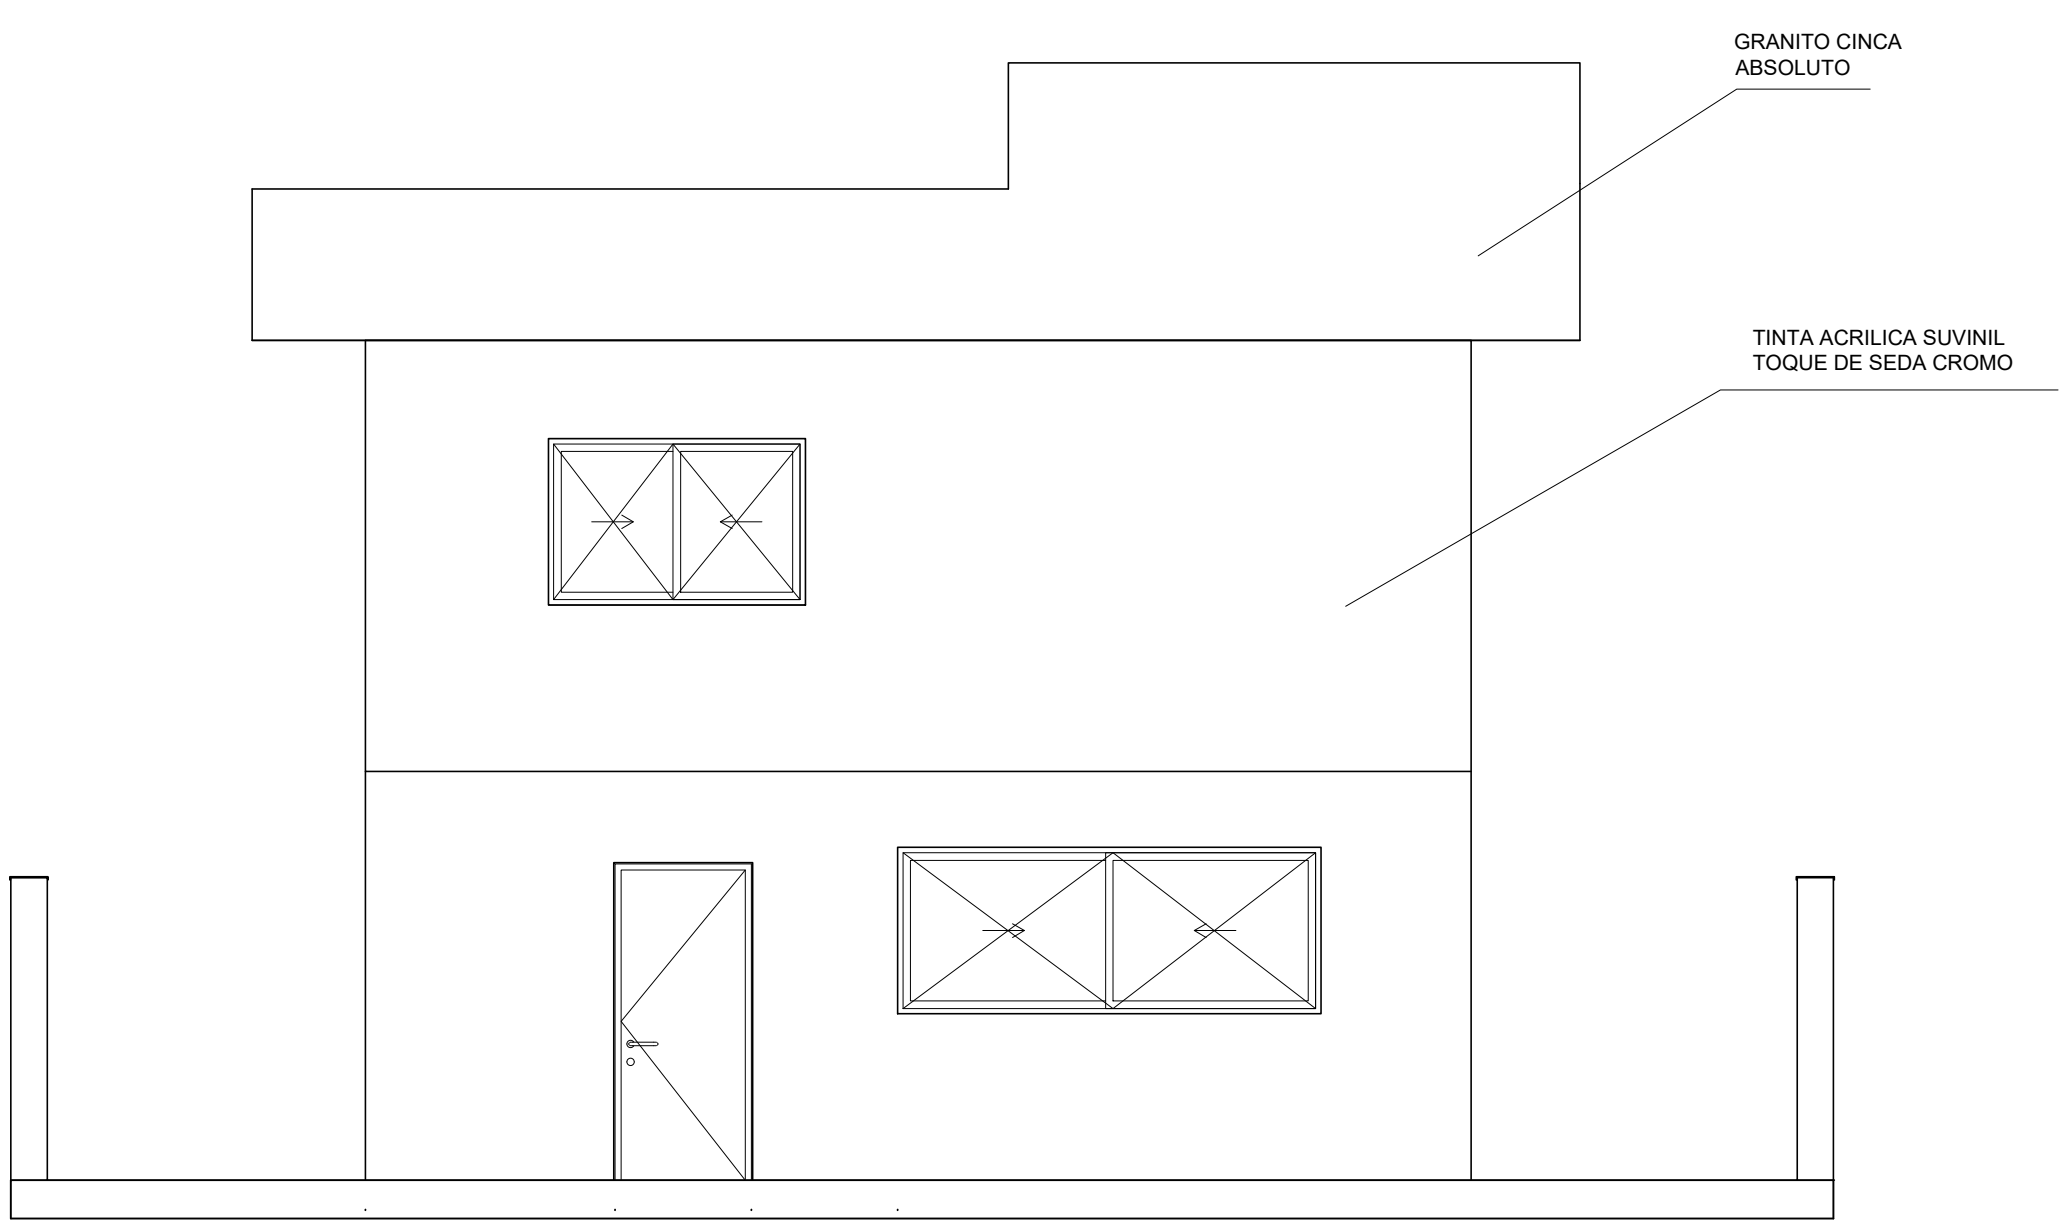


GRANITO CINZA ABSOLUTO

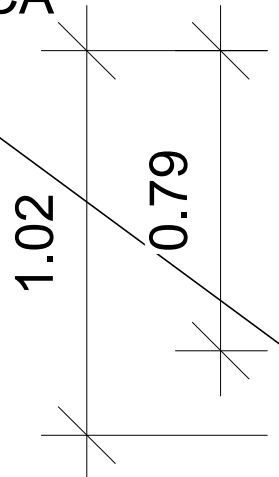

MANTA ASFÁLTICA BRANCA.

VIRGA DE CONCRETO 0.14X0.47

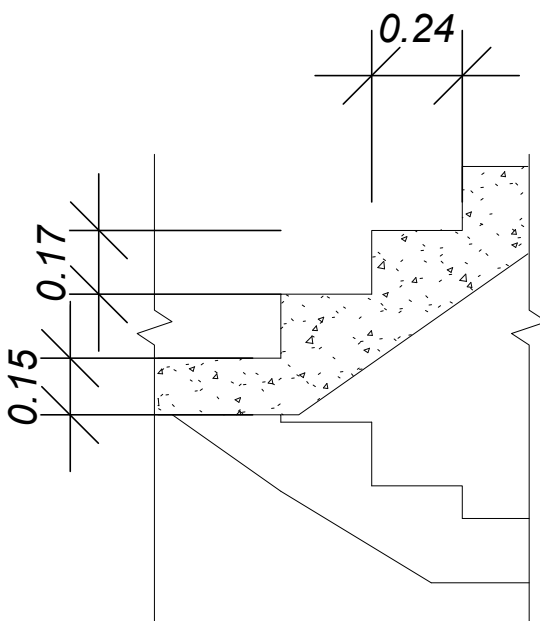


Tabelas de Esquadrias - Portas				
Marca de tipo	Material	Largura bruta	Altura bruta	Quantidade
P01	Madeira	0.92	2.10	1
P02	Madeira	0.72	2.10	5
P03	Madeira	0.62	2.10	4
P04	Madeira	0.82	2.10	2
P05	Madeira	1.70	2.10	1
P06	Aluminio	5.00	2.40	1
P07	Aluminio	1.52	2.40	1
P08	Aluminio	1.50	1.40	1
Total geral:				16

Tabela de janela							
Comentários de tipos	Marca de tipo	Largura bruta	Altura bruta	Altura do peitoril	Material	Vidro	Modelo
Sala	J01	1.70	1.10	1.10	Alumínio	Vidro Liso	Correr
Sala	J02	2.80	1.10	1.00	Alumínio	Vidro Liso	Correr
Cozinha	J03	2.80	1.10	1.10	Alumínio	Vidro Liso	Correr
Escritório	J04	1.70	1.10	1.10	Alumínio	Vidro Liso	Correr
Lavabo	J05	0.60	1.00	1.10	Alumínio	Vidro Fosco	MAXIM-AR
Escada	J06	2.10	5.00	0.40	Alumínio	Vidro Liso	Fixa
Banh. Área De Serviços	J07	0.60	1.00	1.10	Alumínio	Vidro fosco	MAXIM-AR
Áreaa De Serviços	J08	1.70	1.10	1.10	Alumínio	Vidro Liso	Correr
Dorm. 1	J09	1.70	1.10	1.10	Alumínio	Vidro Liso	Correr
Dorm. 2	J10	1.70	1.10	1.10	Alumínio	Vidro Liso	Correr
Banh. Superior	J11	0.80	0.60	1.50	Alumínio	Vidro, fosco	MAXIM-AR
Banh. Suíte	J12	0.80	0.60	1.50	Alumínio	Vidro, fosco	MAXIM-AR
Closed	J13	0.60	0.60	1.30	Alumínio	Vidro, fosco	MAXIM-AR
Suíte	J14	1.70	1.10	1.10	Alumínio	Vidro Liso	Correr


Total geral: 14

TABELA RESUMO DE ACABAMENTOS							
	ITEM	MATERIAL	DIMENSÃO	COR	MODELO/CÓDIGO	FABRICANTE	OBSERVAÇÃO
PISO	1	Porcelanato Polido	82 X 62	Champagne	879373	Elizabeth	Junta de 2 mm
	2	Cerâmica -Pocelanato	60x120cm	Branco	759303	Portinari	
	3	Porcelanato	59x118,2cm	Branco e cinza	979742	Eliane	
	4	Porcelanato	61,8x61,8cm	Cinza	P82083	Artens	Combina com o Rejunte 90423942
	5	Porcelanato	83x83	Branco	966907	Embramaco	
PAREDE	1	Tinta acrílica		Cromio	3109 10 10	Suvinil	Aplica em paredes acabadas.
	2	Revestimento Esmaltado	10x20cm	cinza	232595	Portobello	Rejunte branco. Junta de 4mm
	3	Revestimento borda reta	10x20cm	Preto	788650	Portobello	Rejunte branco
	4	Revestimento borda reta	33x100cm	cinza	739988	Portinari	Rejunte Cinza
	5	Cerâmica	43x43	branco	101010165	Ceral	Marmorizado, Brilhante, PEI 4
	6	Porcelanato	83x83	Branco	866907	Embramaco	Rejunte Cinza
	7	Porcelanato	92x92	branco	970745	Villagres	
RODAPÉ	1	Porcelanato Polido	10x62	Champagne	879373	Elizabeth	Juntas de encaixe cortado em 45°
	2	Cerâmica -Pocelanato	10x120cm	Branco	759303	Portinari	Juntas de encaixe cortado em 45°
	3	Porcelanato	10x61,8cm	Cinza	P82083	Artens	Combina com o Rejunte 90423942
FORRO	1	Sancra.	A definir	branco	A definir	A definir.	Consultar um especialista
	2	Teto-Rodapé	14x60	branco	AMB	xps2sa75	Consultar um especialista
	3	Sancra.	2.55X1.55	branco	A definir	A definir.	Consultar um especialista
	4	Sancra.	1.93x2.10	branco	A definir	A definir.	Consultar um especialista
	5	Sancra.	2.99X3.83	branco	A definir	A definir.	Consultar um especialista
	6	Sancra.	3.94X2.65	branco	A definir	A definir.	Consultar um especialista


	INSTITUTO FEDERAL DE EDUCAÇÃO, CIÊNCIA E TECNOLOGIA			
	DISCIPLINA	DESENHO DE CONSTRUÇÃO CIVIL	PROFESSORES	ANTONIO DEZOTTI FILHO
	DESENHO	DETALHES E TABELAS	ESCALA	1:20 DATA 16 / 06 / 2022
VISTO	NOME	PRONTUÁRIO	FOLHA	
	GUSTAVO R. SILVESTRE DA SILVA	SP3068412	04/04	

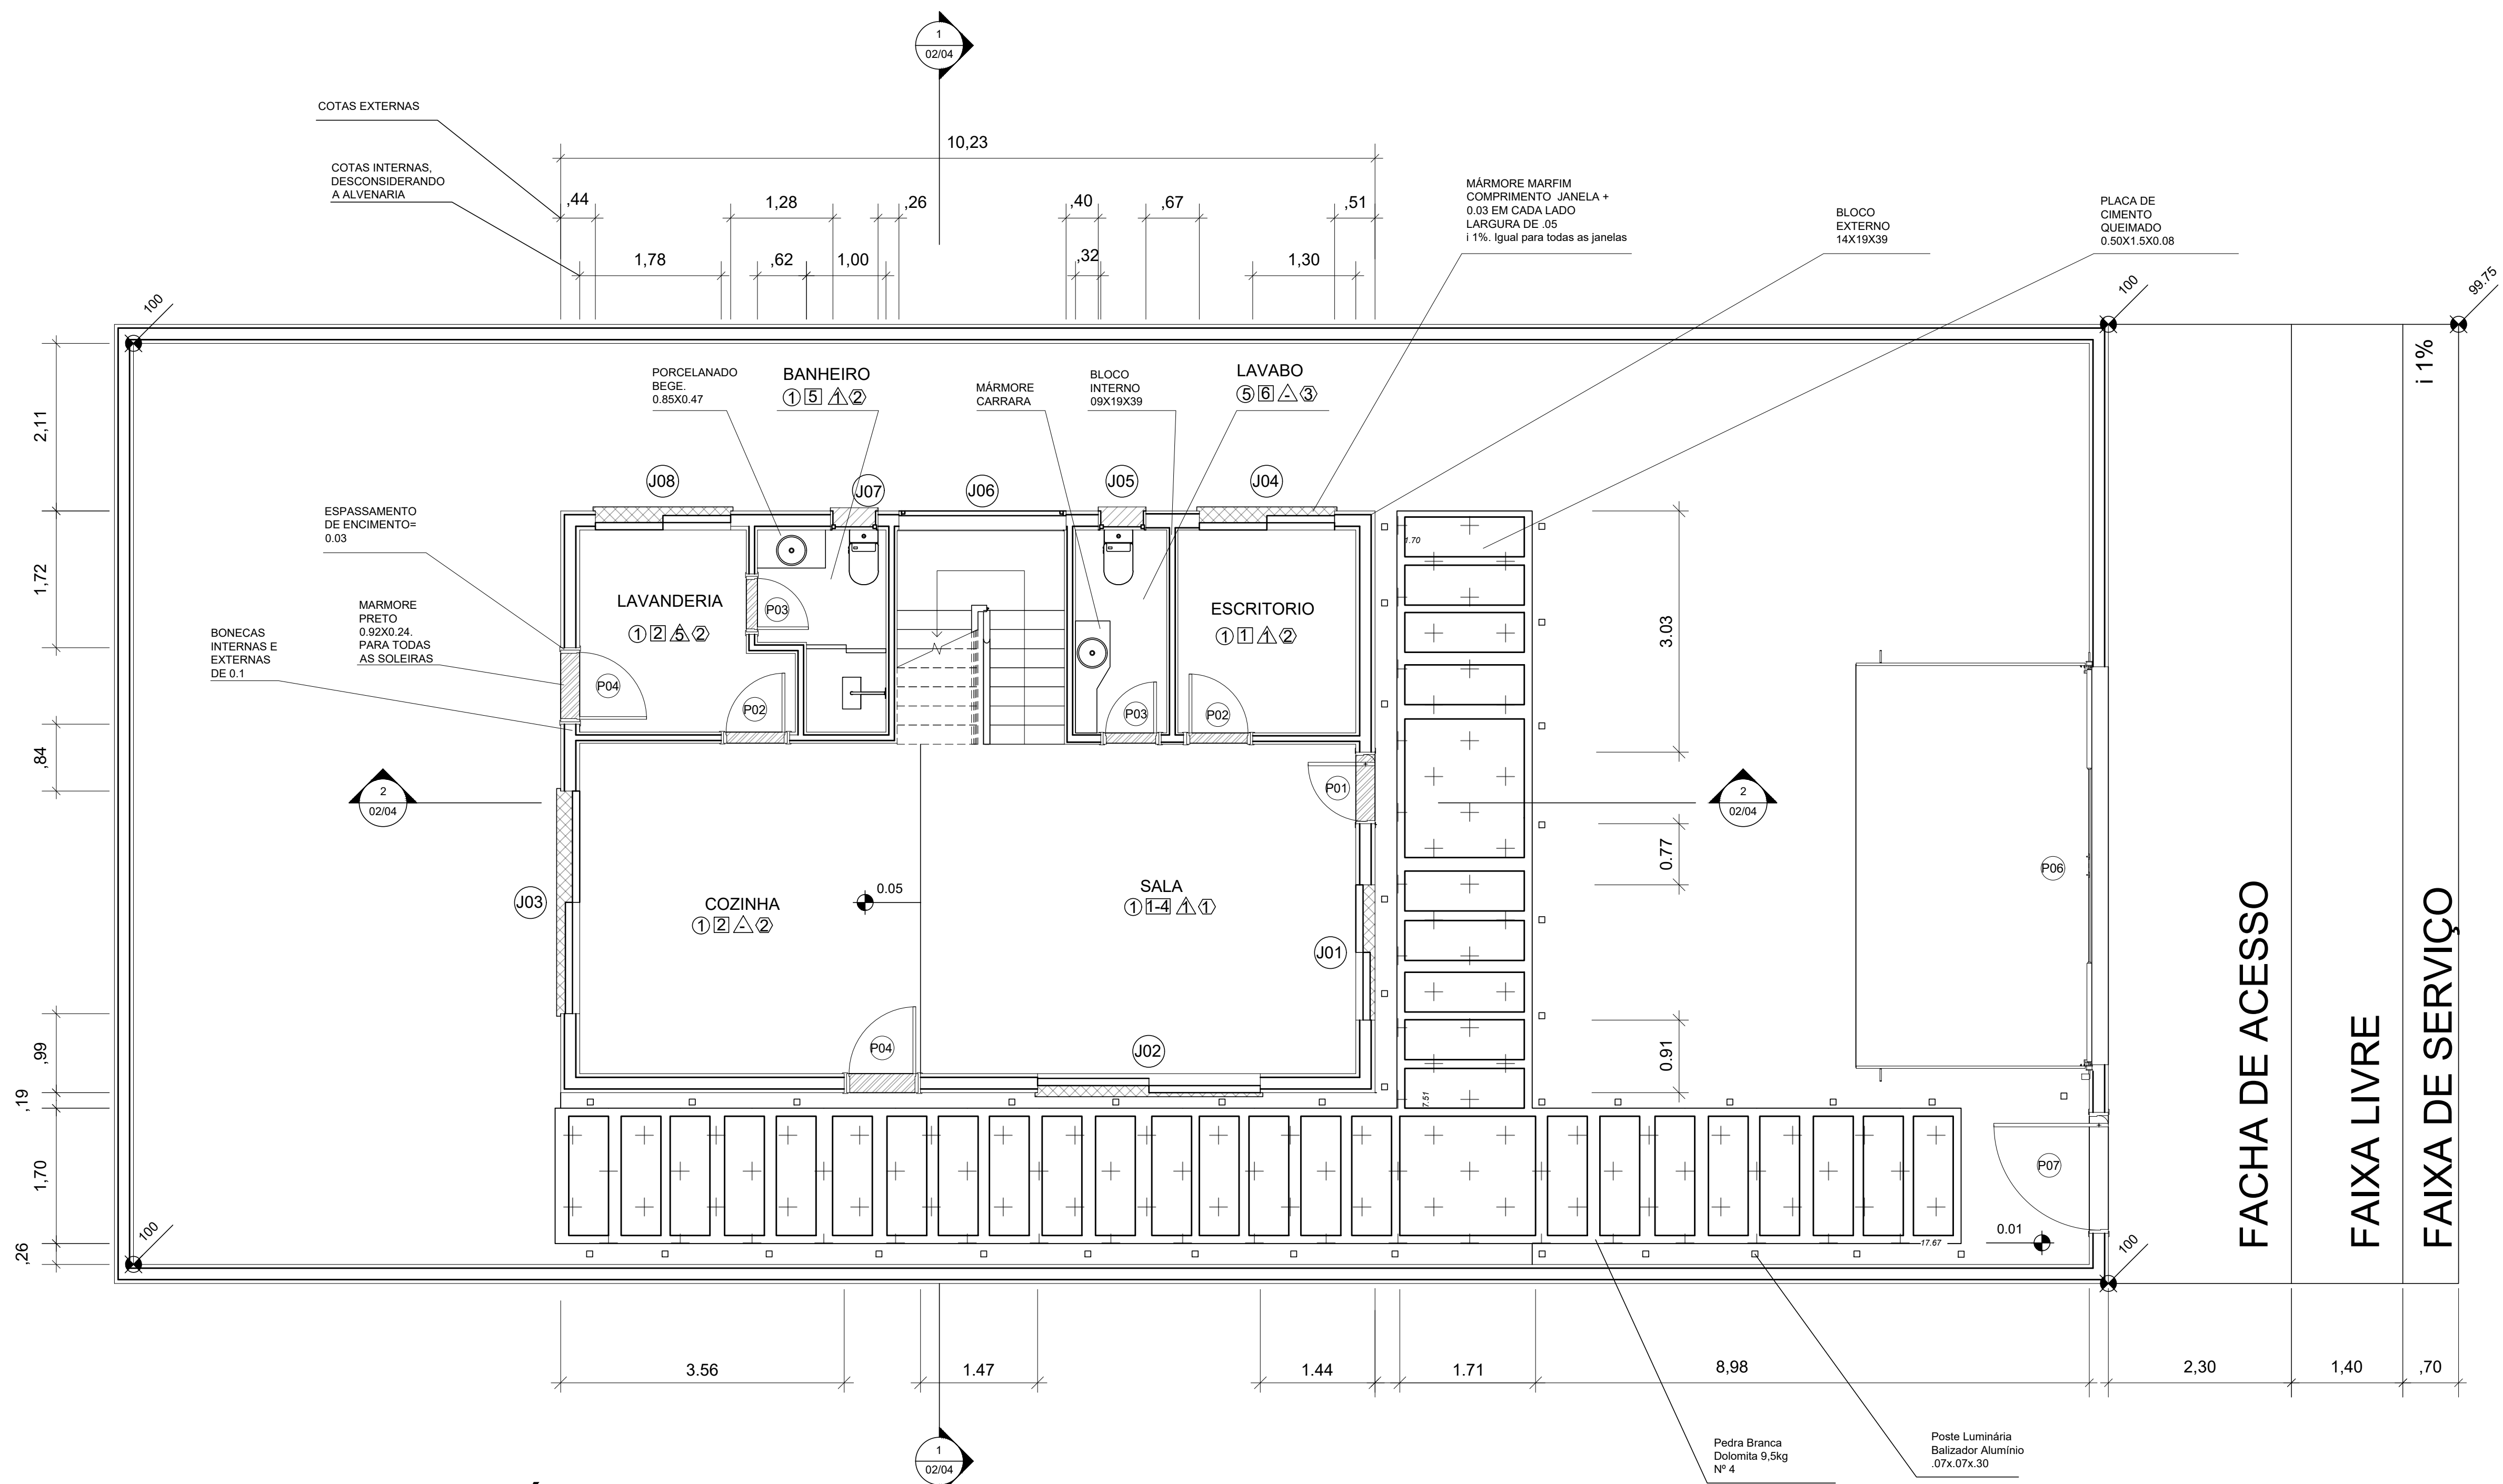

1 PLANTA PAV. TÉRREO
ESCALA: 1:50

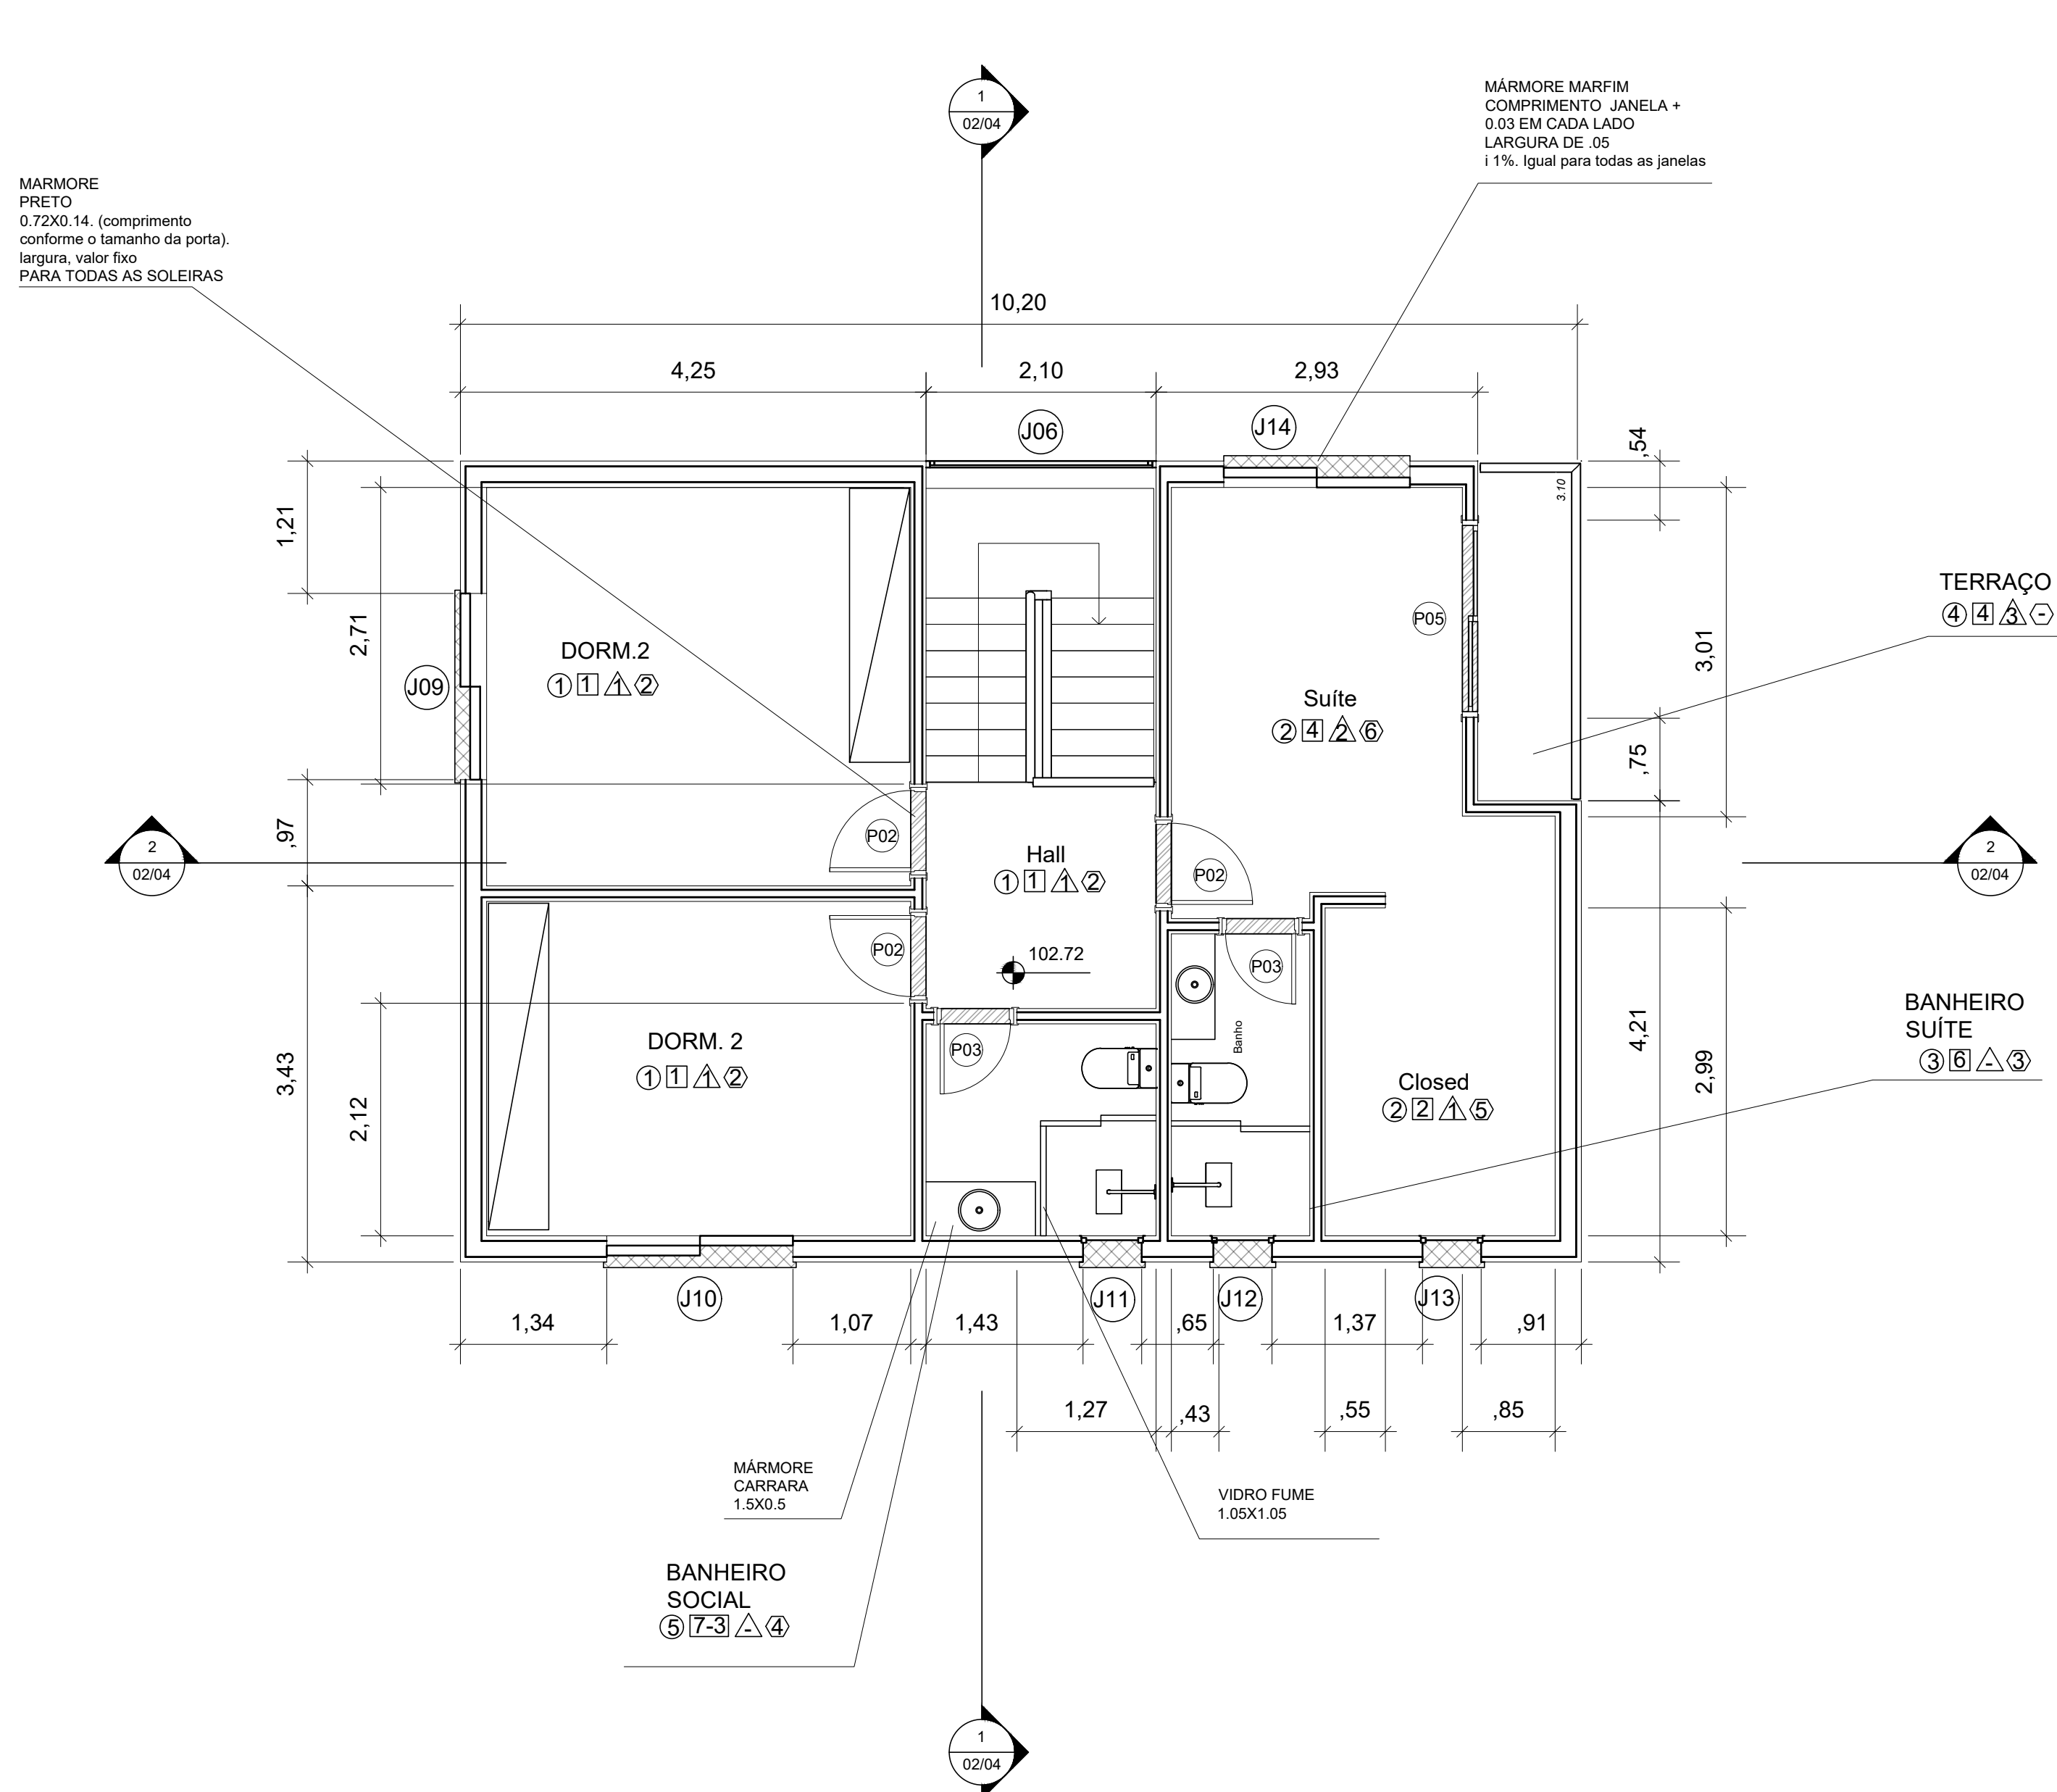

2 PLANTA PAV. SUPERIOR
ESCALA: 1:50

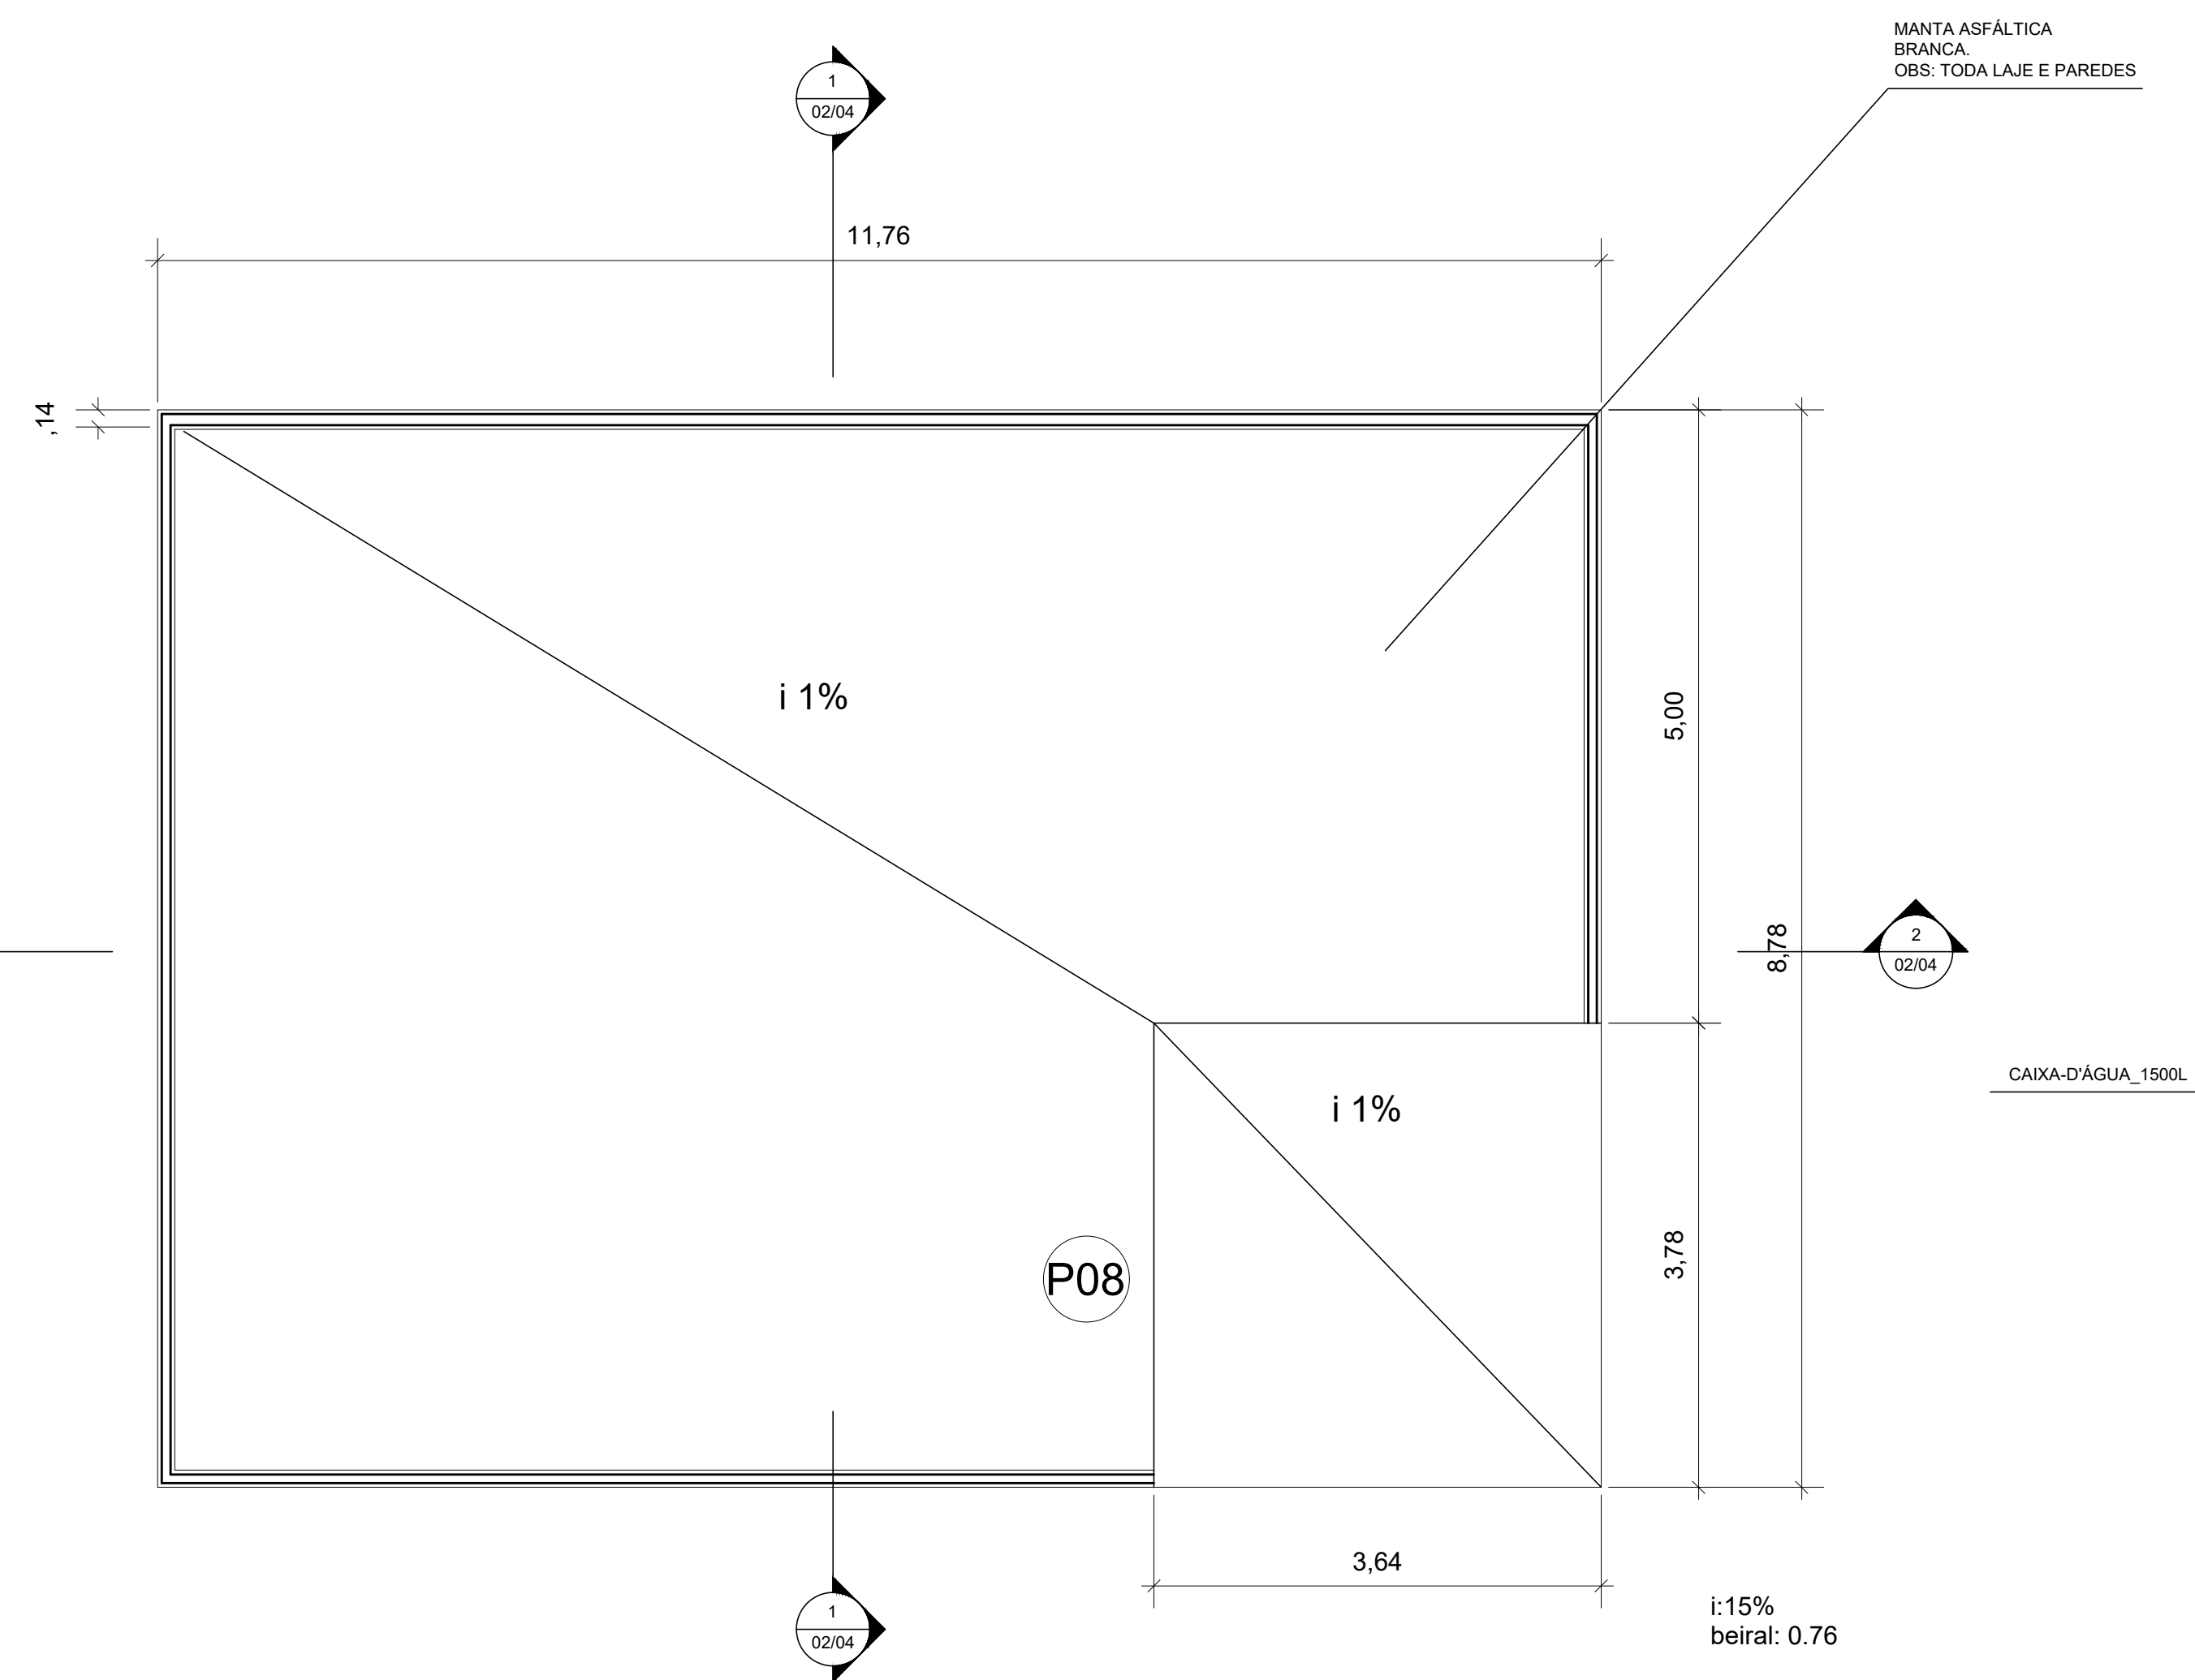

3 PLANTA - COBERTURA
ESCALA: 1:50