




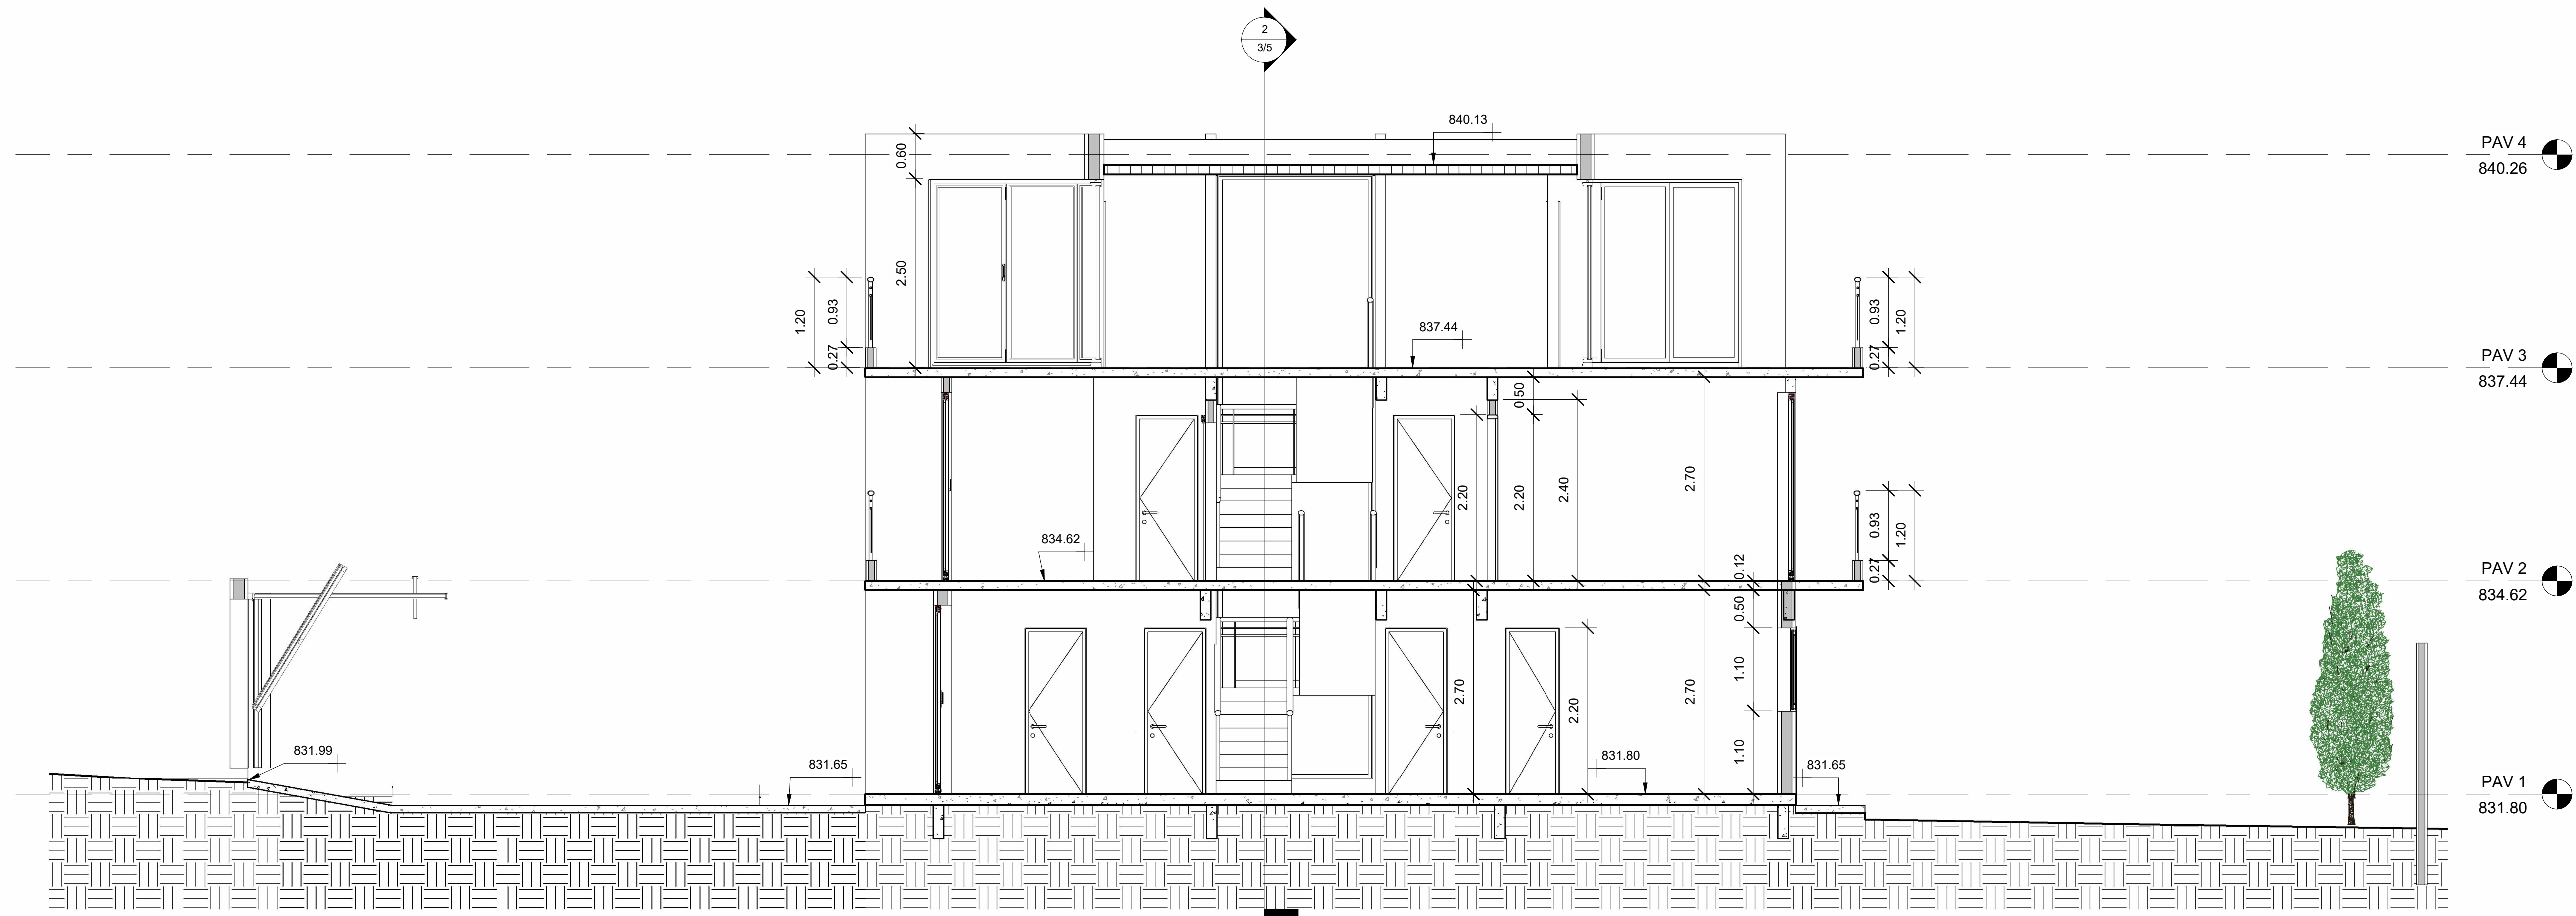


1 CORTE LONGITUDINAL
1 : 50

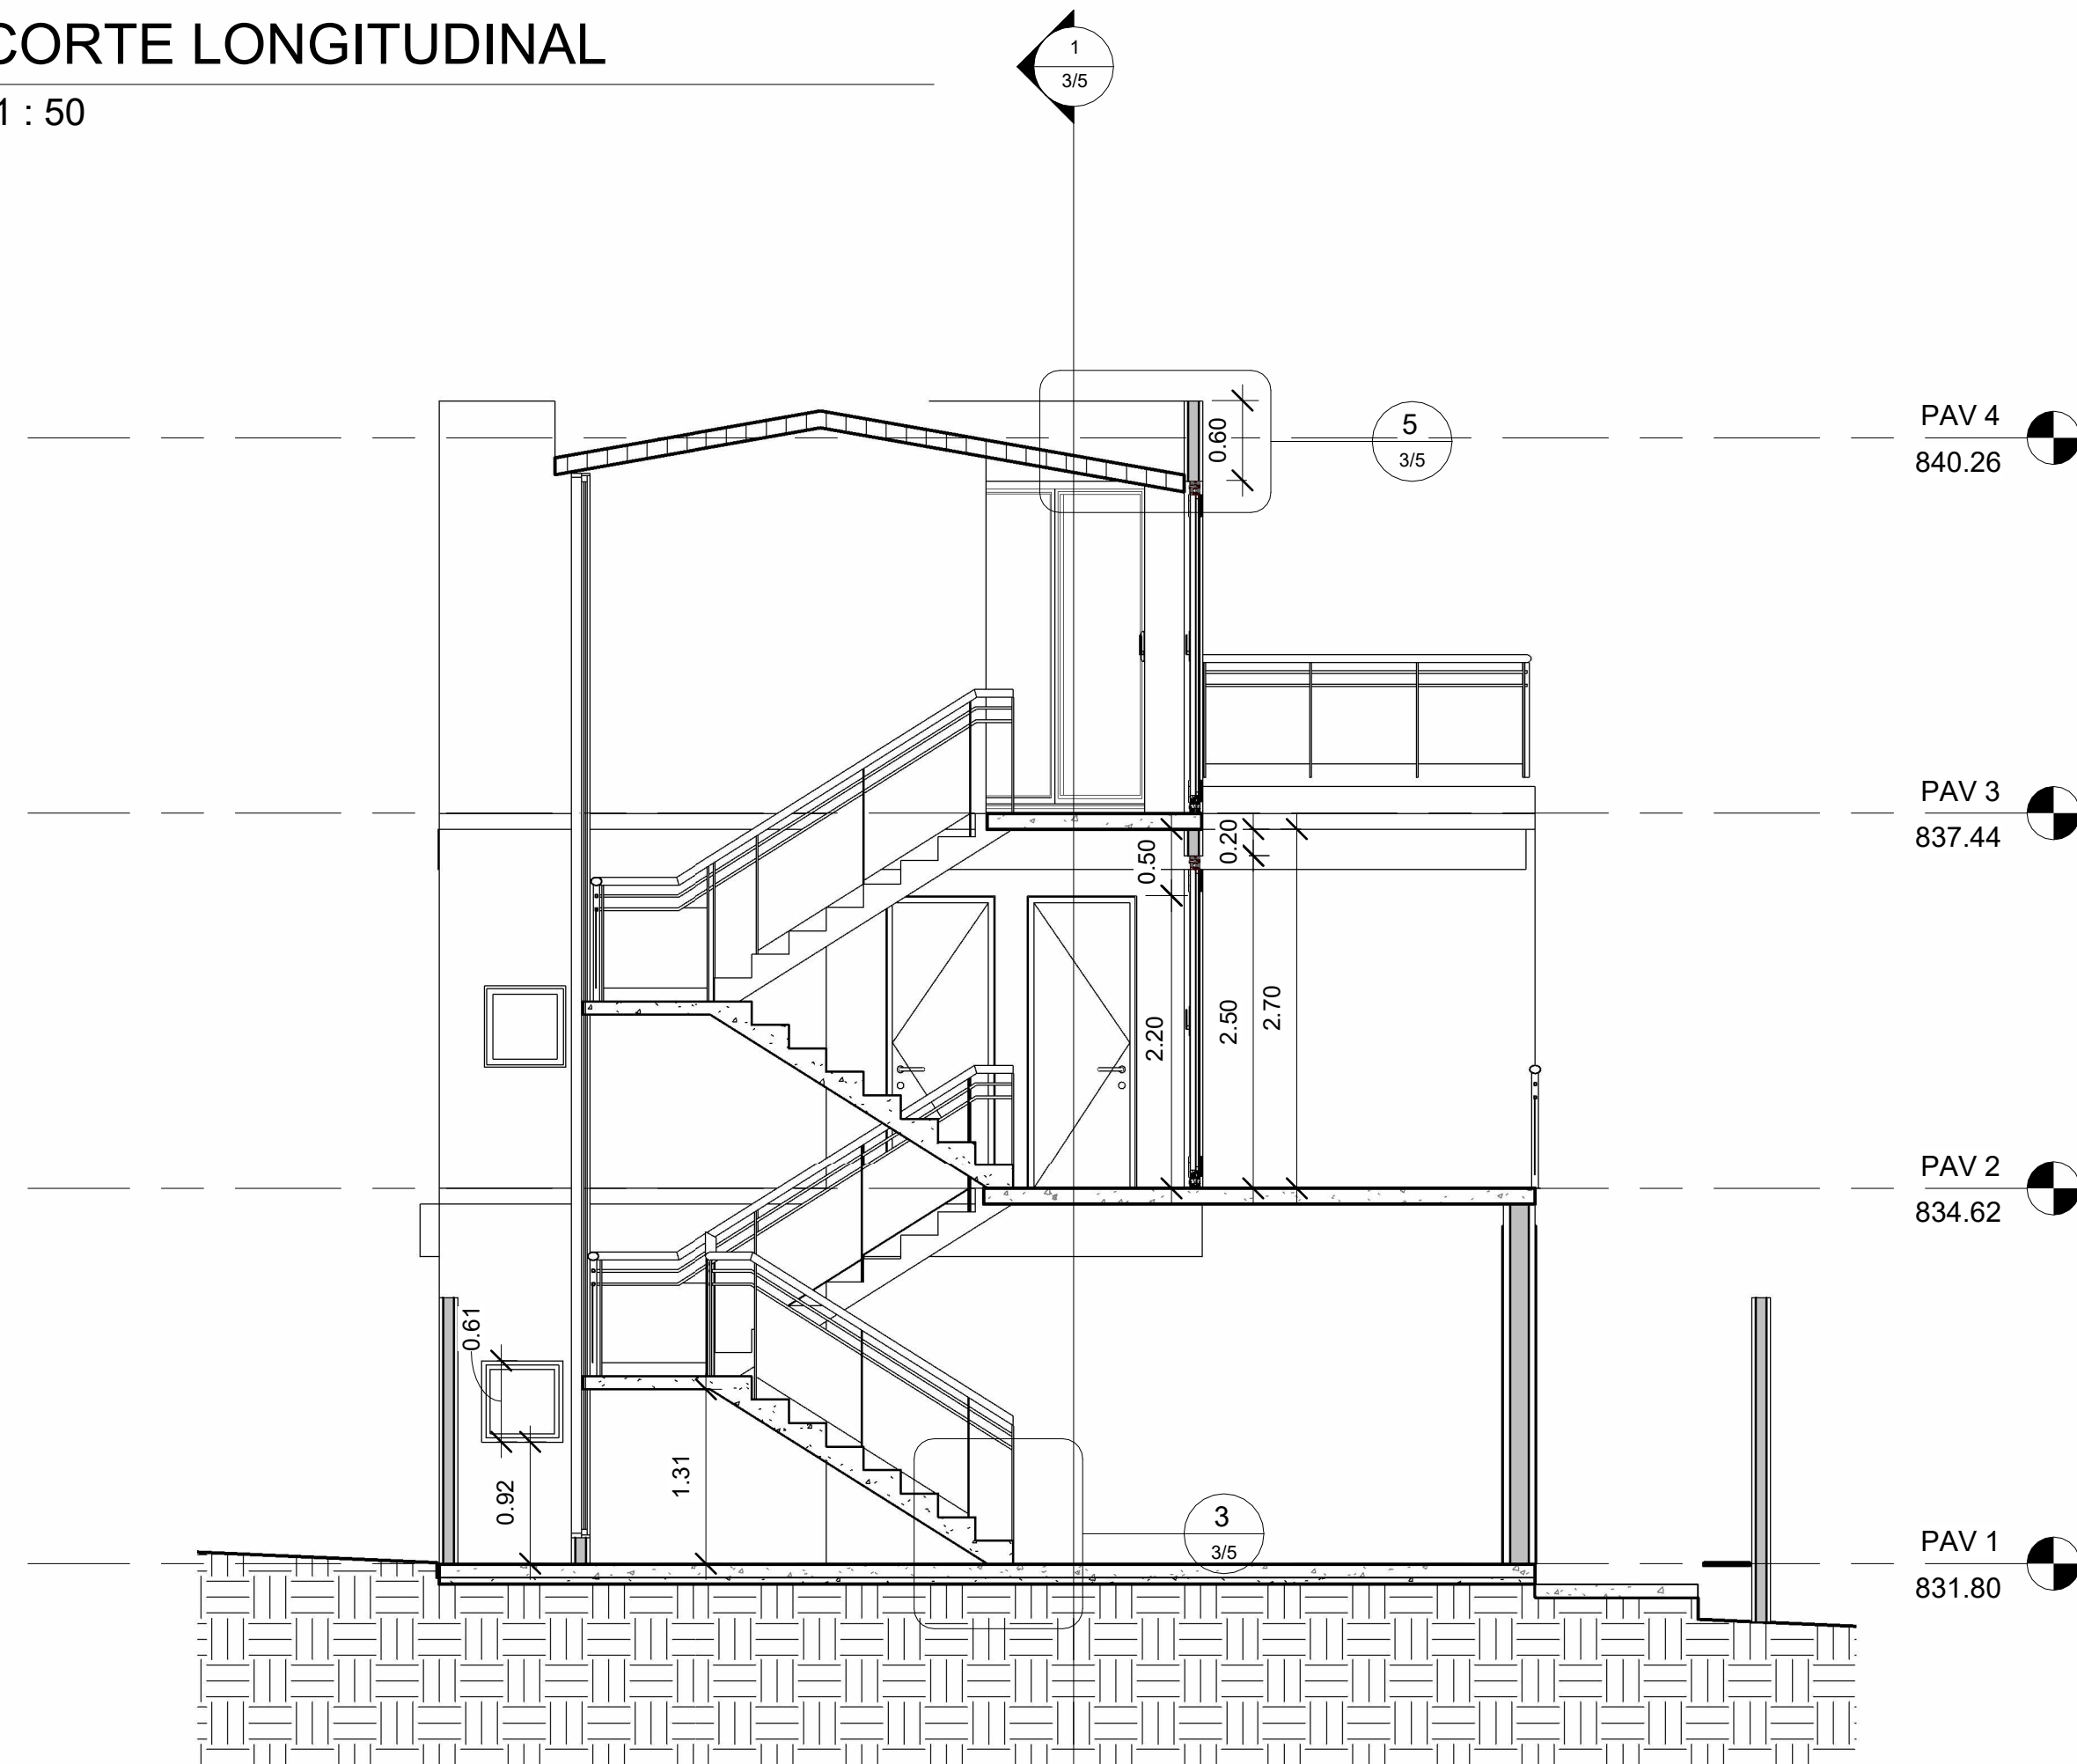


2 CORTE TRANSVERSAL
1 : 50

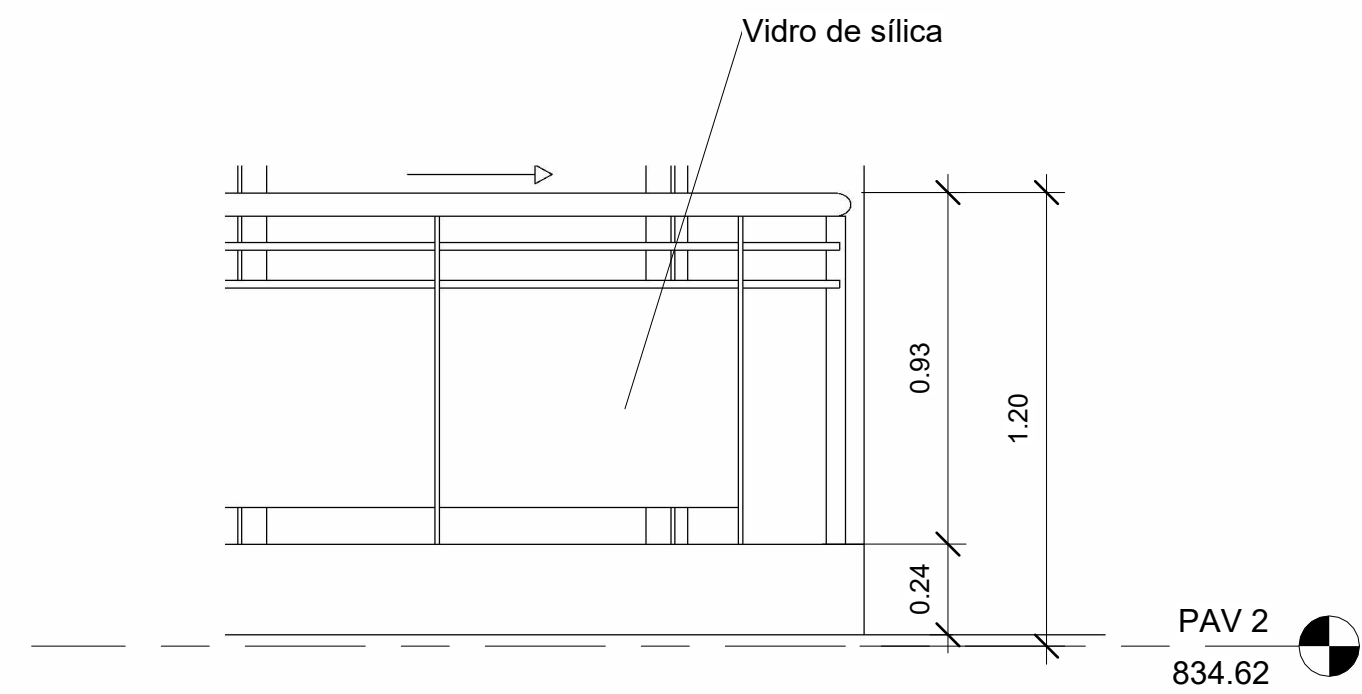

4 DETALHE - GUARDA
CORPO
1 : 20

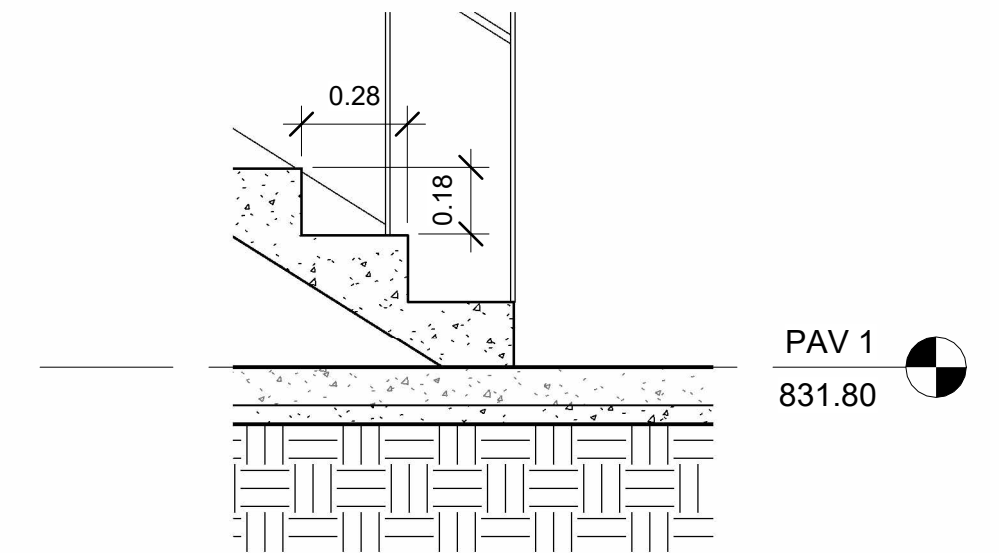

3 DETALHE - ESCADA
1 : 20

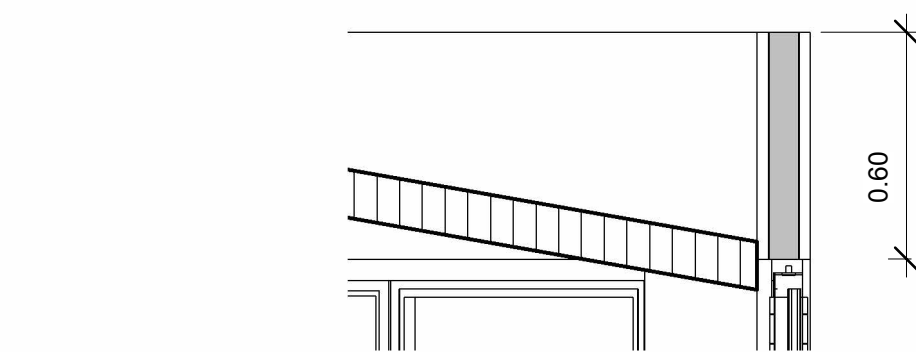

5 DETALHE - COBERTURA
1 : 20