




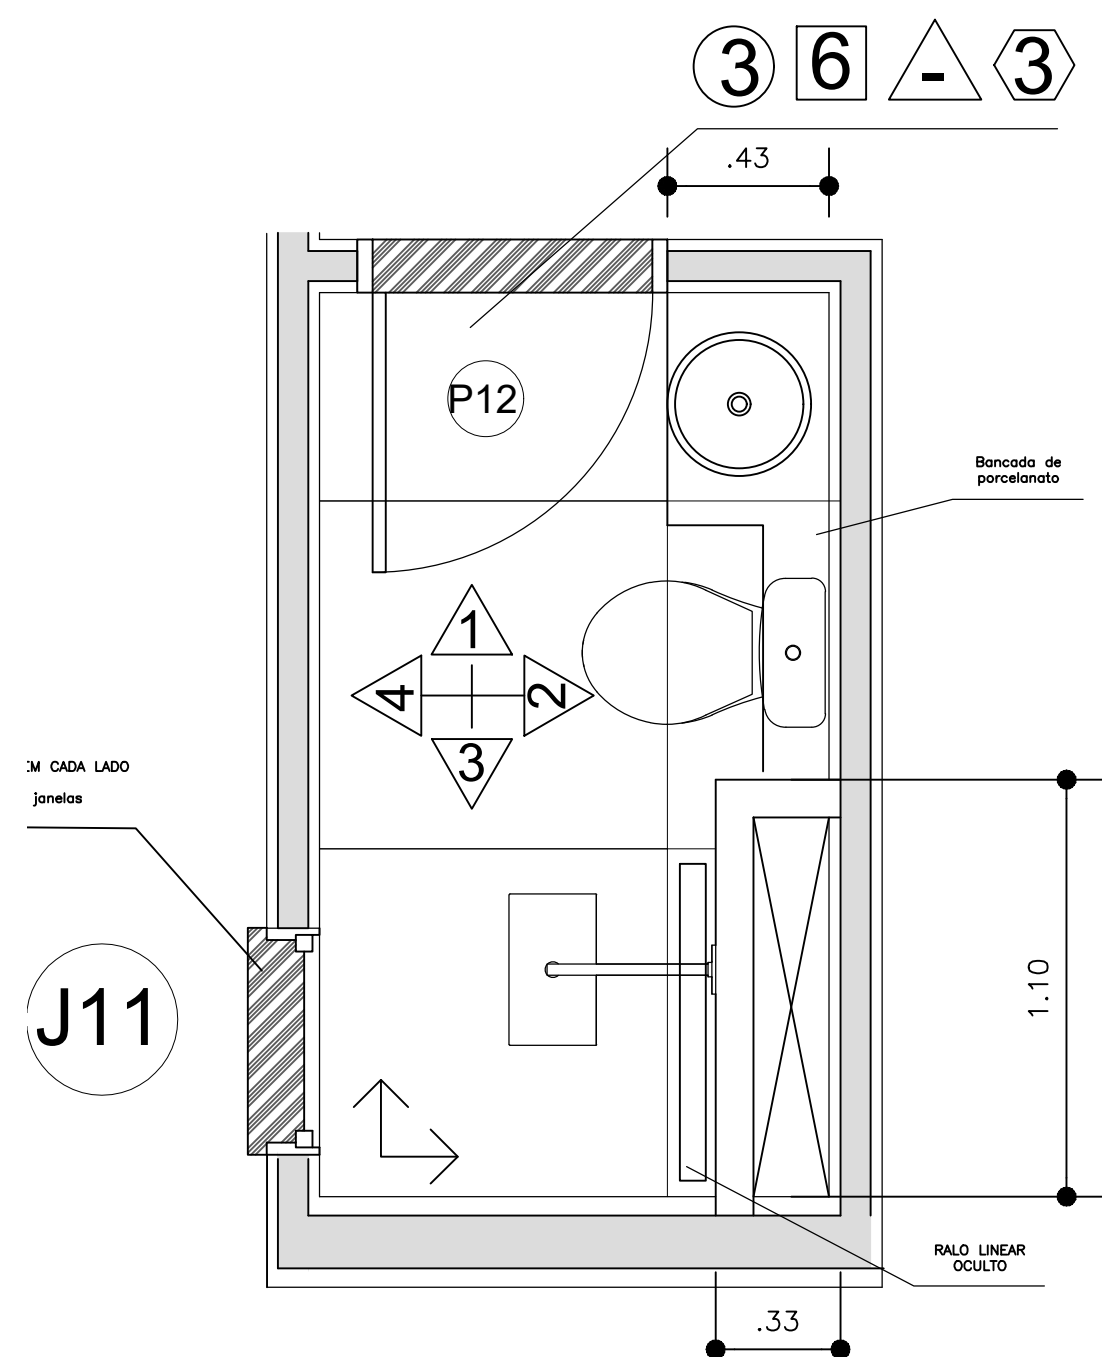


1 BANHEIRO DA SUÍTE
ESCALA: 1:20

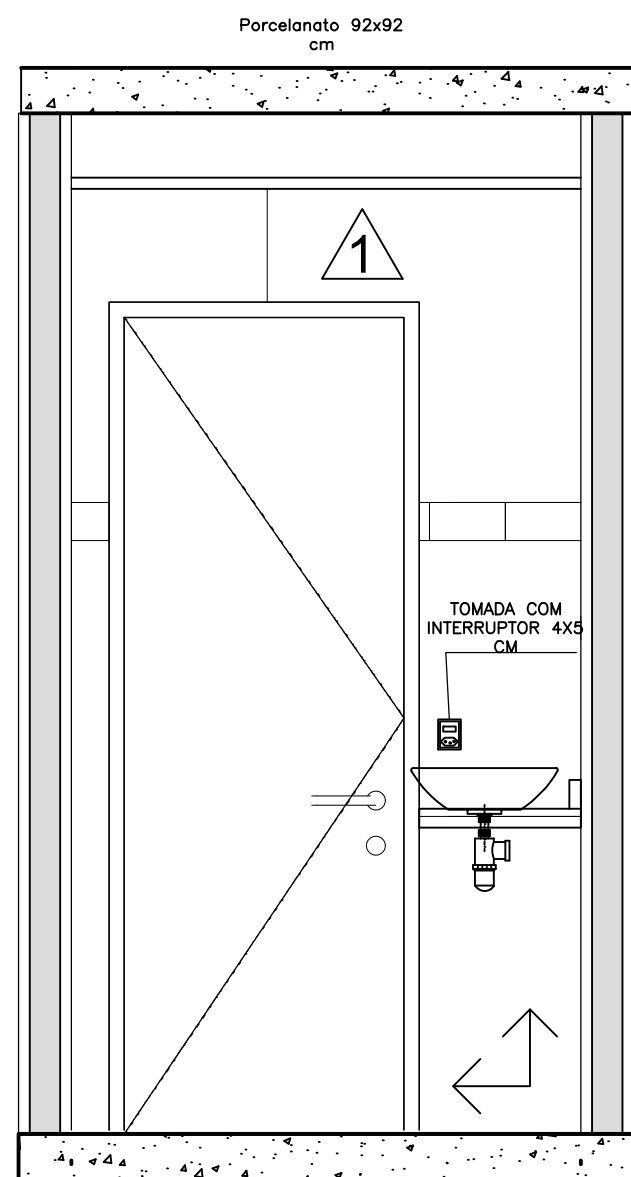


2 ELEVÇÃO 1
ESCALA: 1:20

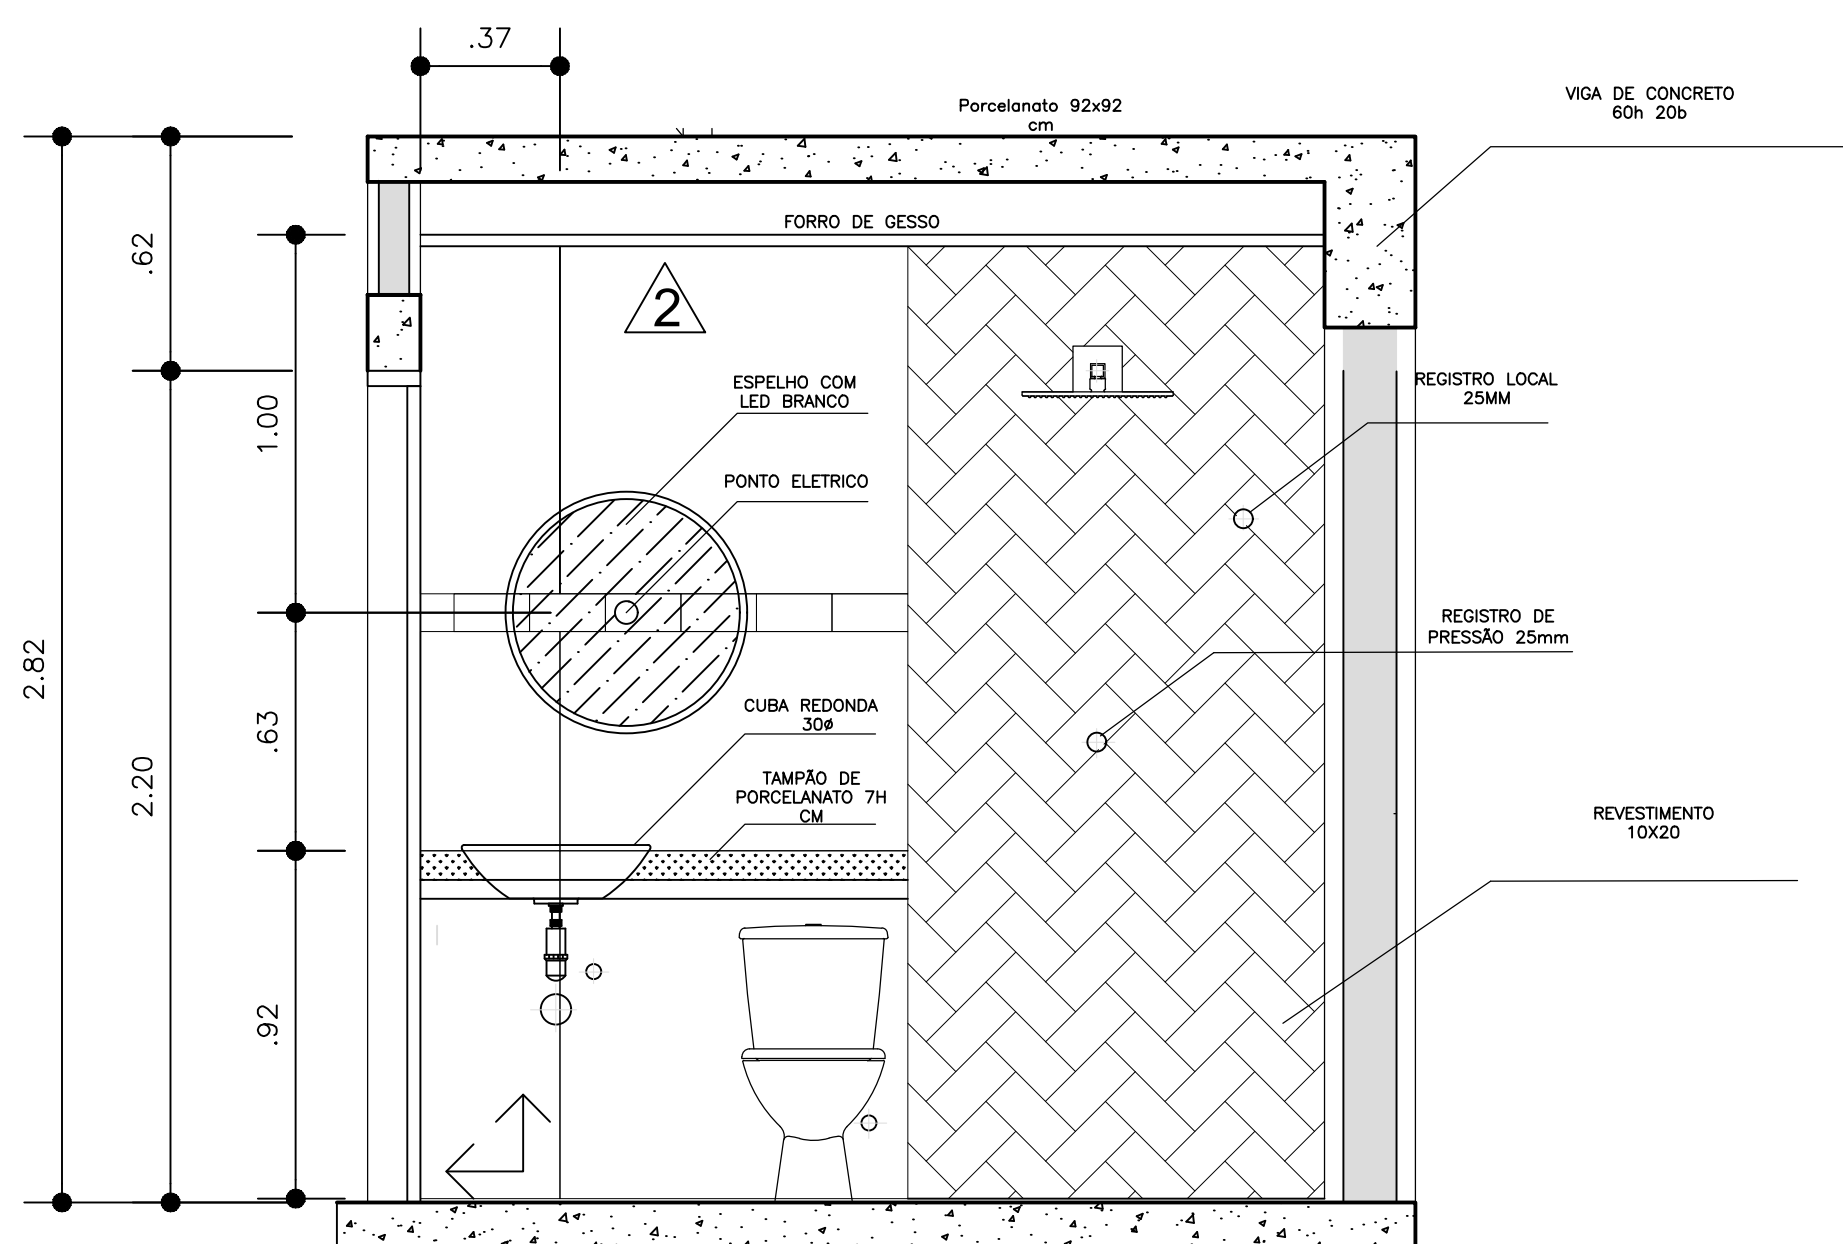


3 ELEVÇÃO 2
ESCALA: 1:20

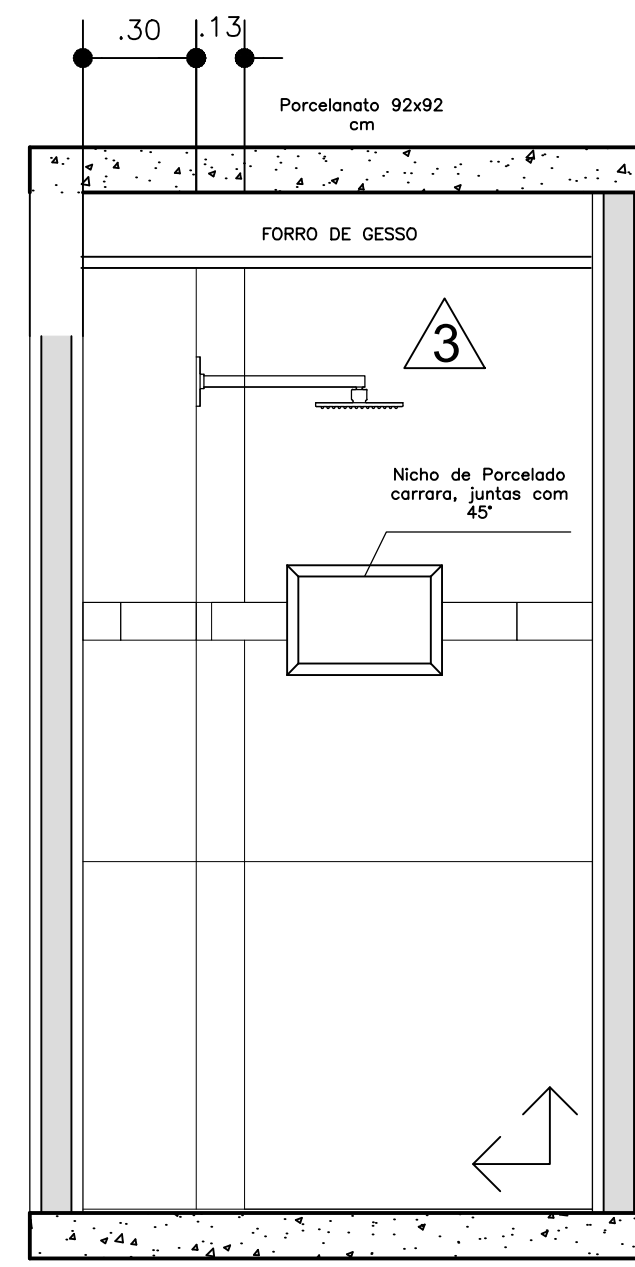


4 ELEVÇÃO 3
ESCALA: 1:20

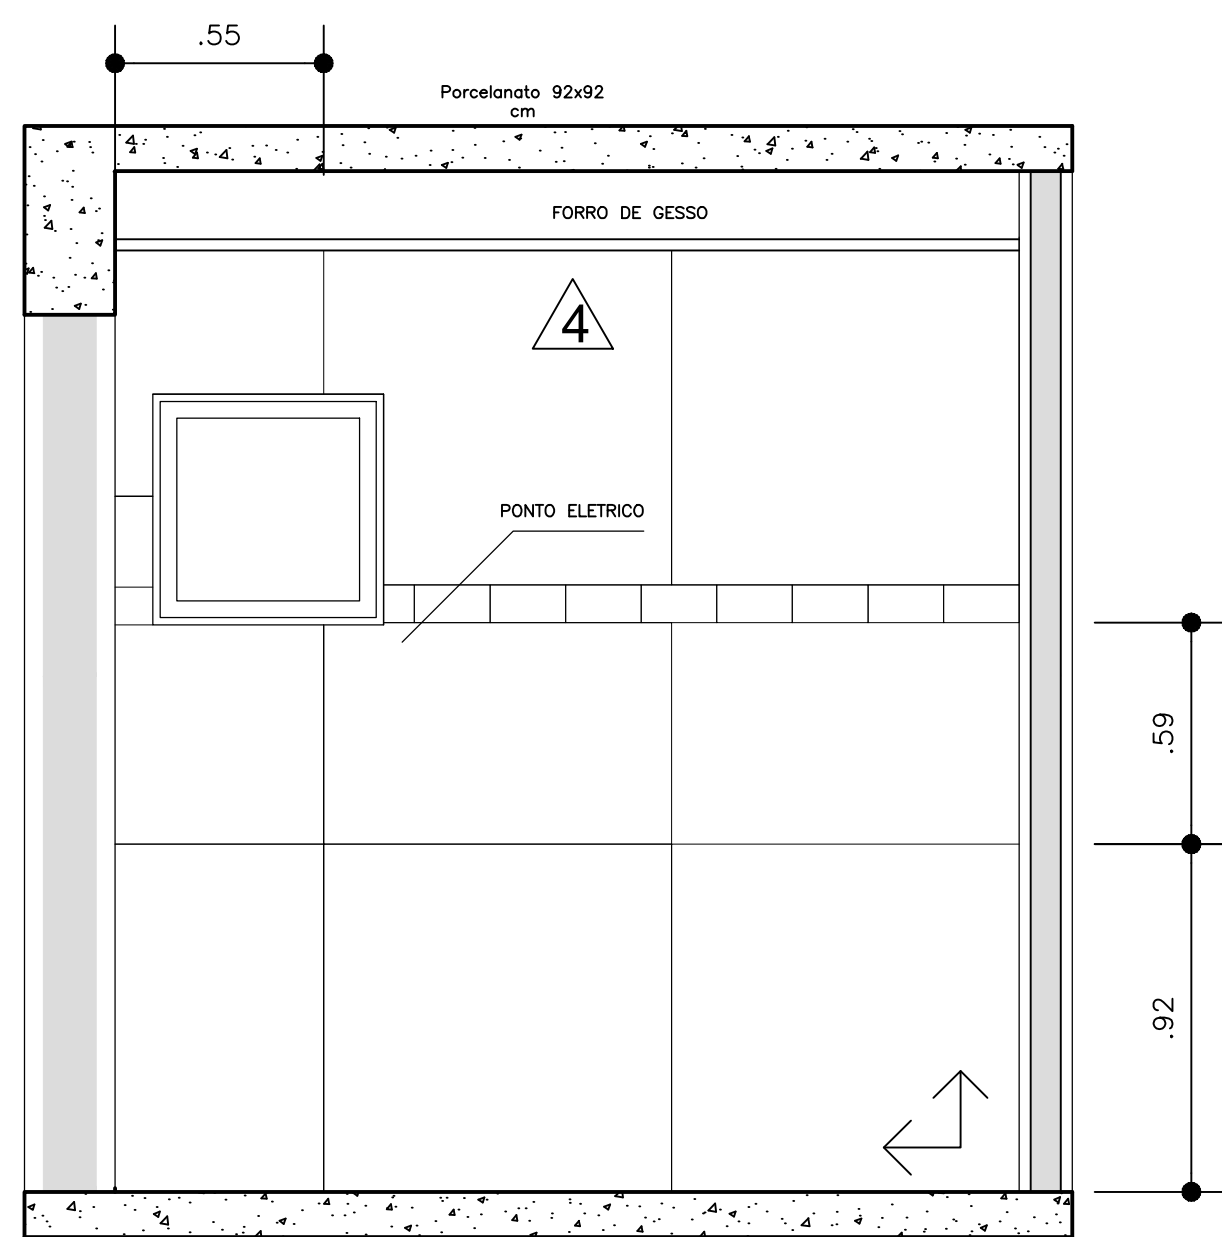

1 ELEVÇÃO 4
ESCALA: 1:50

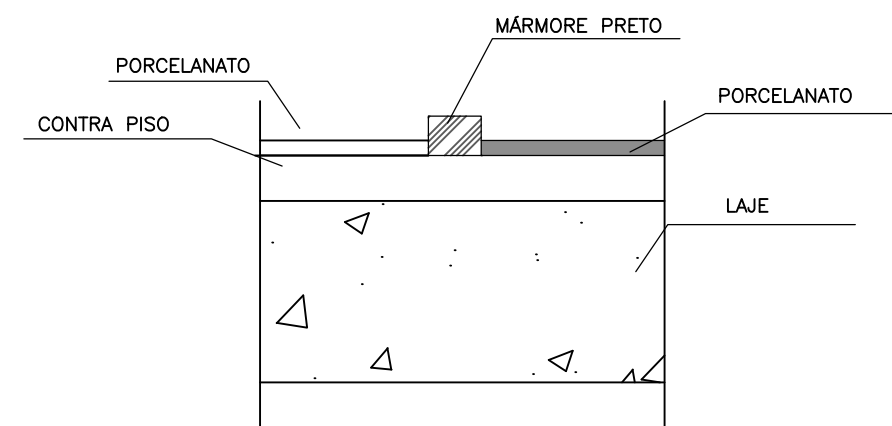

2 ELEVÇÃO 1
ESCALA: 1:20

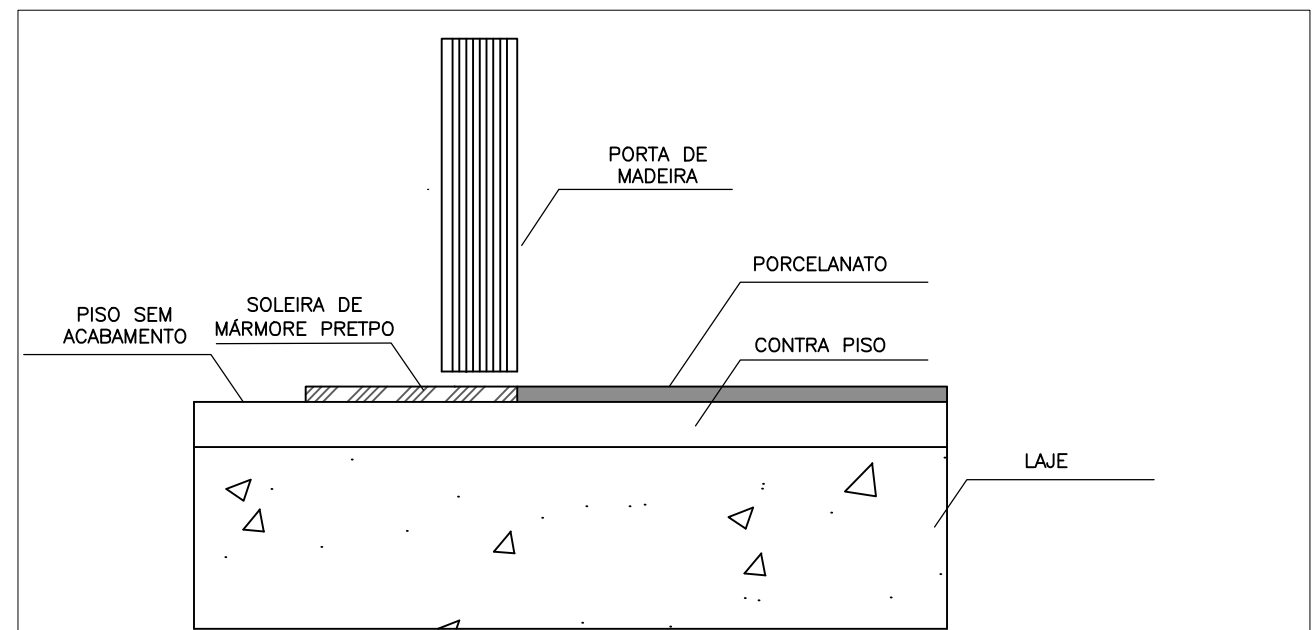

2 ELEVÇÃO 1
ESCALA: 1:20

Tabelas de Metais e louças

Tipo	Marca	Material	Largura bruta	Altura bruta	Quantidade
Culpa	Deca	vidro	0.3	0.30	1
Torneira	Torneira	Aço	0,25	0.20	1
Ralo	Pingo Casa	Inox	0,10	1	1
Registro de Pressao	Registro de Pressao	Aço	0,025Ø	0	1
Registro de Gaveta	Registro de Gaveta	Aço	0.025Ø	0	1
Bacia Sanitaria	Deca	Axis	0.68	0.78	1

Tabelas de Esquadrias - Portas

Marca de tipo	Material	Largura bruta	Altura bruta	Quantidade
P03	Madeira	0.72	2.2	4

Tabela de janela

Comentário s de tipos	Marca de tipo	Largura bruta	Altura bruta	Altura do peitoril	Material	Vidro	Modelo
Banh. Superior	J11	0.80	0.60	1.50	Alumínio	Vidro, fosco	MAXIM-AR

