

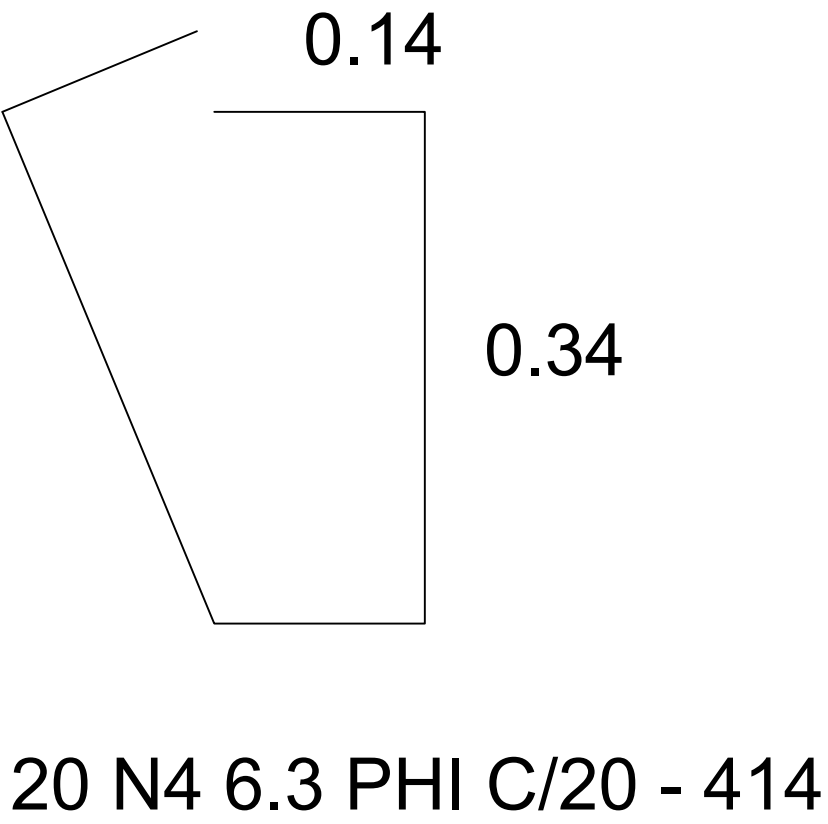
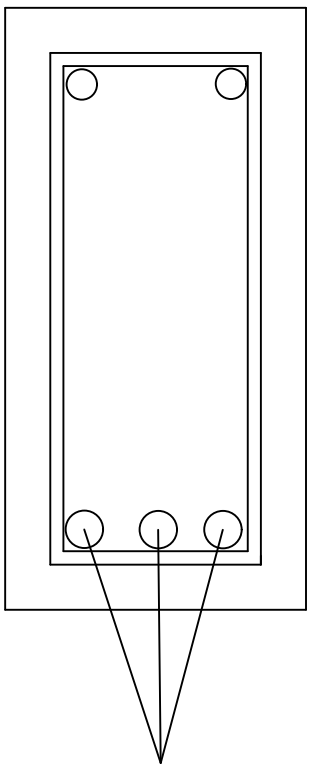
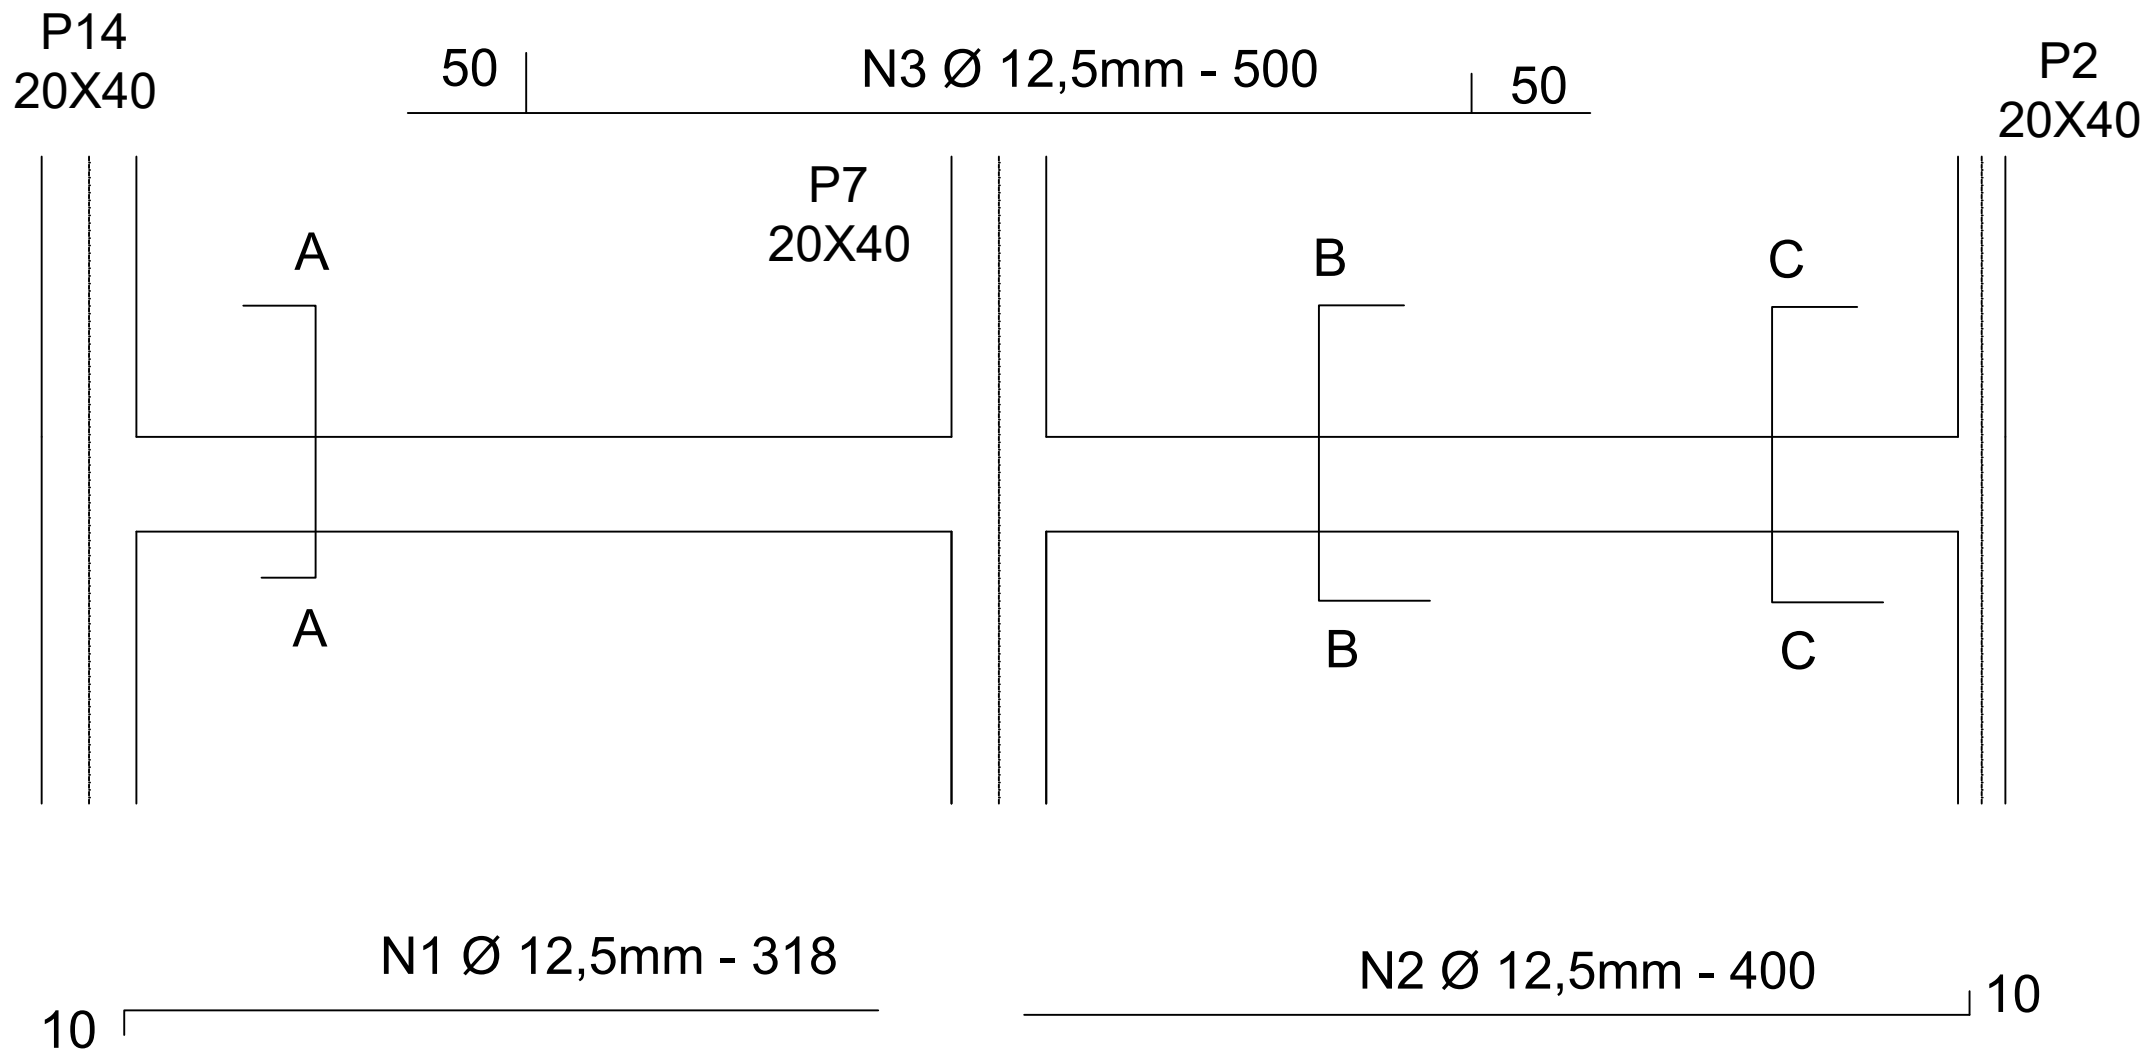
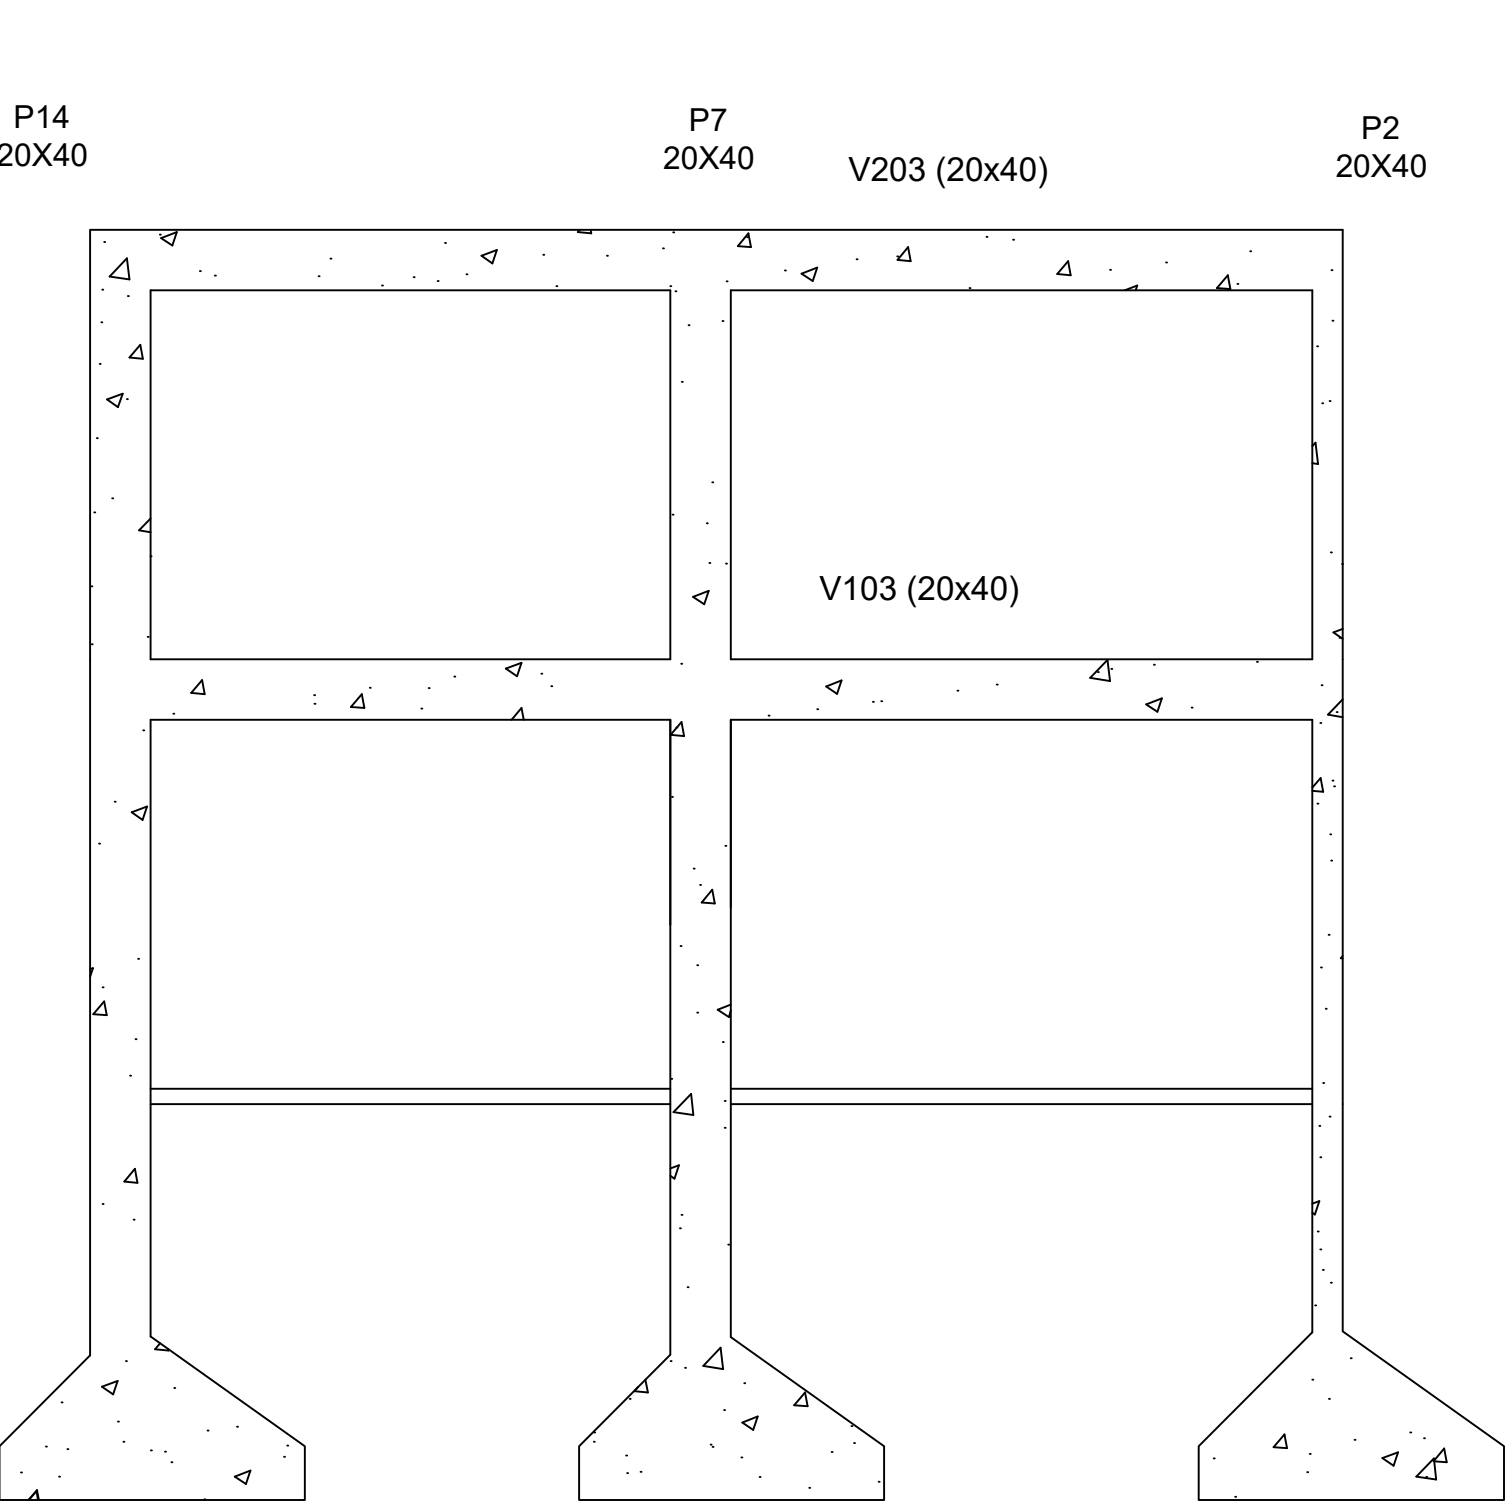
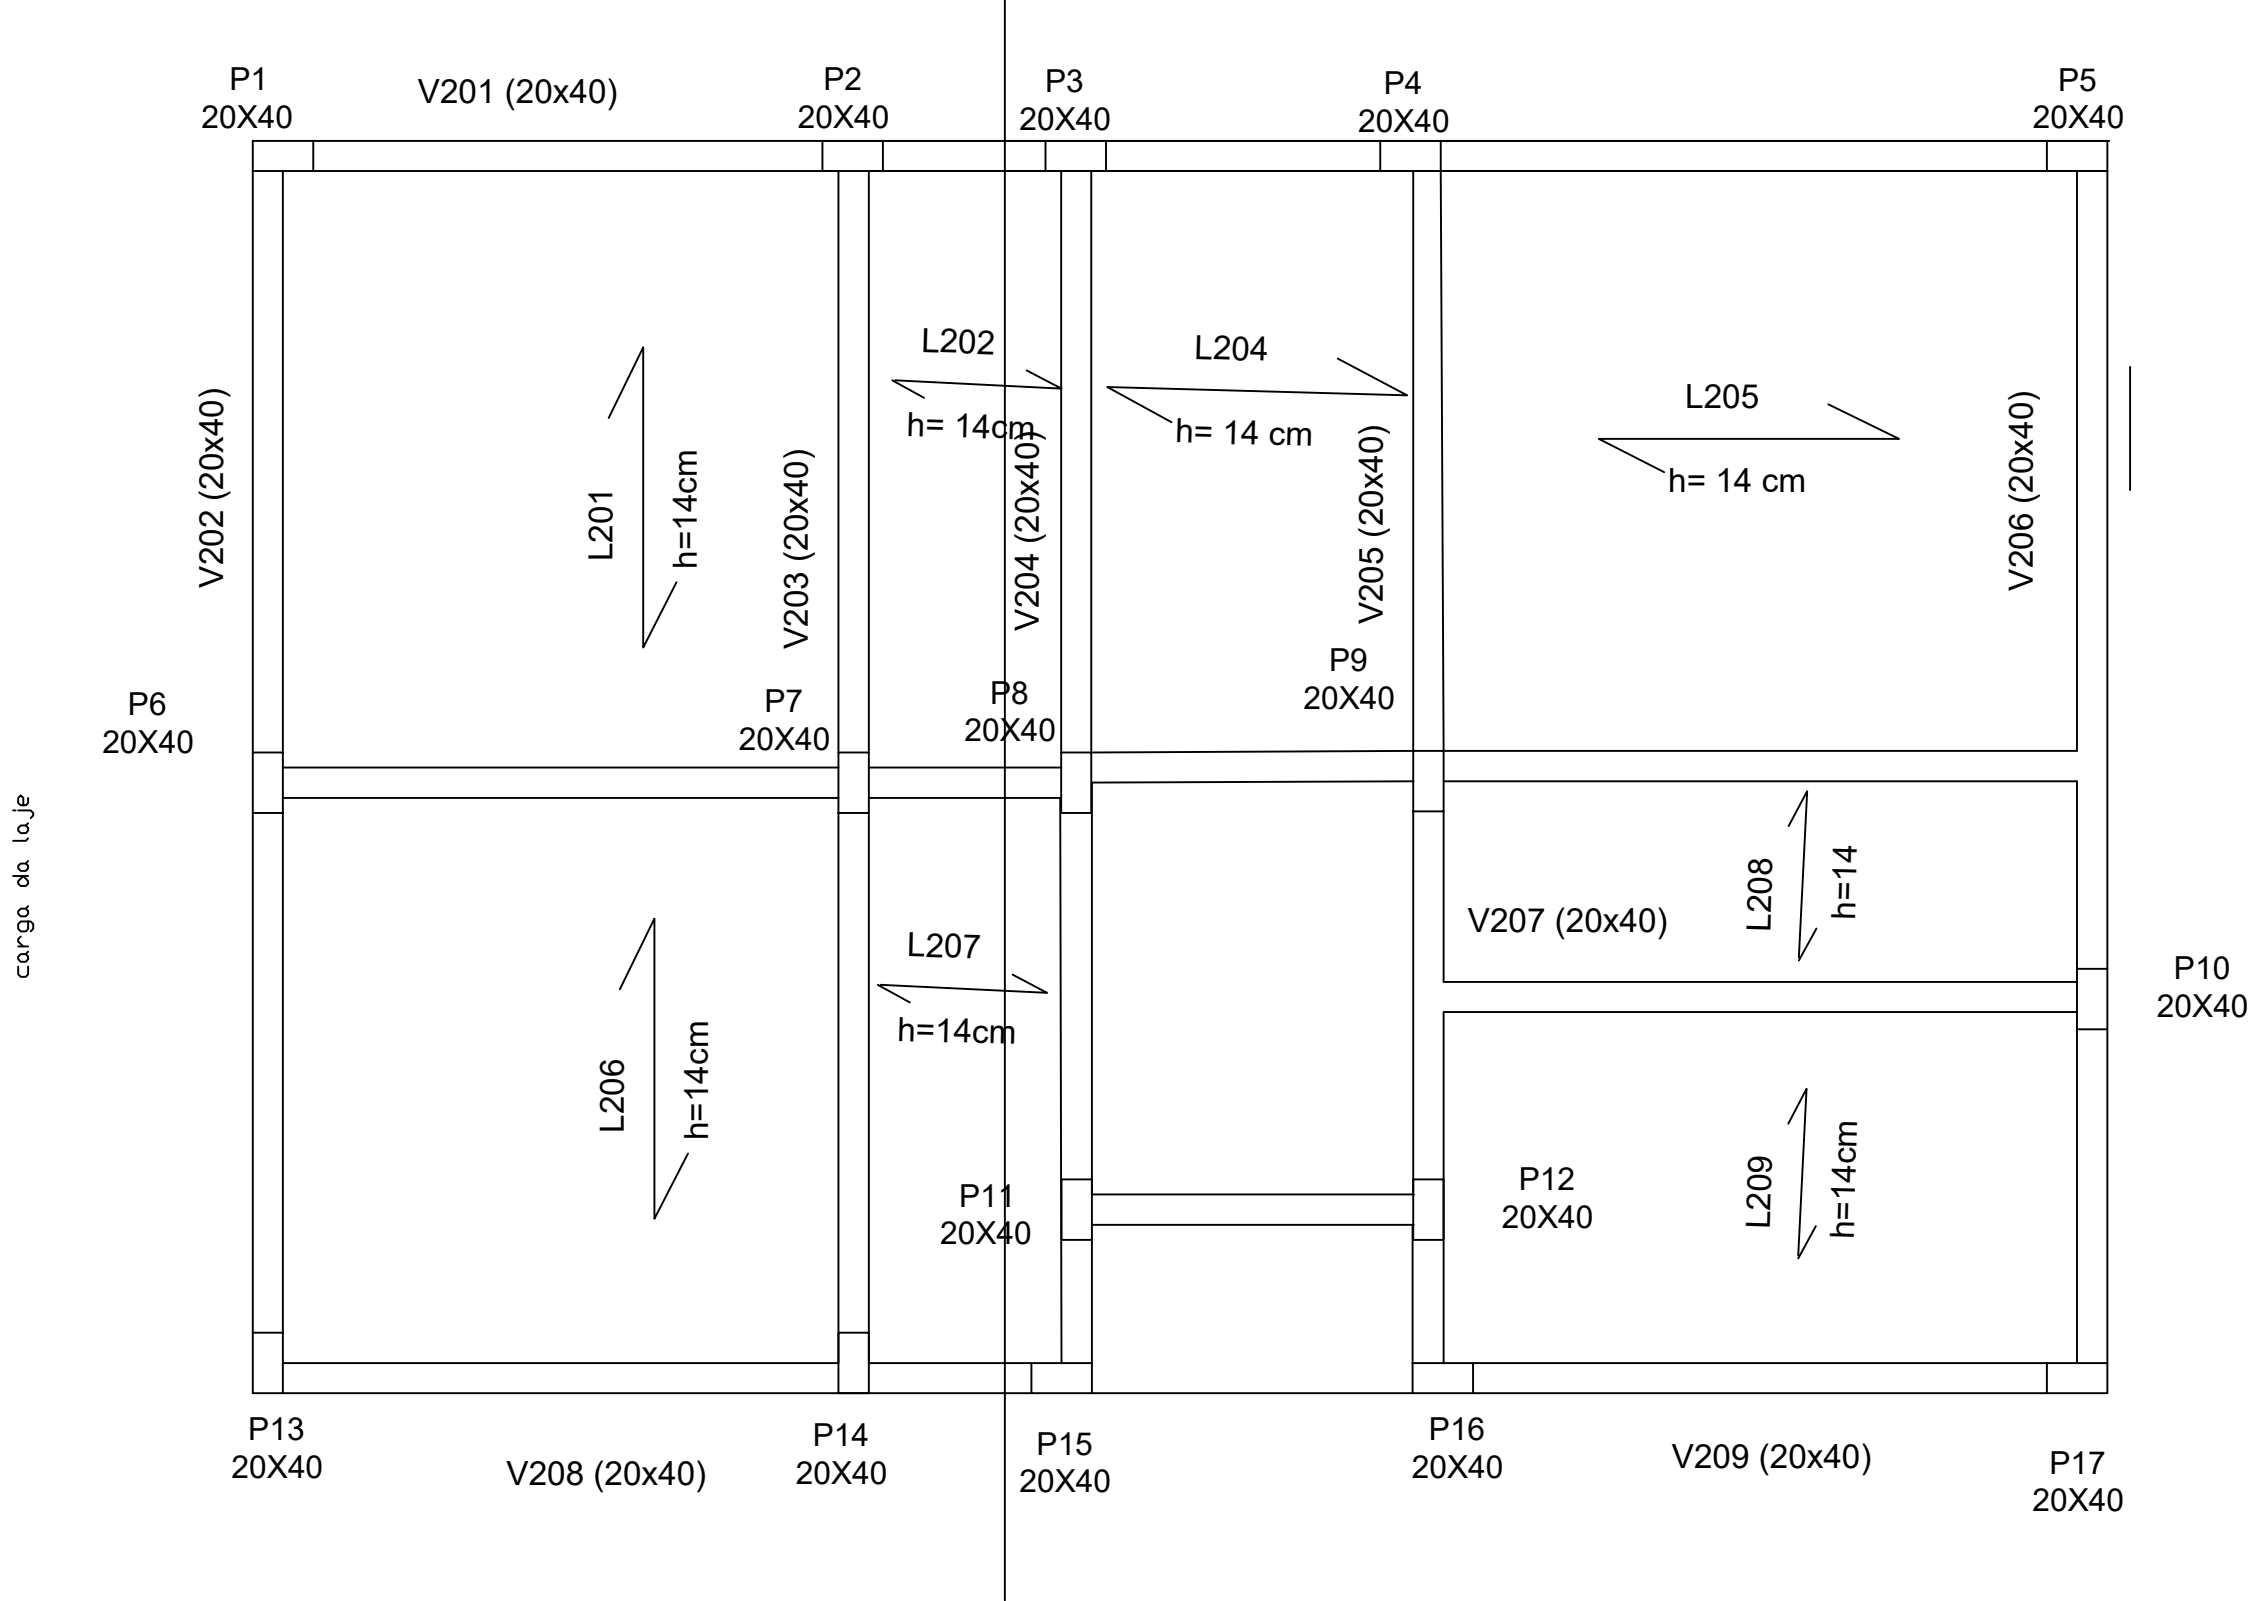
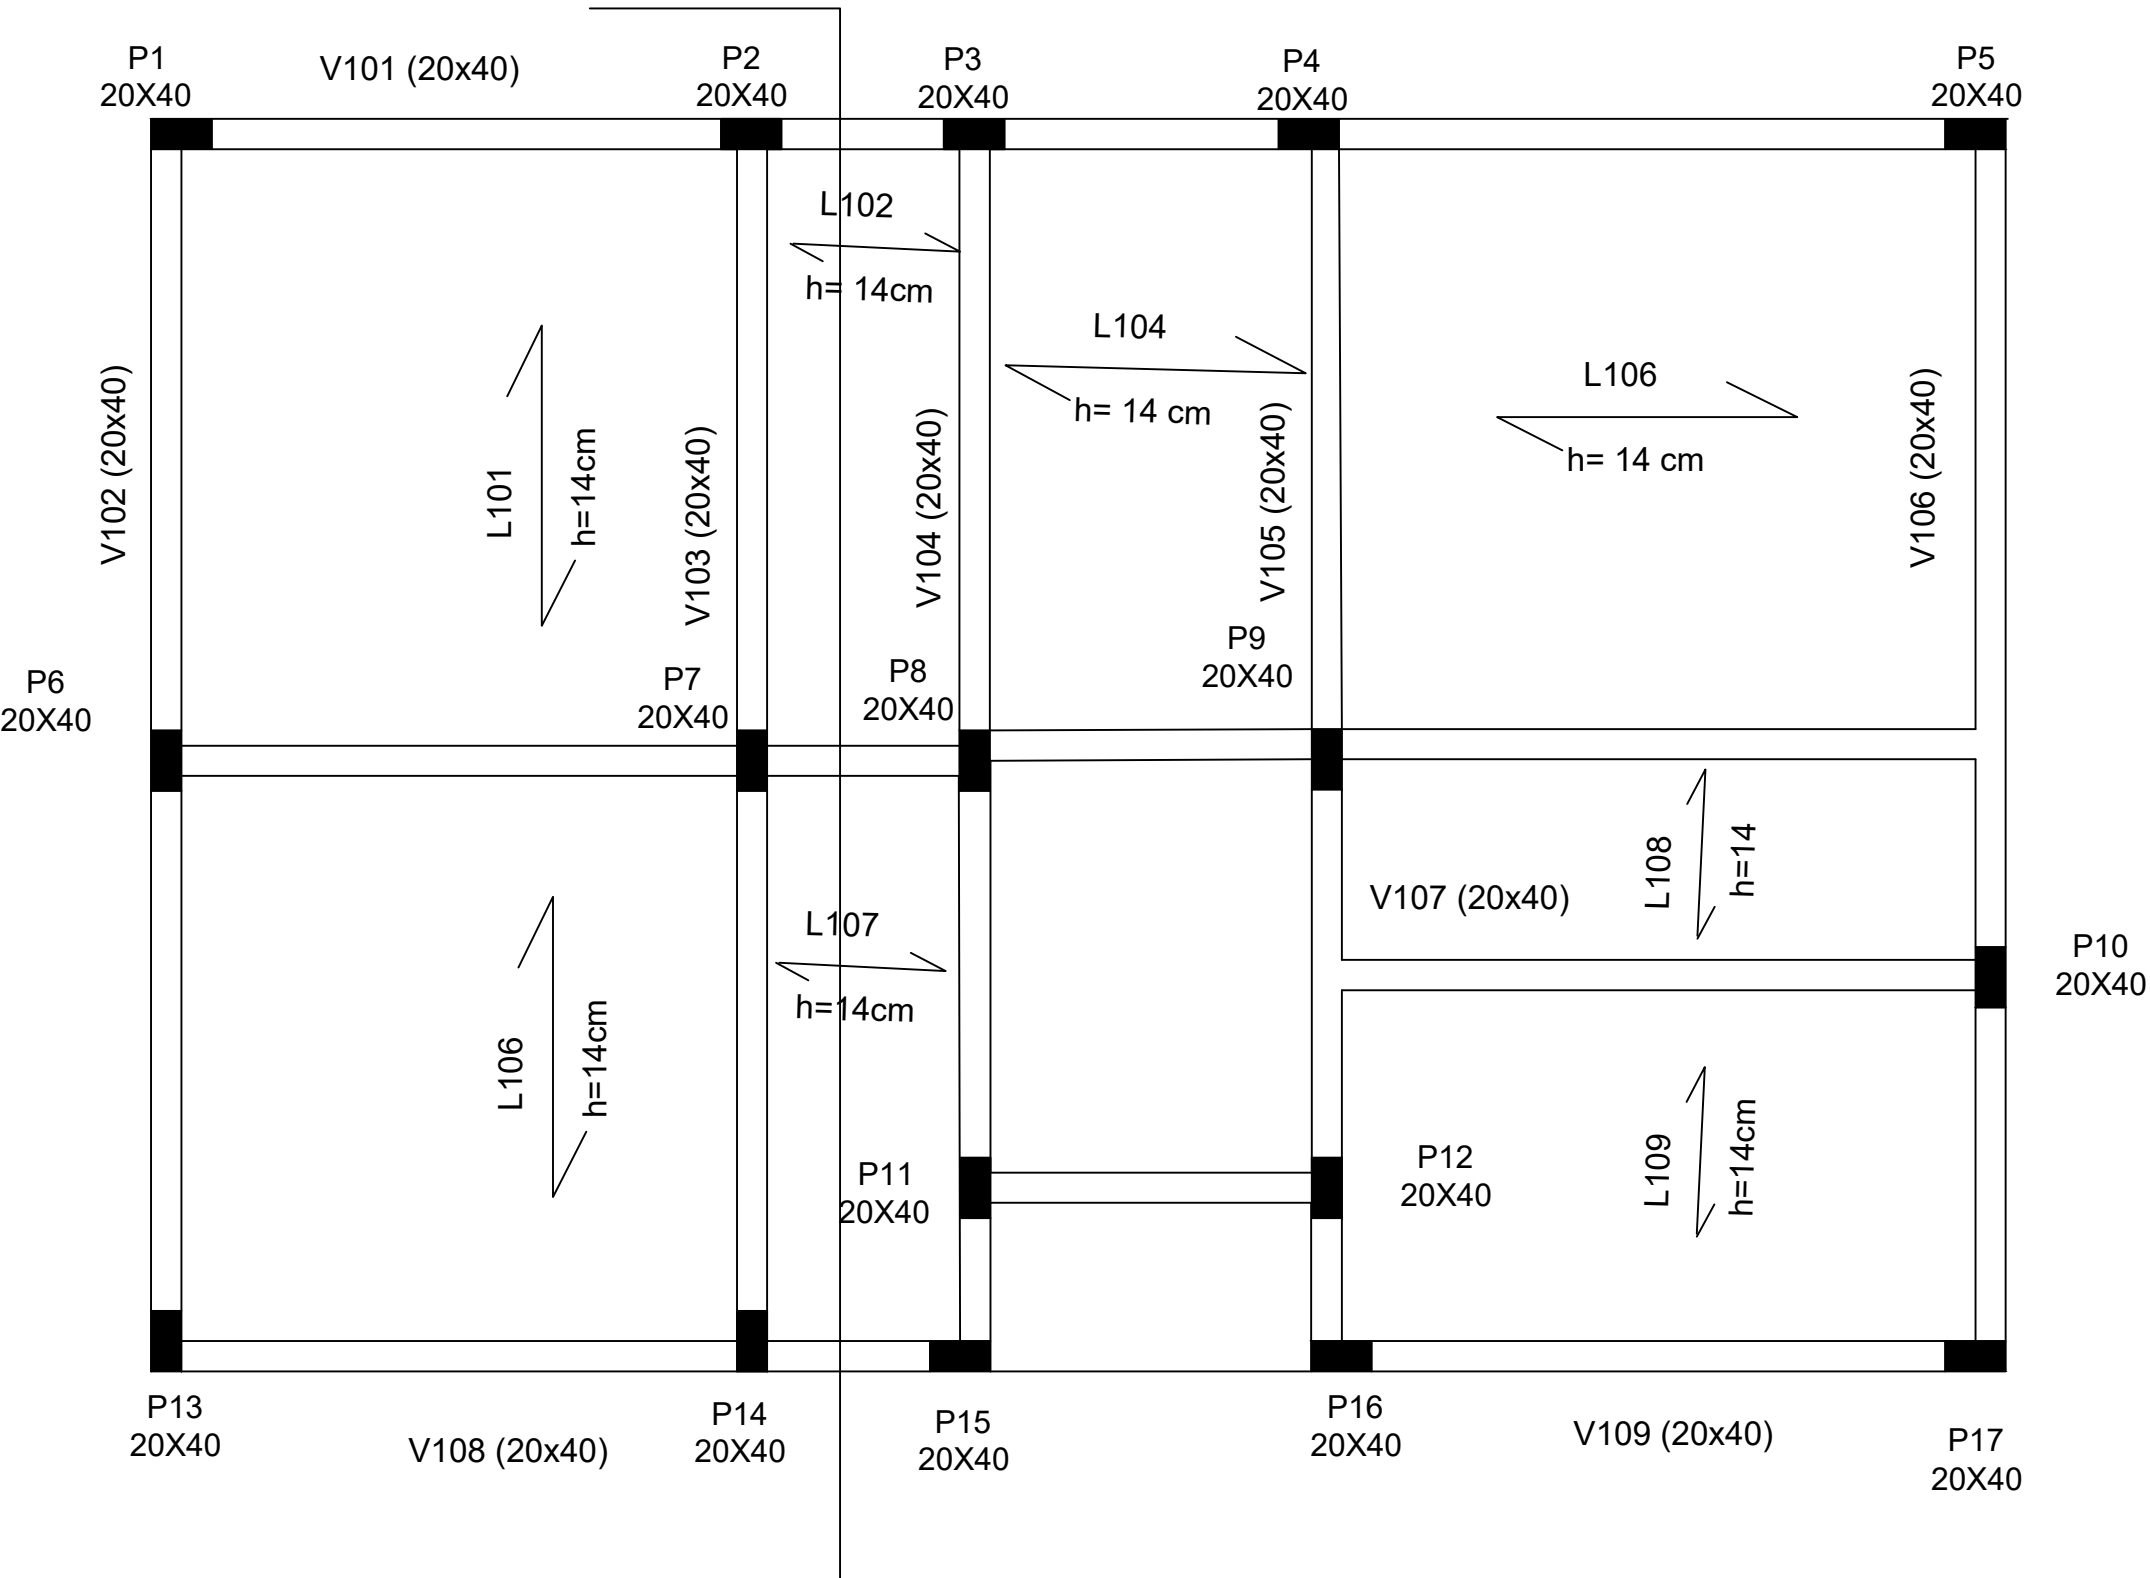
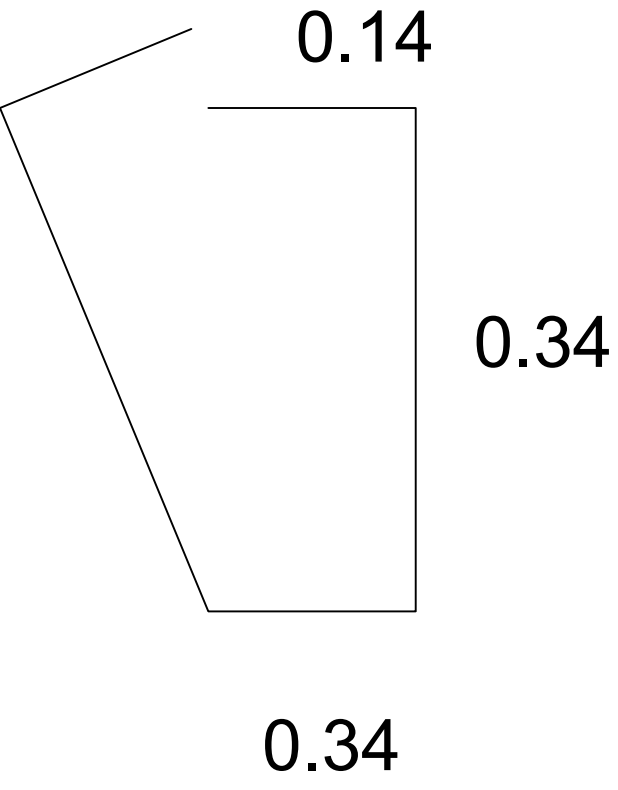


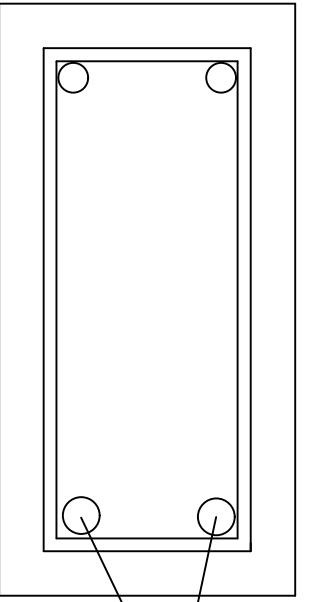

N1
CORTE - AA

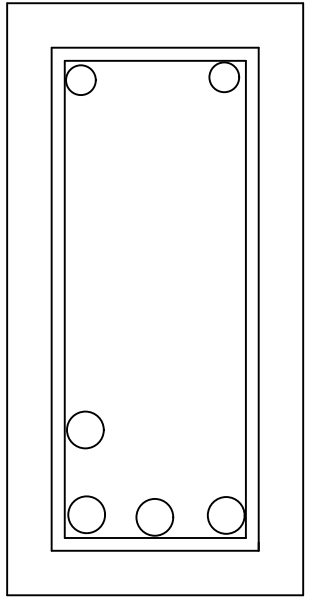

N3
CORTE - BB

N2
CORTE - CC

18 N5 6.3 PHI C/20 -

Carregamento	Esp (m)	Gaamma (kN/m²)	Total (kN/m²)
Contra piso	0,04	21	0,84
Impermeabilizante	0,05	0,11	0,0055
Revestimento Gesso	0,02	15	0,3
Porcelanato	0,01	21	0,21
Sobrecarga		1,5	1,5
Total 1 (kN/m²)			2,8555

Paredes Sobre Laje		
Lx	Ly	Alaje (M²)
3,97	4,34	17,2298

Paredes					
MATERIAL	Esp (m)	Largura (m)	Pé direito (m)	Gaamma (kN/m³)	Carga (Kn)
Tijolo Furado	0,14	3,8	2,7	14	20,1096
Repoco	0,06	3,8	2,7	21	12,9276
Impermeabiliz	0,04	3,8	2,7	0,11	0,045144
Total 2 (kN/m²)					33,08234
Cpar (kN/m²)	1,92007				
Total 2 (kN/m²)	4,77557				
hest (cm)	Peso próp. (kN/m²)		1,36		
hlaje (cm)					
Carga total (kN/m²)	6,13557	Especificações			
Capa (cm)	4	total (cm)	14		
Enchimento	40	Vigota	433 arranjo 1		
Inter eixo (cm)	50				