
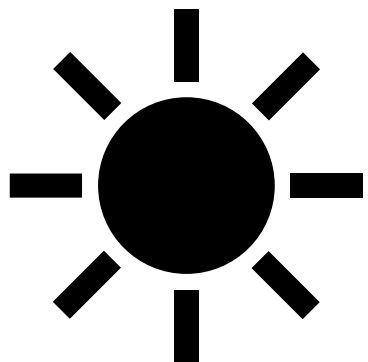


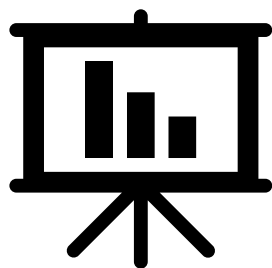


Fundamentos dos quais usamos para desenvolver o projeto


- Legislação municipal, Código de obras.
- Pedidos e ideias das clientes
- Programa de Necessidades
- Orientação Solar

Estudo Volumétrico

- PAV. SUPERIOR

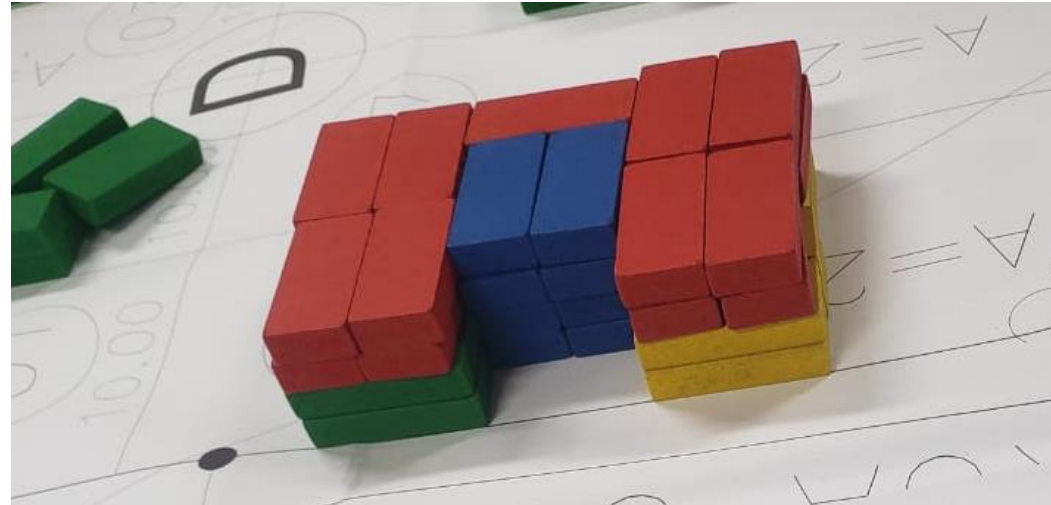

- PAV. INFERIOR

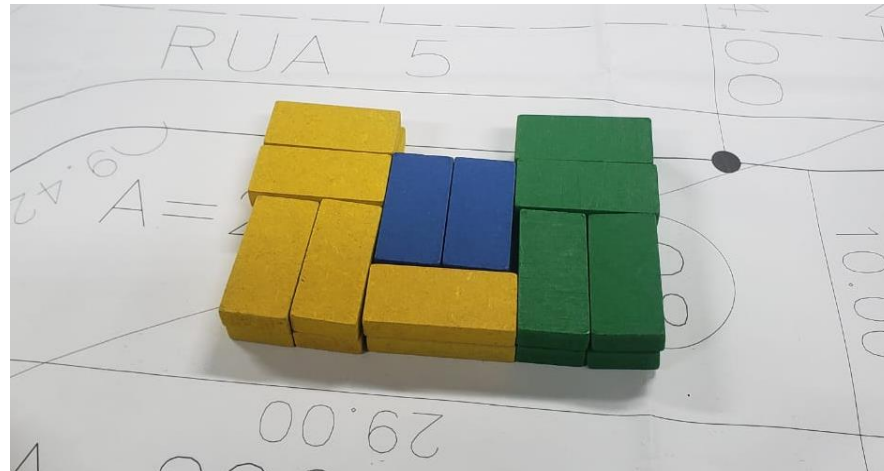

Fichas técnicas


FICHA TÉCNICA

LOCAÇÃO	RUA 5	
ÁREA DO LOTE	290,00 M²	
RECUOS	FROTAL MIN.: 2M	LATERAL MIN.: 1.5
GABARITO	7 M	
	LEGISLAÇÃO	PROJETADO
C.A	299.00 M²	188.90 / 63%
T.O	80%	94.5 M²/ 32%
T.P	20%	59.8 M² / 21%


PROGRAMAS DE NECESSIDADES


COMPATIMENTOS	ÁREA
ÁREA SOCIAL	
SALA	29.50 M²
ESCRITORIO	76.56 M²
LAVABO	3.43 M²
ÁREA DE SERVIÇOS	
COZINHA	25.80 M²
B.W.C SERVIÇOS	3.43 M²
ÁREA DE SERVIÇOS	7.52 M²
ÁREA ÍNTIMA	
DORM. 1	14.70 M²
DORM. 2	12.57 M²
B.W.C SUPERIOR	3.43 M²
B.W.C SUÍTE	3.43 M²
CLOSED	17,79 M²
SUÍTE	17,79 M²
VARANDA	4.61 M²
TERRAÇO	7.15 M²
ÁREA DE CIRCULAÇÃO	
ESCADA	6.00 M²
CIRCULAÇÃO	6.88 M²

PAVIMENTO
SUPERIOR
ESCALA 1:50

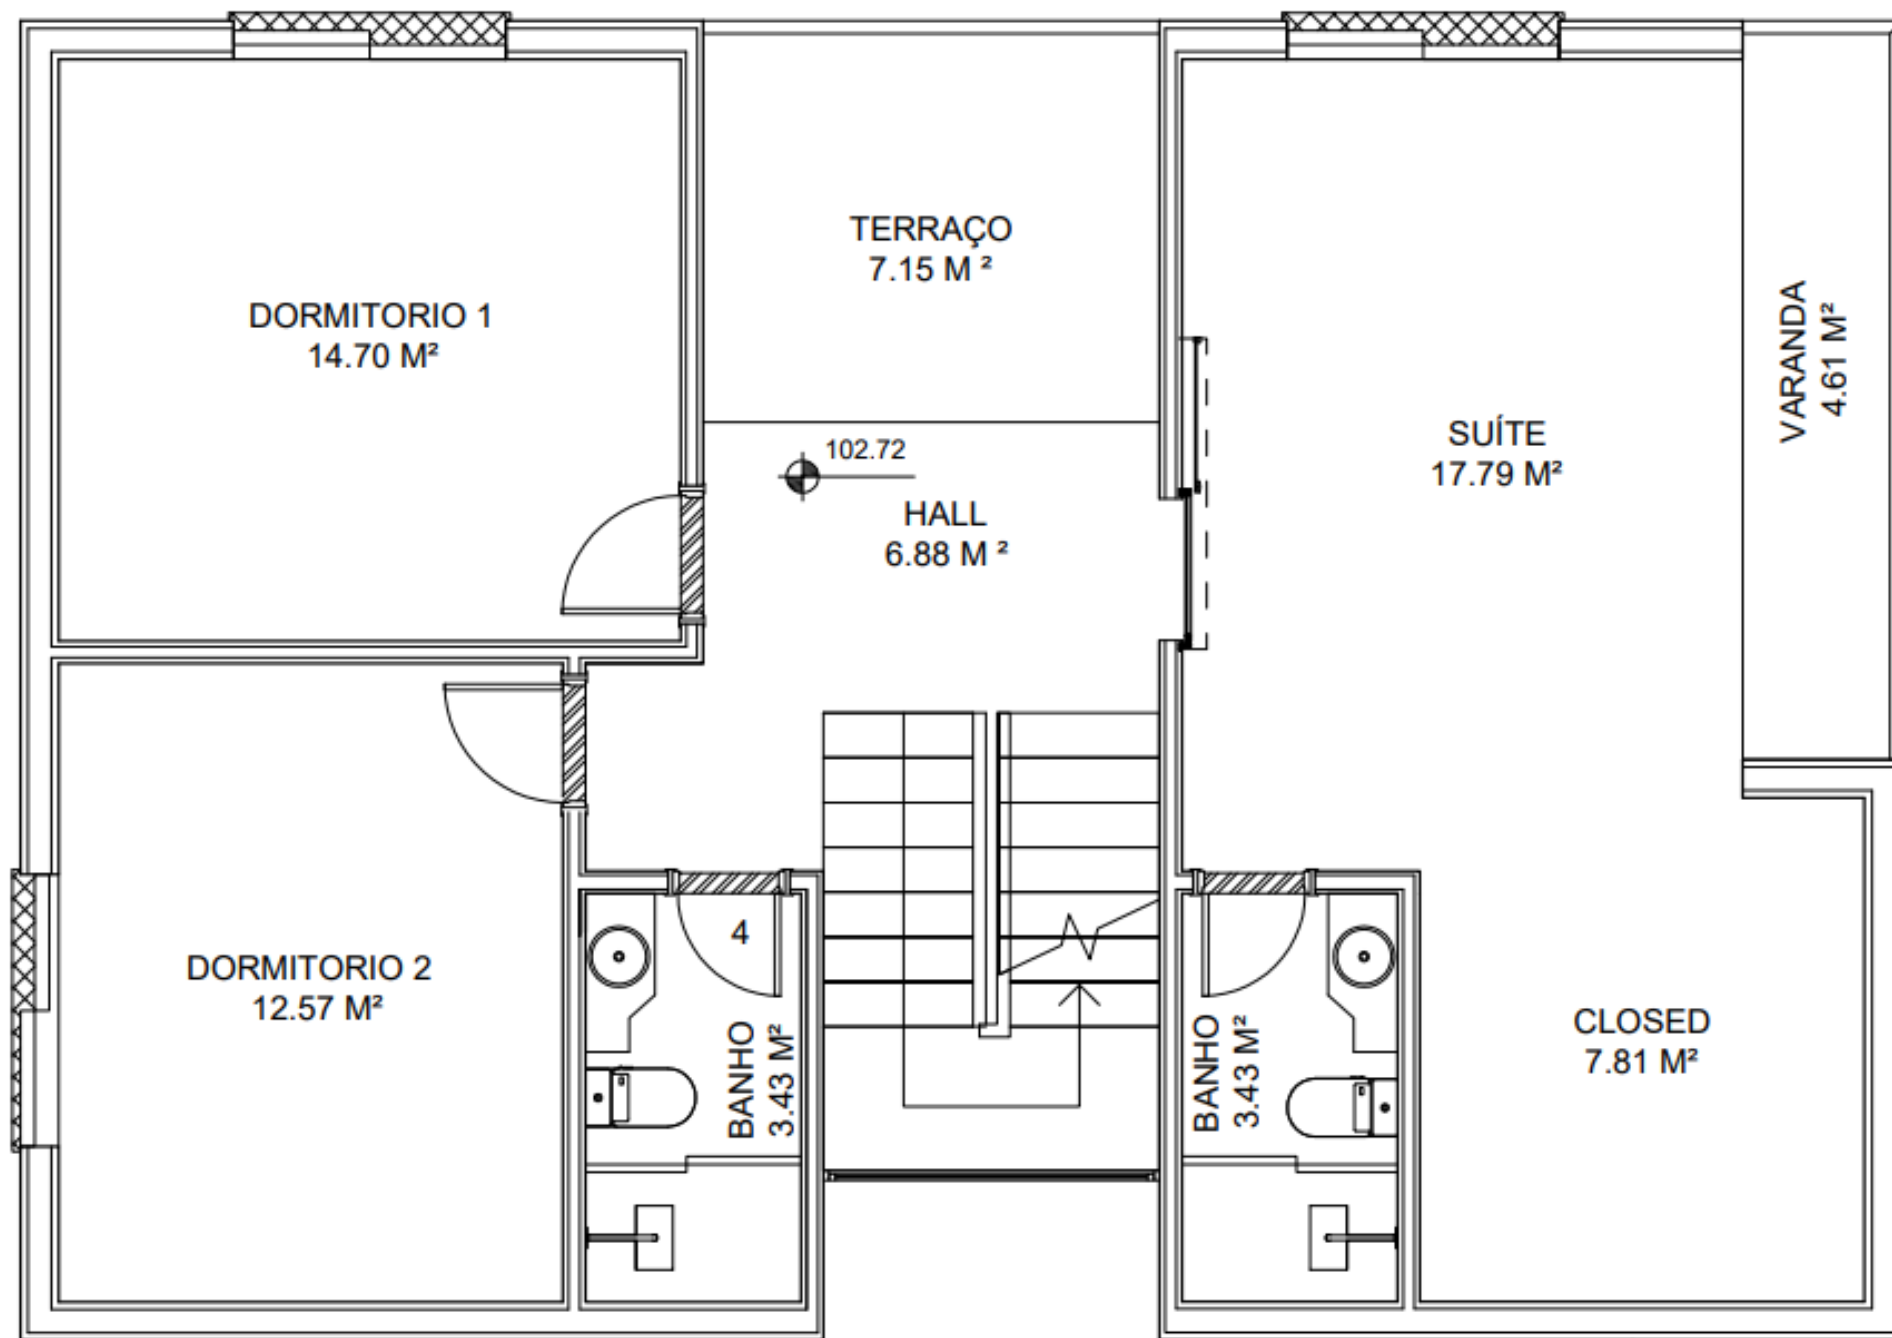


PAVIMENTO
INFERIOR
ESCALA 1:50

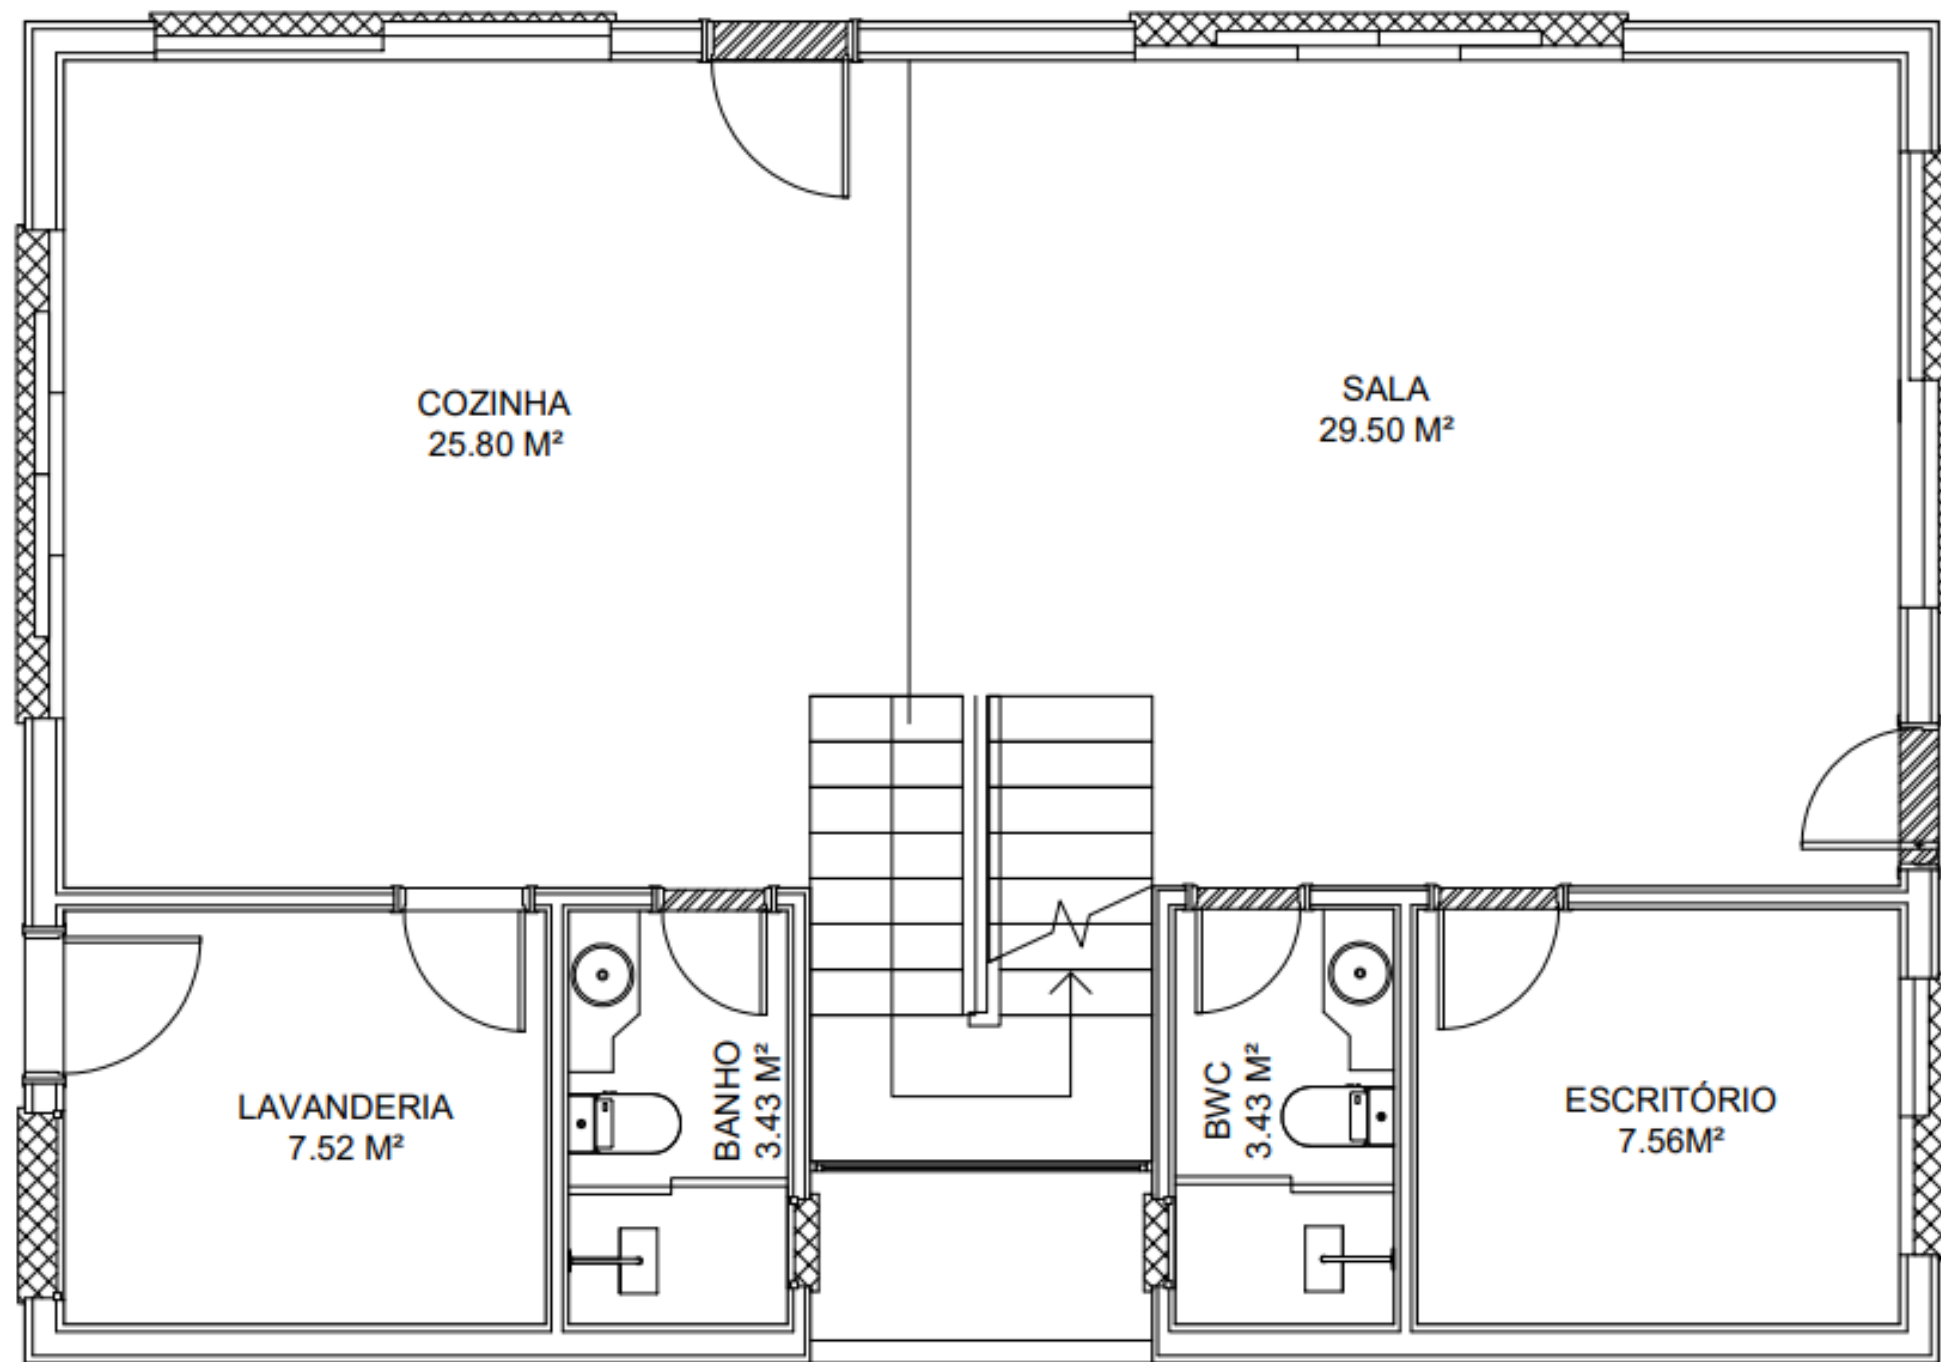


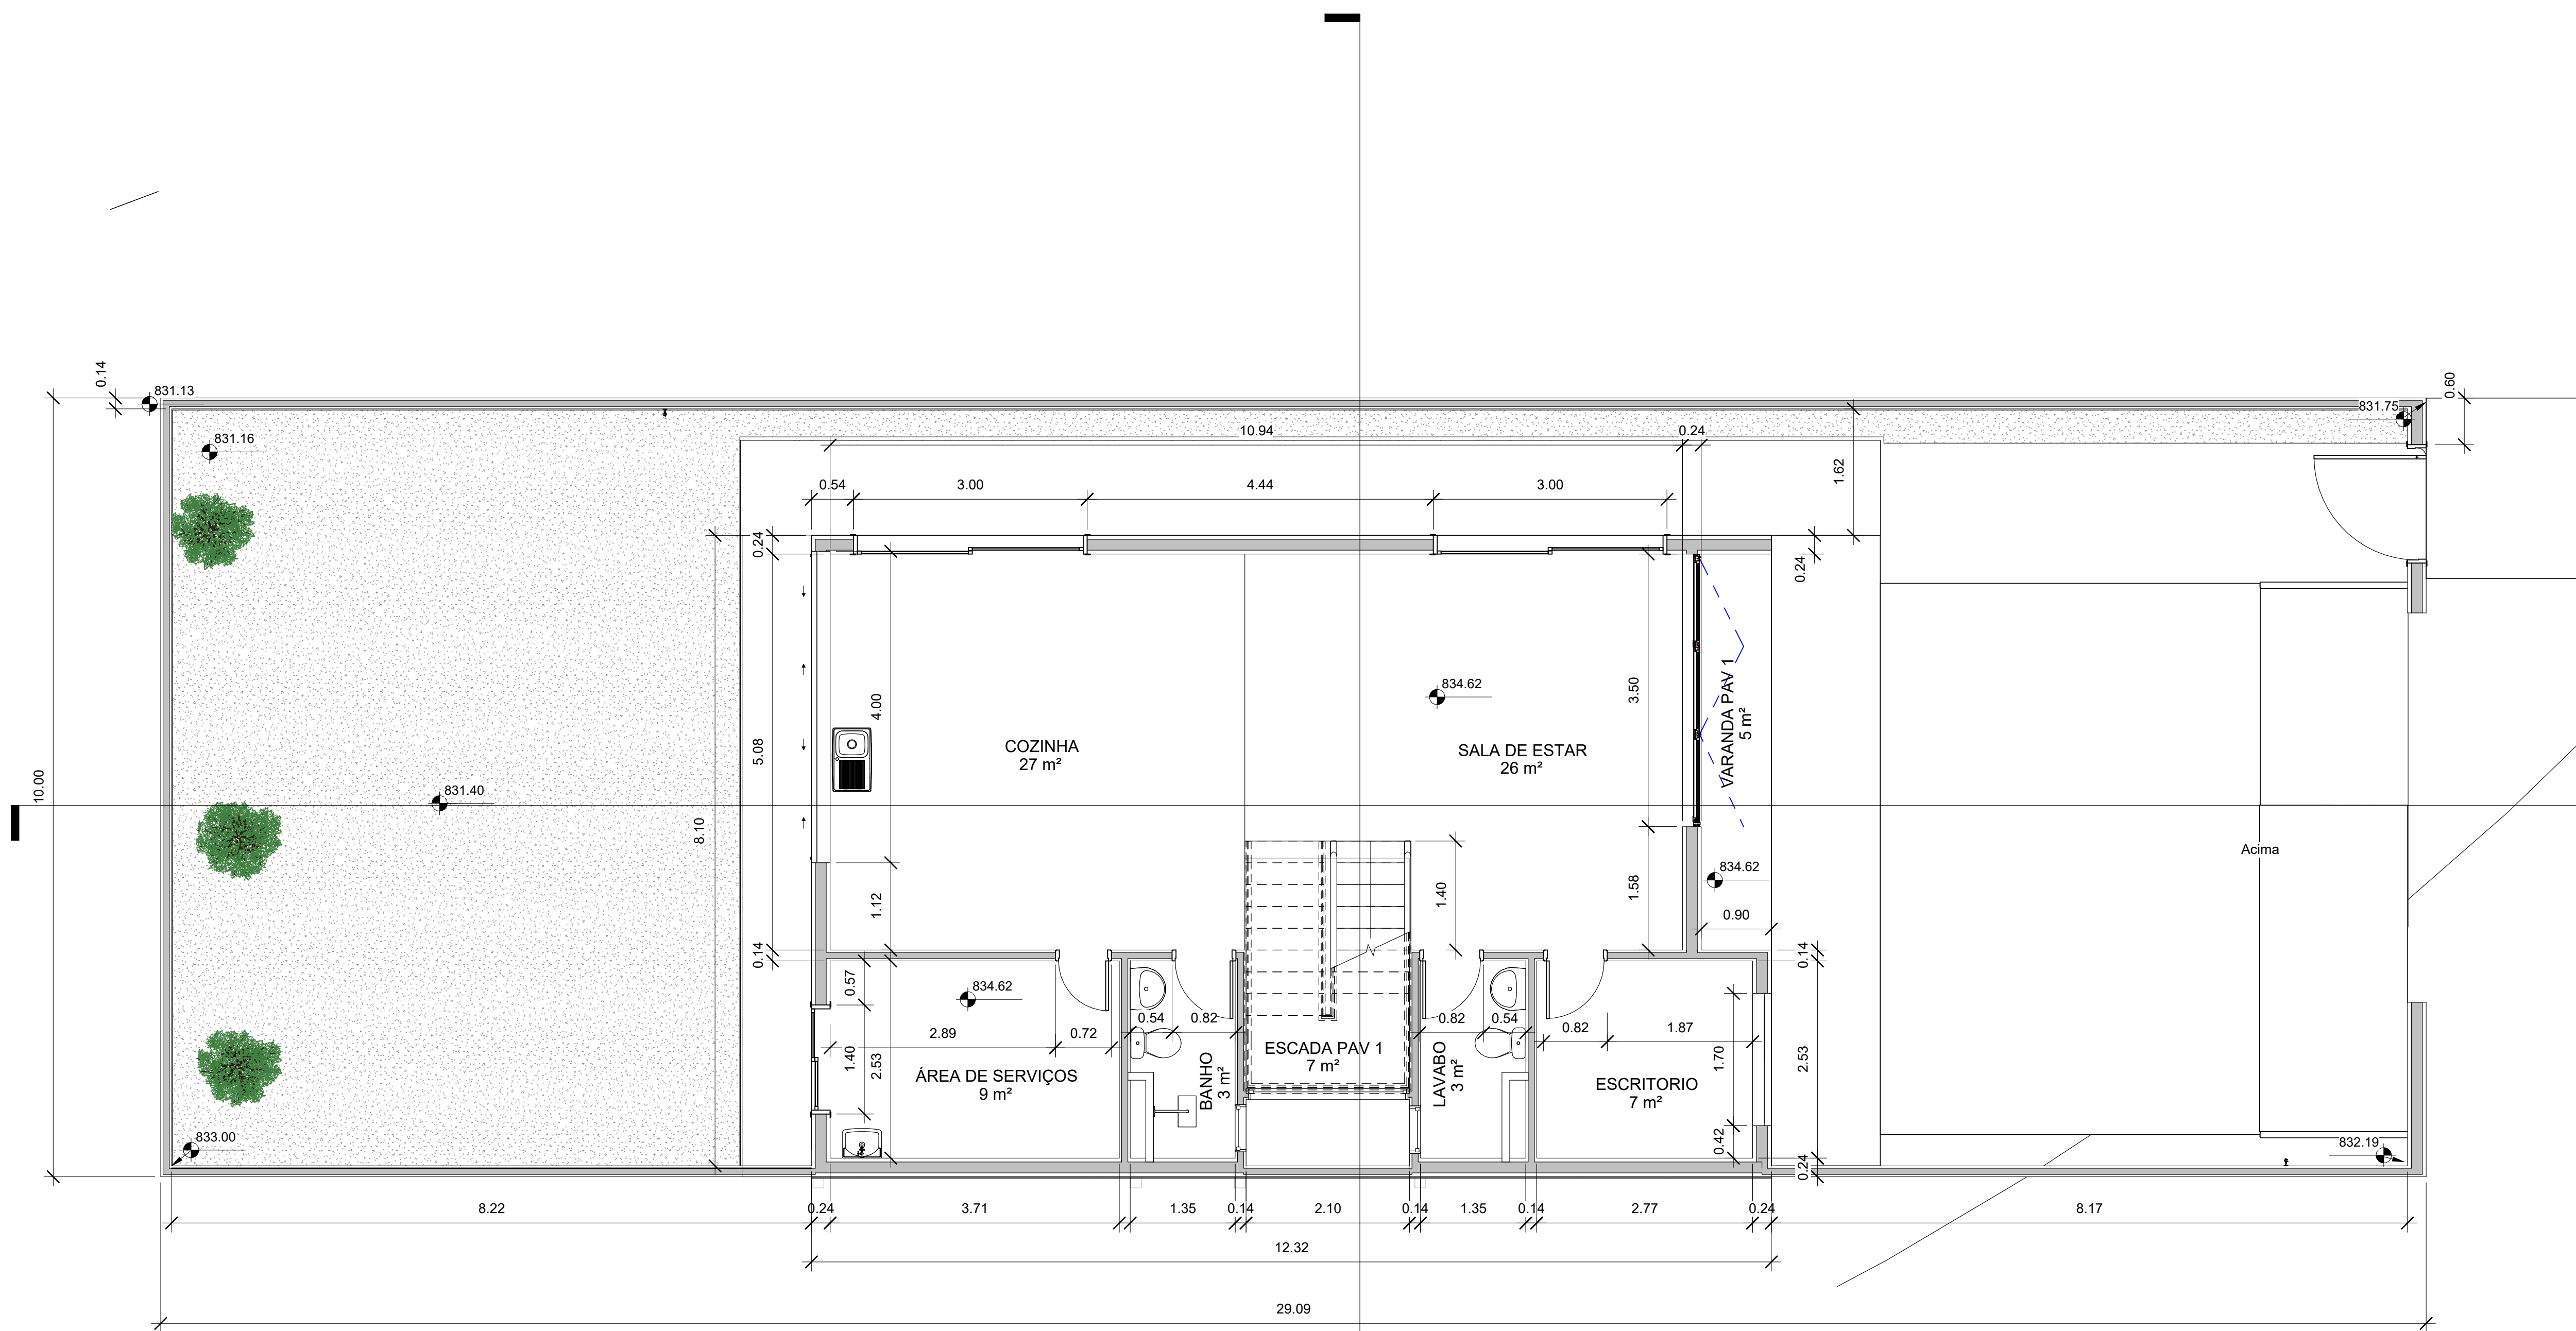


1 PAV 1
1 : 50

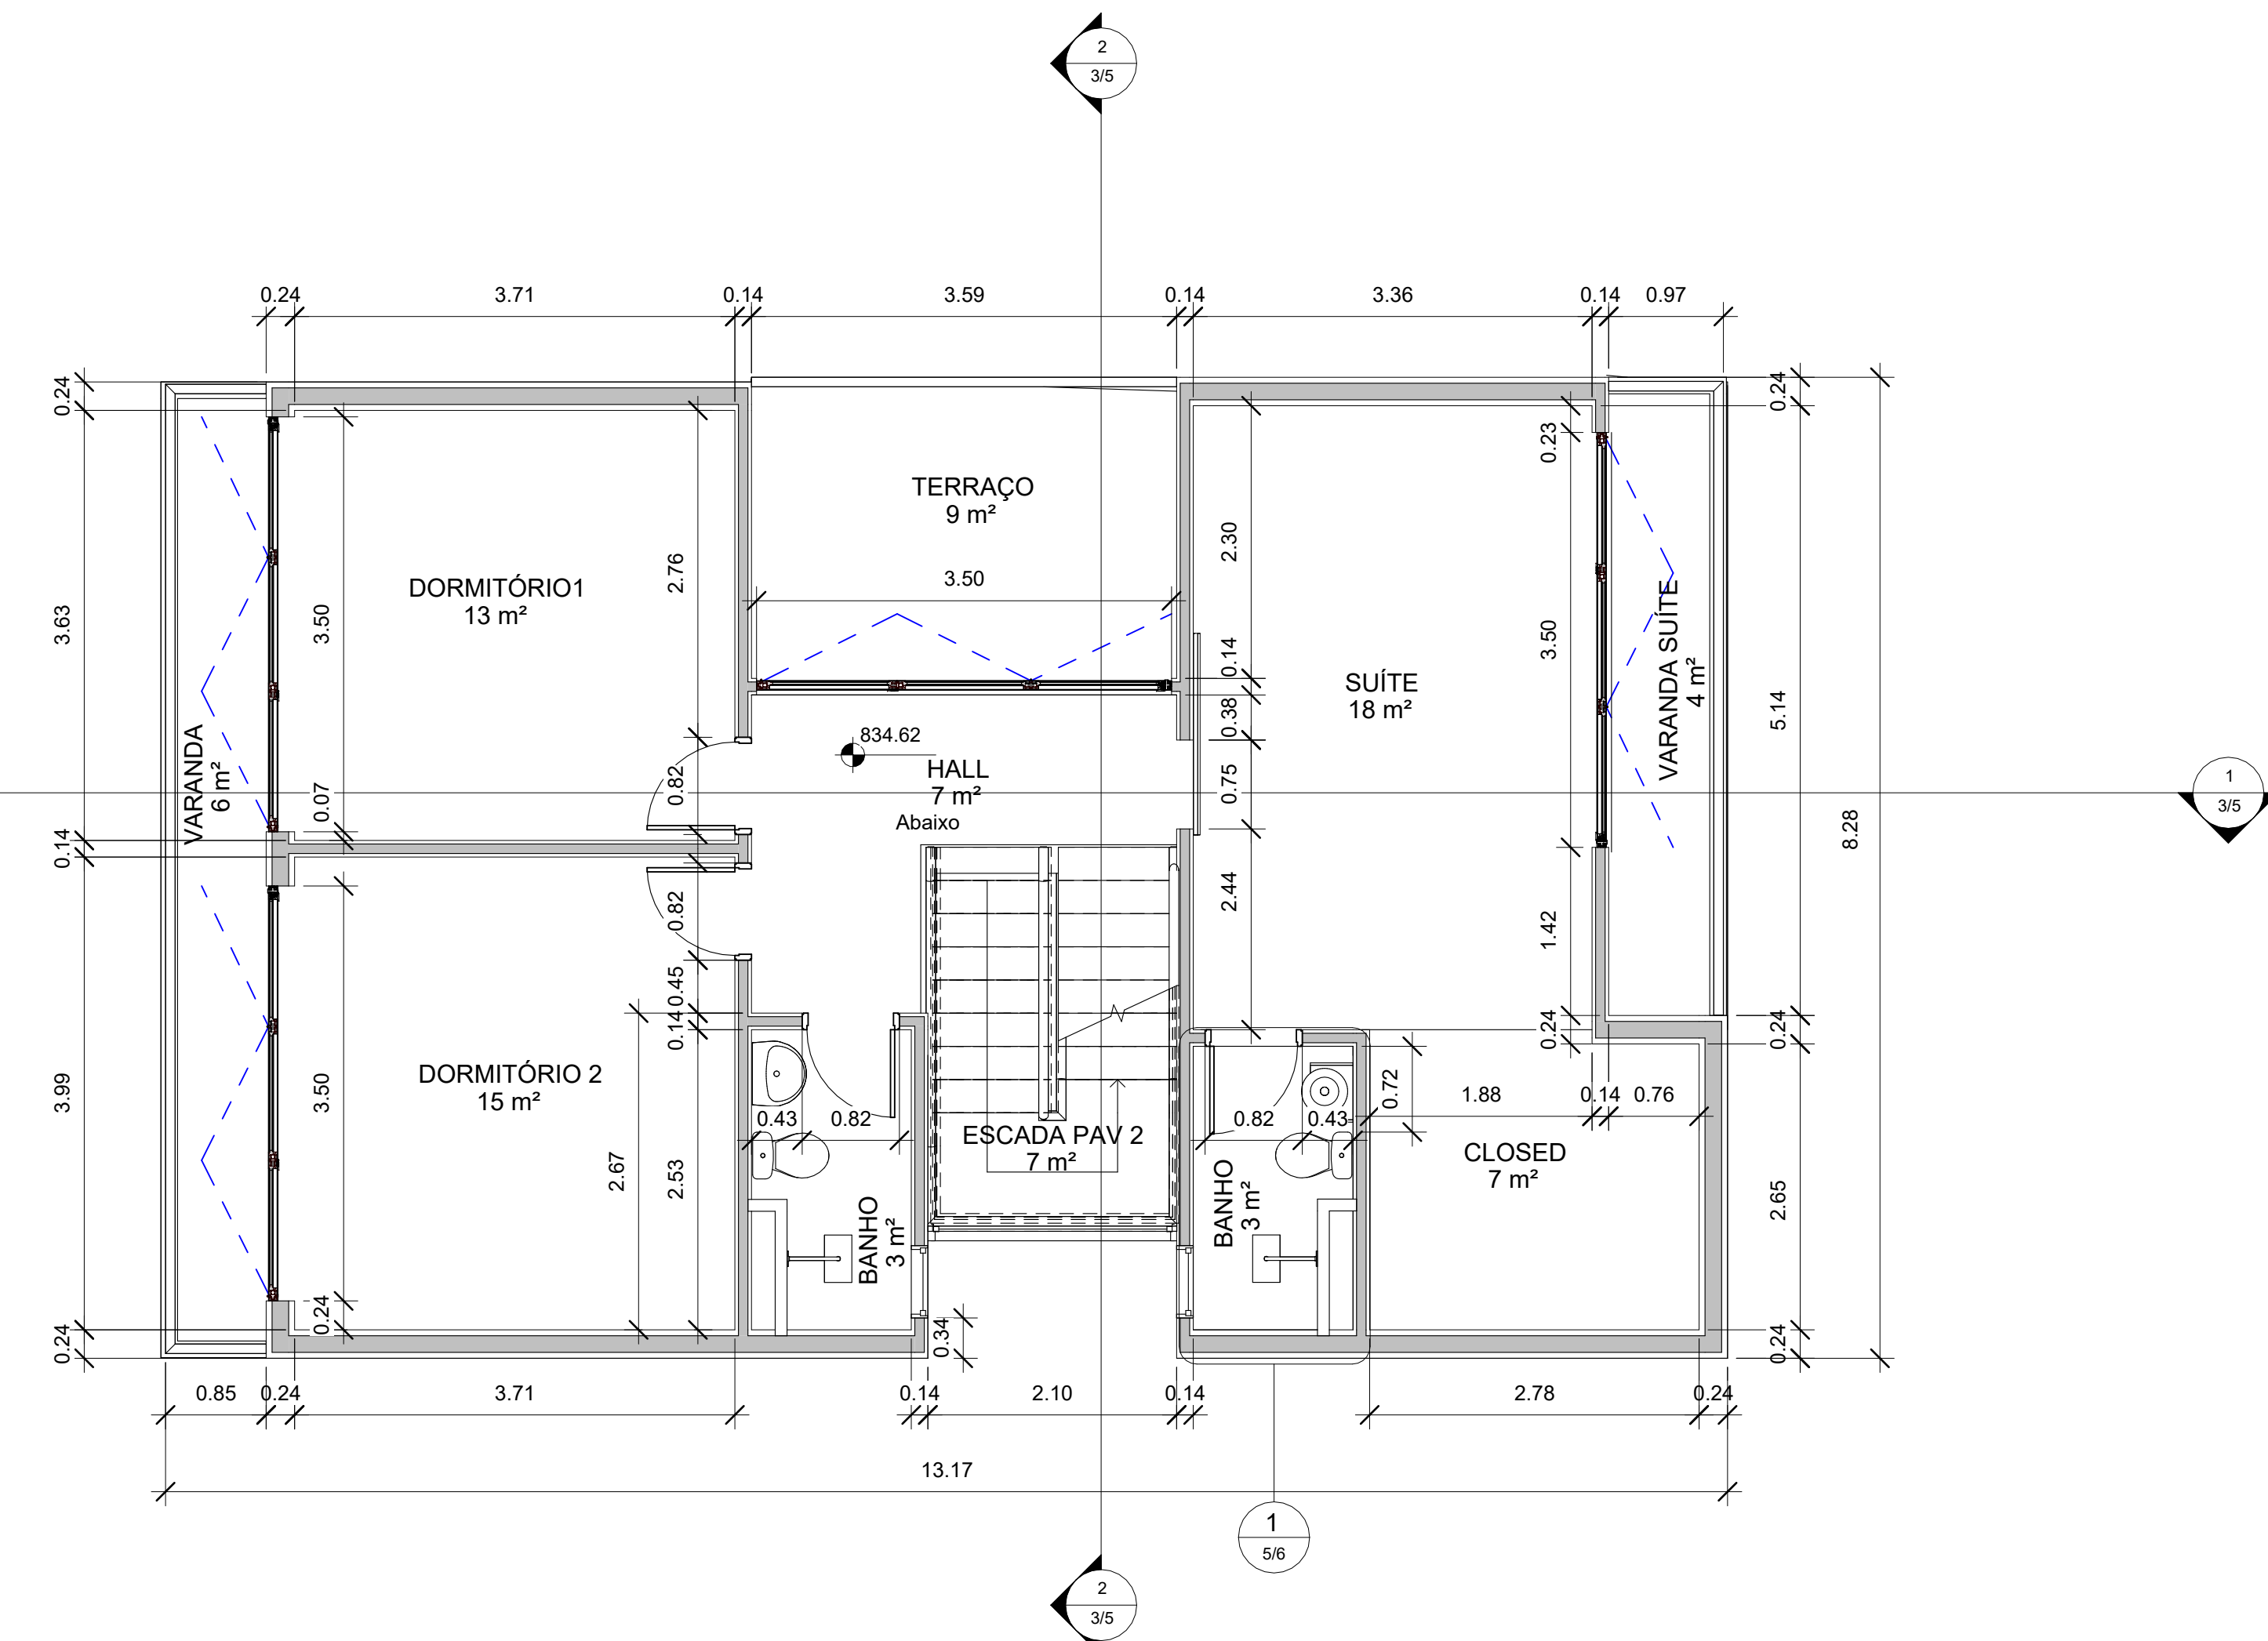


2 PAV 2
1 : 50

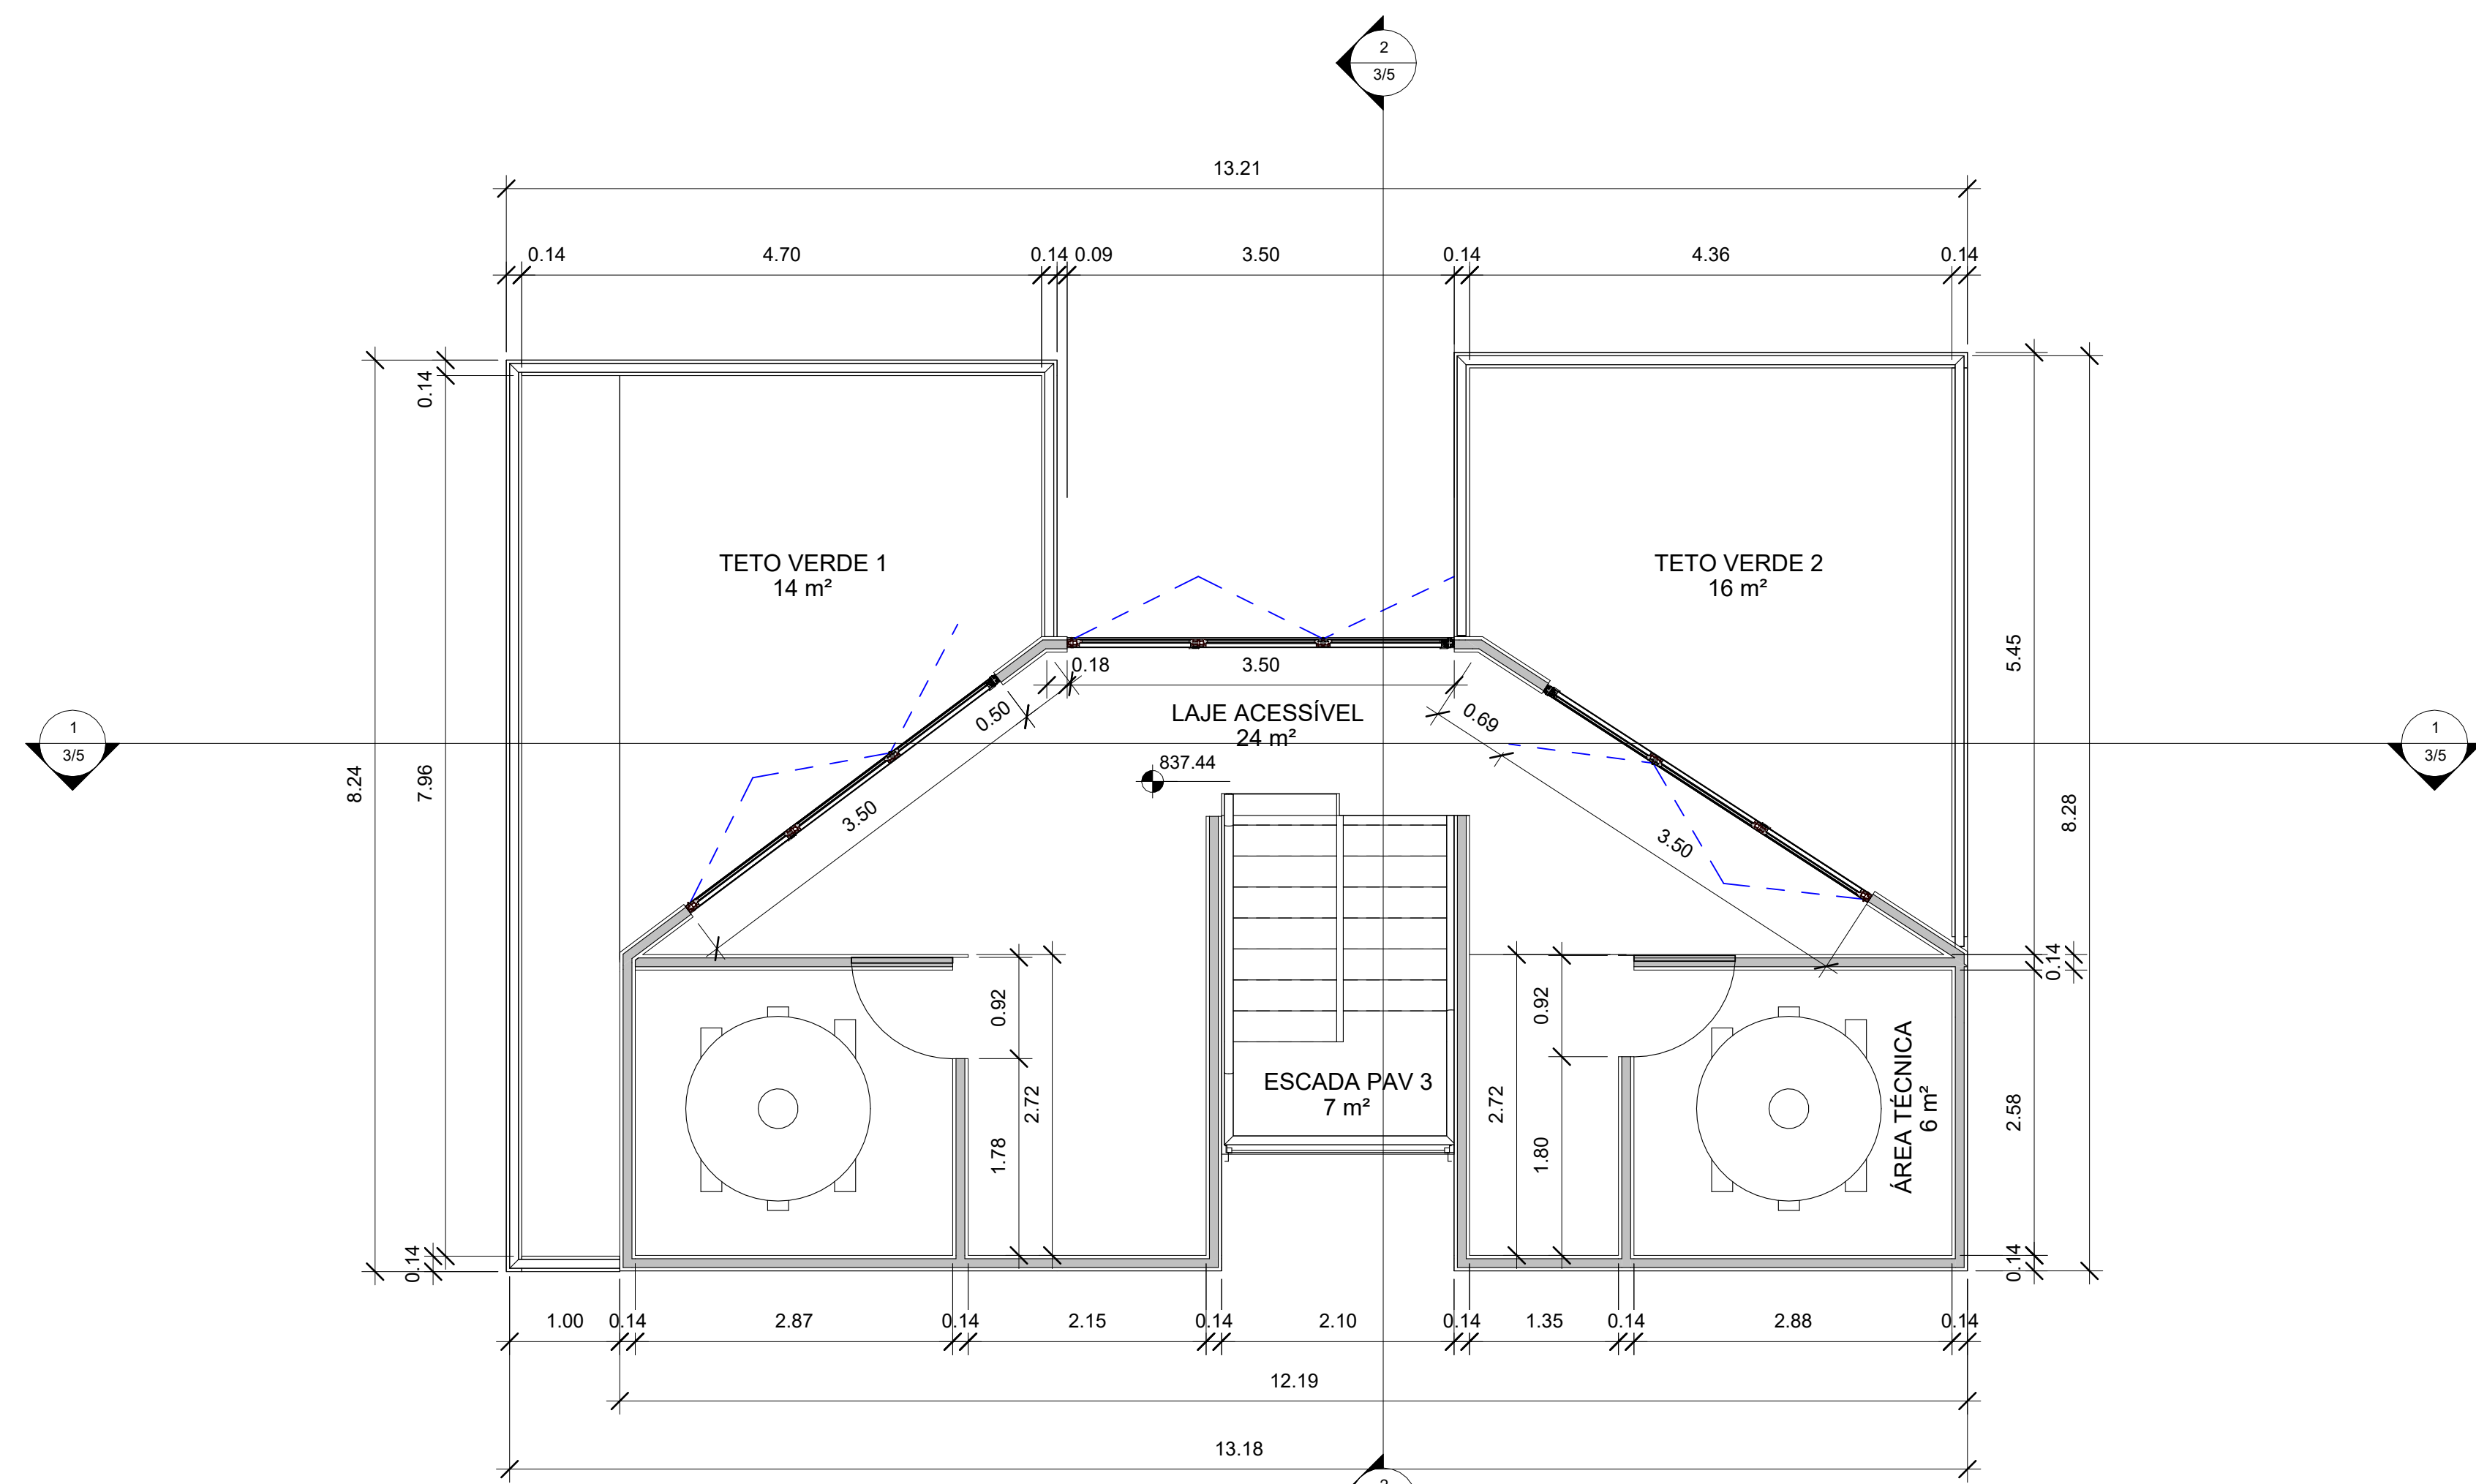


3 PAV 3
1 : 50

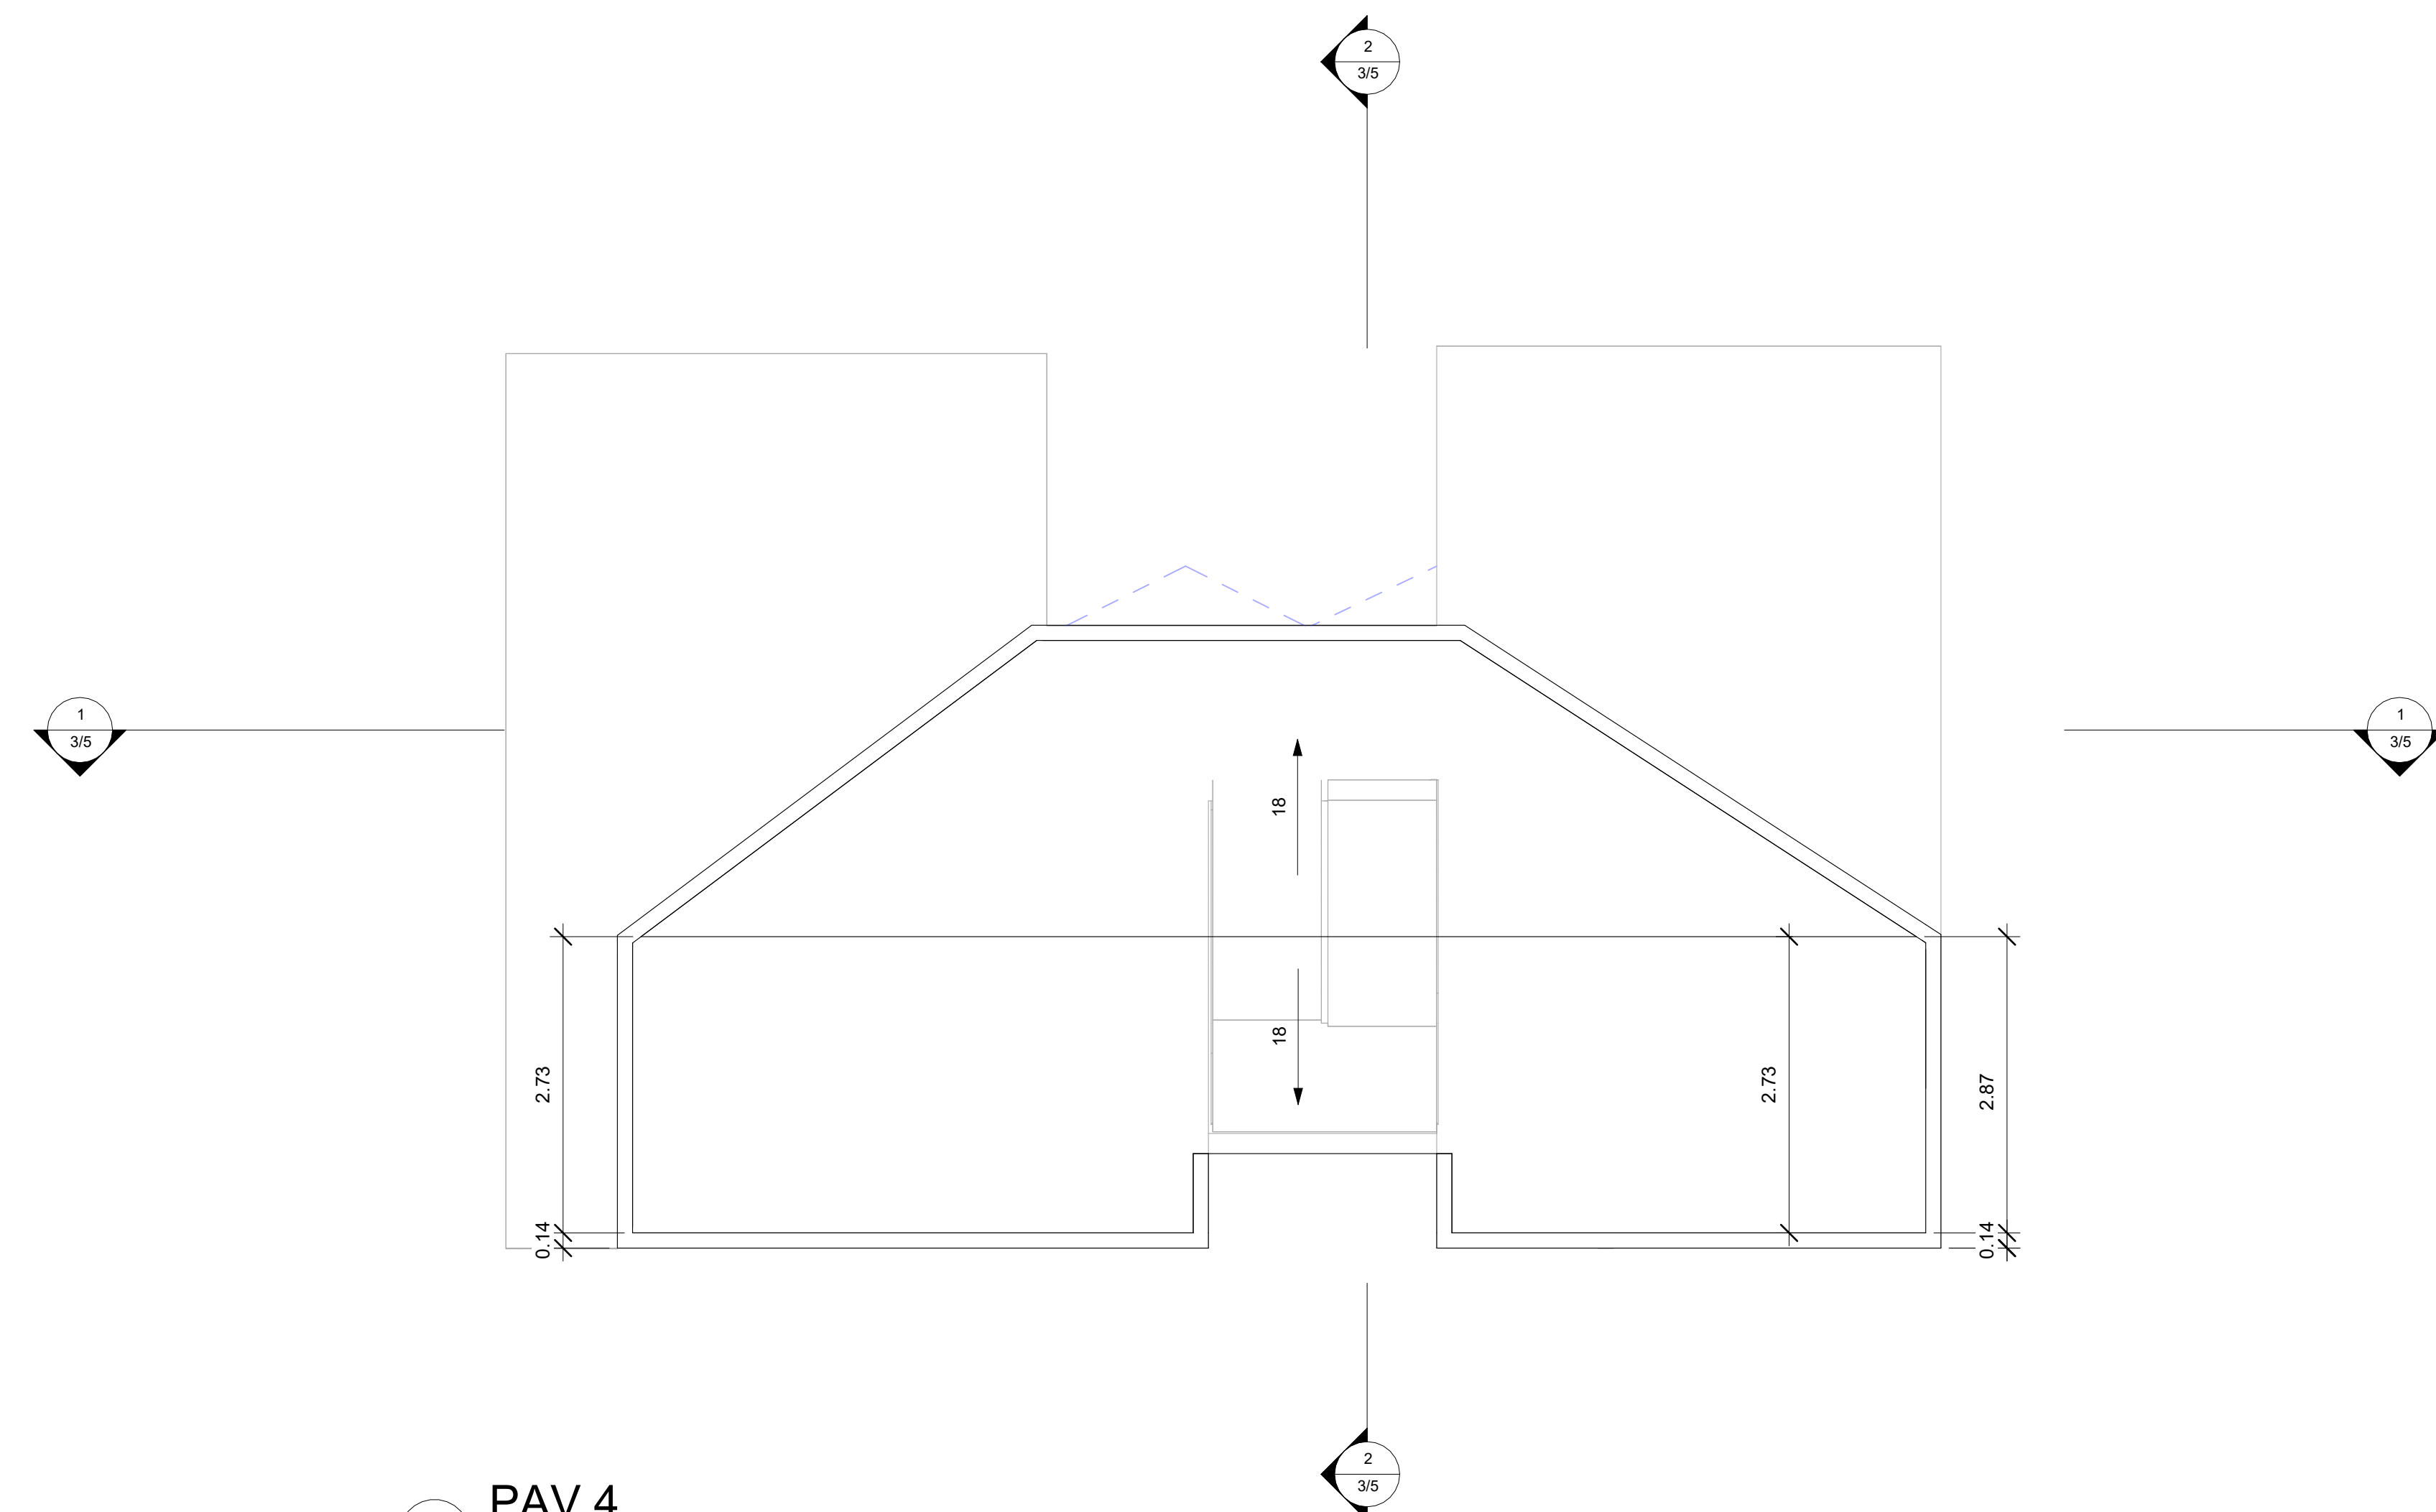


4 PAV 4
1 : 50

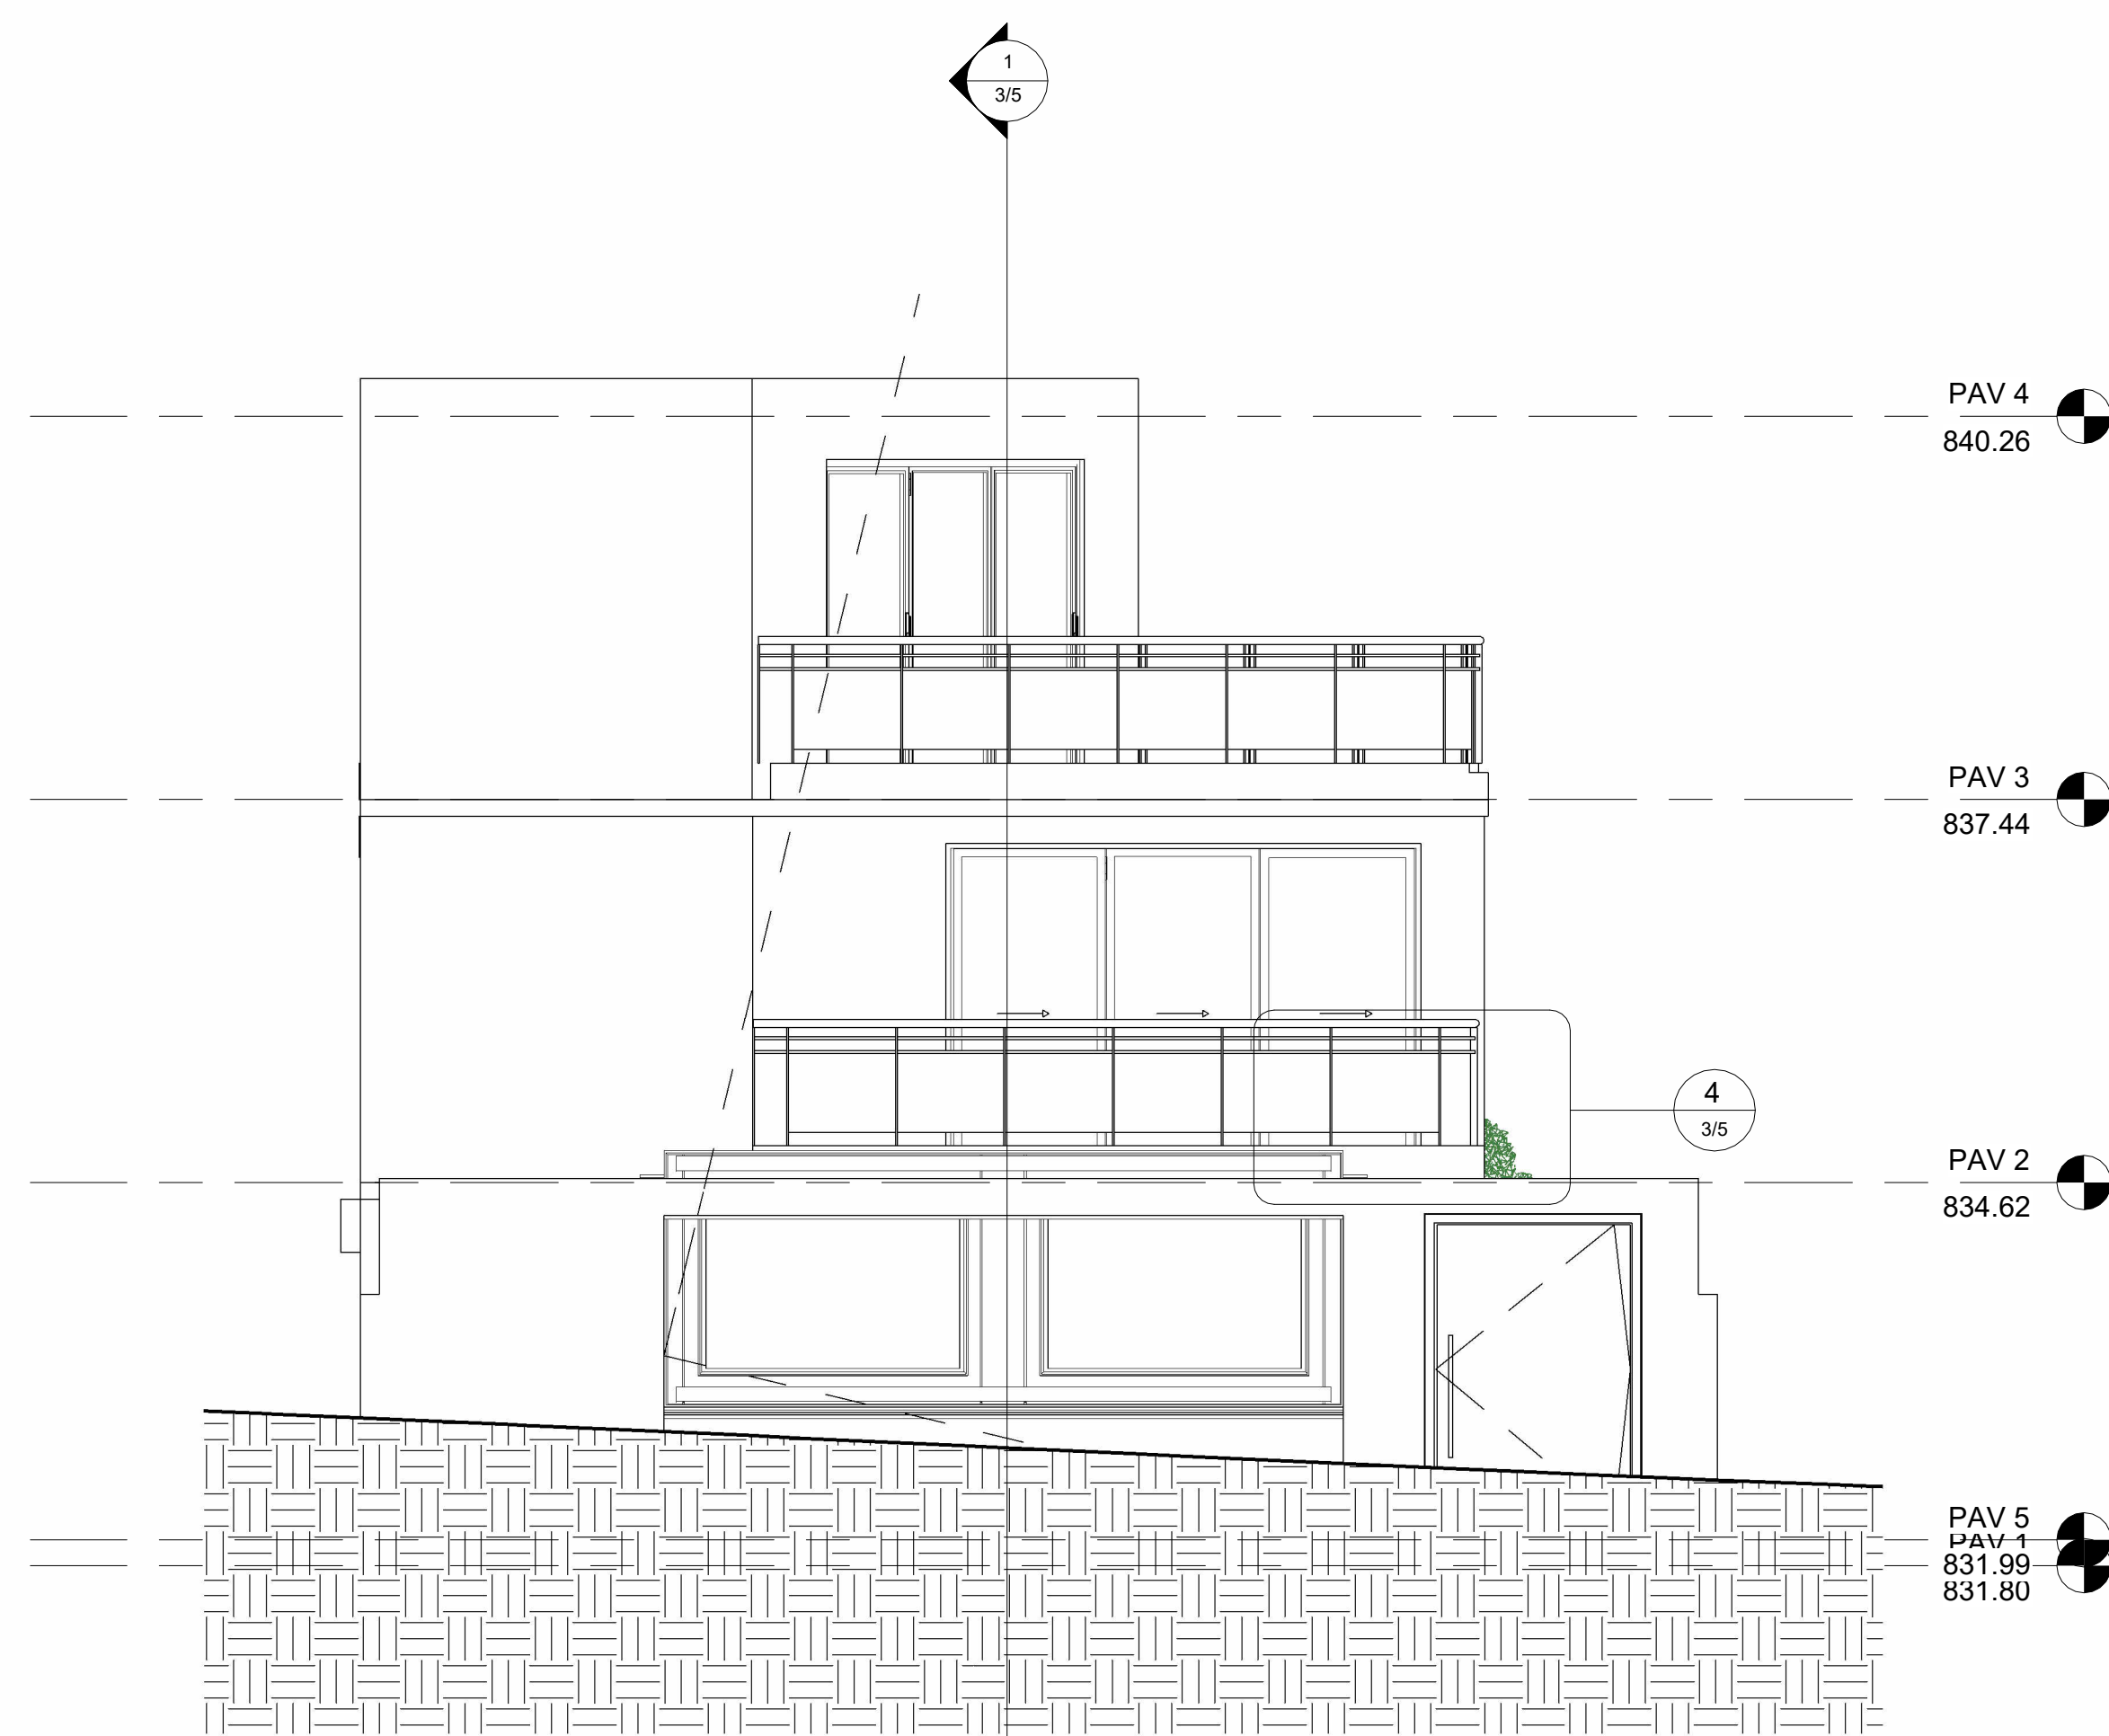


1 Leste
1 : 50

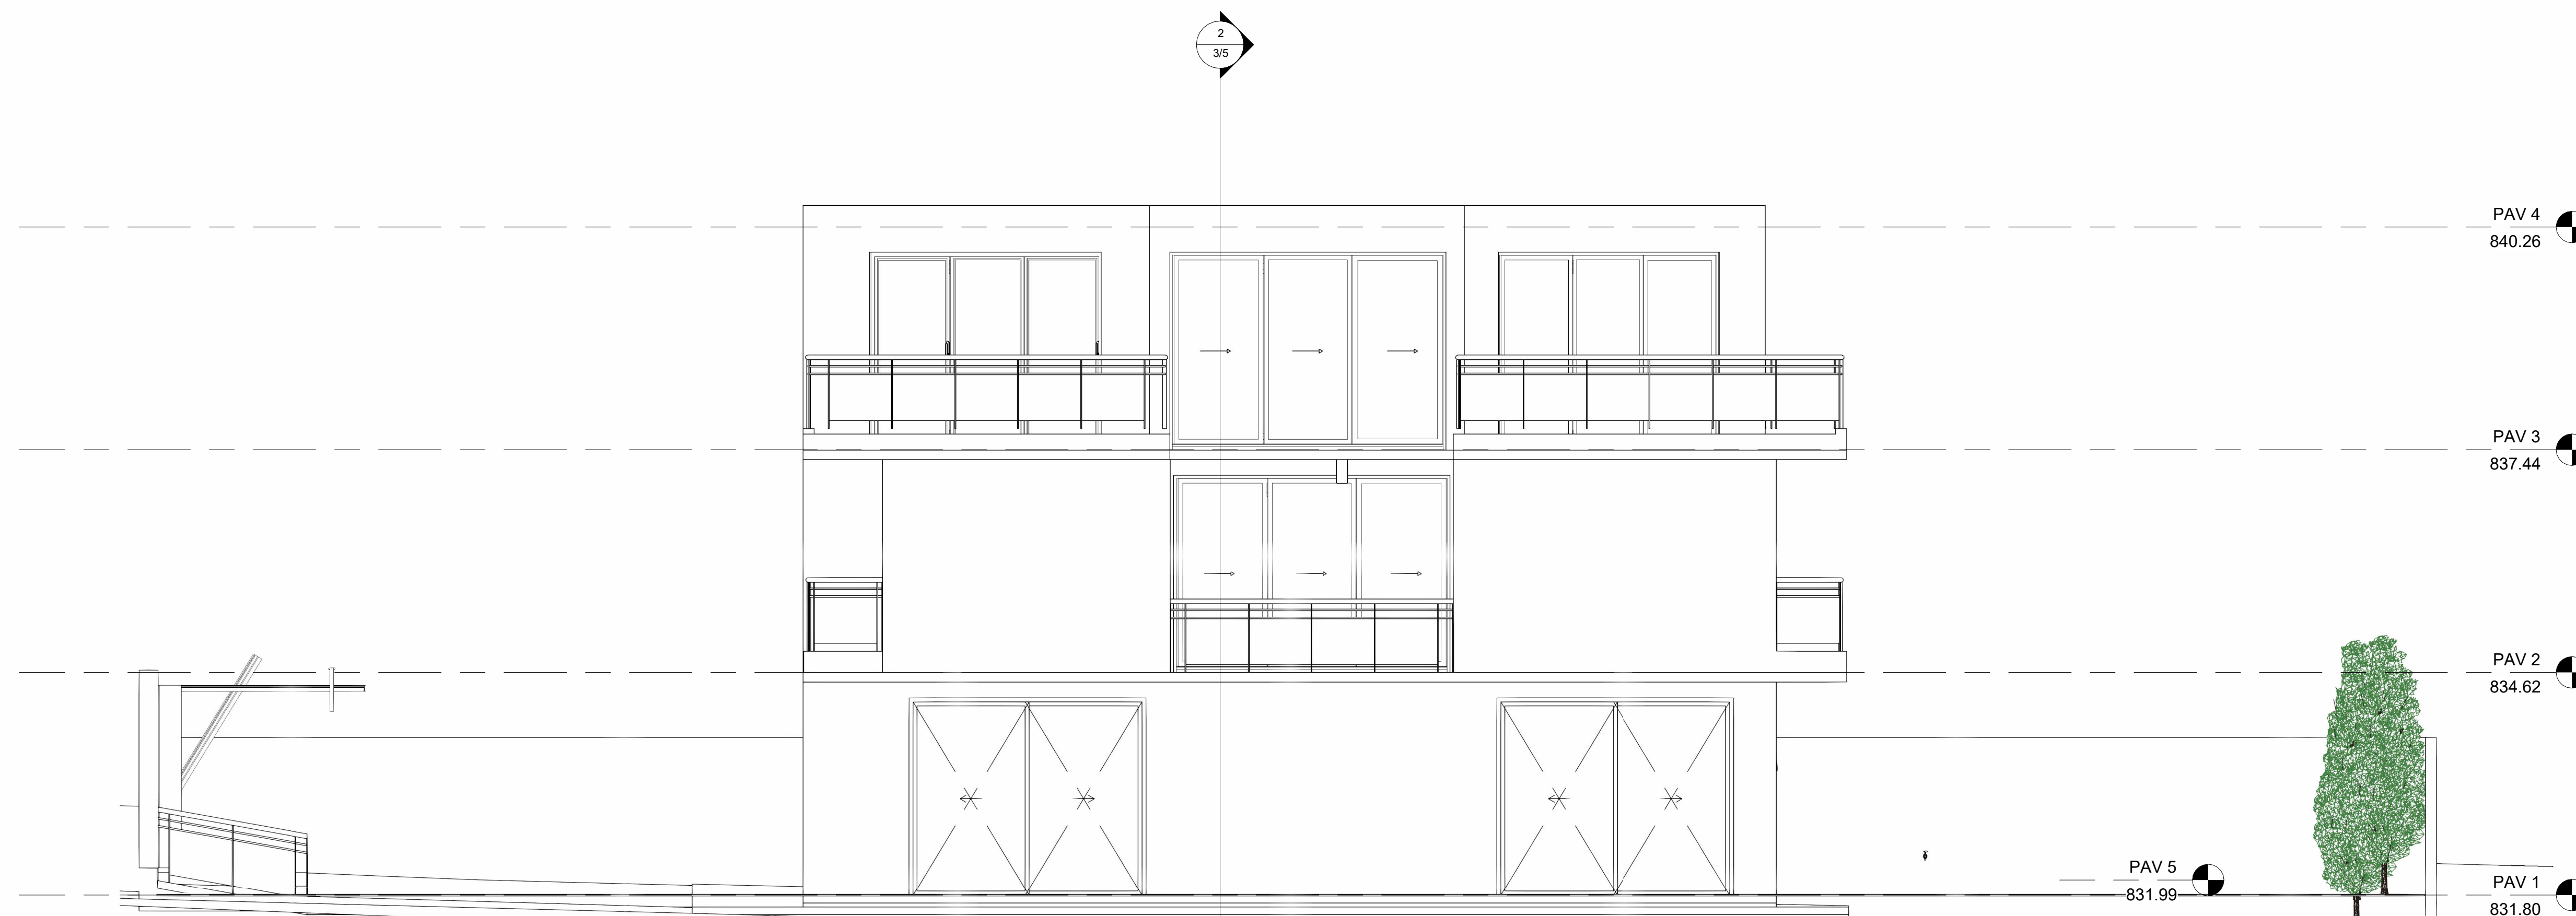


2 Norte
1 : 50

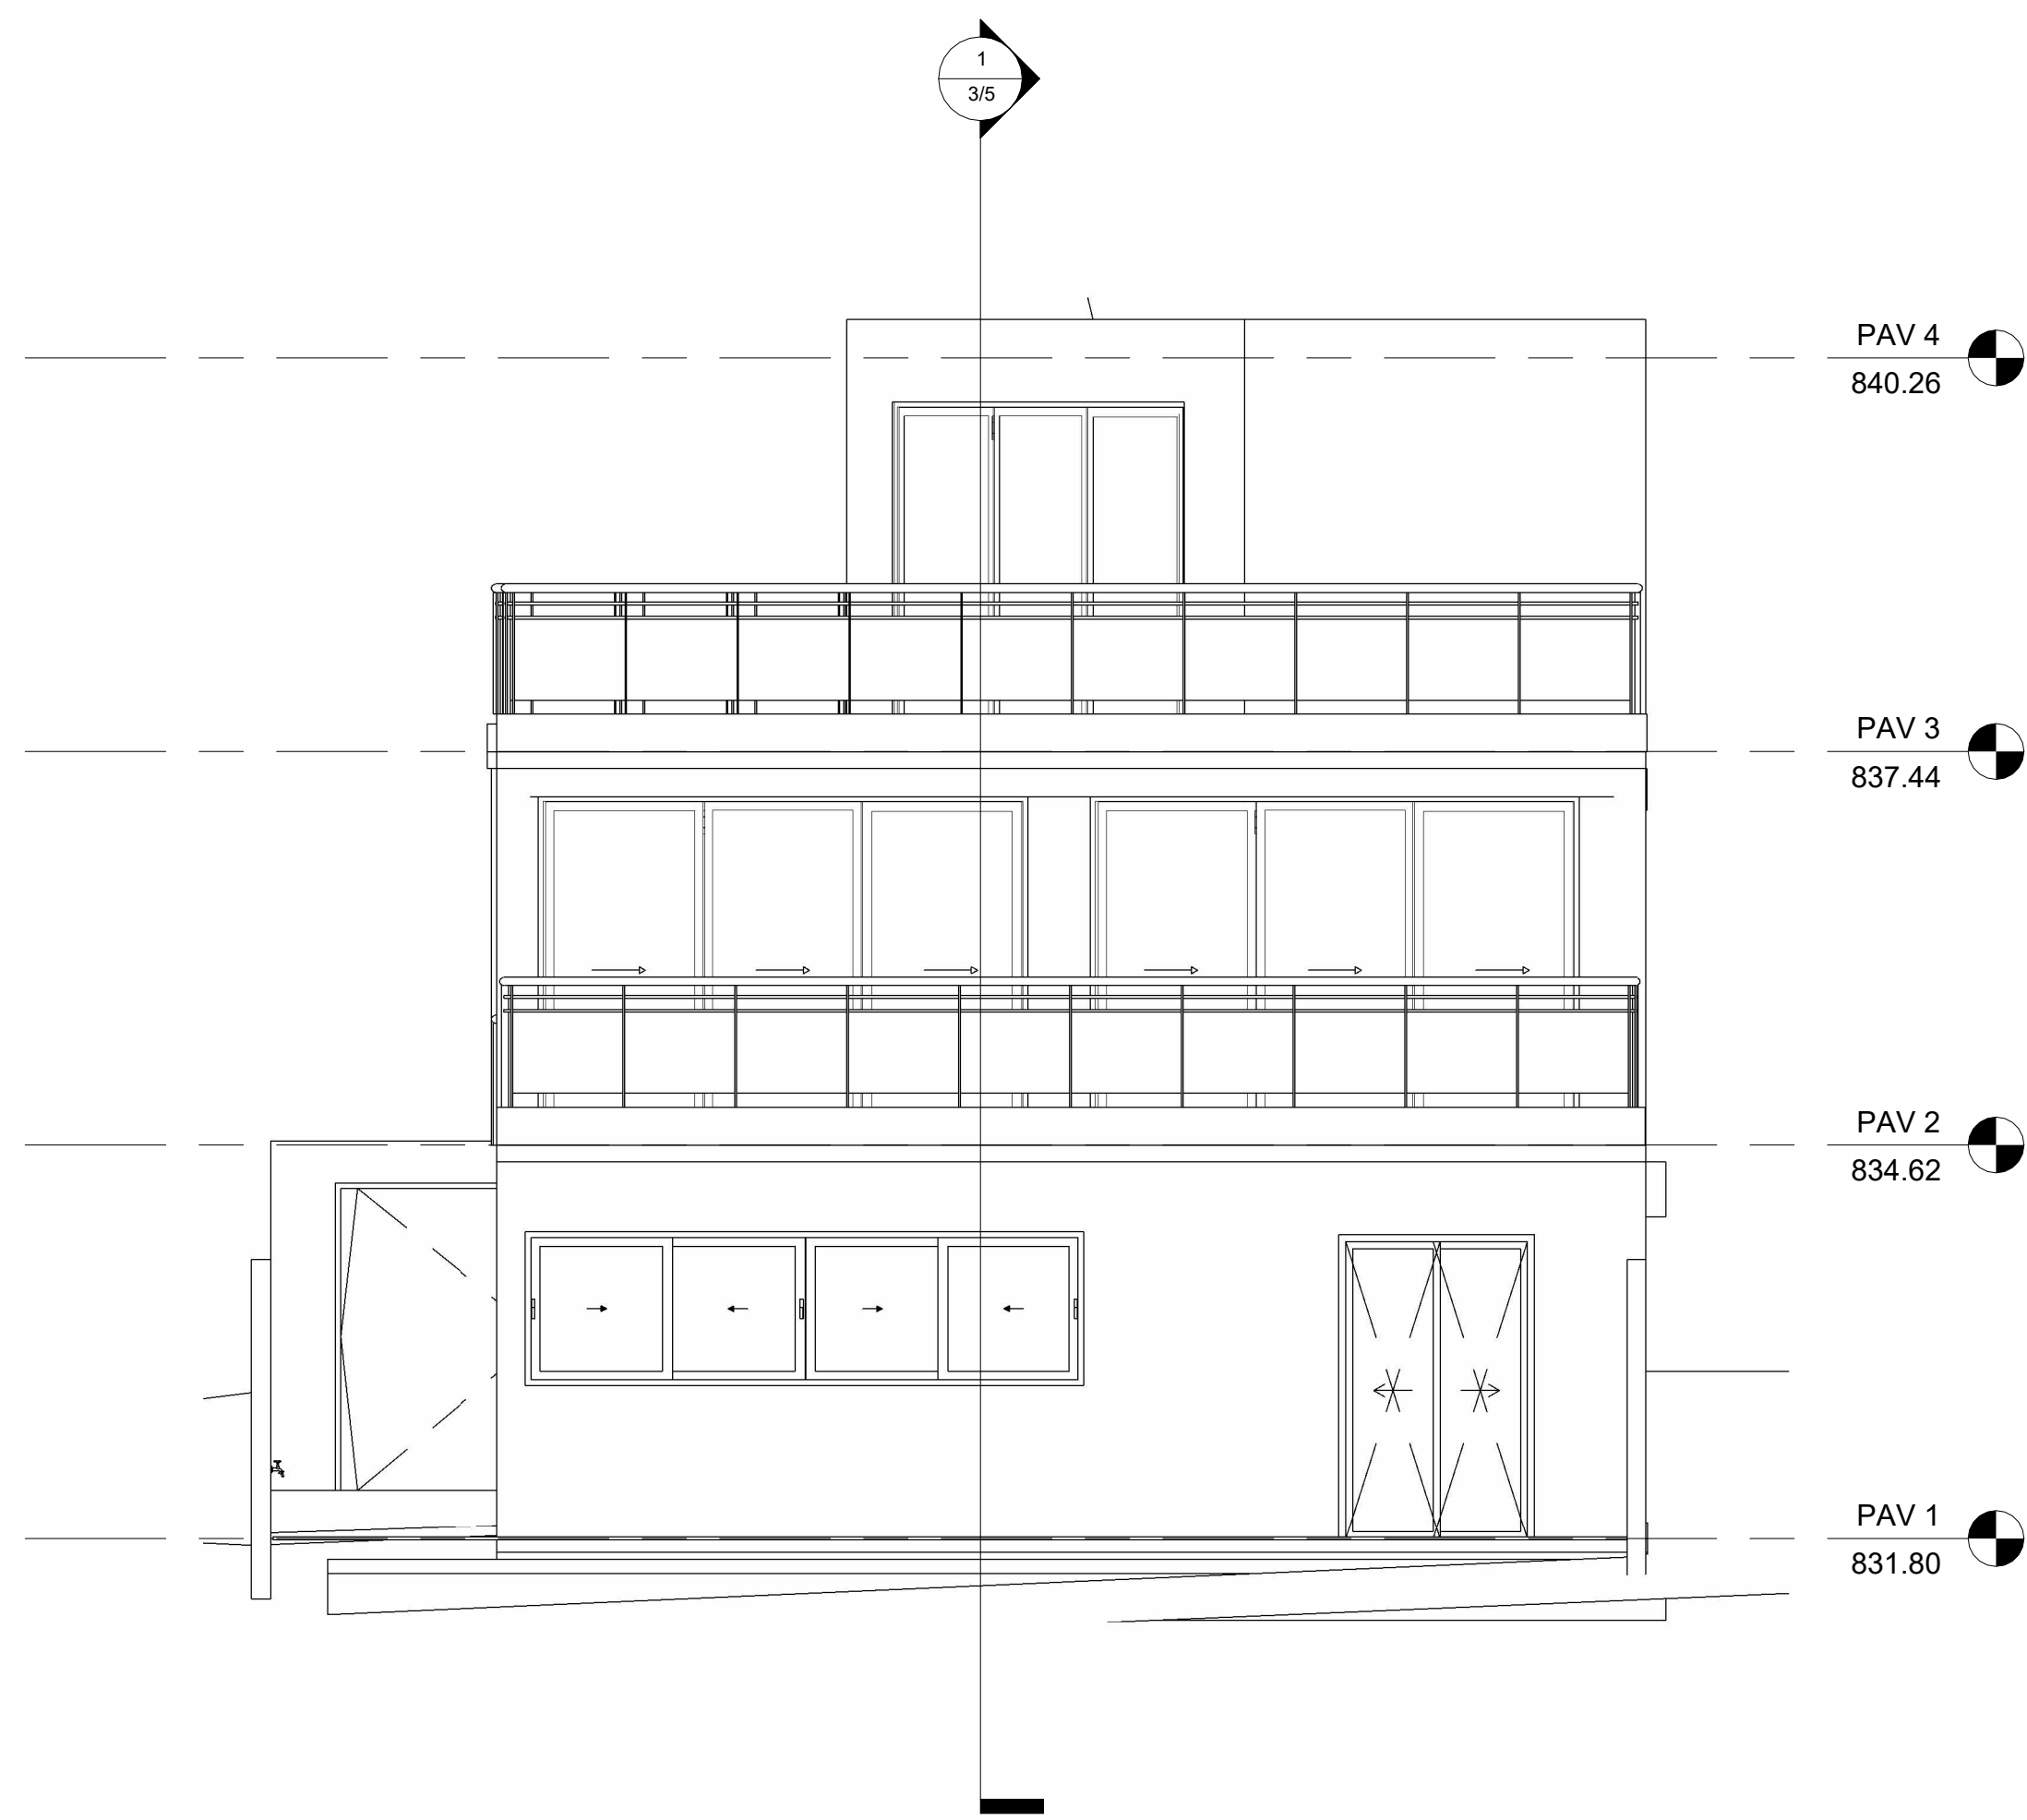


3 Oeste
1 : 50

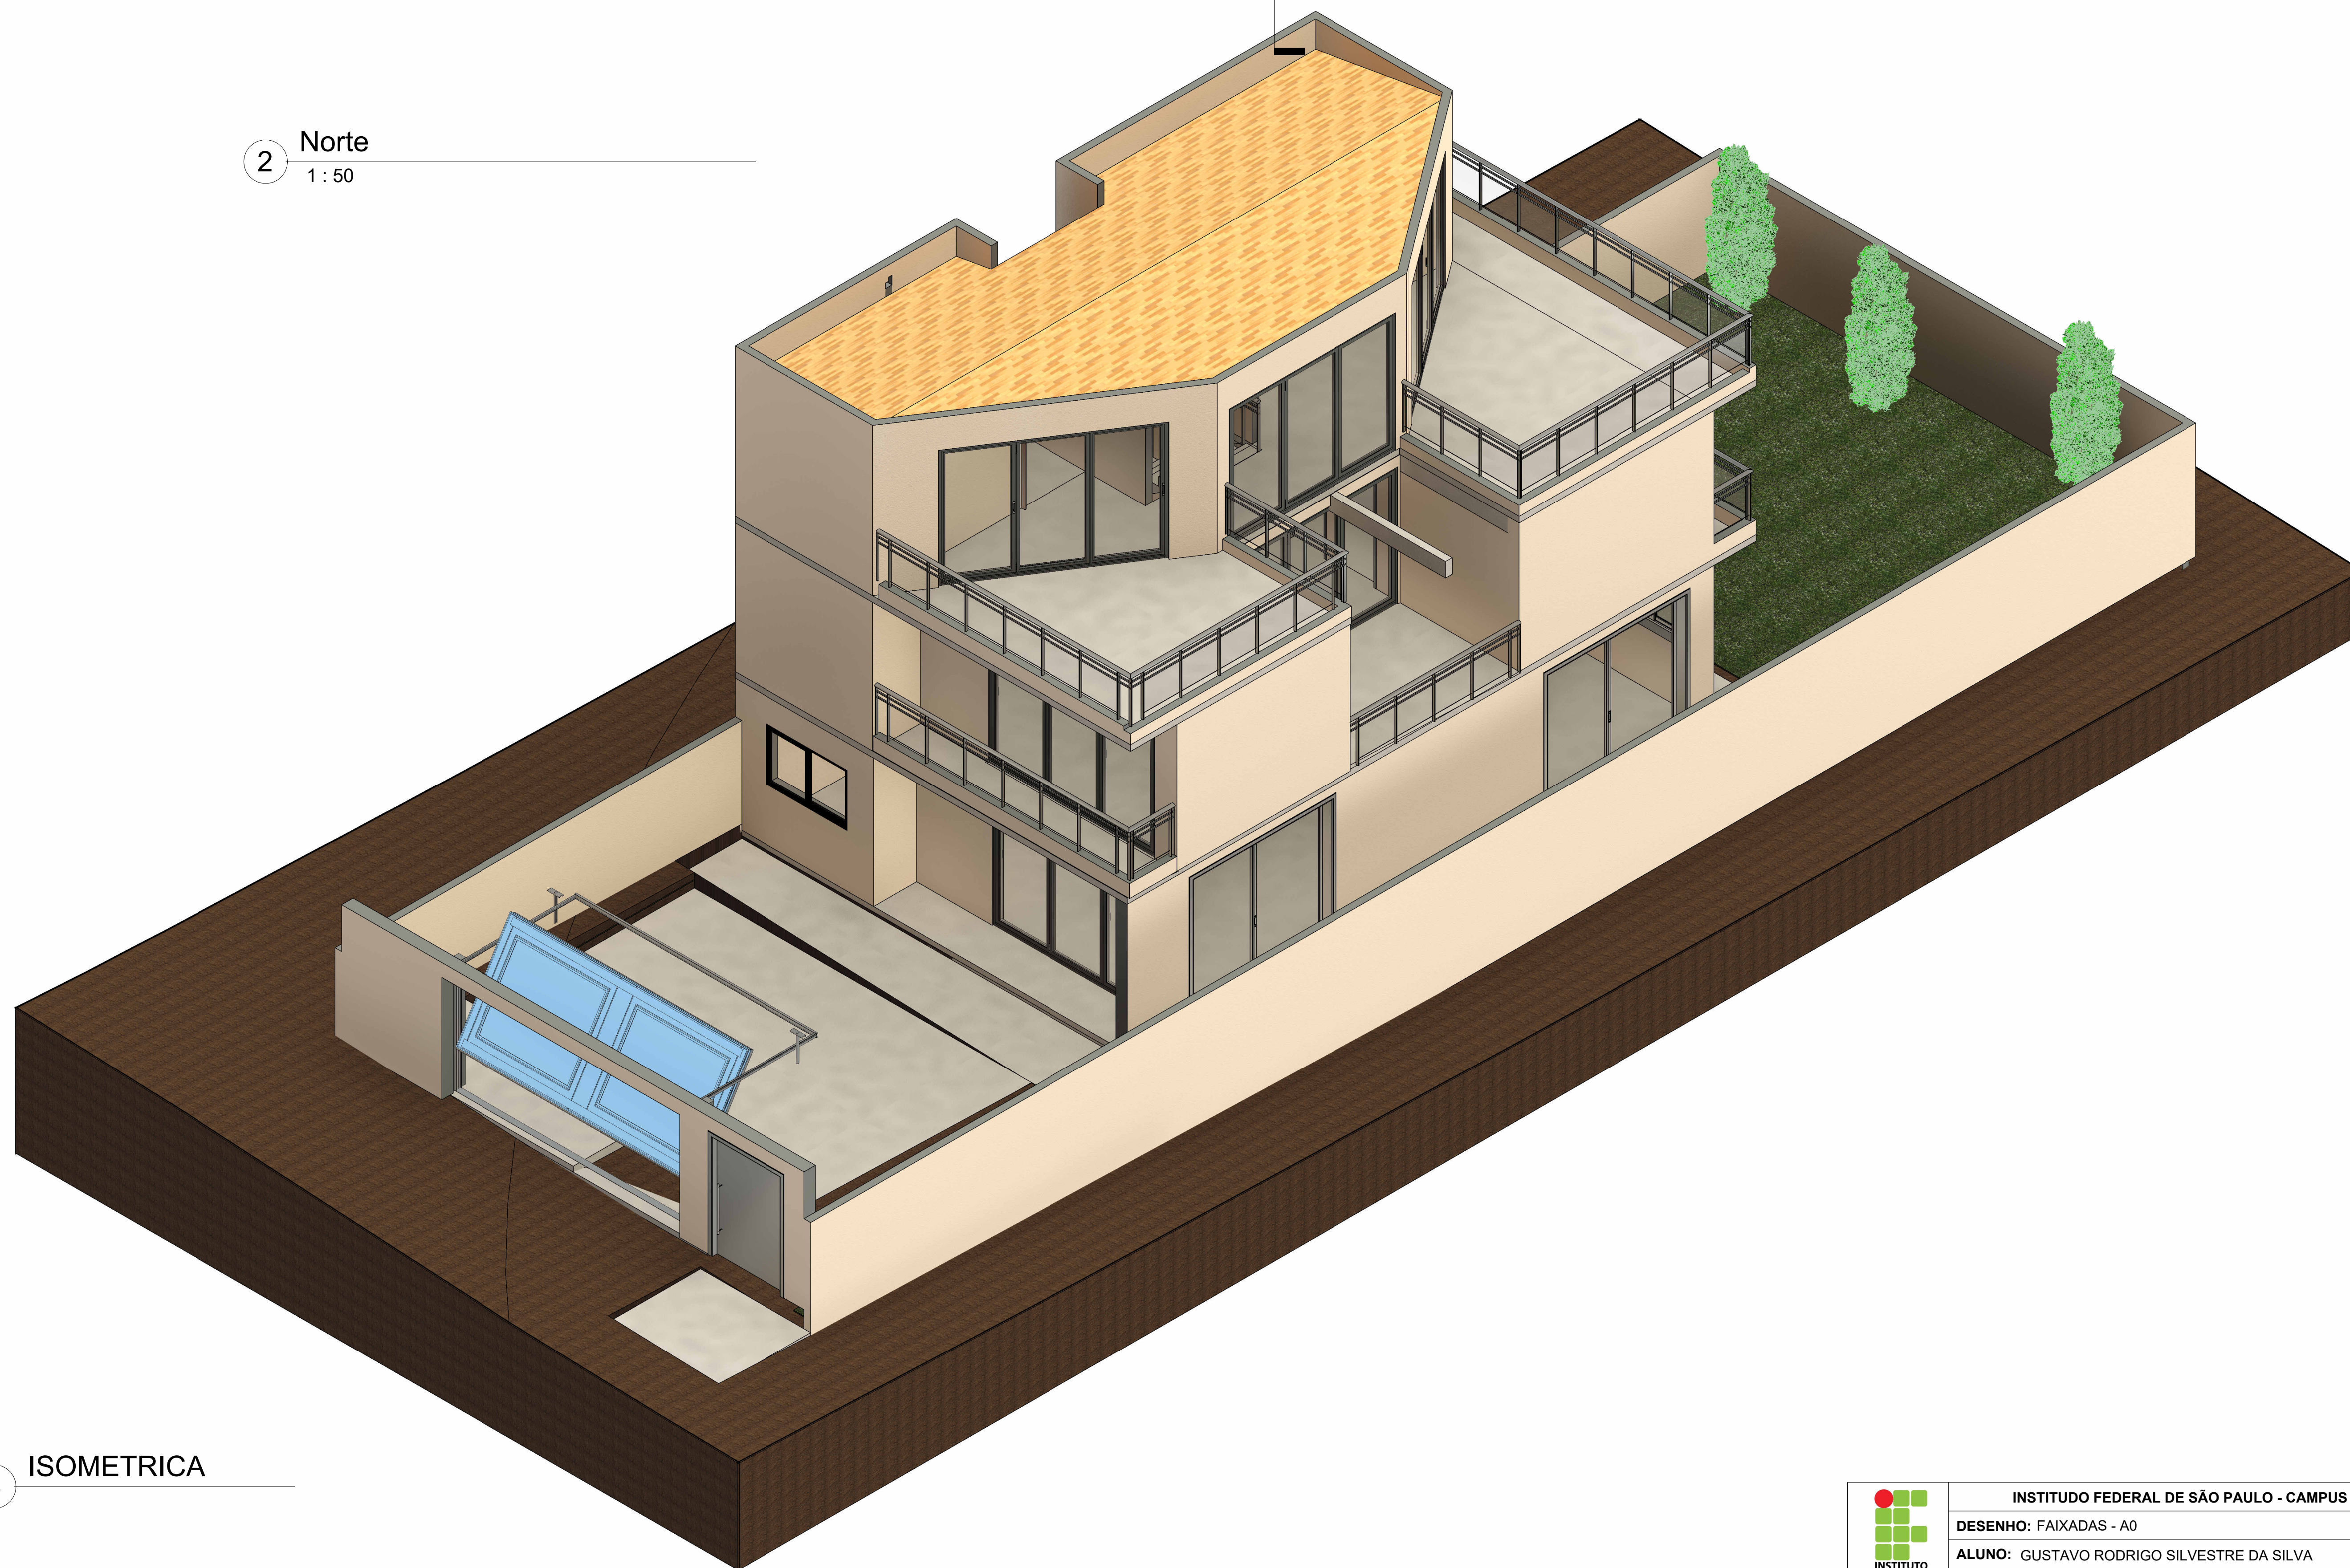


4 ISOMETRICA

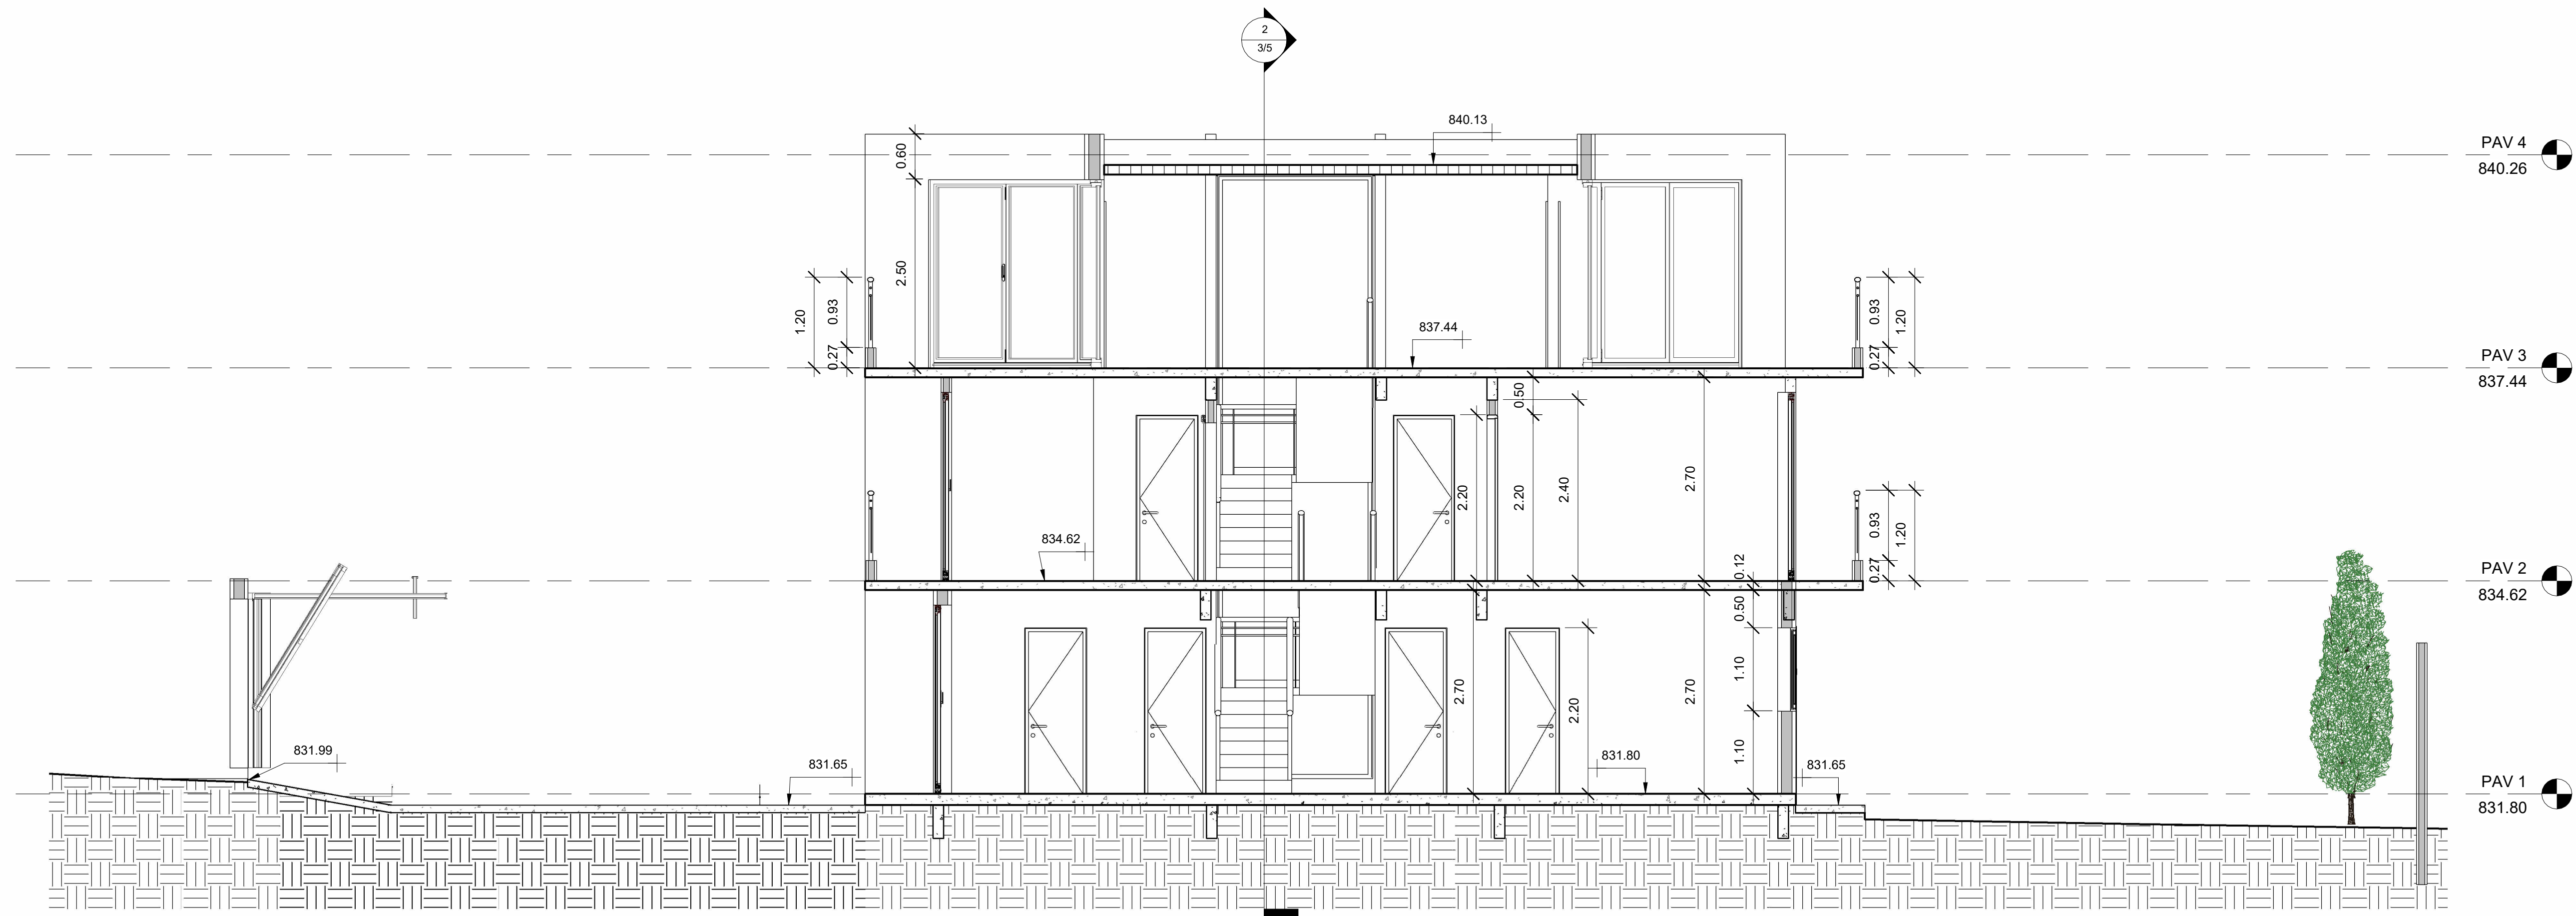


1 CORTE LONGITUDINAL
1 : 50

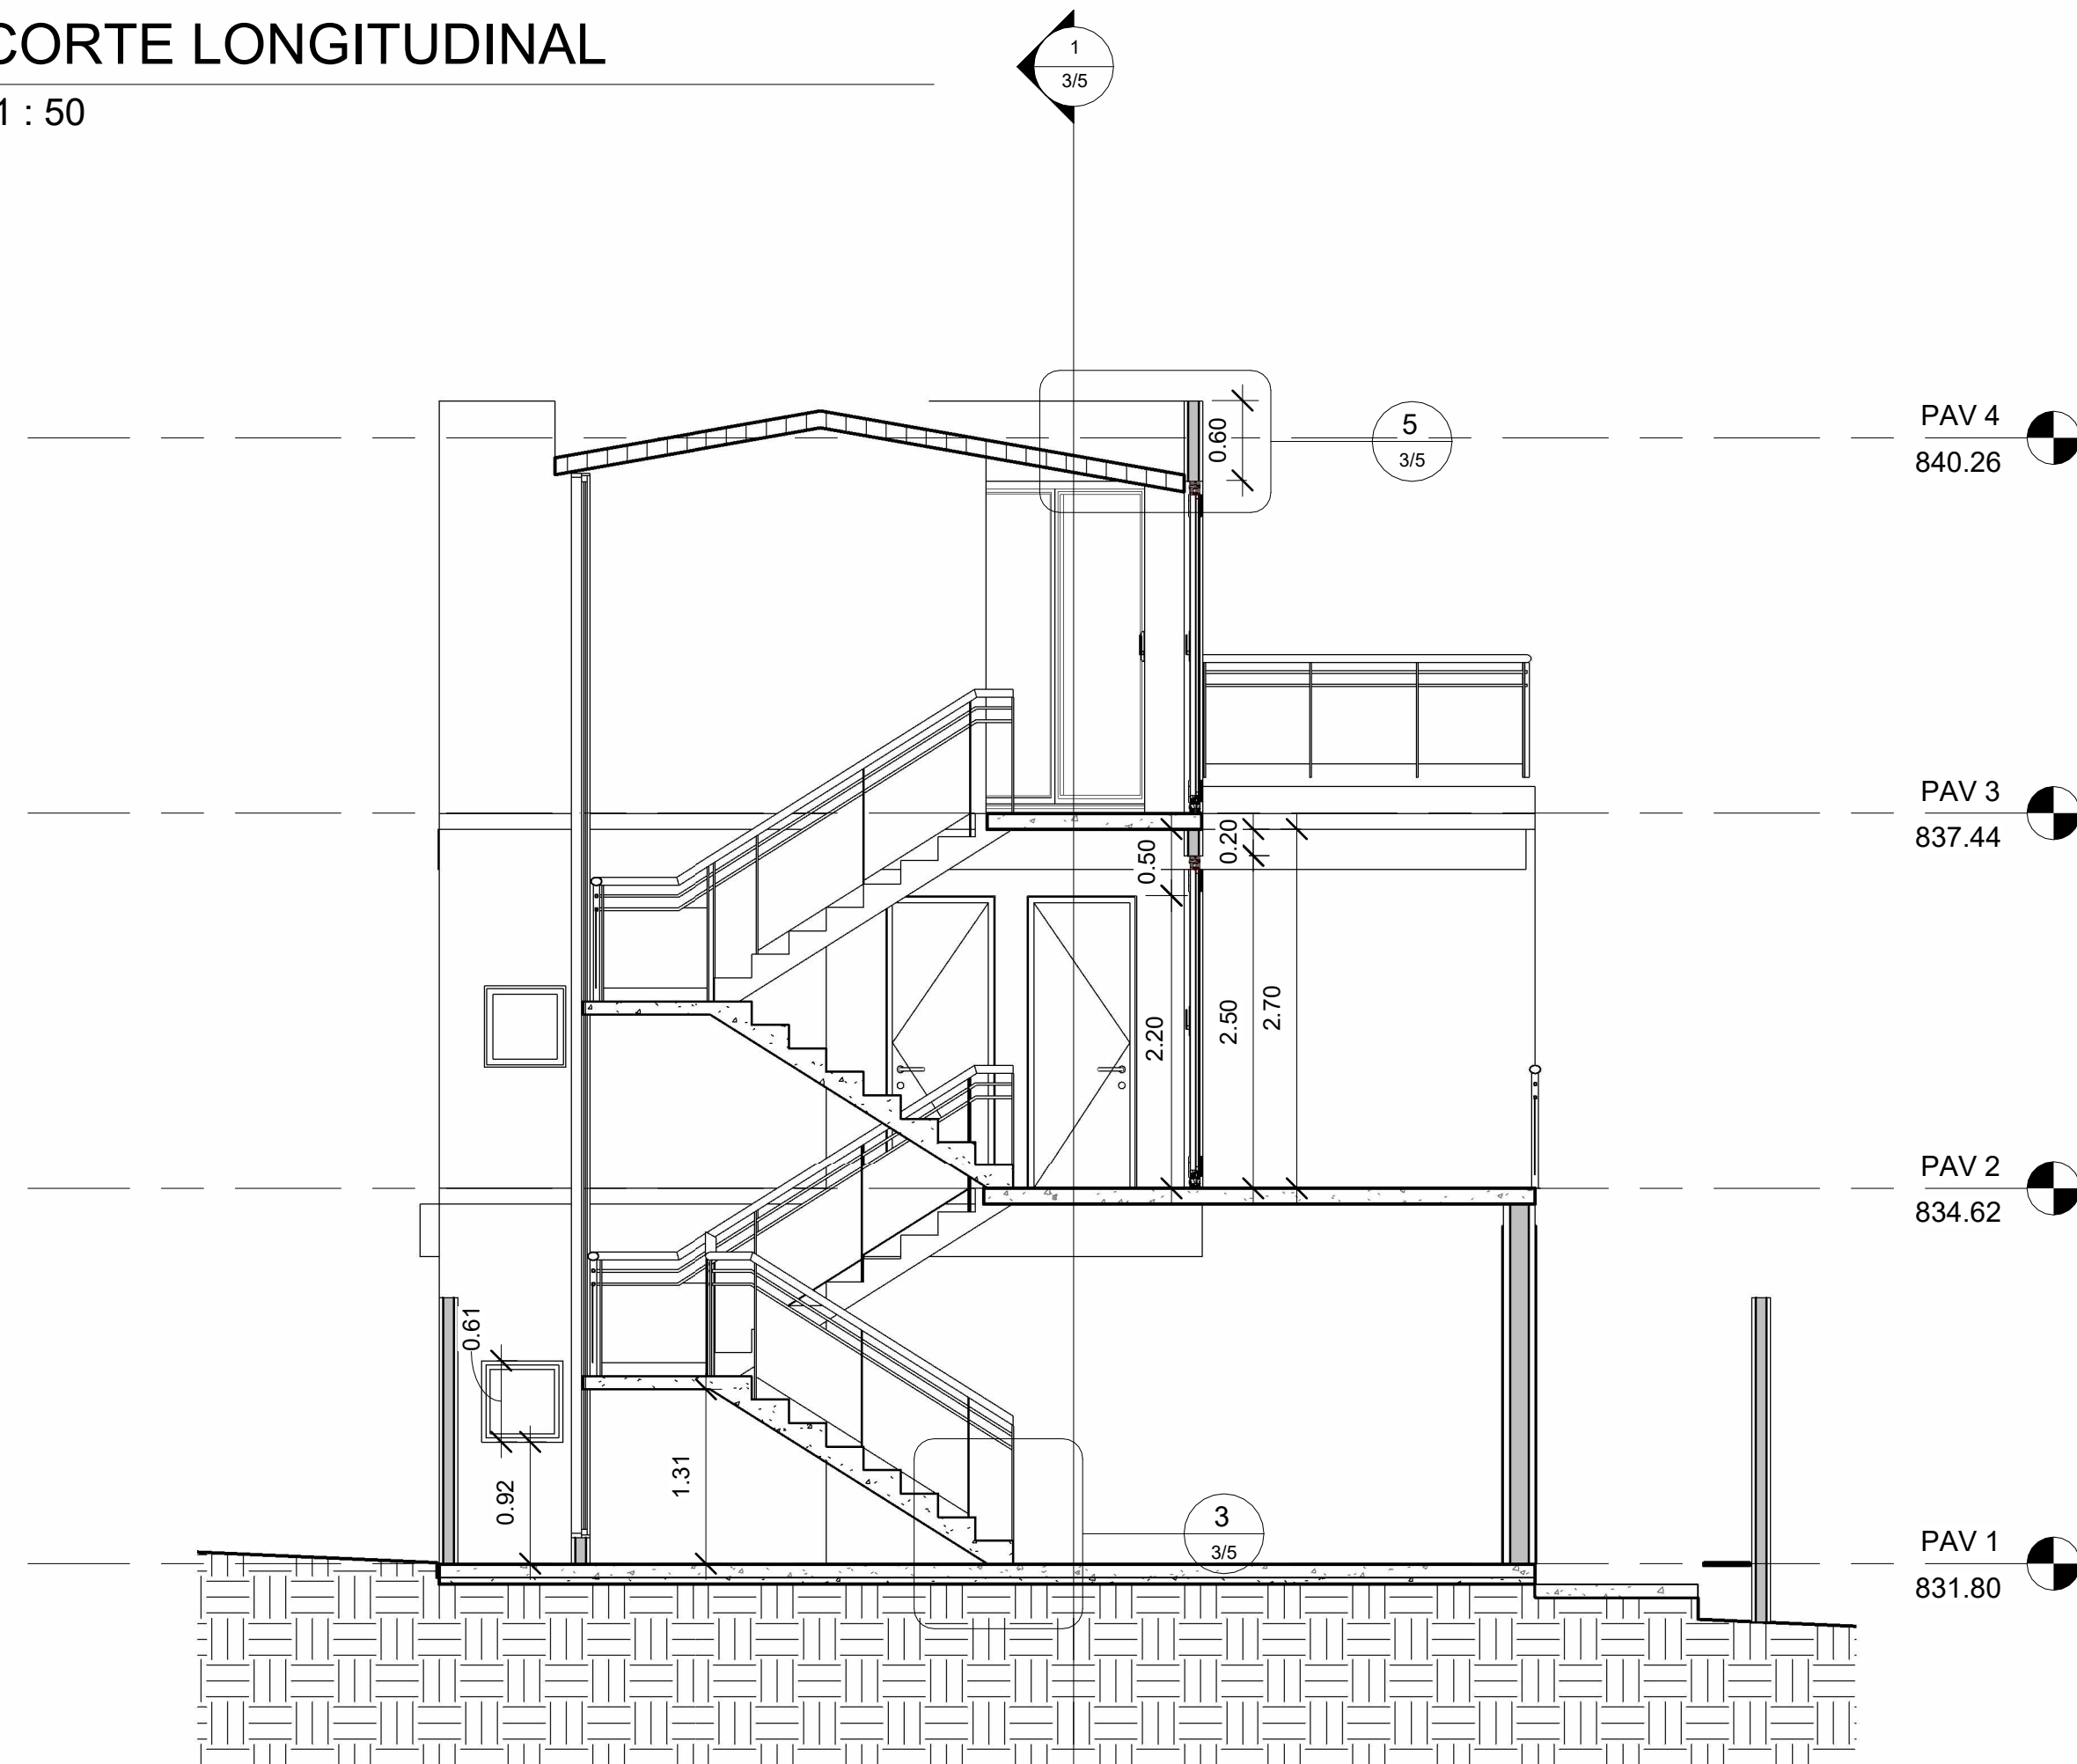


2 CORTE TRANSVERSAL
1 : 50

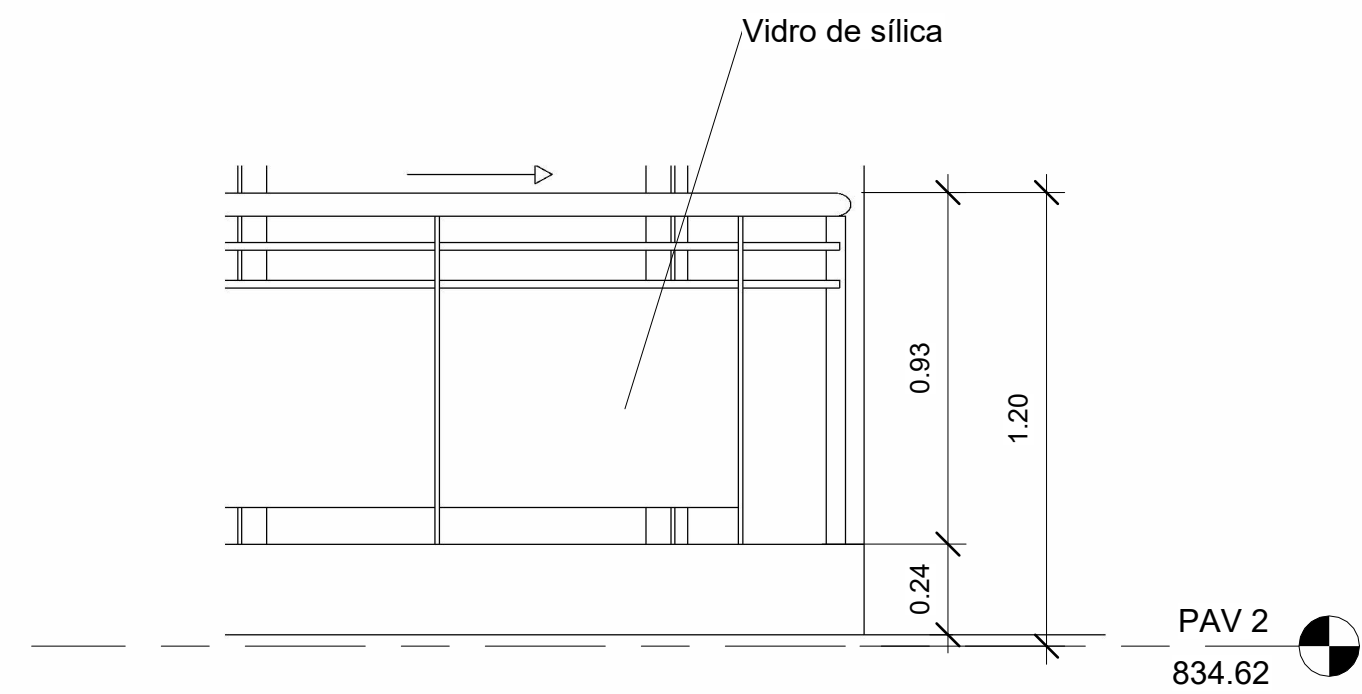


4 DETALHE - GUARDA
CORPO
1 : 20

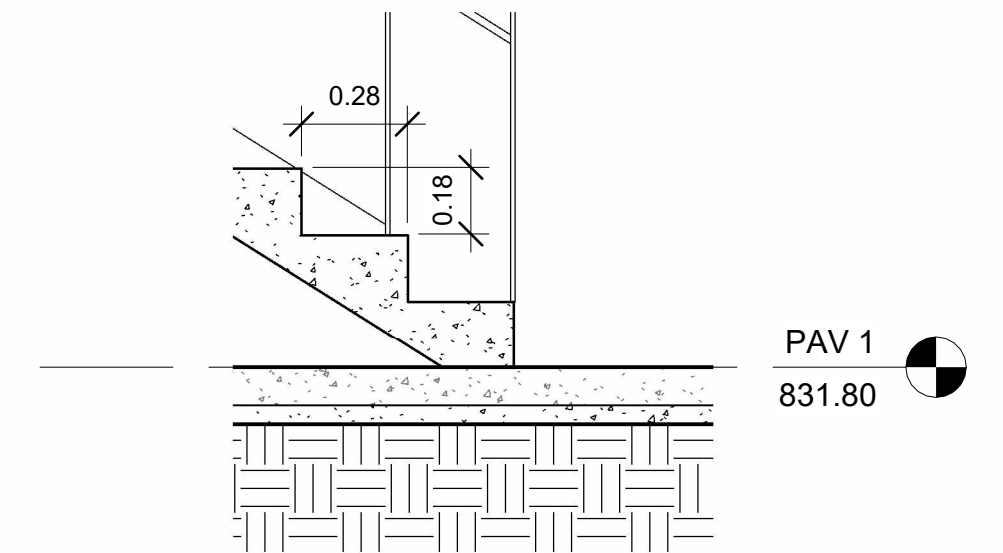


3 DETALHE - ESCADA
1 : 20

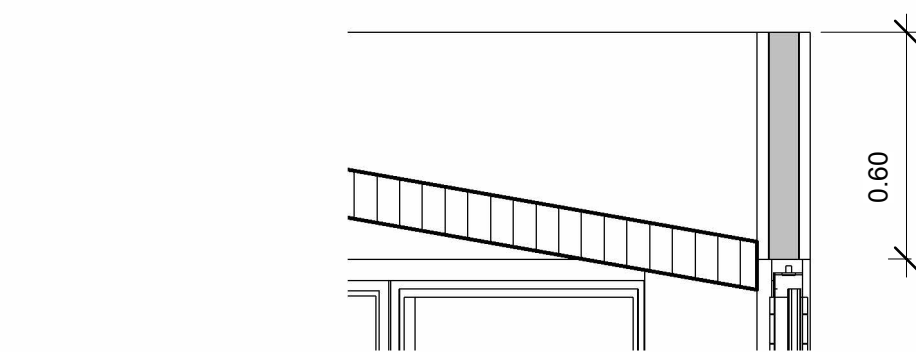


5 DETALHE - COBERTURA
1 : 20

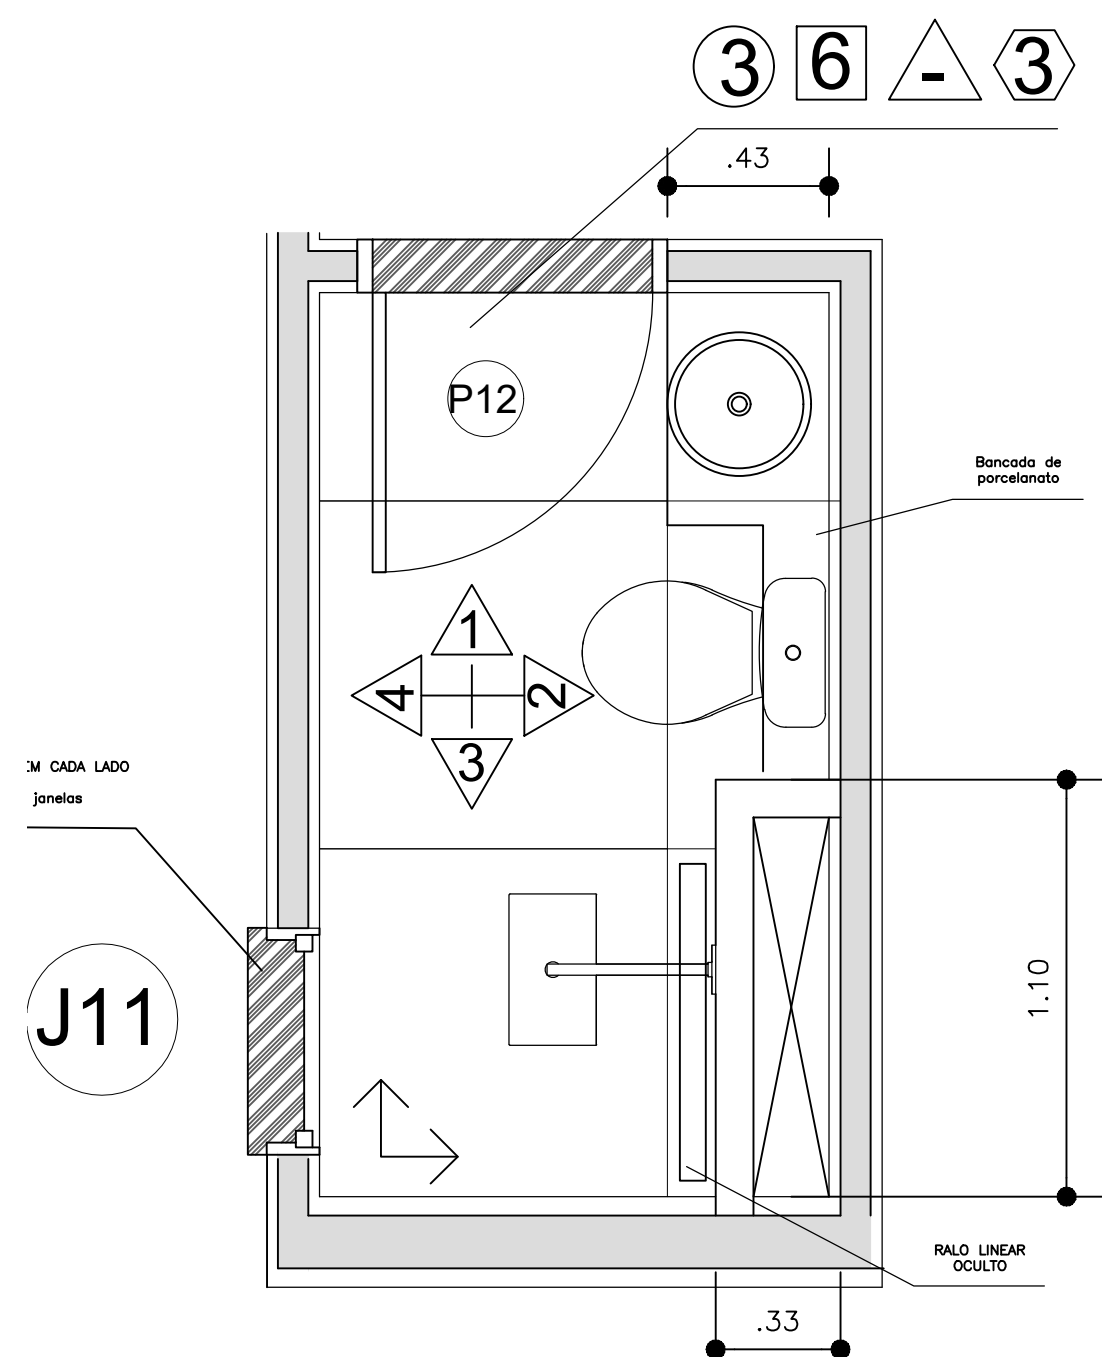


1 BANHEIRO DA SUÍTE
ESCALA: 1:20

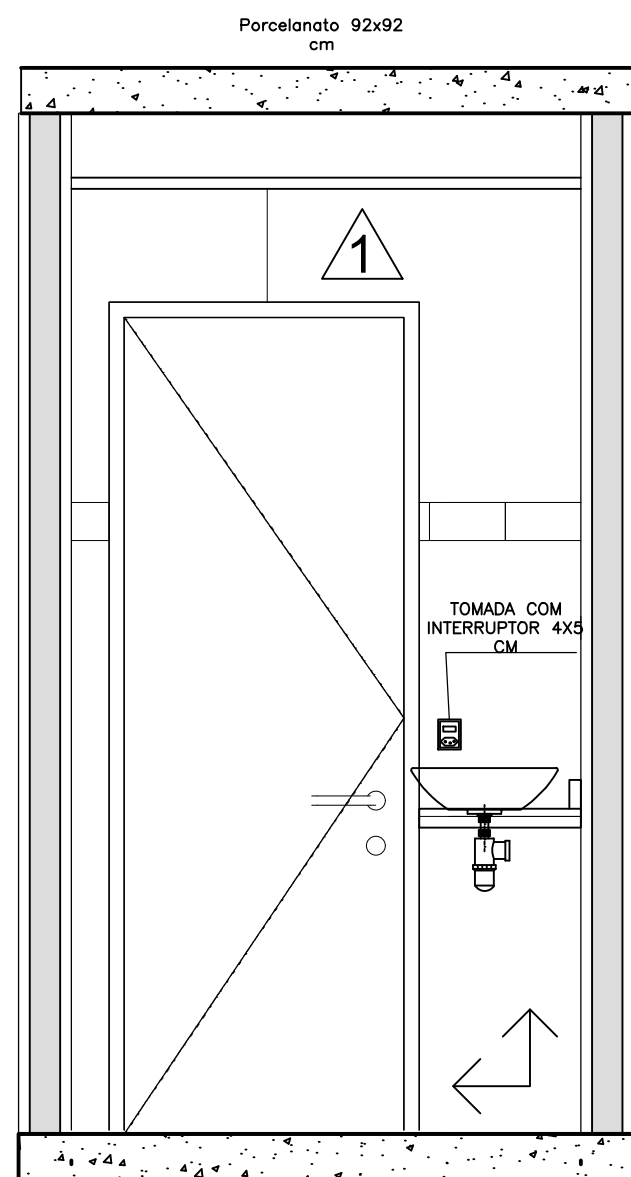


2 ELEVÇÃO 1
ESCALA: 1:20

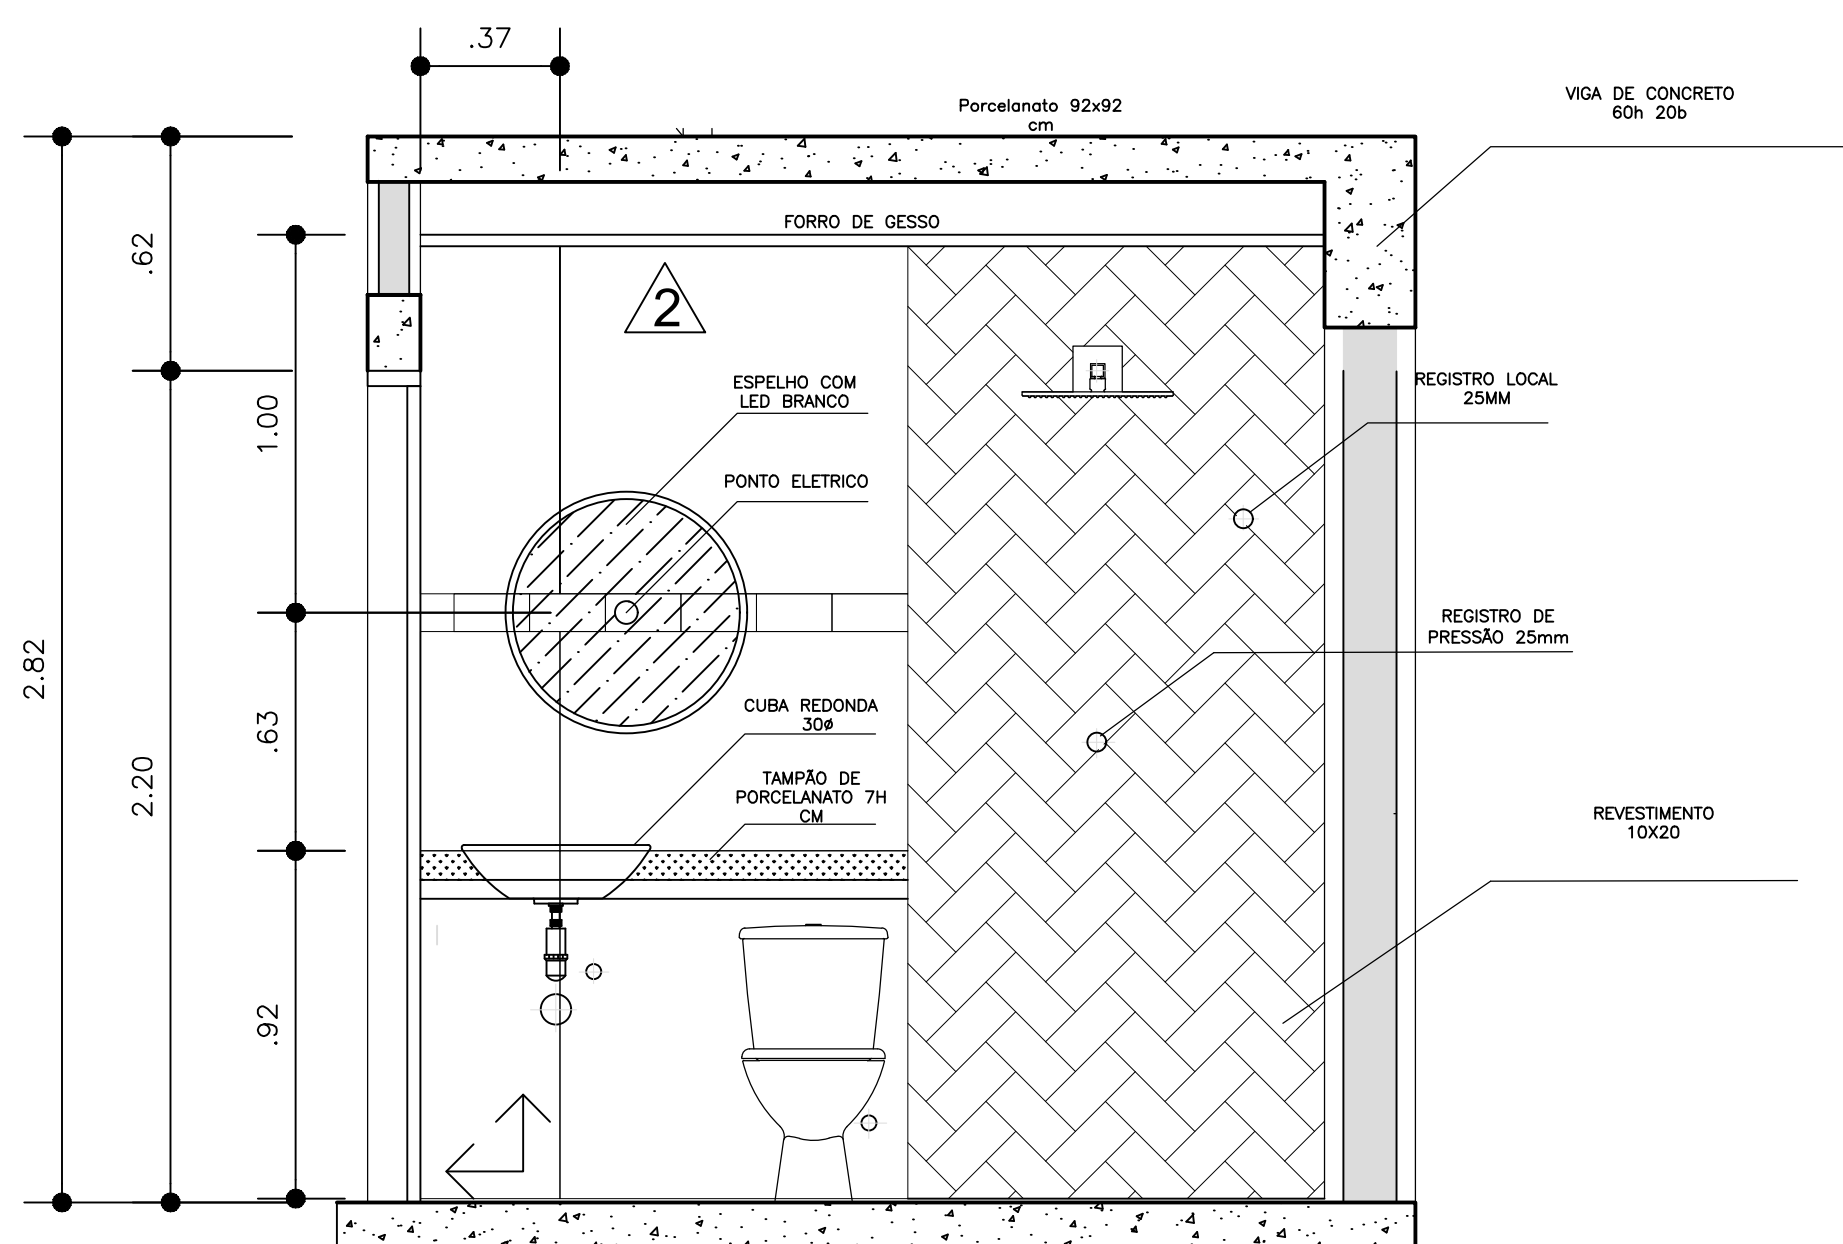


3 ELEVÇÃO 2
ESCALA: 1:20

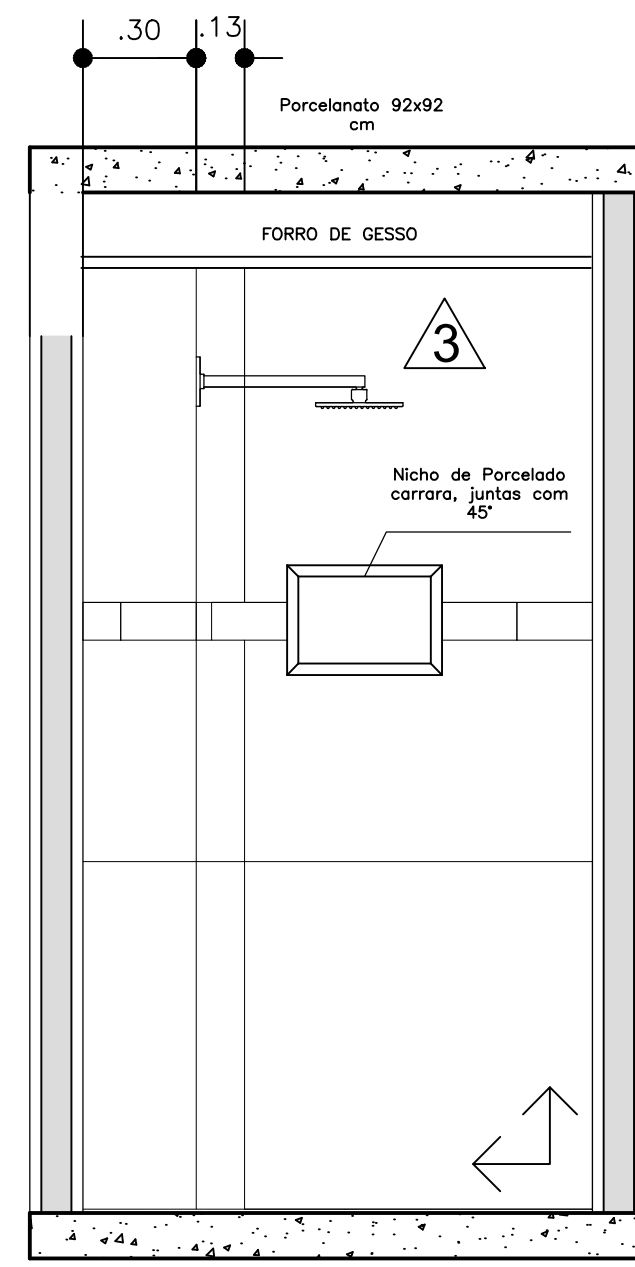


4 ELEVÇÃO 3
ESCALA: 1:20

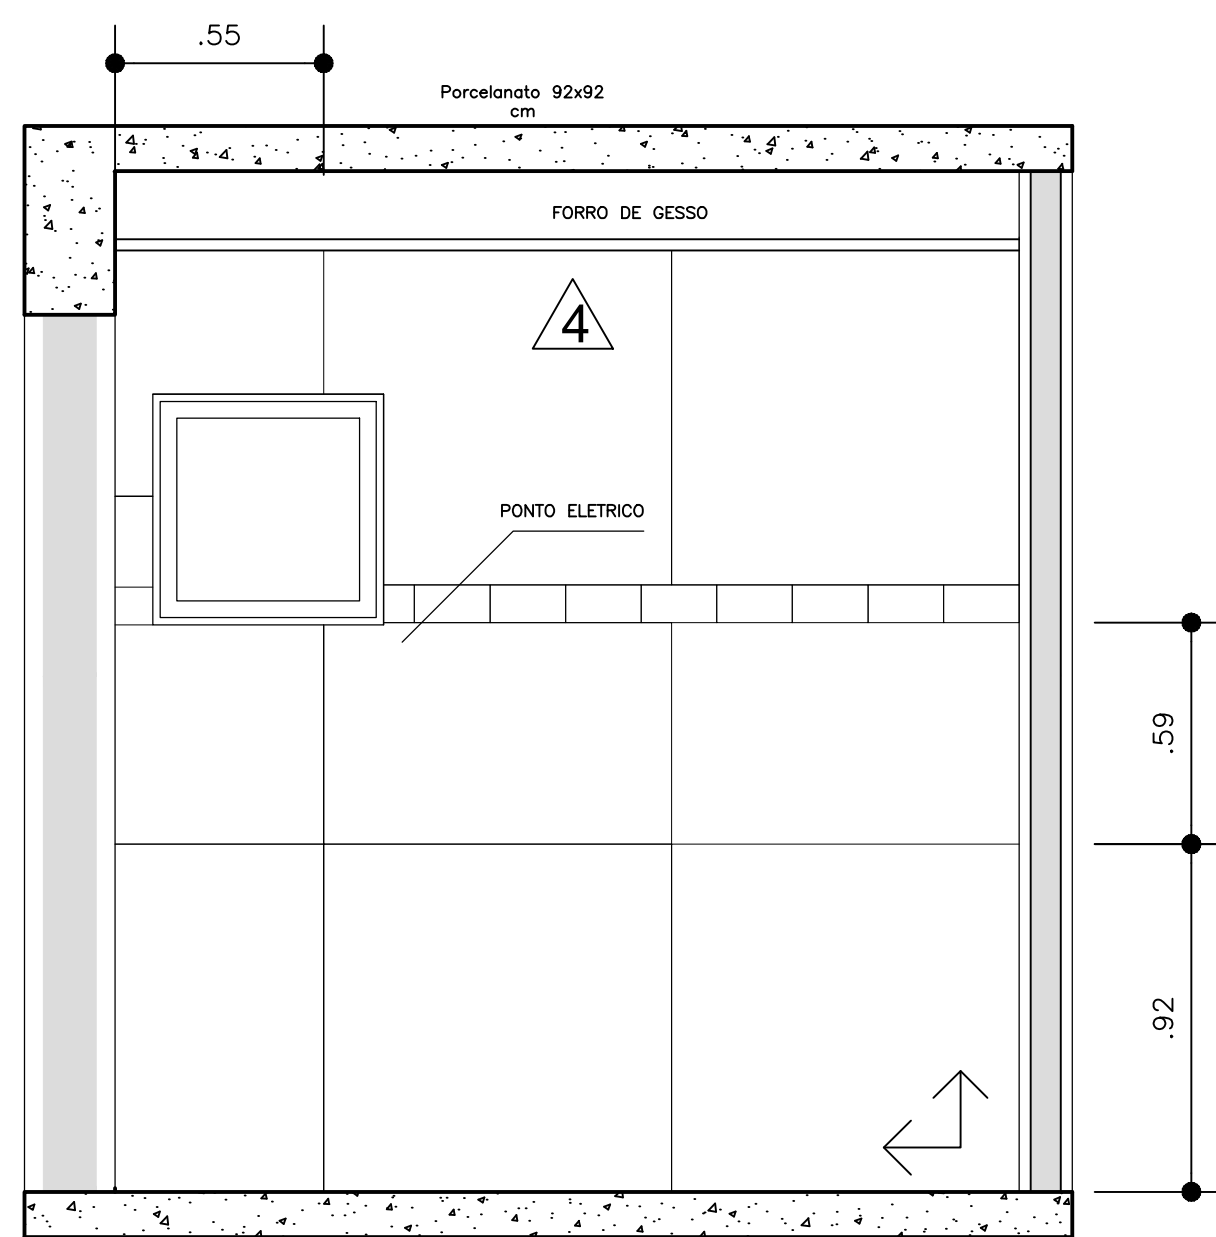

1 ELEVÇÃO 4
ESCALA: 1:50

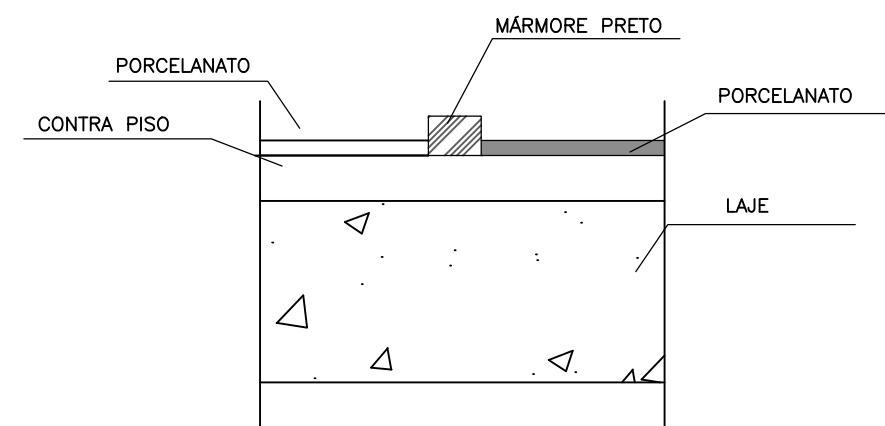

2 ELEVÇÃO 1
ESCALA: 1:20

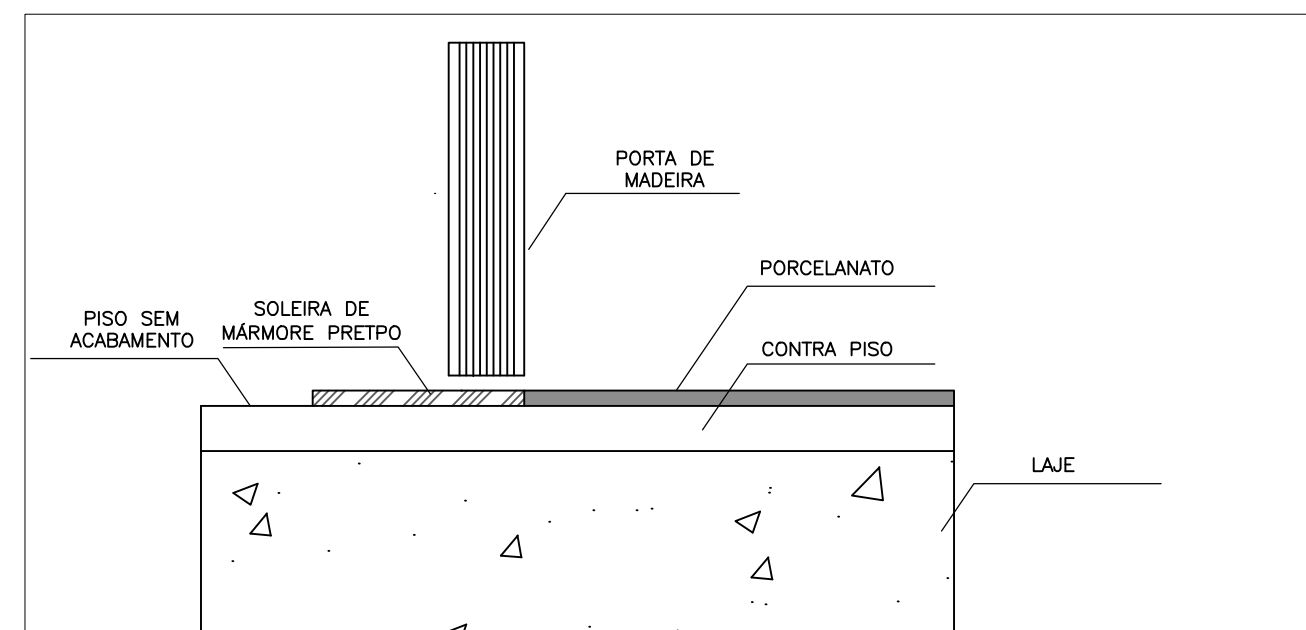

2 ELEVÇÃO 1
ESCALA: 1:20

Tabelas de Metais e louças


Tipo	Marca	Material	Largura bruta	Altura bruta	Quantidade
Culpa	Deca	vidro	0.3	0.30	1
Torneira	Torneira	Aço	0,25	0.20	1
Ralo	Pingo Casa	Inox	0,10	1	1
Registro de Pressao	Registro de Pressao	Aço	0,025Ø	0	1
Registro de Gaveta	Registro de Gaveta	Aço	0.025Ø	0	1
Bacia Sanitaria	Deca	Axis	0.68	0.78	1

Tabelas de Esquadrias - Portas

Marca de tipo	Material	Largura bruta	Altura bruta	Quantidade
P03	Madeira	0.72	2.2	4



Tabela de janela

Comentário s de tipos	Marca de tipo	Largura bruta	Altura bruta	Altura do peitoril	Material	Vidro	Modelo
Banh. Superior	J11	0.80	0.60	1.50	Alumínio	Vidro, fosco	MAXIM-AR

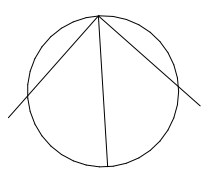


RUA
01

RUA
01

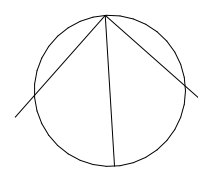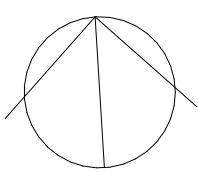


RUA
01

RUA
01

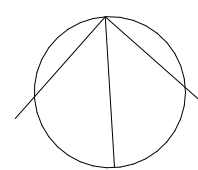

RUA
03

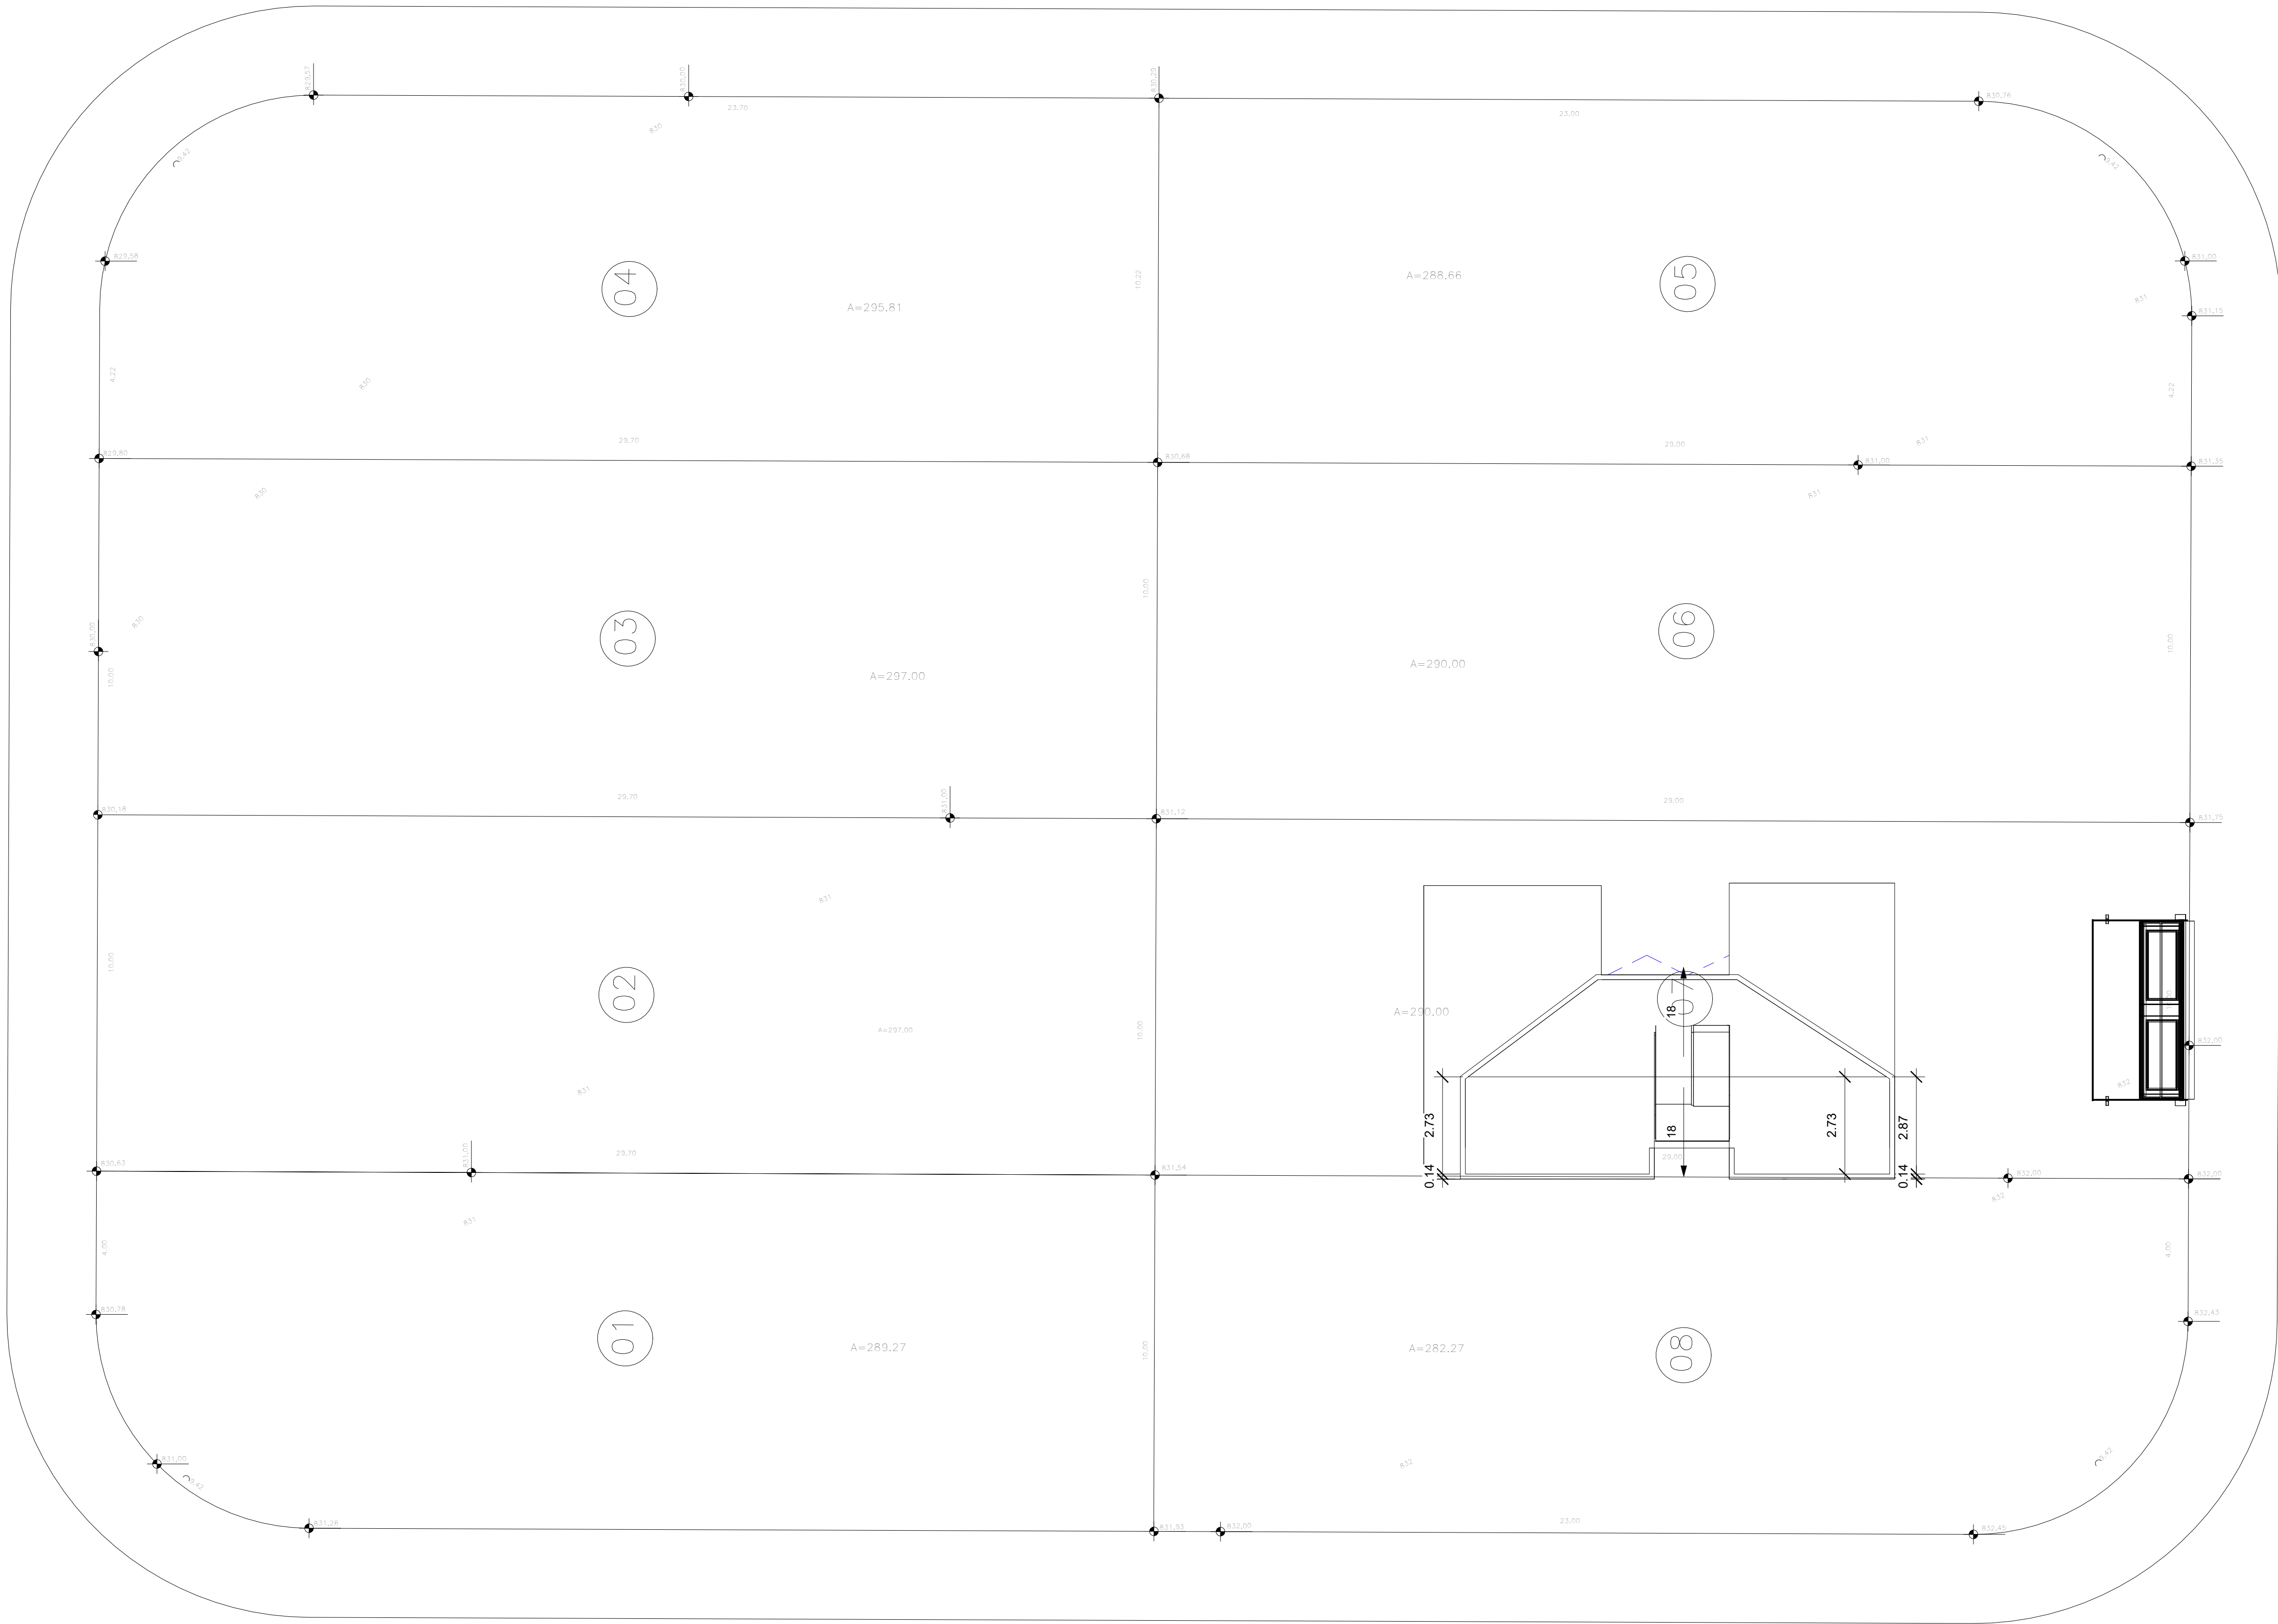

1






PAV 4 Copiar 1
1 : 100

RUA
5


RUA
5



INSTITUTO FEDERAL DE SÃO PAULO - CAMPUS SP		
DESENHO: IMPLANTAÇÃO - QUADRA		
ALUONO: GUSTAVO RODRIGO SILVESTRE DA SILVA	PRANCHA 5/7	
DOCENTE: LÉTICIA - ELIANE	DISCIPLINA: PJIU4	

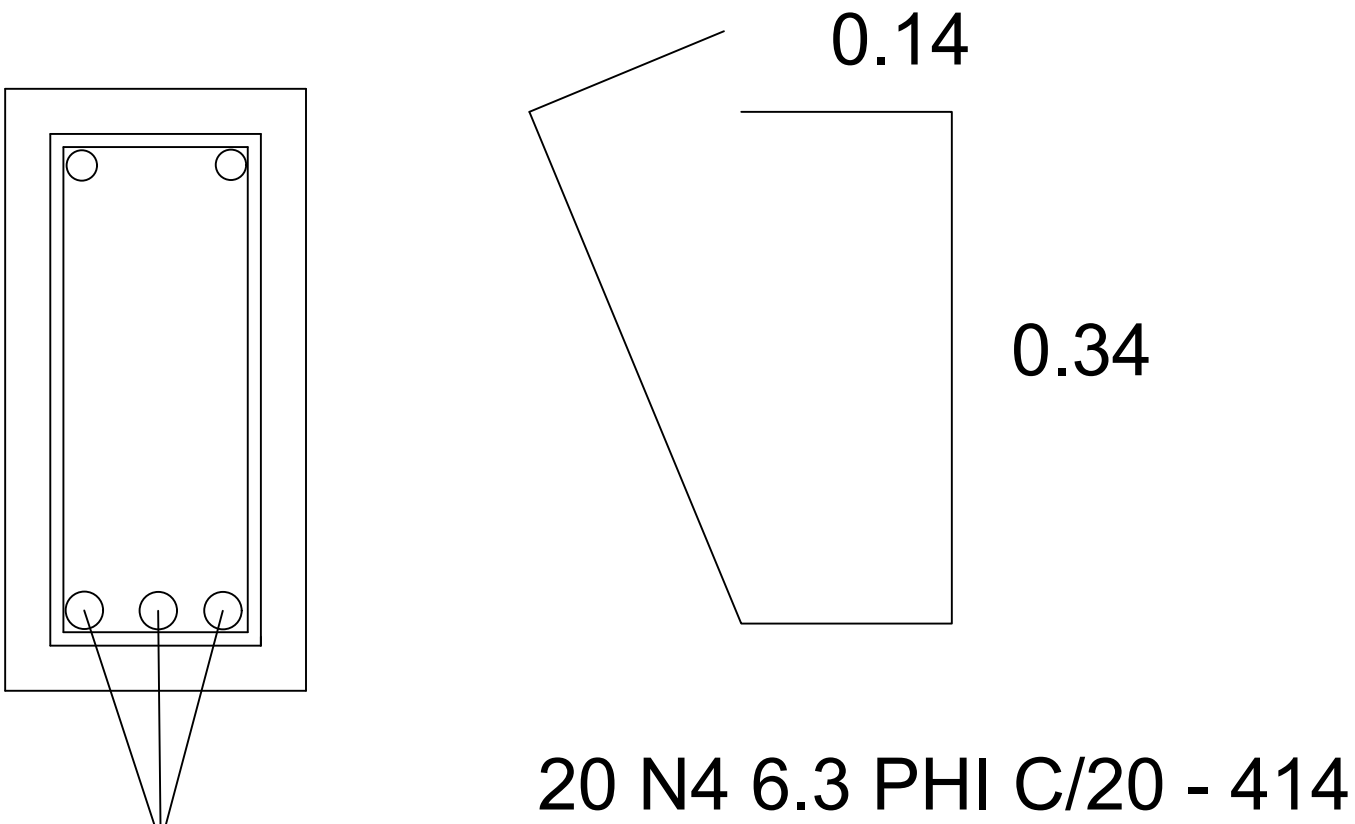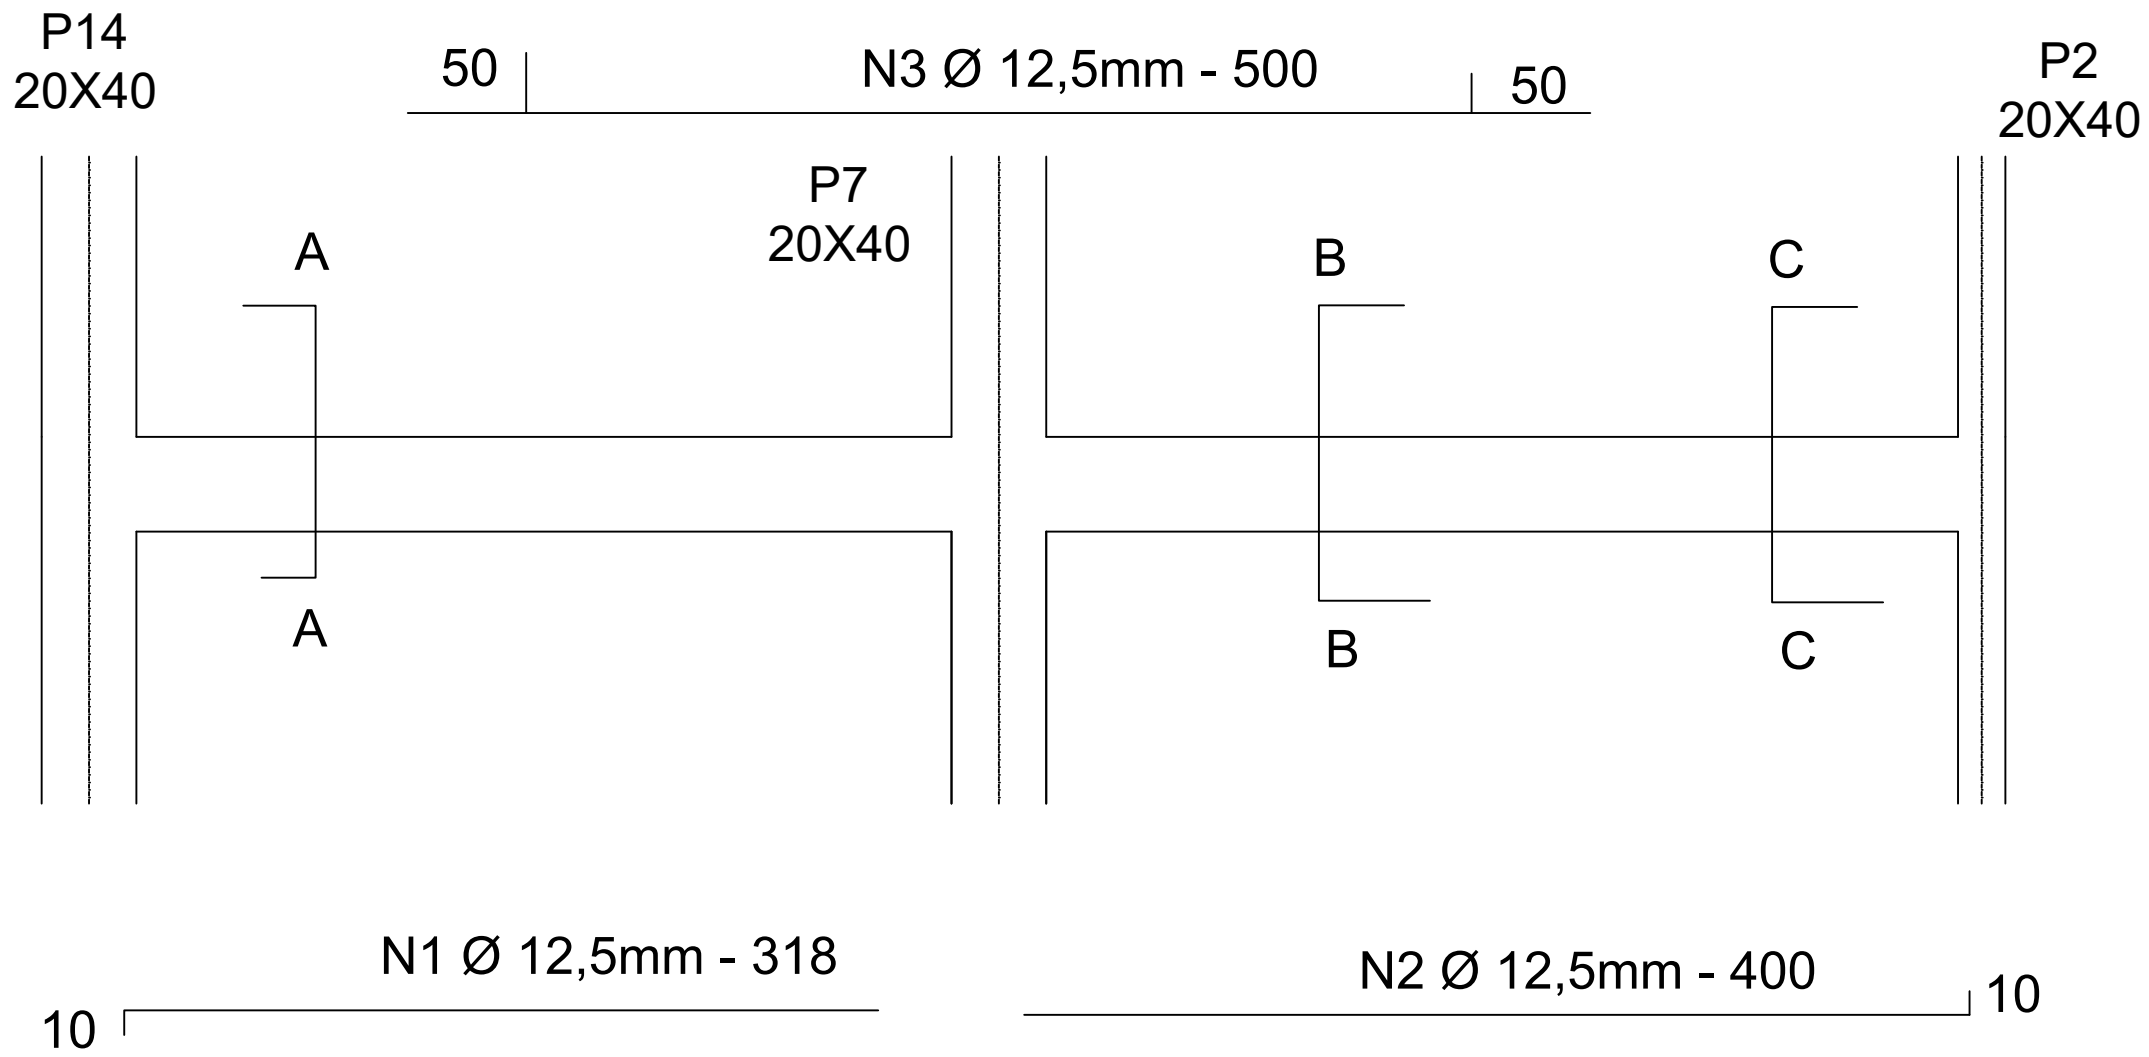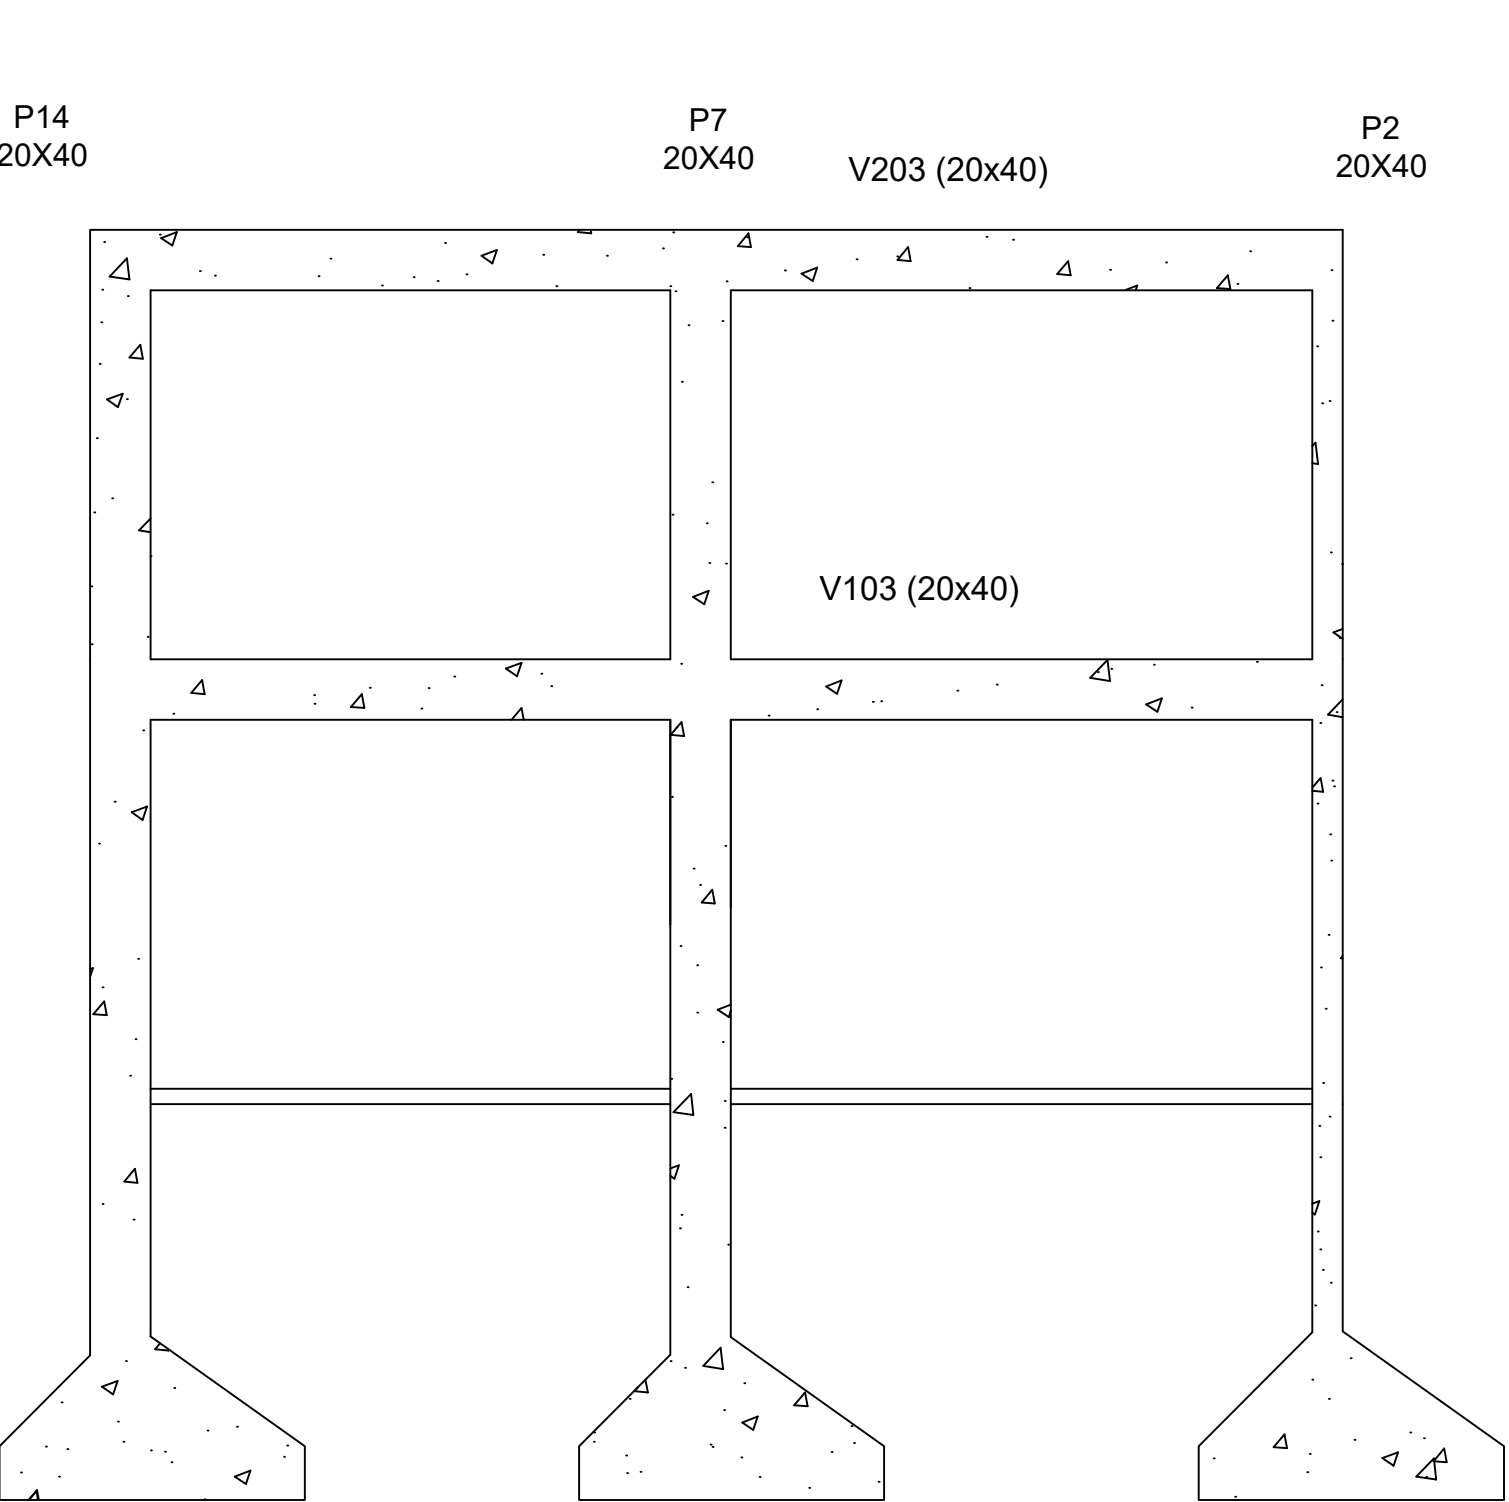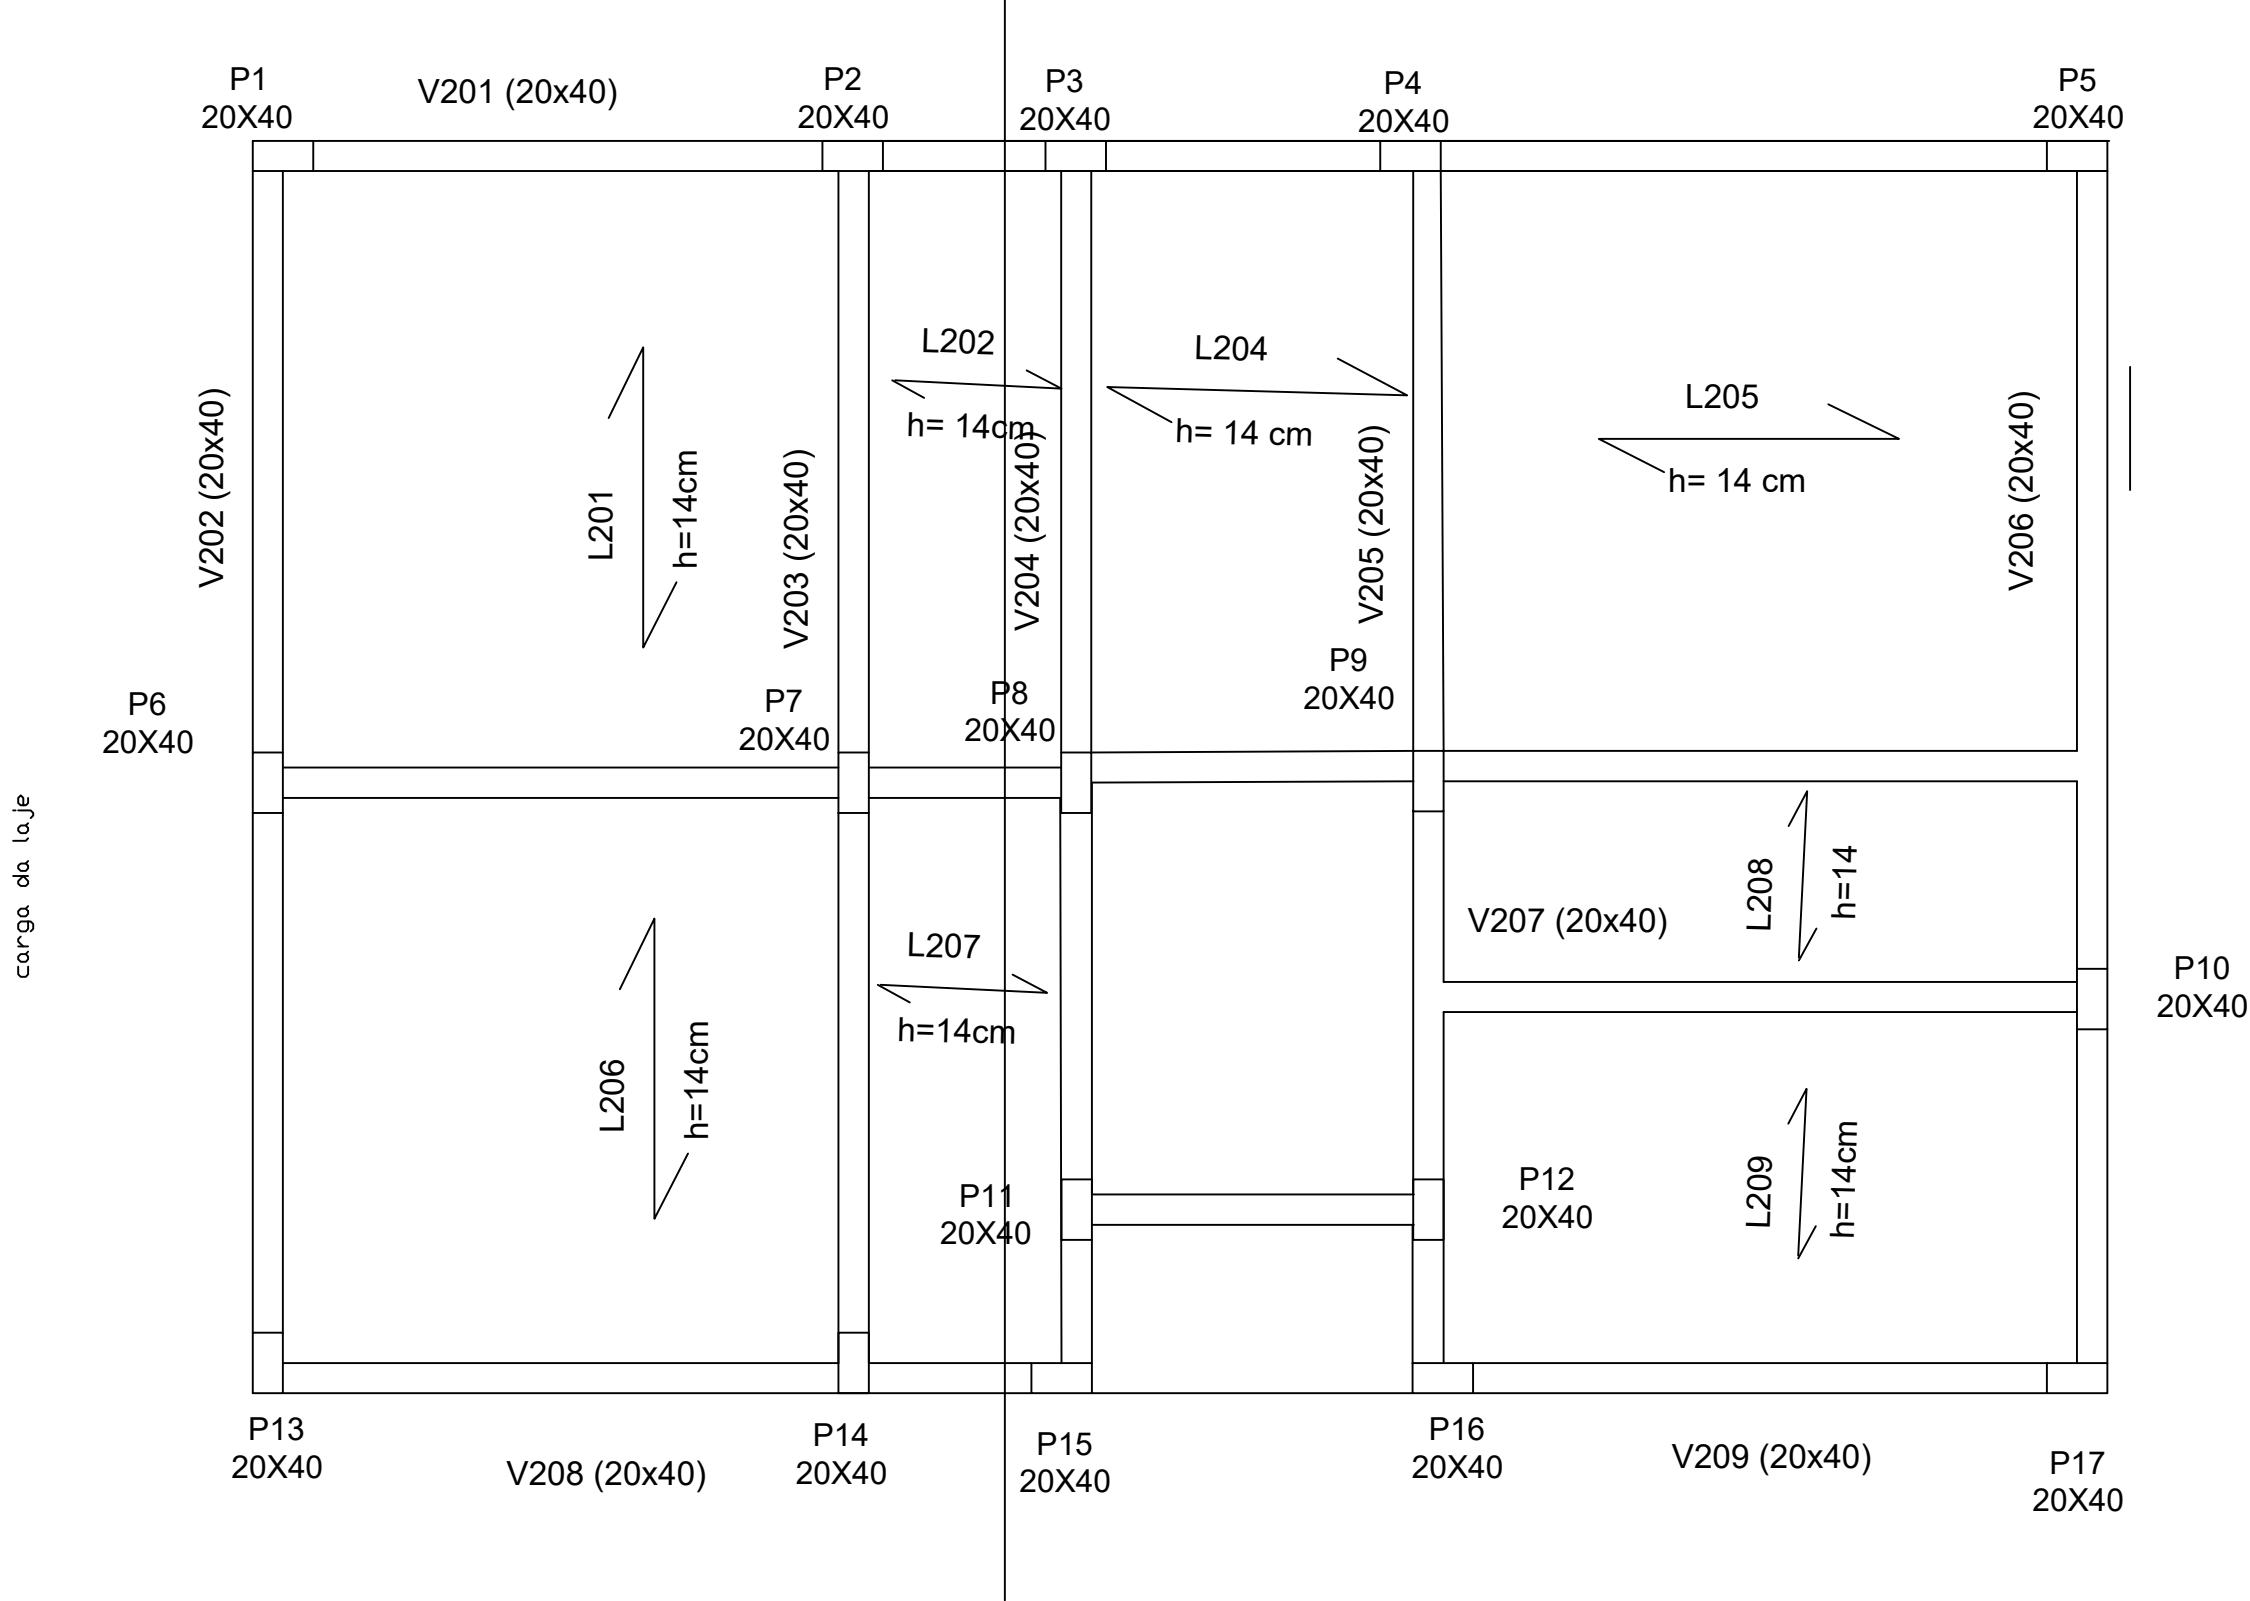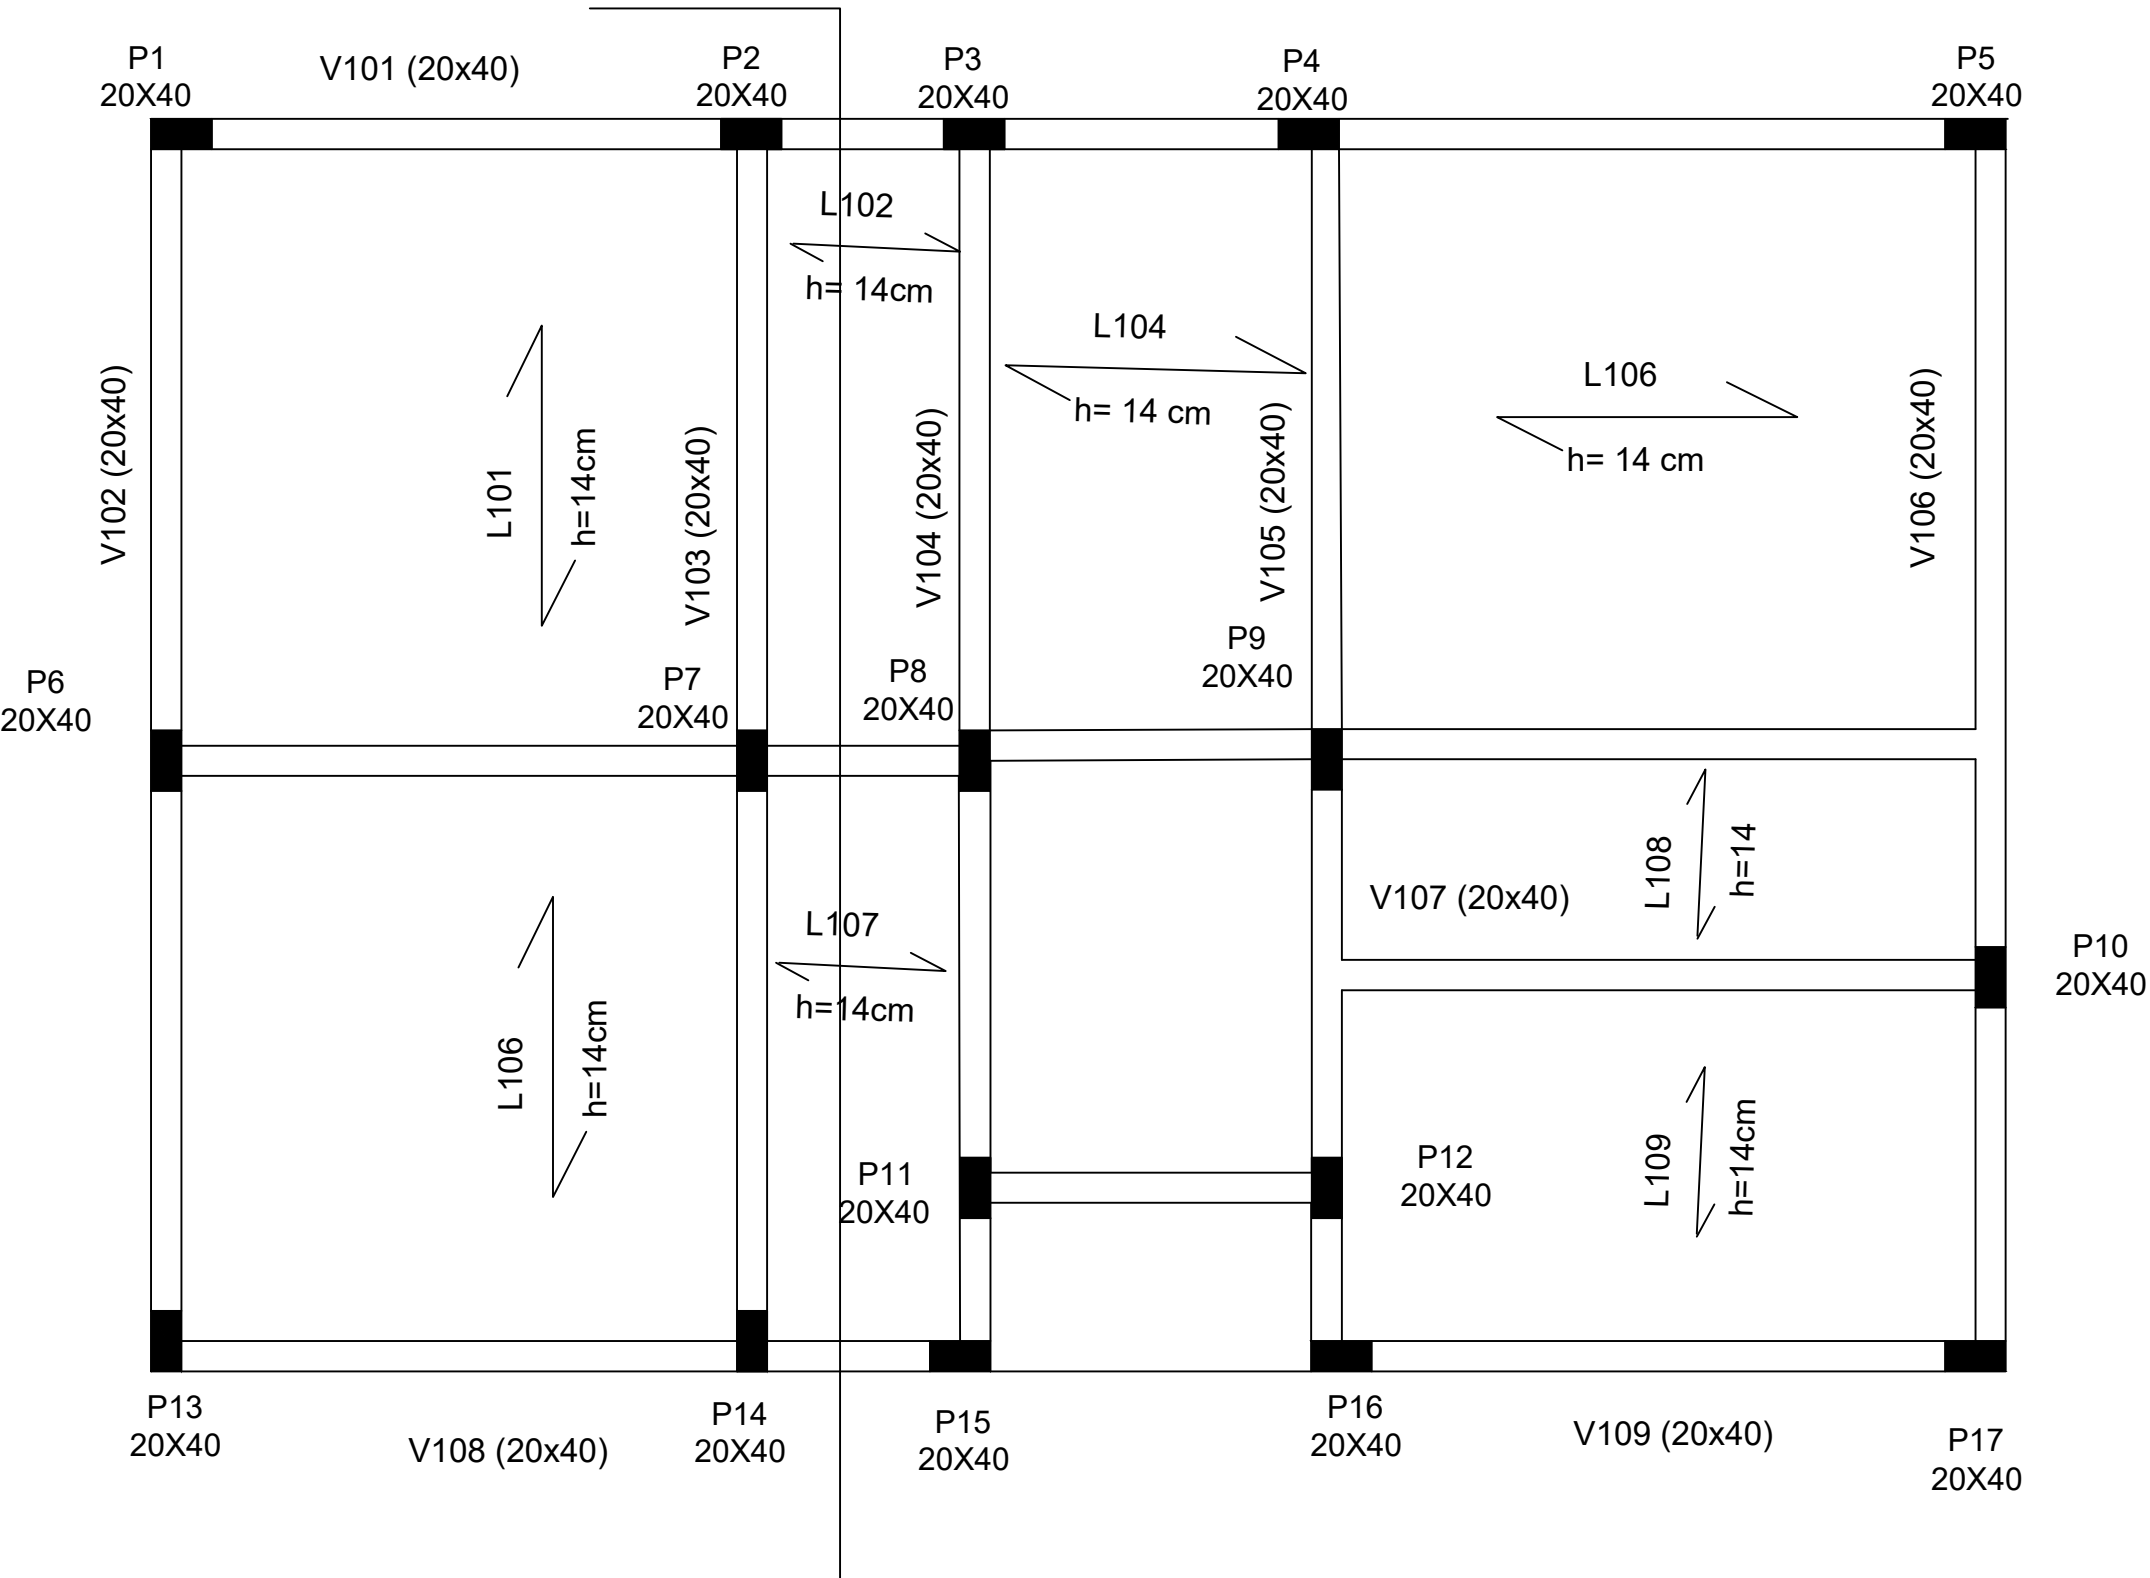

N1
CORTE - AA

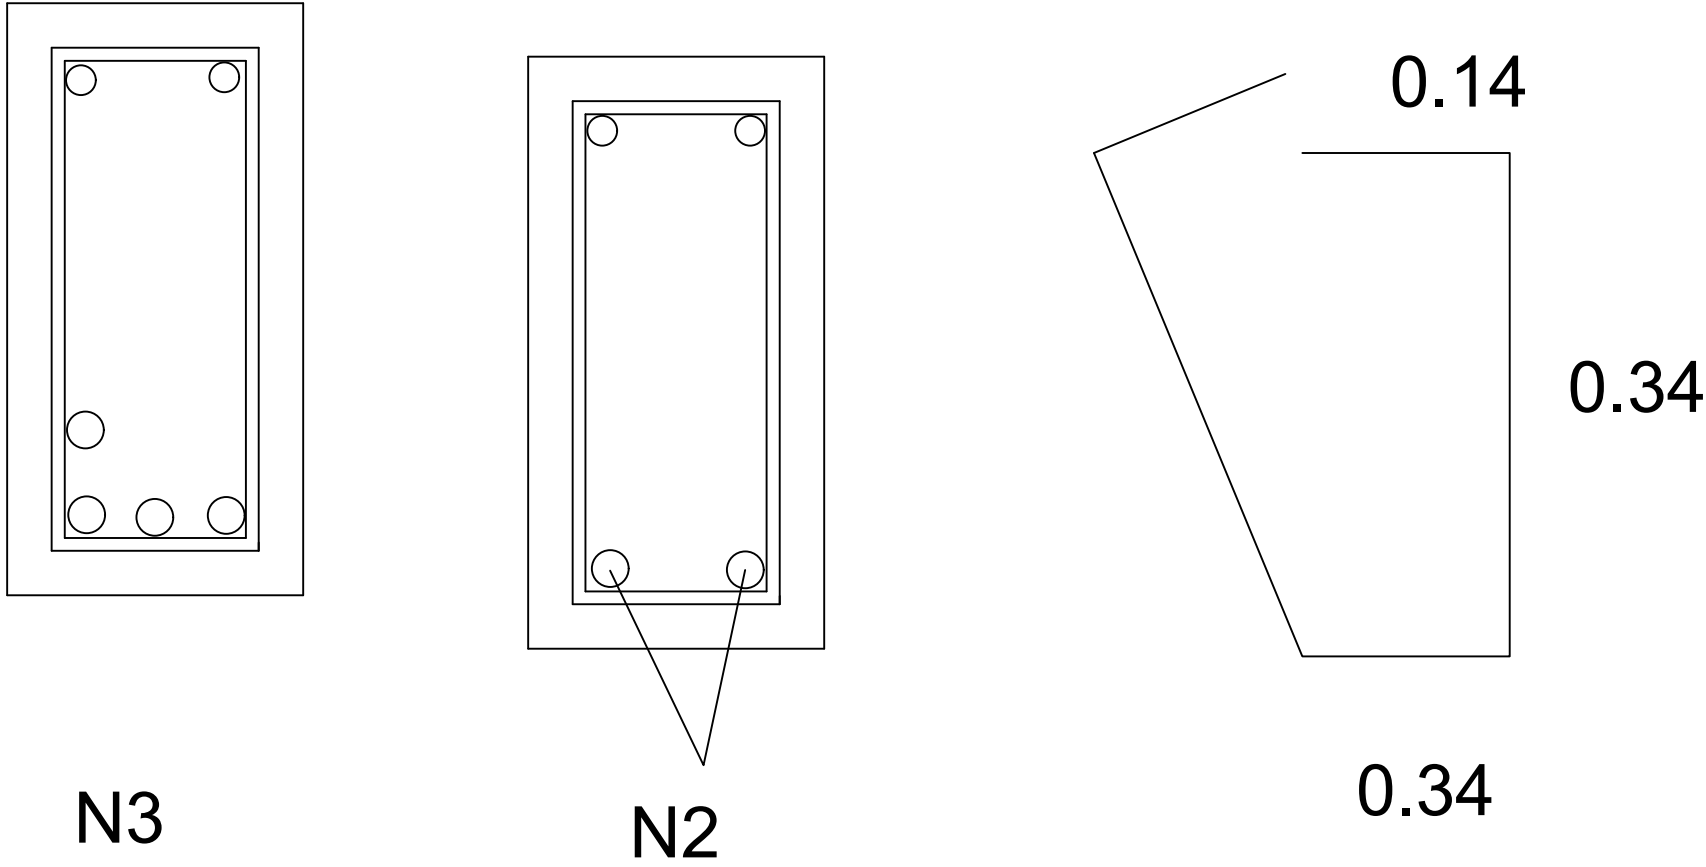

N3
CORTE - BB

N2
CORTE - CC

18 N5 6.3 PHI C/20 -

Carregamento	Esp (m)	Gaamma (kN/m²)	Total (kN/m²)
Contra piso	0,04	21	0,84
Impermeabilizante	0,05	0,11	0,0055
Revestimento Gesso	0,02	15	0,3
Porcelanato	0,01	21	0,21
Sobrecarga		1,5	1,5
Total 1 (kN/m²)			2,8555

Paredes Sobre Laje		
Lx	Ly	Alaje (M²)
3,97	4,34	17,2298

Paredes					
MATERIAL	Esp (m)	Largura (m)	Pé direito (m)	Gaamma (kN/m³)	Carga (Kn)
Tijolo Furado	0,14	3,8	2,7	14	20,1096
Repoco	0,06	3,8	2,7	21	12,9276
Impermeabiliz	0,04	3,8	2,7	0,11	0,045144
Total 2 (kN/m²)					33,08234
Cpar (kN/m²)	1,92007				
Total 2 (kN/m²)	4,77557				
hest (cm)	Peso próp. (kN/m²)		1,36		
hlaje (cm)					
Carga total (kN/m²)	6,13557	Especificações			
Capa (cm)	4	total (cm)	14		
Enchimento	40	Vigota	433 arranjo 1		
Inter eixo (cm)	50				