

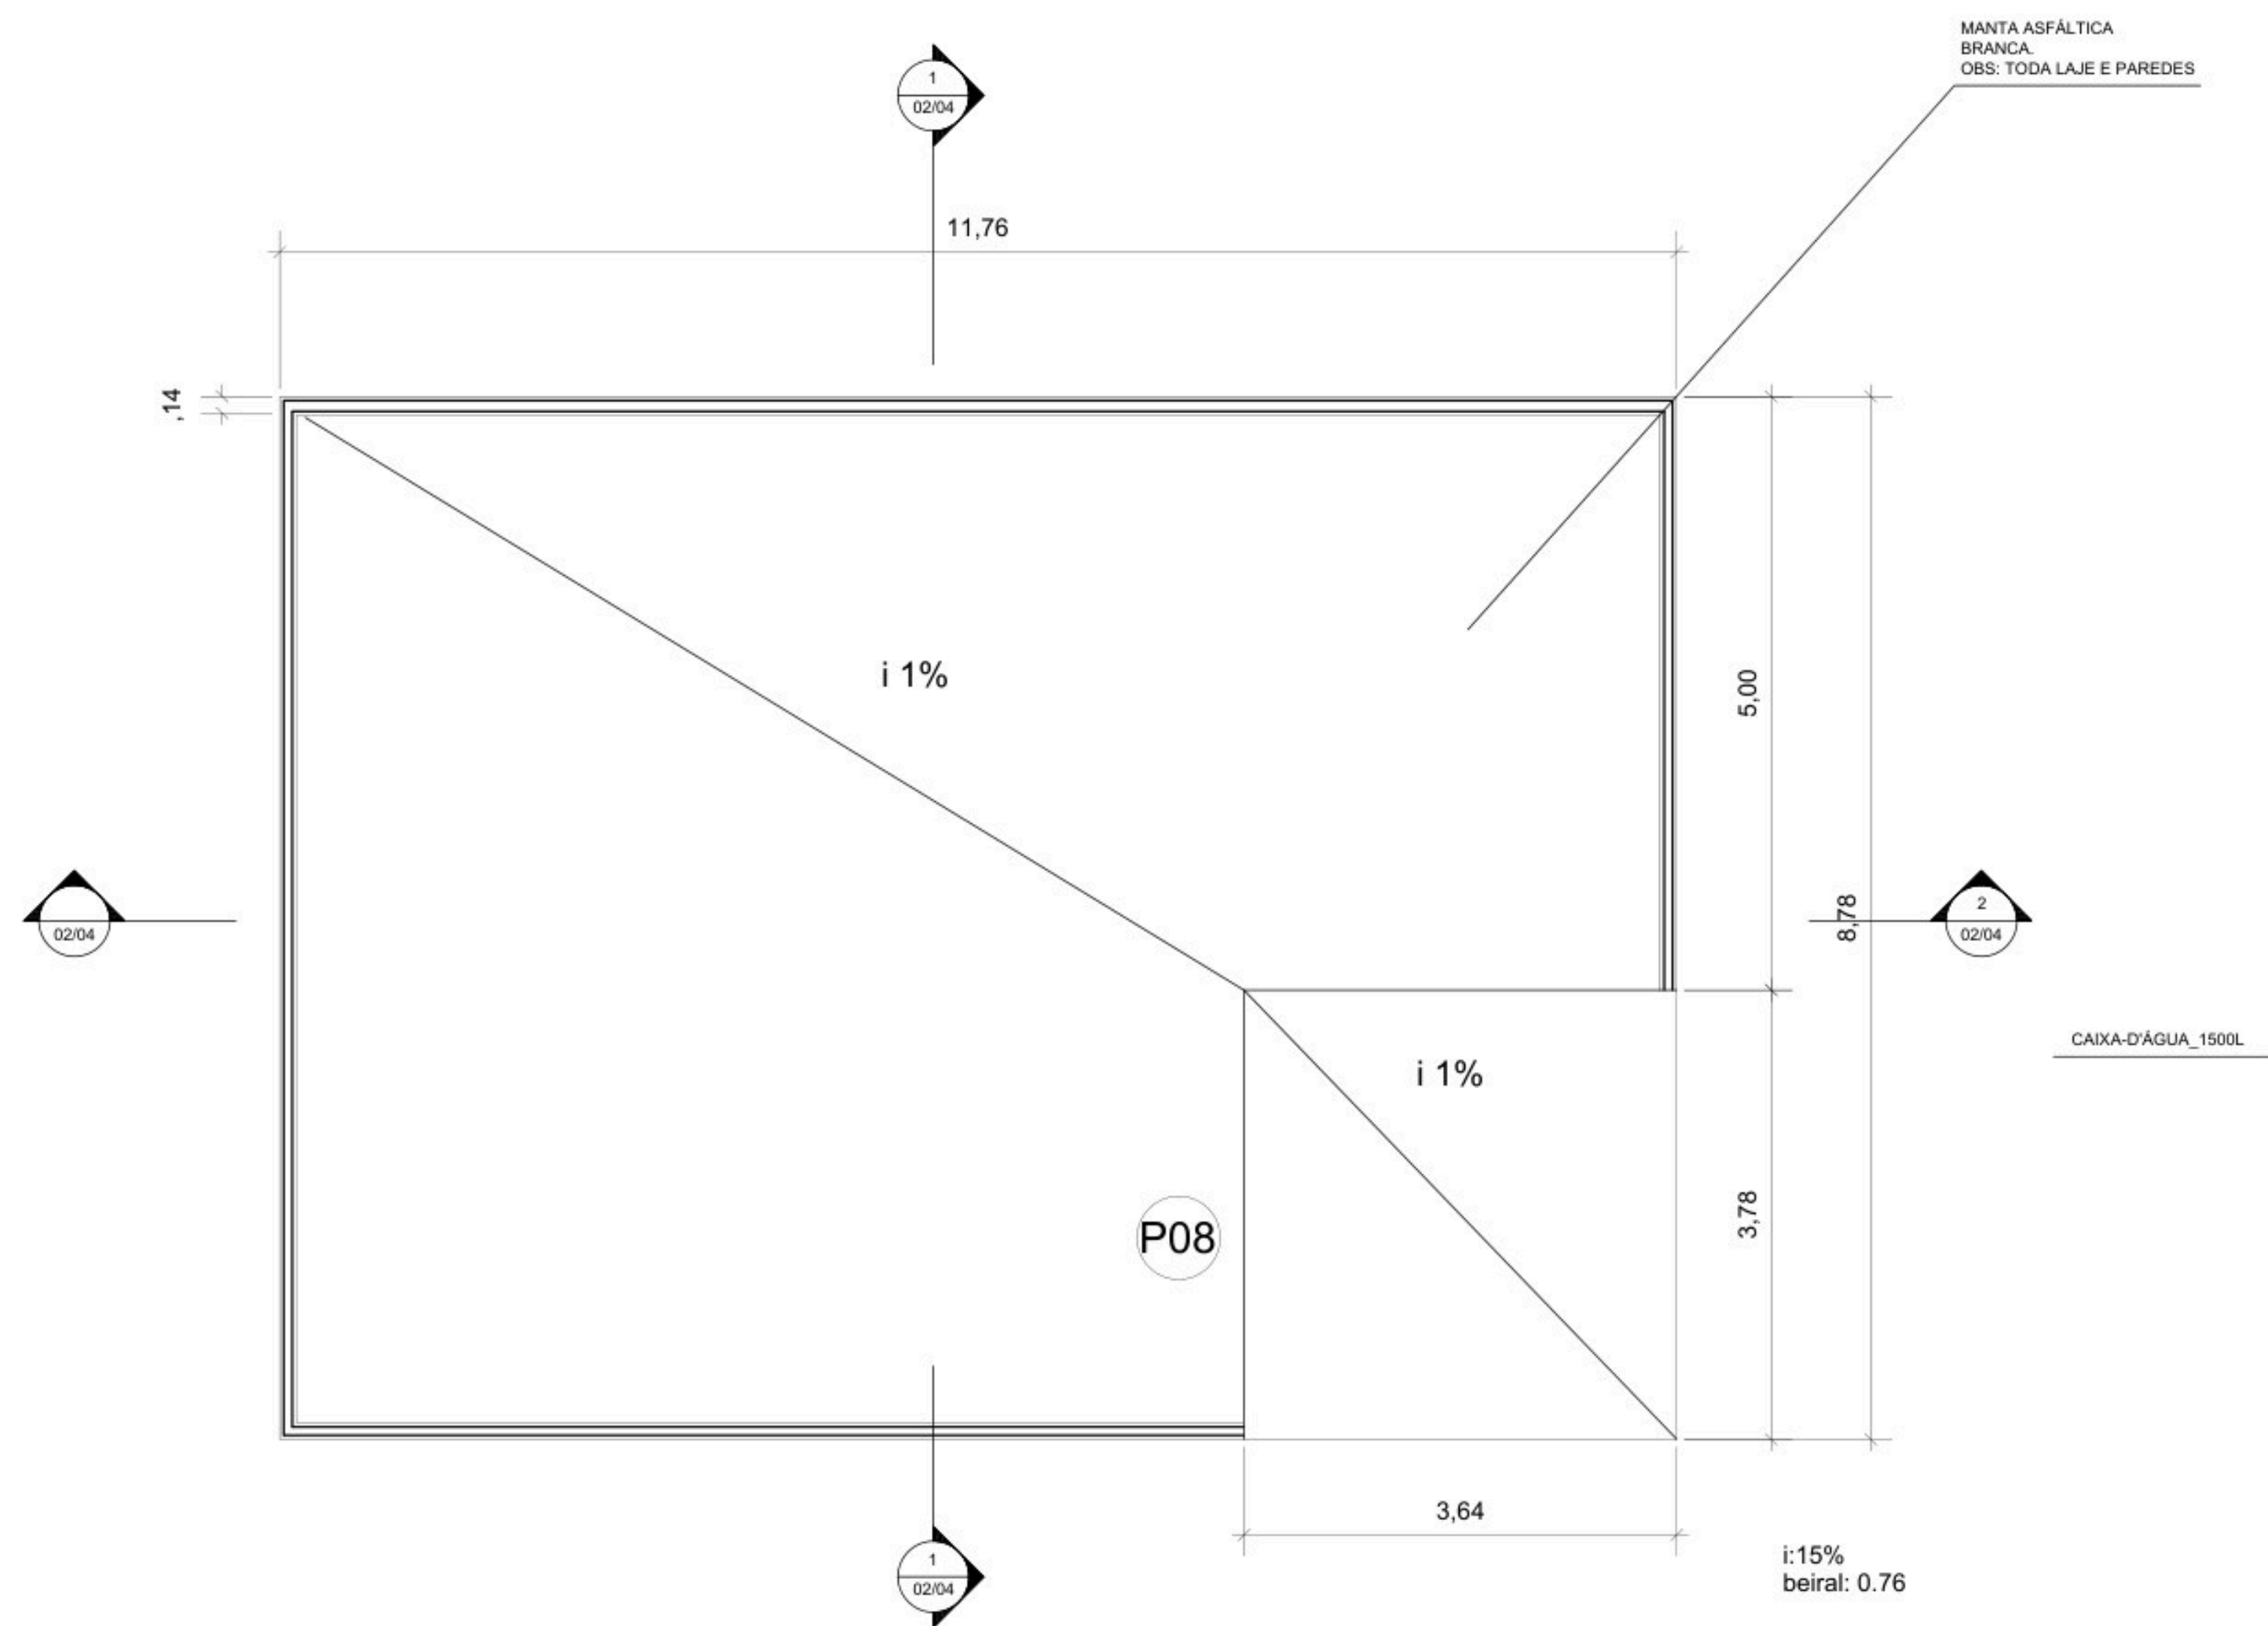
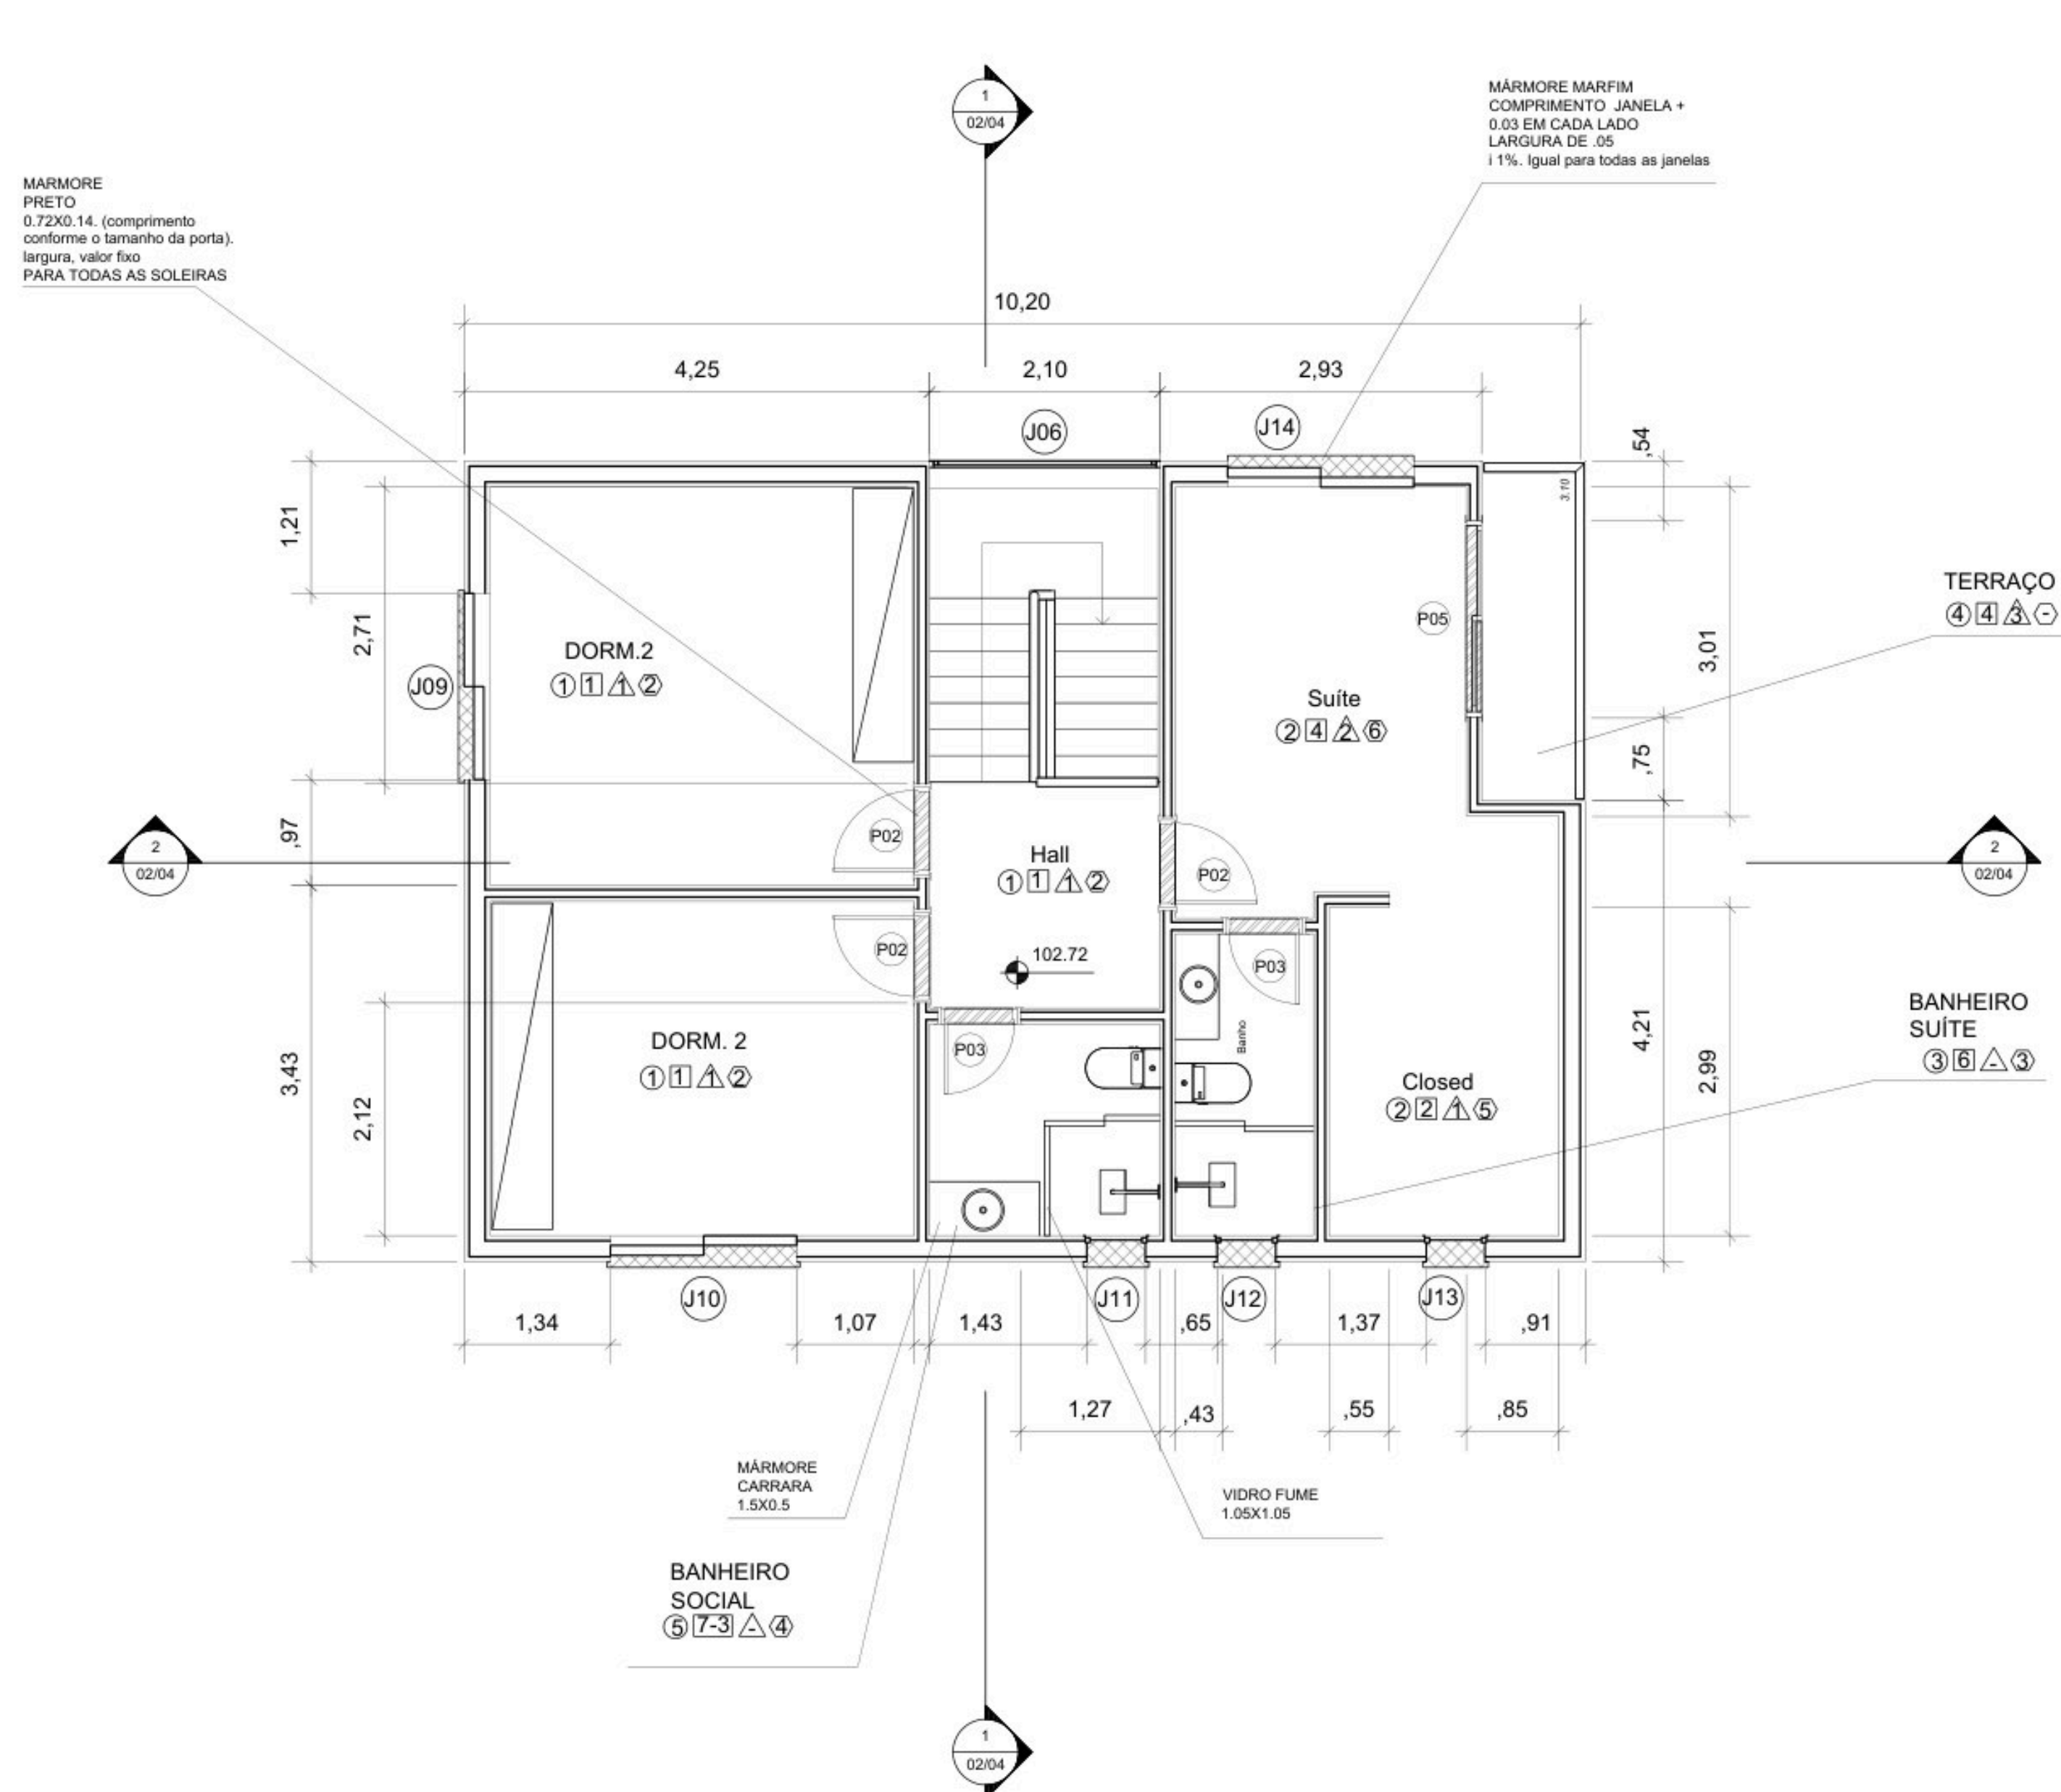
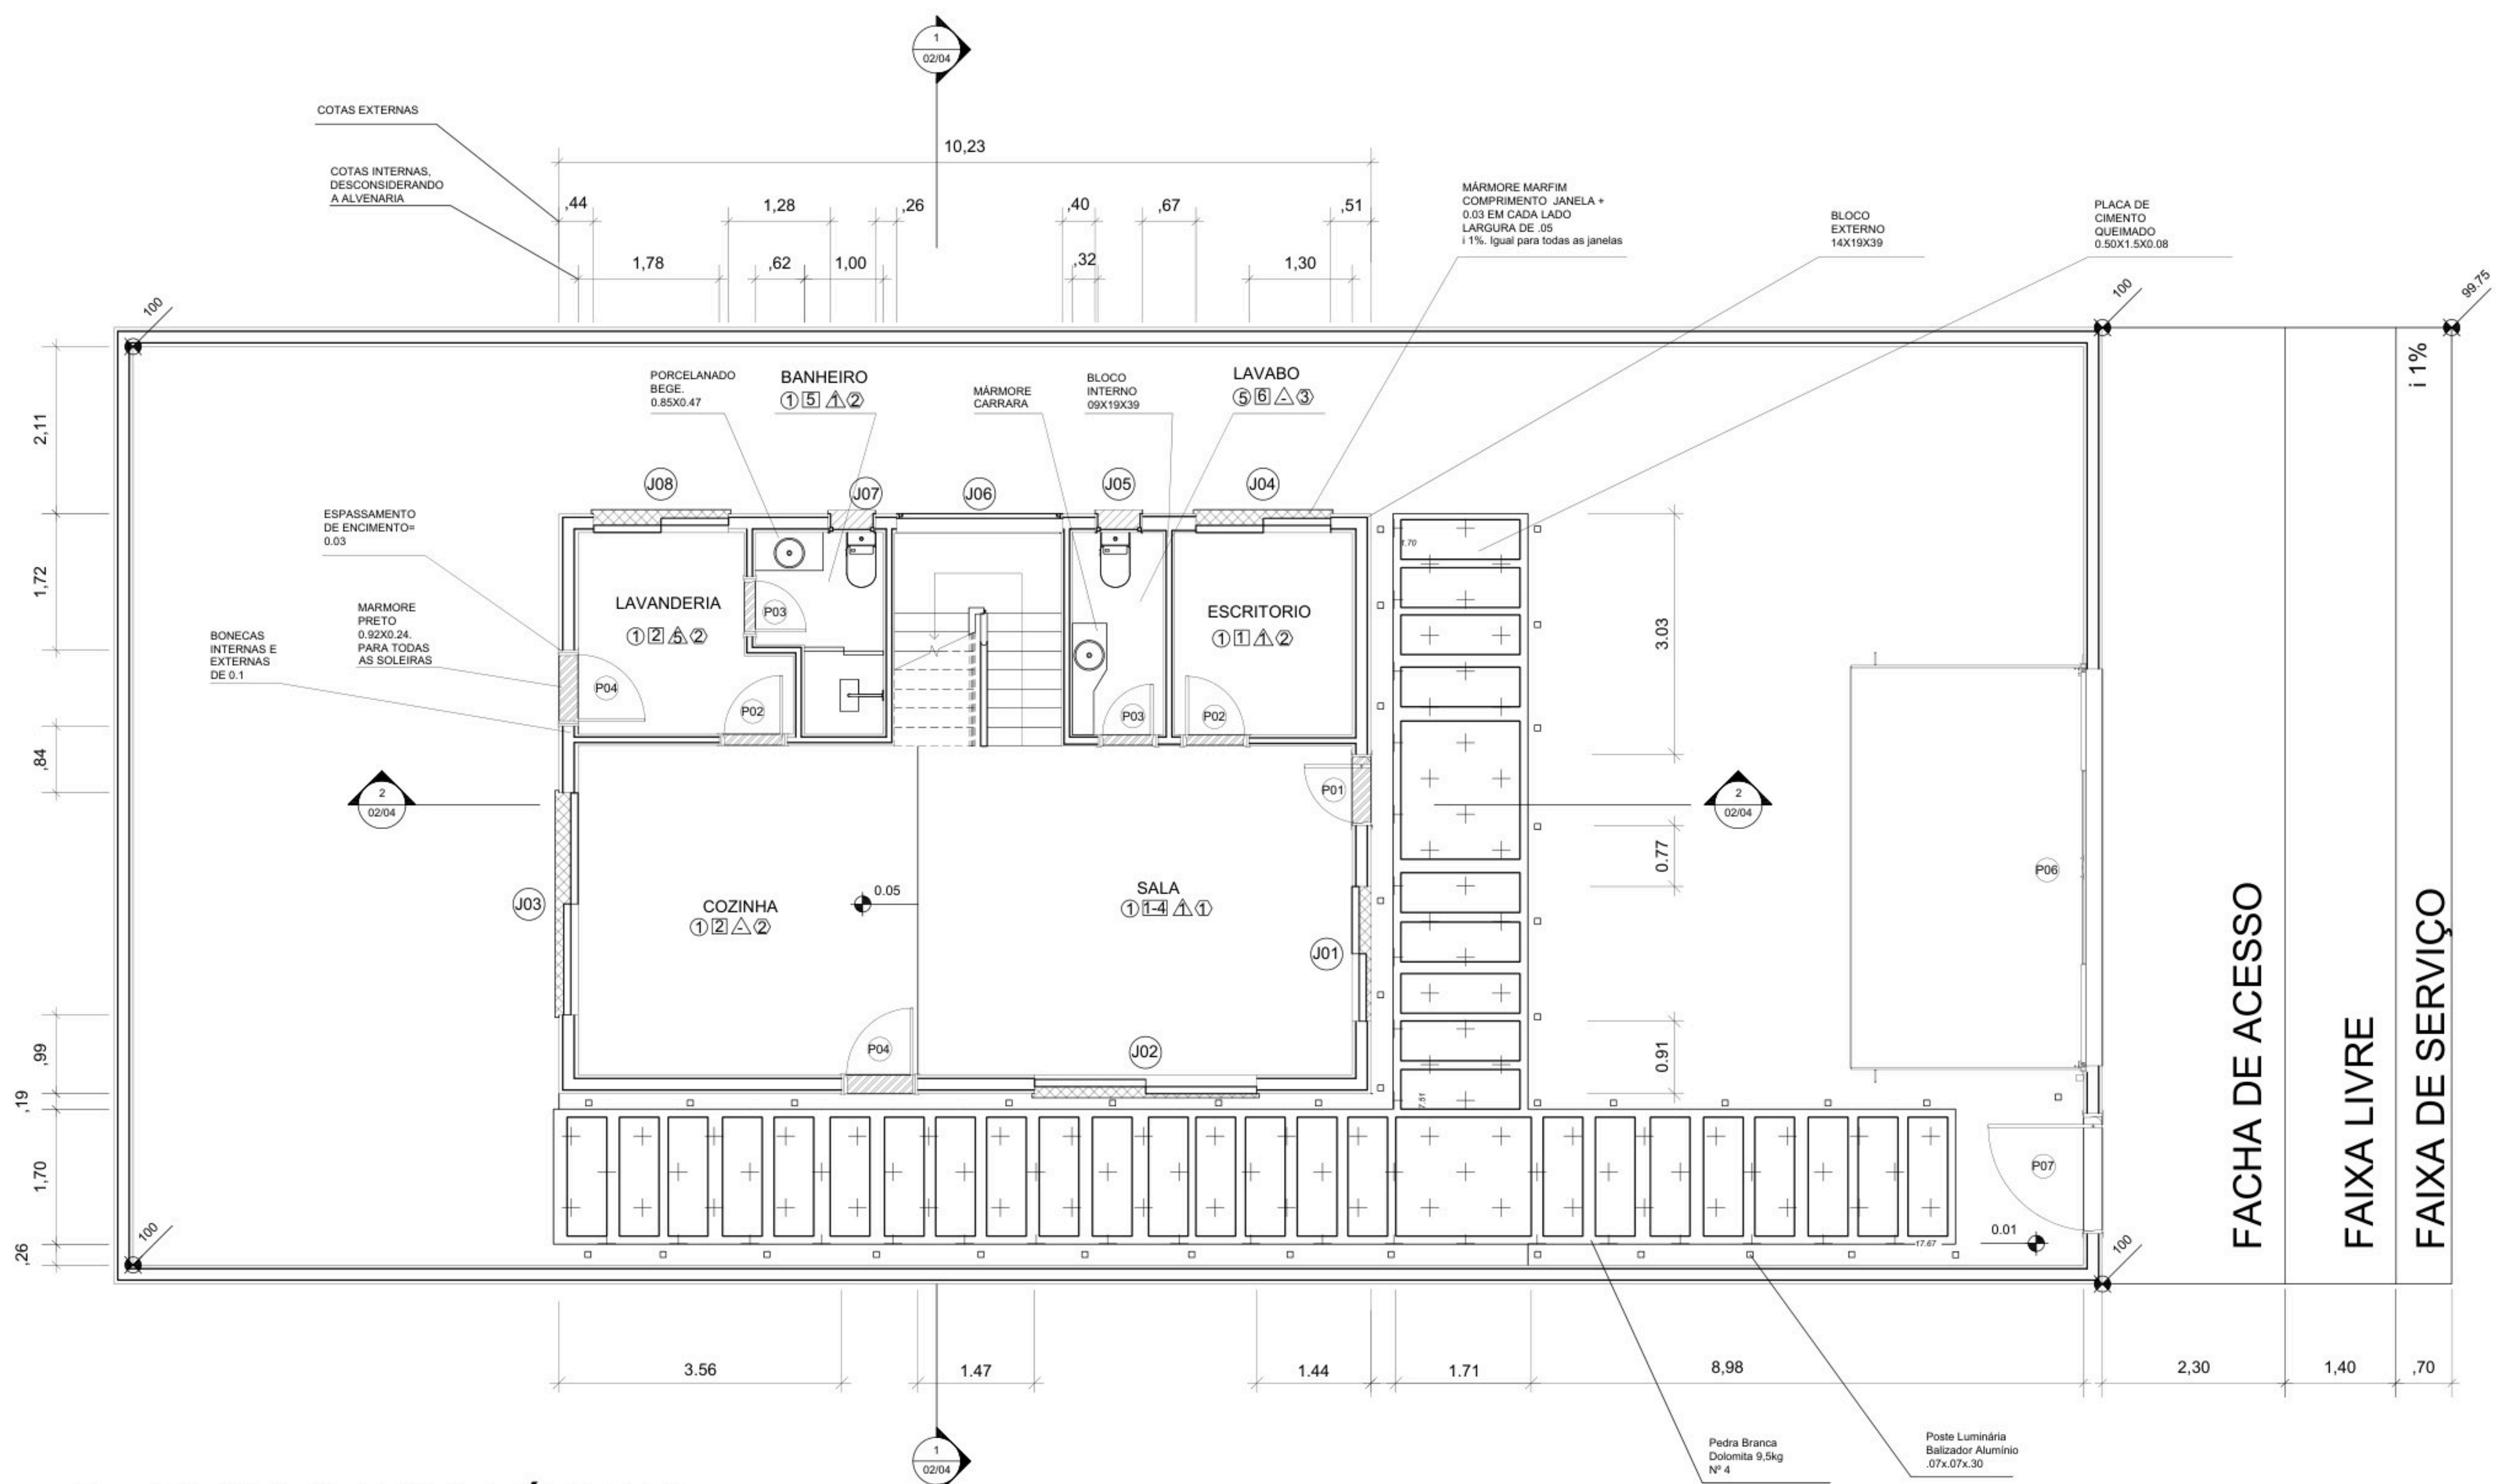


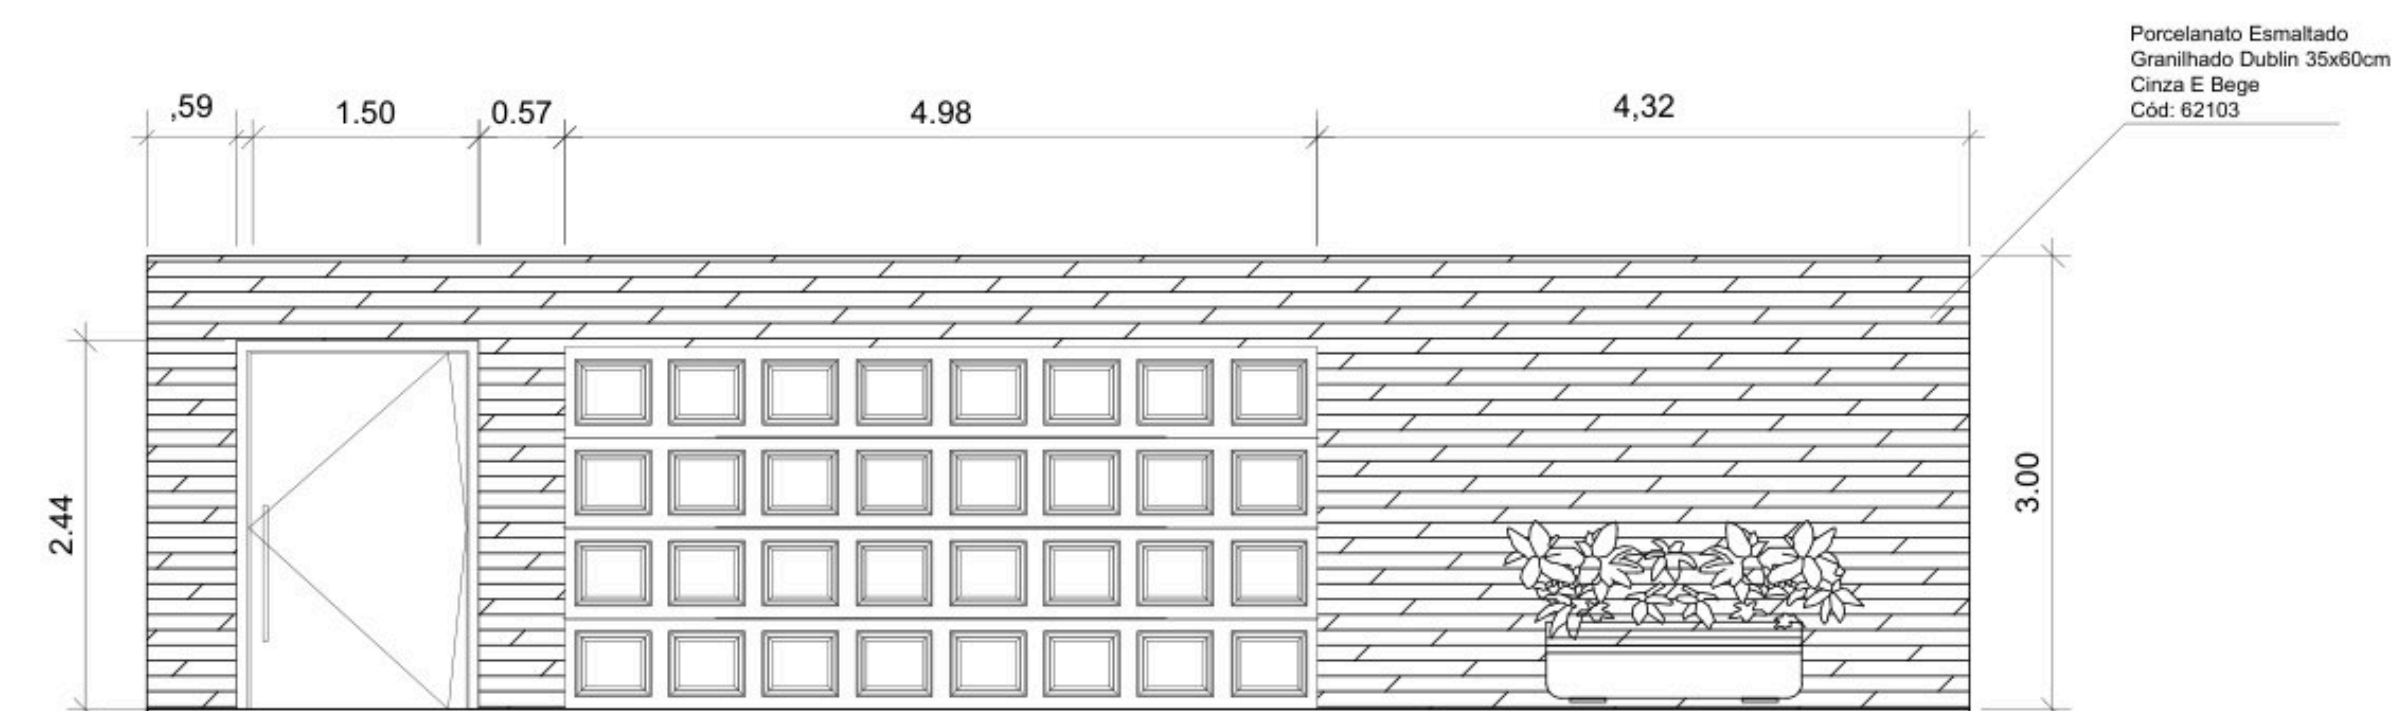

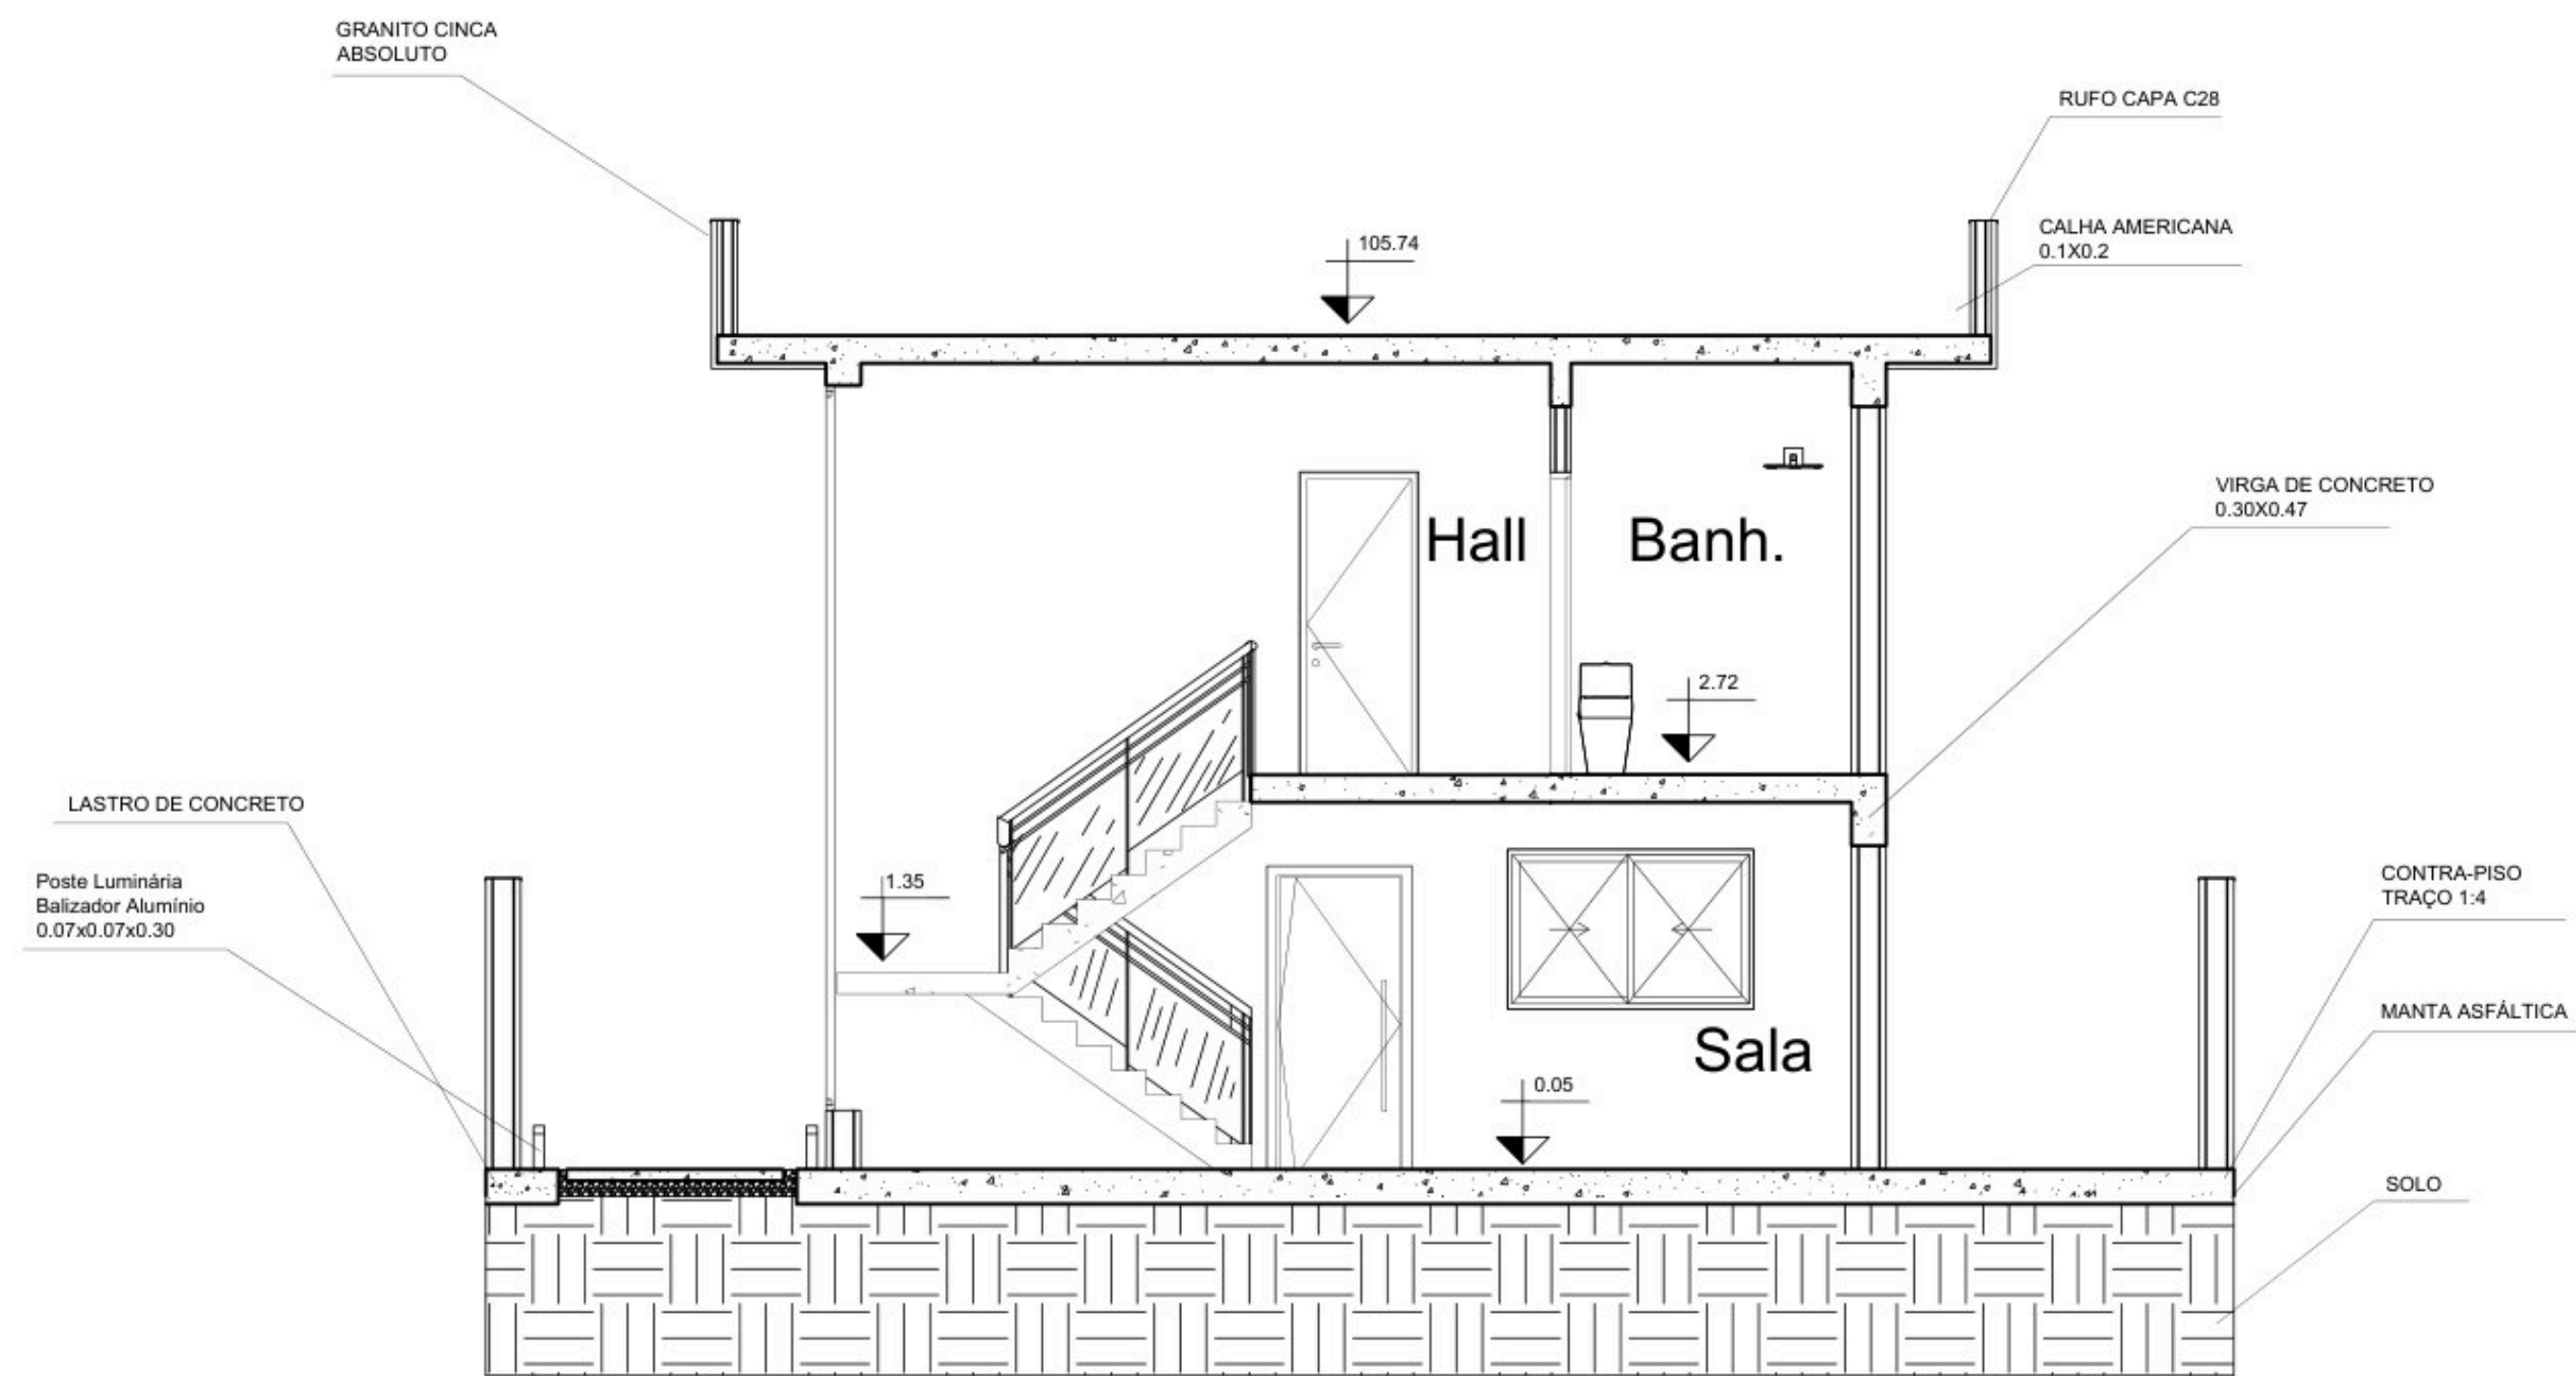


FACHA DE ACESSO





FAIXA LIVRE

FAIXA DE SERVIÇO


i 1%

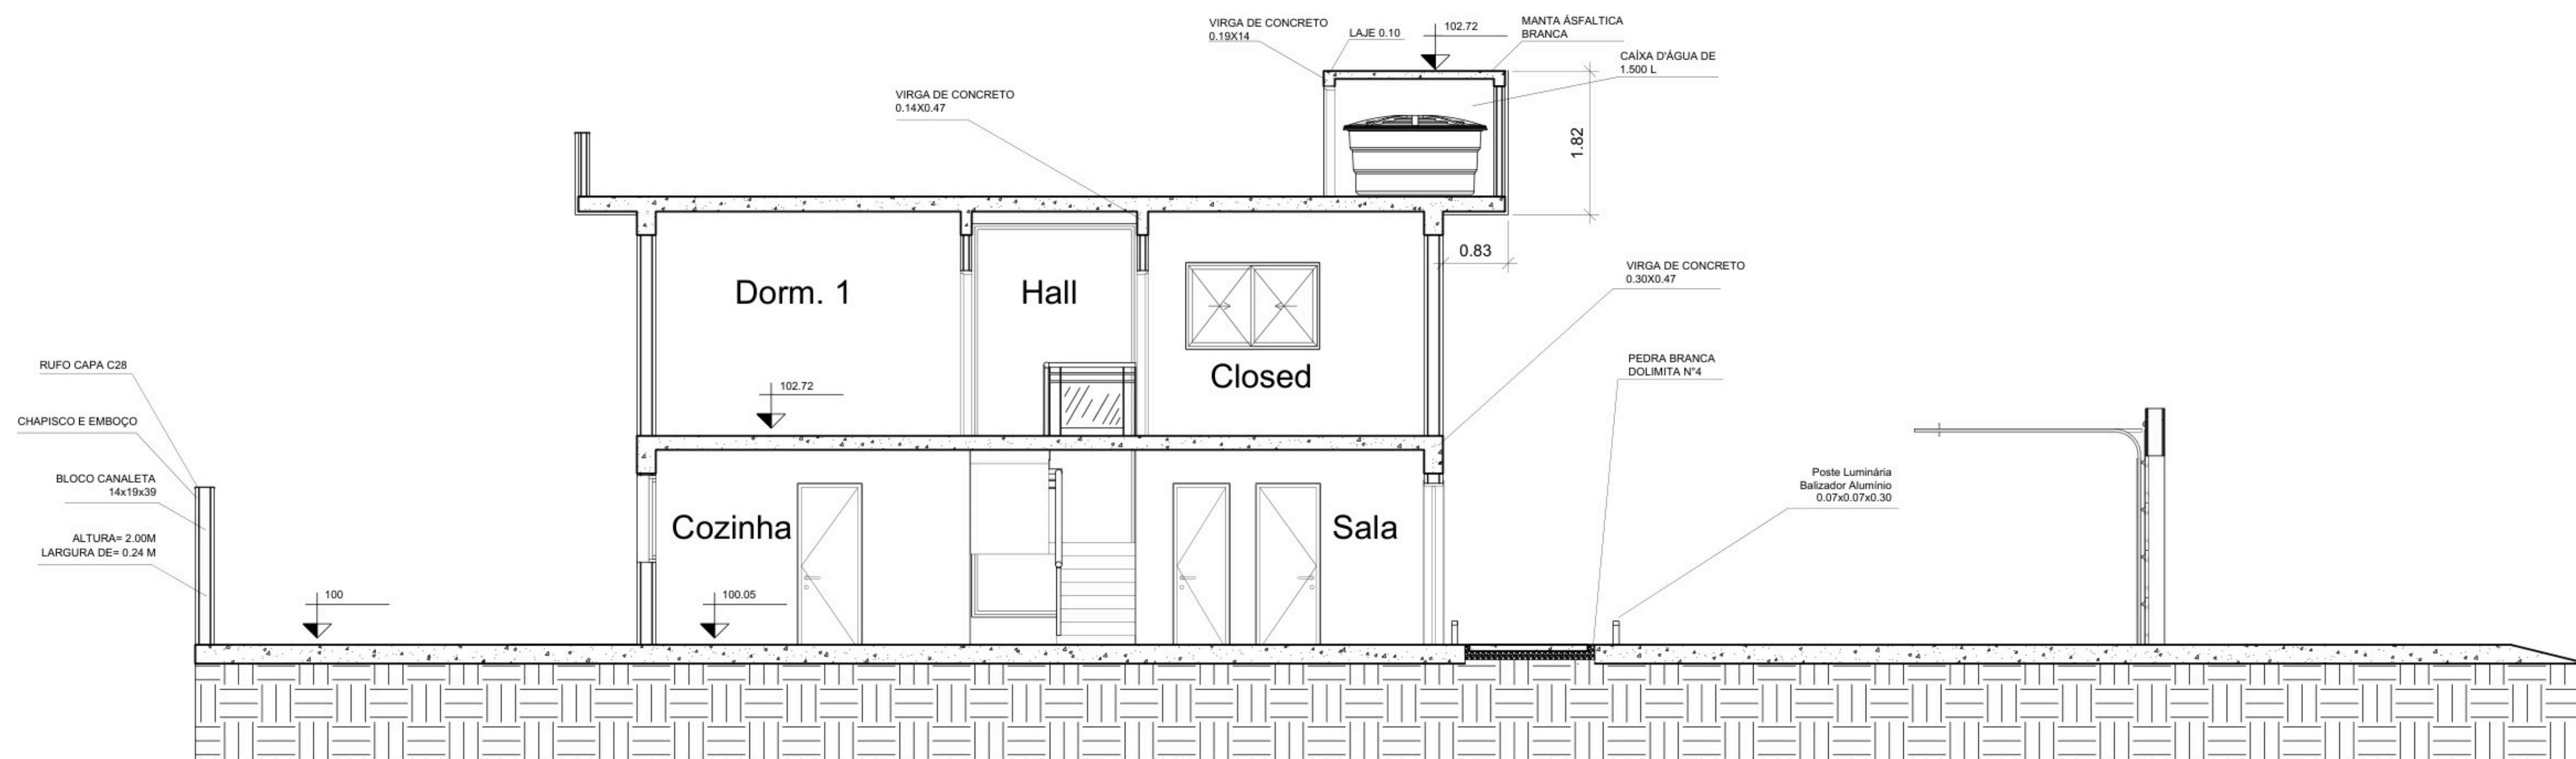

	INSTITUTO FEDERAL DE EDUCAÇÃO, CIÊNCIA E TECNOLOGIA			
	DISCIPLINA	PROFESSORES		
	DESENHO DE CONSTRUÇÃO CIVIL	ANTÔNIO DEZOTTI FILHO		
	DESENHO	ESCALA	DATA	
VISTO	NOME	PROFESSOR	FOLHA	
	GUSTAVO R. SILVESTRE DA SILVA		02/04	

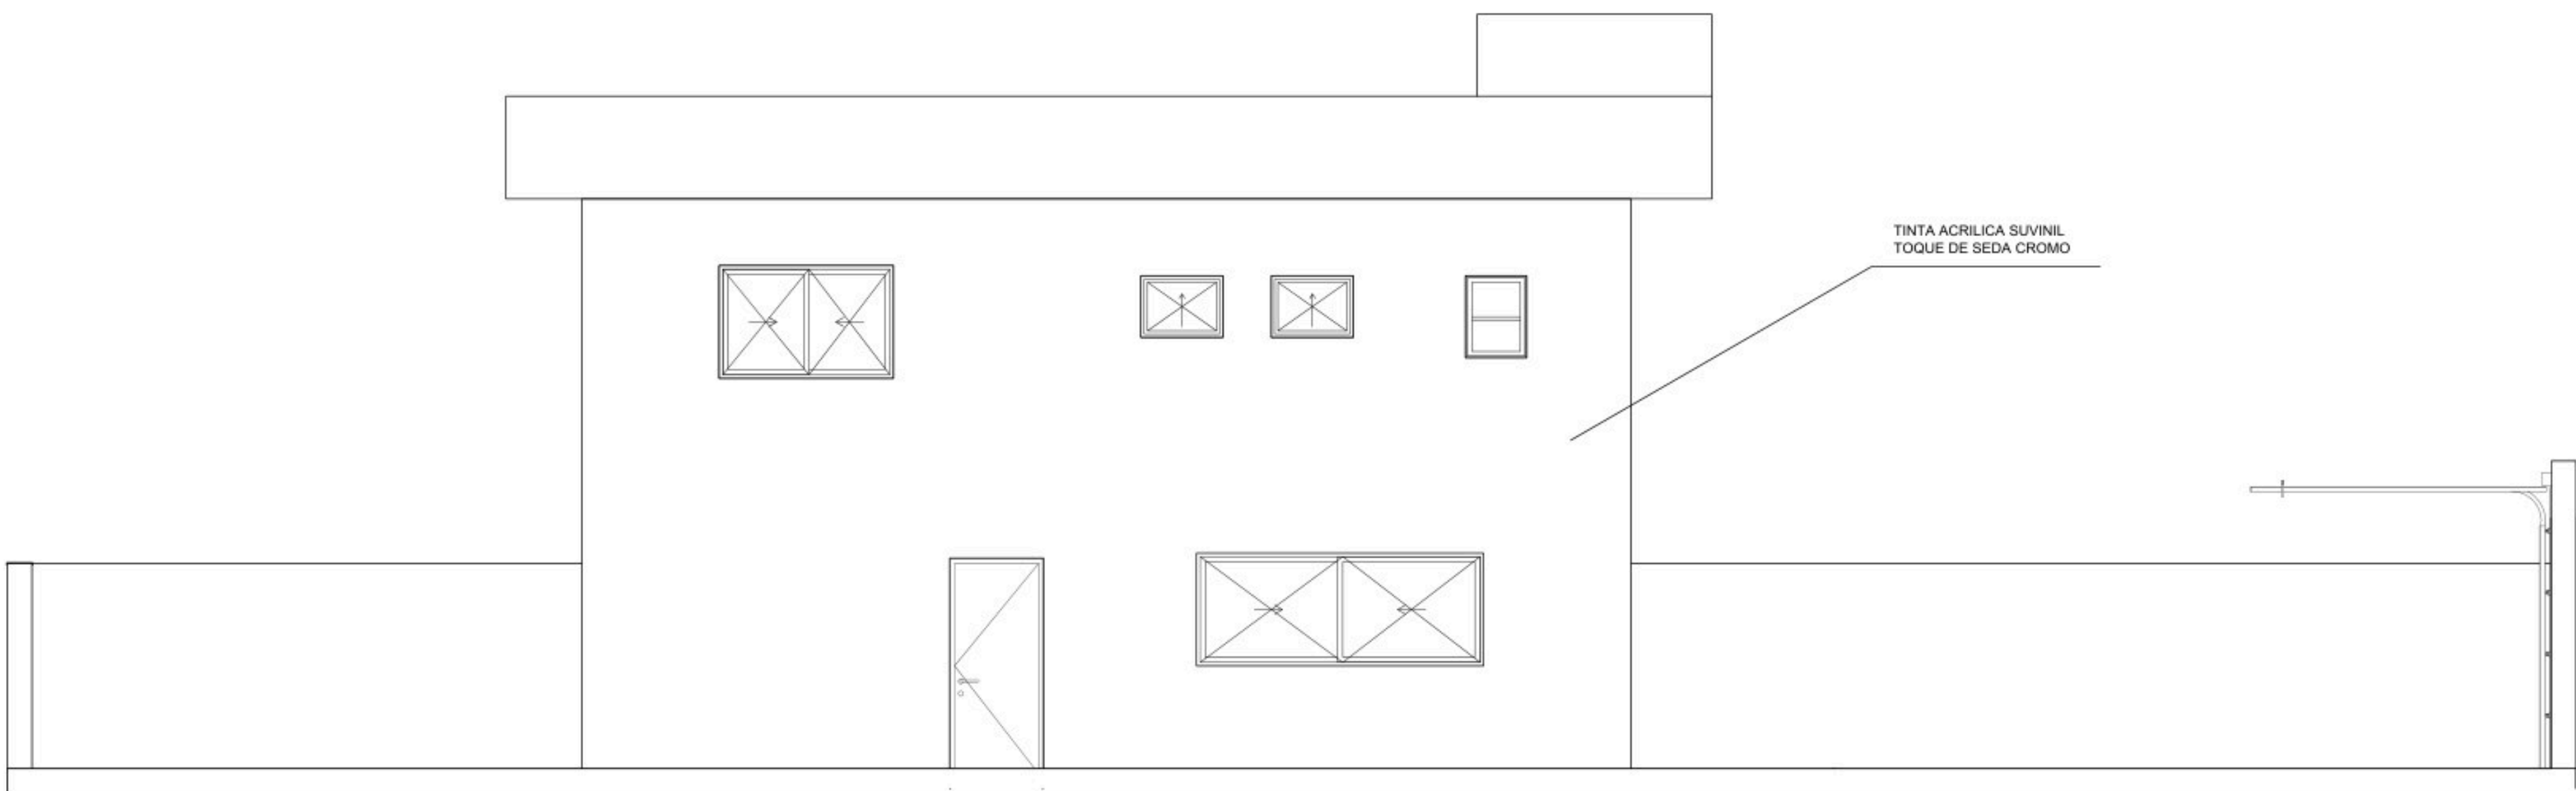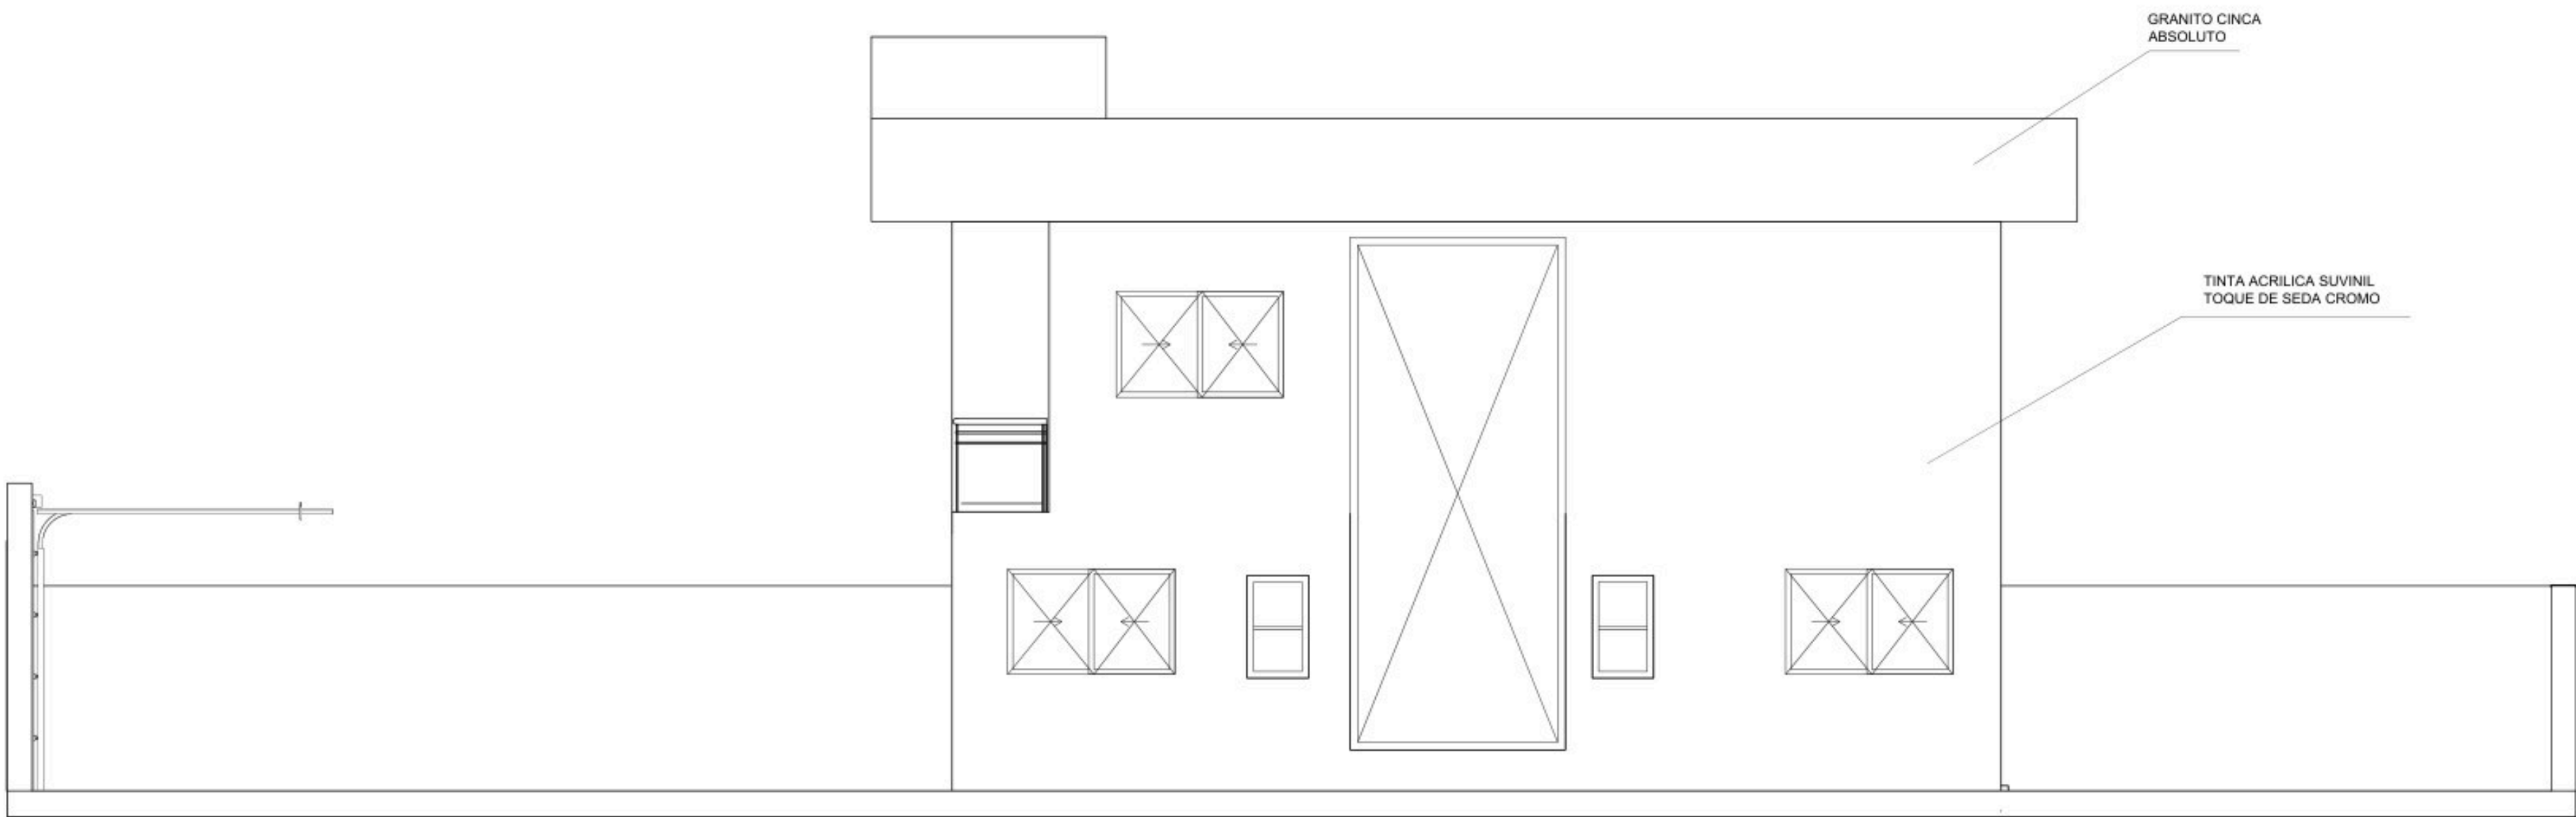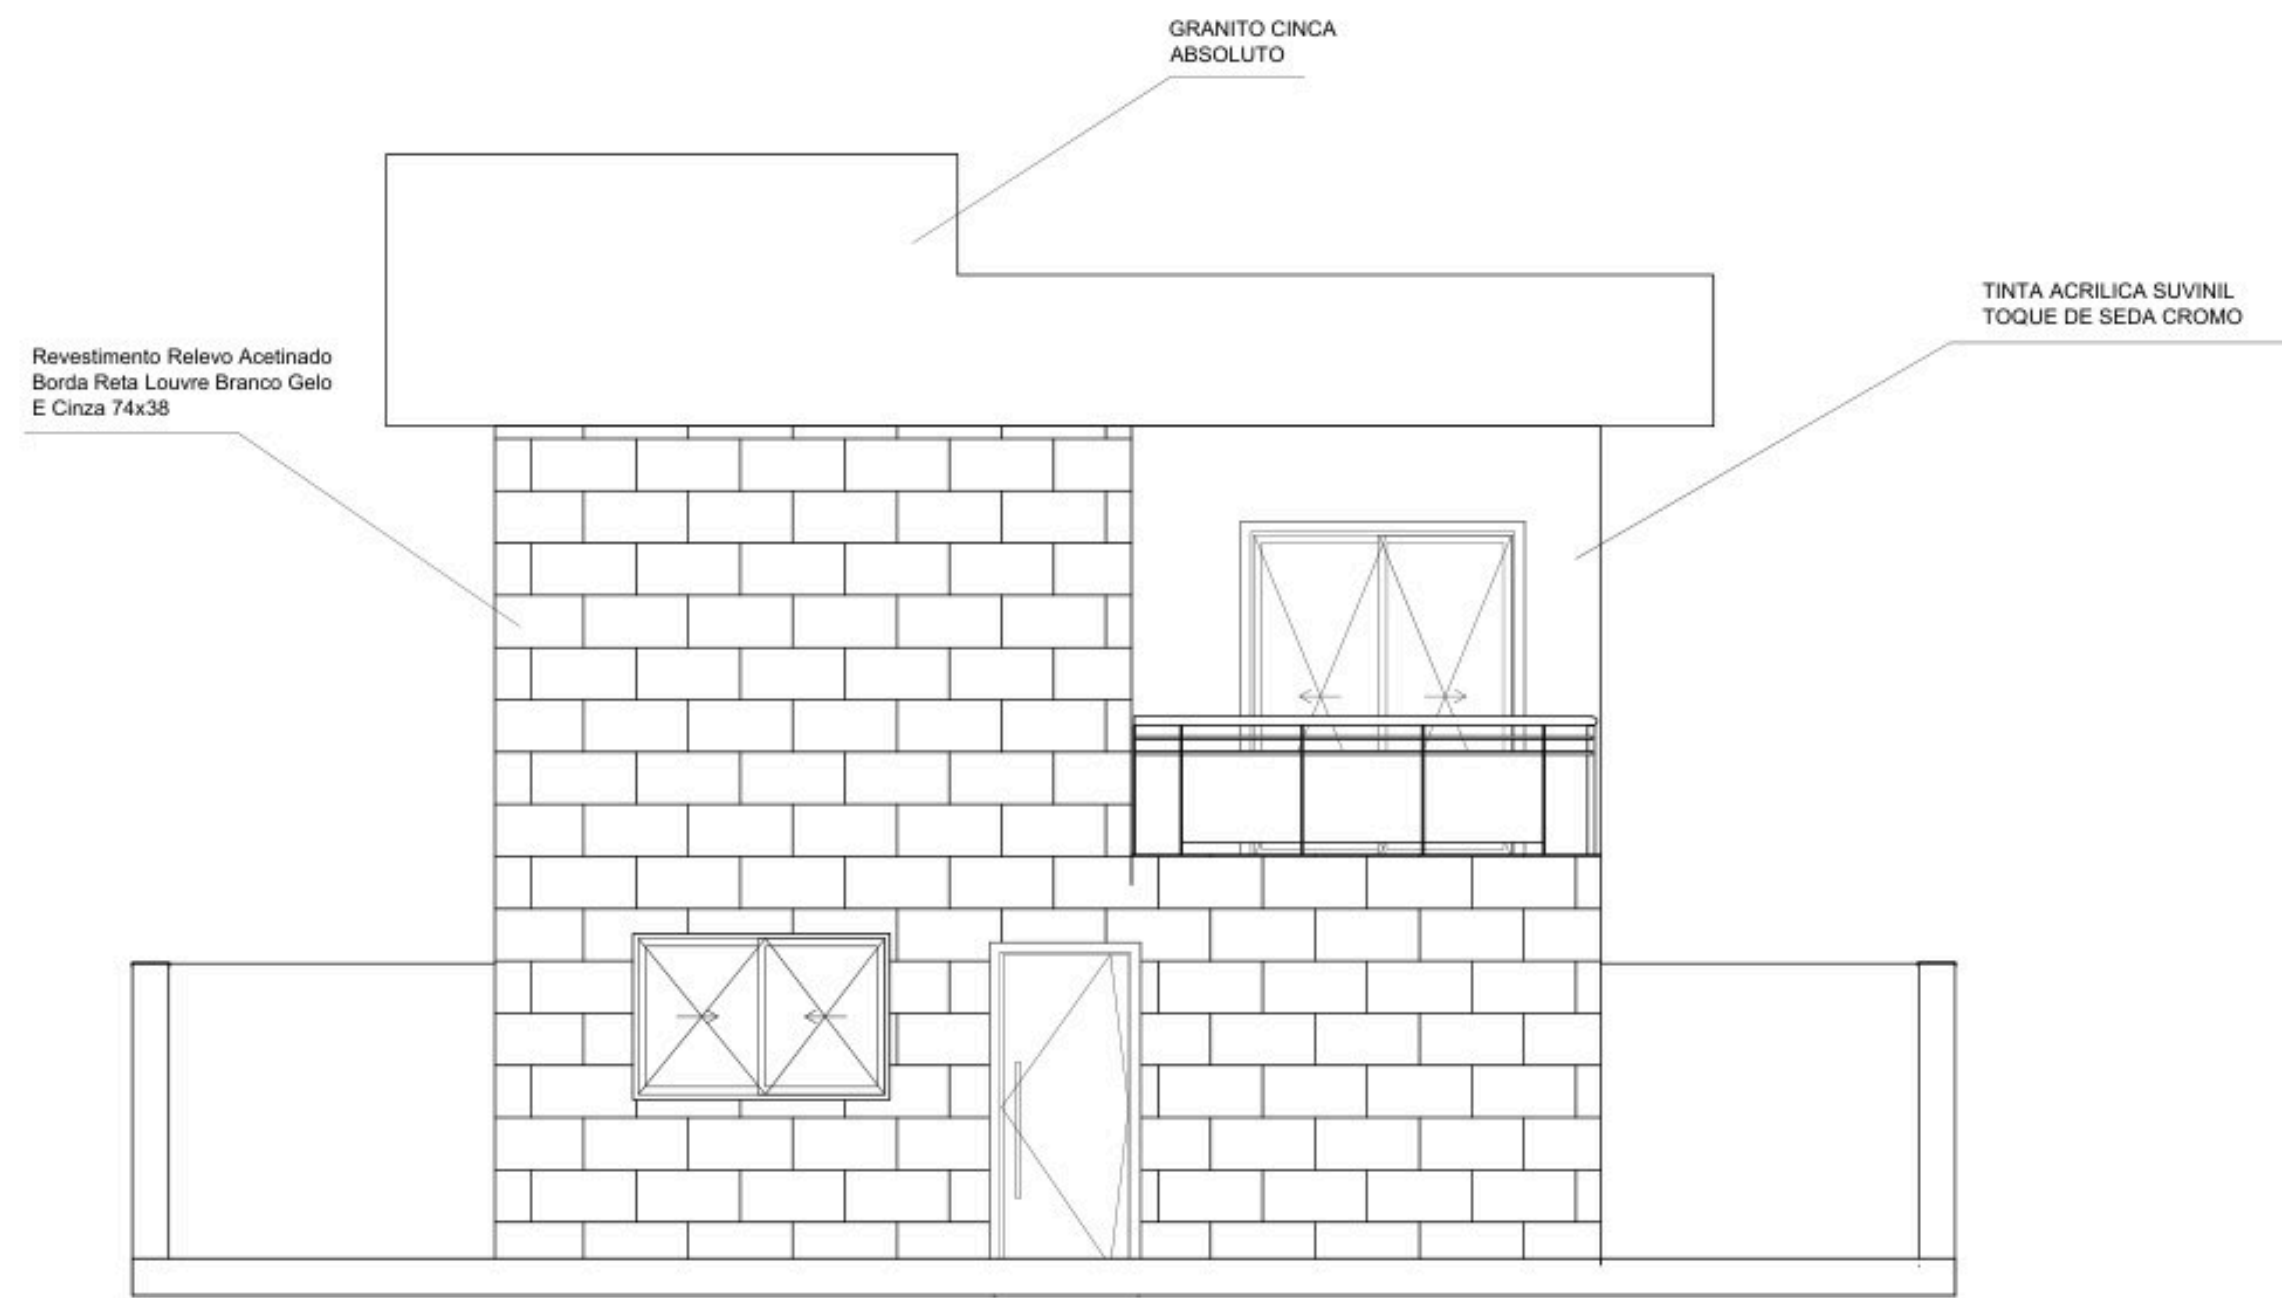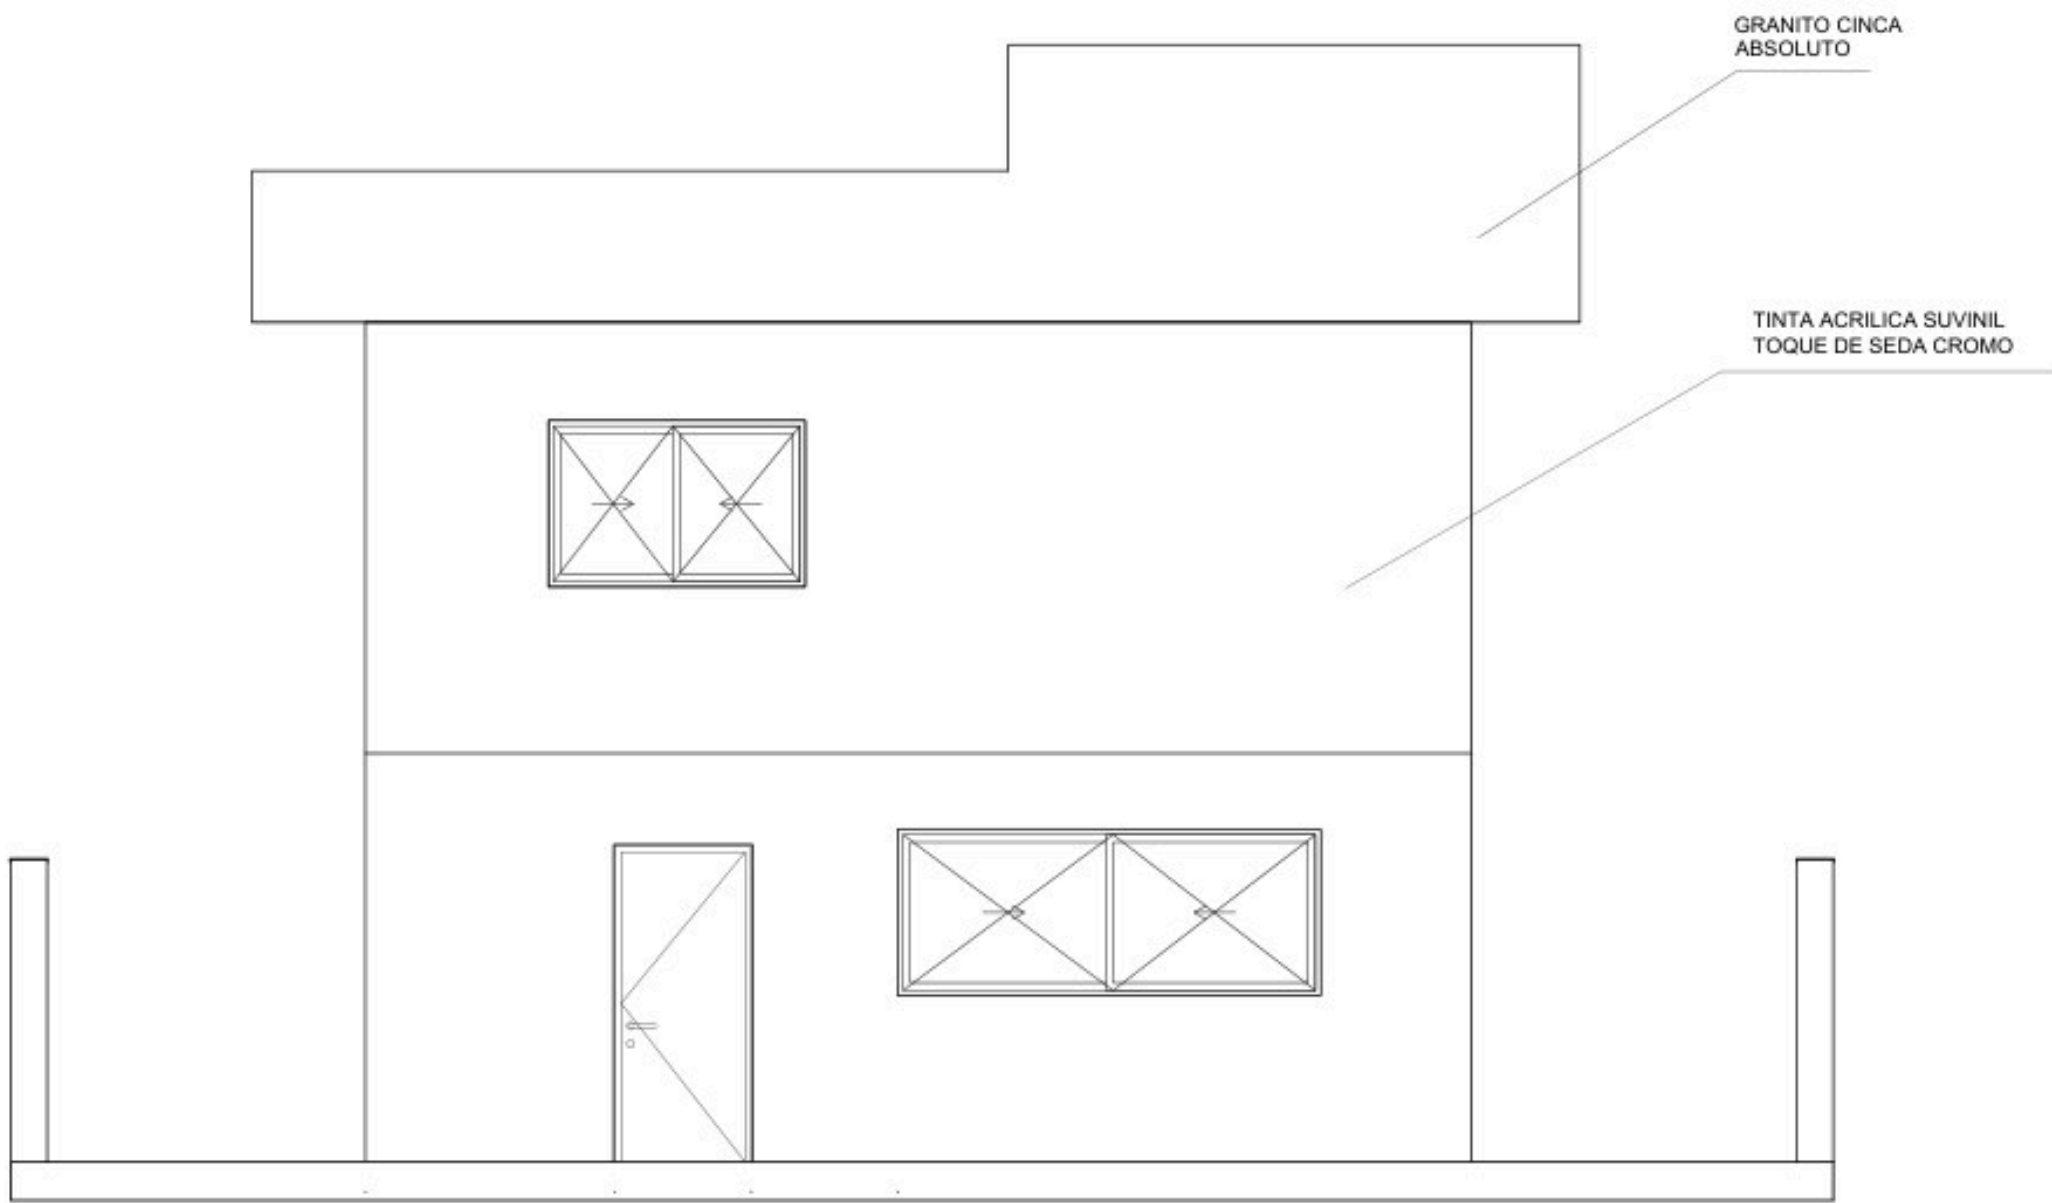


GRANITO CINZA
ABSOLUTO

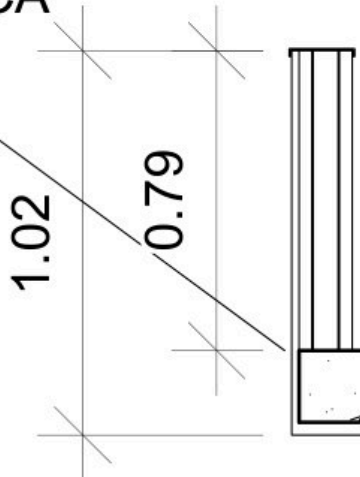

MANTA ASFÁLTICA
BRANCA.

VIRGA DE CONCRETO
0.14X0.47

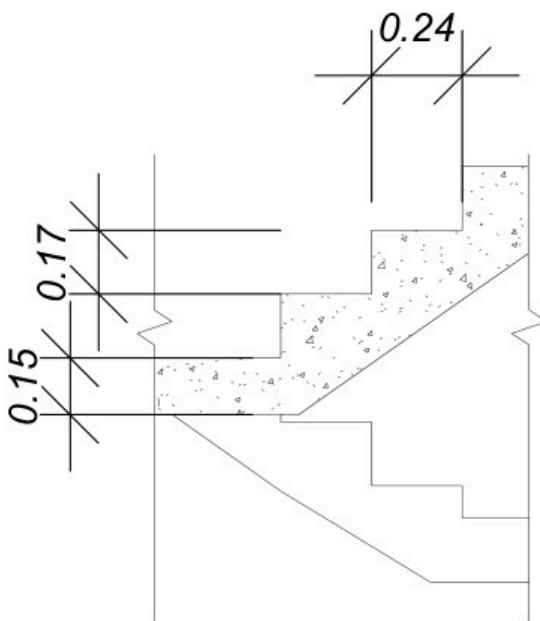

Tabelas de Esquadrias - Portas				
Marca de tipo	Material	Largura bruta	Altura bruta	Quantidade
P01	Madeira	0.92	2.10	1
P02	Madeira	0.72	2.10	5
P03	Madeira	0.62	2.10	4
P04	Madeira	0.82	2.10	2
P05	Madeira	1.70	2.10	1
P06	Alumínio	5.00	2.40	1
P07	Alumínio	1.52	2.40	1
P08	Alumínio	1.50	1.40	1
Total geral:				16

Tabela de janela							
Comentários de tipos	Marca de tipo	Largura bruta	Altura bruta	Altura do peitoril	Material	Vidro	Modelo
Sala	J01	1.70	1.10	1.10	Alumínio	Vidro Liso	Correr
Sala	J02	2.80	1.10	1.00	Alumínio	Vidro Liso	Correr
Cozinha	J03	2.80	1.10	1.10	Alumínio	Vidro Liso	Correr
Escritório	J04	1.70	1.10	1.10	Alumínio	Vidro Liso	Correr
Lavabo	J05	0.60	1.00	1.10	Alumínio	Vidro Fosco	MAXIM-AR
Escada	J06	2.10	5.00	0.40	Alumínio	Vidro Liso	Fixa
Banh. Área De Serviços	J07	0.60	1.00	1.10	Alumínio	Vidro fosco	MAXIM-AR
Área De Serviços	J08	1.70	1.10	1.10	Alumínio	Vidro Liso	Correr
Dorm. 1	J09	1.70	1.10	1.10	Alumínio	Vidro Liso	Correr
Dorm. 2	J10	1.70	1.10	1.10	Alumínio	Vidro Liso	Correr
Banh. Superior	J11	0.80	0.60	1.50	Alumínio	Vidro, fosco	MAXIM-AR
Banh. Suíte	J12	0.80	0.60	1.50	Alumínio	Vidro, fosco	MAXIM-AR
Closed	J13	0.60	0.60	1.30	Alumínio	Vidro, fosco	MAXIM-AR
Suíte	J14	1.70	1.10	1.10	Alumínio	Vidro Liso	Correr

Total geral: 14

TABELA RESUMO DE ACABAMENTOS							
	ITEM	MATERIAL	DIMENSÃO	COR	MODELO/CÓDIGO	FABRICANTE	OBSERVAÇÃO
PISO	1	Porcelanato Polido	82 X 62	Champagne	879373	Elizabeth	Junta de 2 mm
	2	Cerâmica -Porcelanato	80x120cm	Branco	759303	Portinari	
	3	Porcelanato	59x118,2cm	Branco e cinza	979742	Eliane	
	4	Porcelanato	61,8x61,8cm	Cinza	P82083	Artens	Combina com o Rejunte 90423942
	5	Porcelanato	83x83	Branco	966907	Embramaco	
PAREDE	1	Tinta acrílica		Cromio	3109.10.10	Suvinil	Aplica em paredes acabadas
	2	Revestimento Esmaltado	10x20cm	cinza	232595	Portobello	Rejunte branco. Junta de 4mm
	3	Revestimento borda reta	10x20cm	Preto	788650	Portobello	Rejunte branco
	4	Revestimento borda reta	33x100cm	cinza	739988	Portinari	Rejunte Cinza
	5	Cerâmica	43x43	branco	101010165	Ceral	Marmorizado, Brilhante, PEI 4
	6	Porcelanato	83x83	Branco	866907	Embramaco	Rejunte Cinza
	7	Porcelanato	92x92	branco	970745	Villagres	
RODAPÉ	1	Porcelanato Polido	10x62	Champagne	879373	Elizabeth	Juntas de encaixe cortado em 45°
	2	Cerâmica -Porcelanato	10x120cm	Branco	759303	Portinari	Juntas de encaixe cortado em 45°
	3	Porcelanato	10x61,8cm	Cinza	P82083	Artens	Combina com o Rejunte 90423942
FORRO	1	Sancra.	A definir	branco	A definir	A definir.	Consultar um especialista
	2	Teto-Rodapé	14x60	branco	AMB	xps2sa75	Consultar um especialista
	3	Sancra.	2.55X1.55	branco	A definir	A definir.	Consultar um especialista
	4	Sancra.	1.93x2.10	branco	A definir	A definir.	Consultar um especialista
	5	Sancra.	2.99X3.83	branco	A definir	A definir.	Consultar um especialista
	6	Sancra.	3.94X2.65	branco	A definir	A definir.	Consultar um especialista

	INSTITUTO FEDERAL DE EDUCAÇÃO, CIÊNCIA E TECNOLOGIA						
	DISCIPLINA	DESENHO DE CONSTRUÇÃO CIVIL			PROFESSORES	ANTONIO DEZOTTI FILHO	
	DESENHO	DETALHES E TABELAS			ESCALA	1:20	DATA 16 / 06 / 2022
	VISTO	NOME	GUSTAVO R. SILVESTRE DA SILVA		PRONTUÁRIO	FOLHA	04/04